


PŘÍČNÝ ŘEZ GABIONOVÝMI KŘÍDLY V LÍCI NK 1:100


VE SMĚRU STANIČENÍ

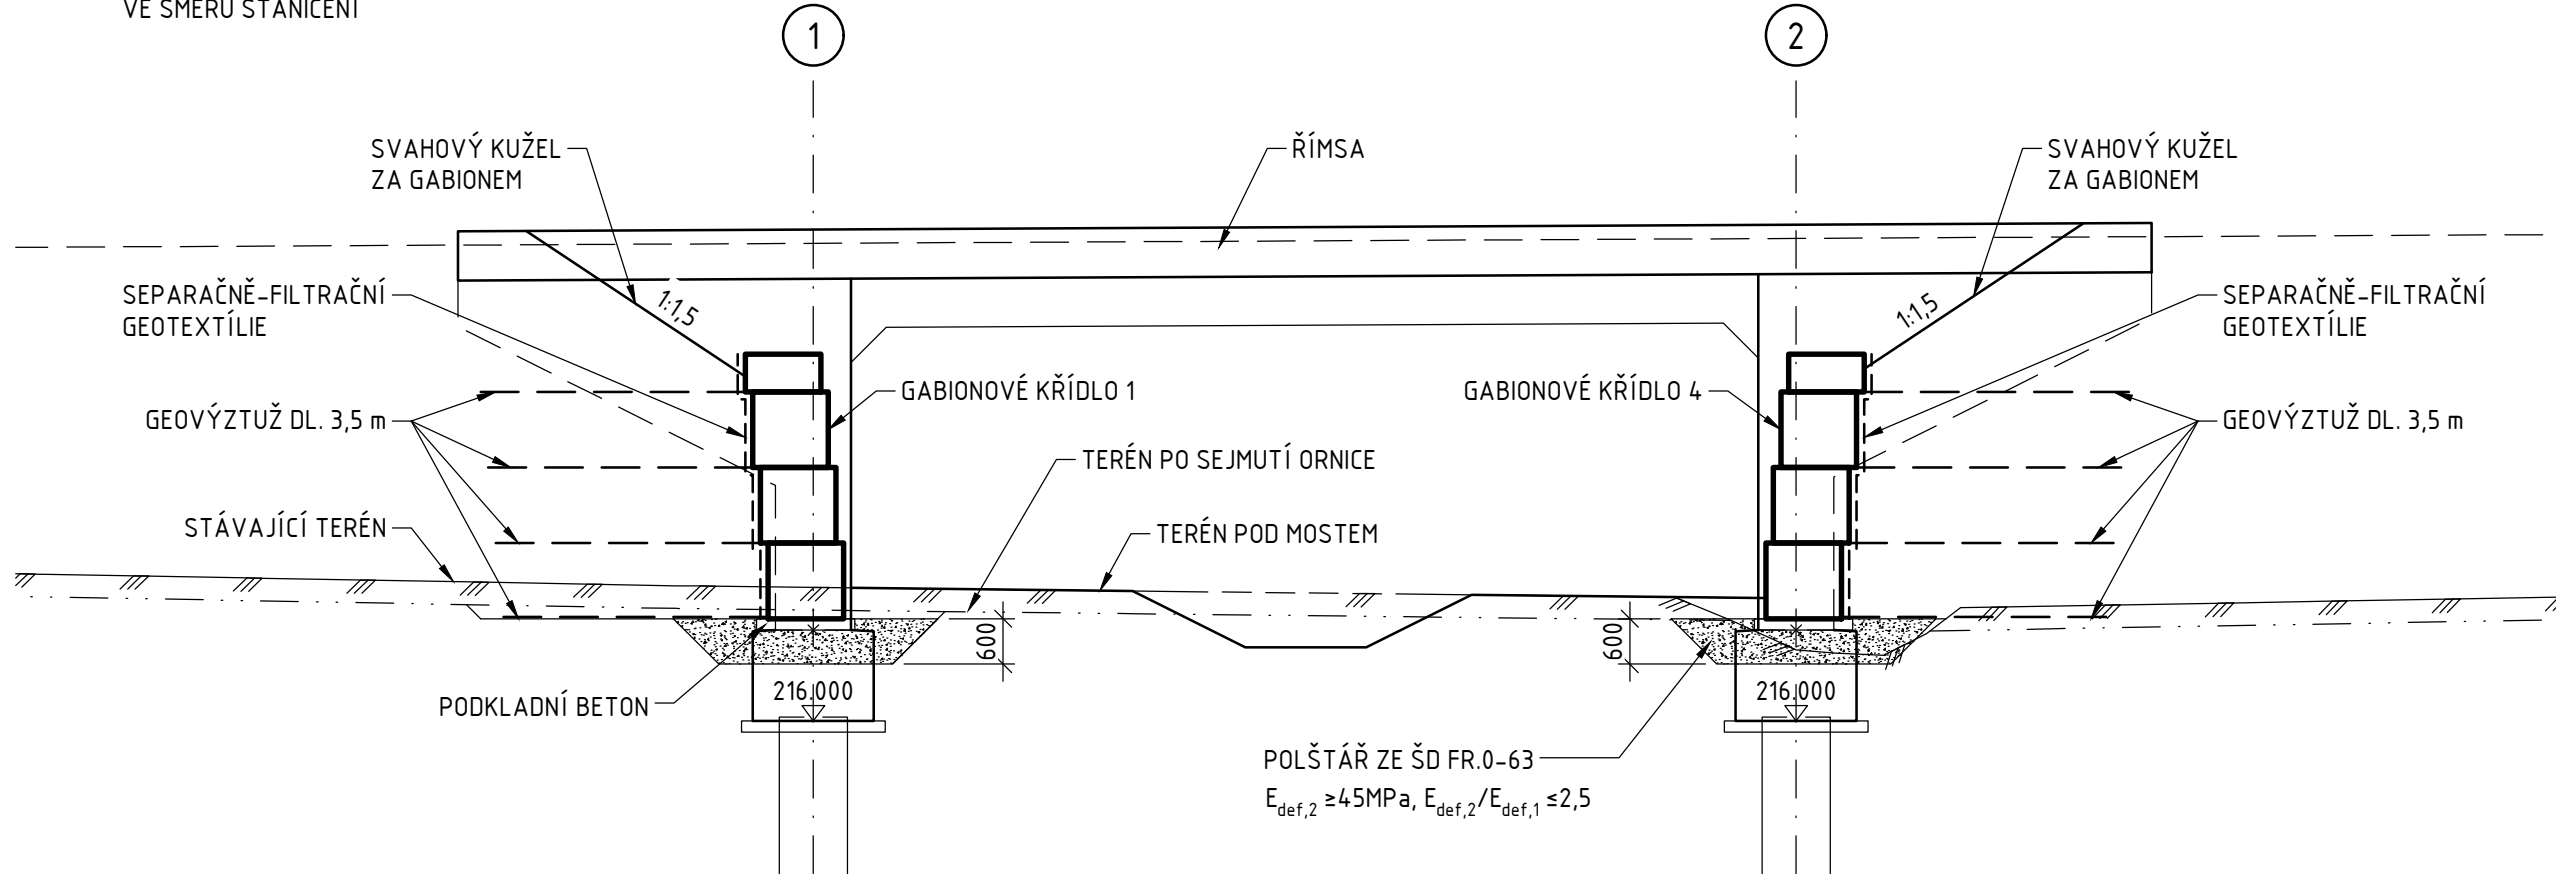


ROZMĚRY GABIONOVÝCH KOŠŮ:

- OZN. Š. DL. V.
A - 1000 x 2000 x 1000
B - 1000 x 2000 x 500
C - 1000 x 1000 x 1000
D - 1000 x 1000 x 500

ROZVINUTÉ POHLEDY - OPĚRA 1 1:100

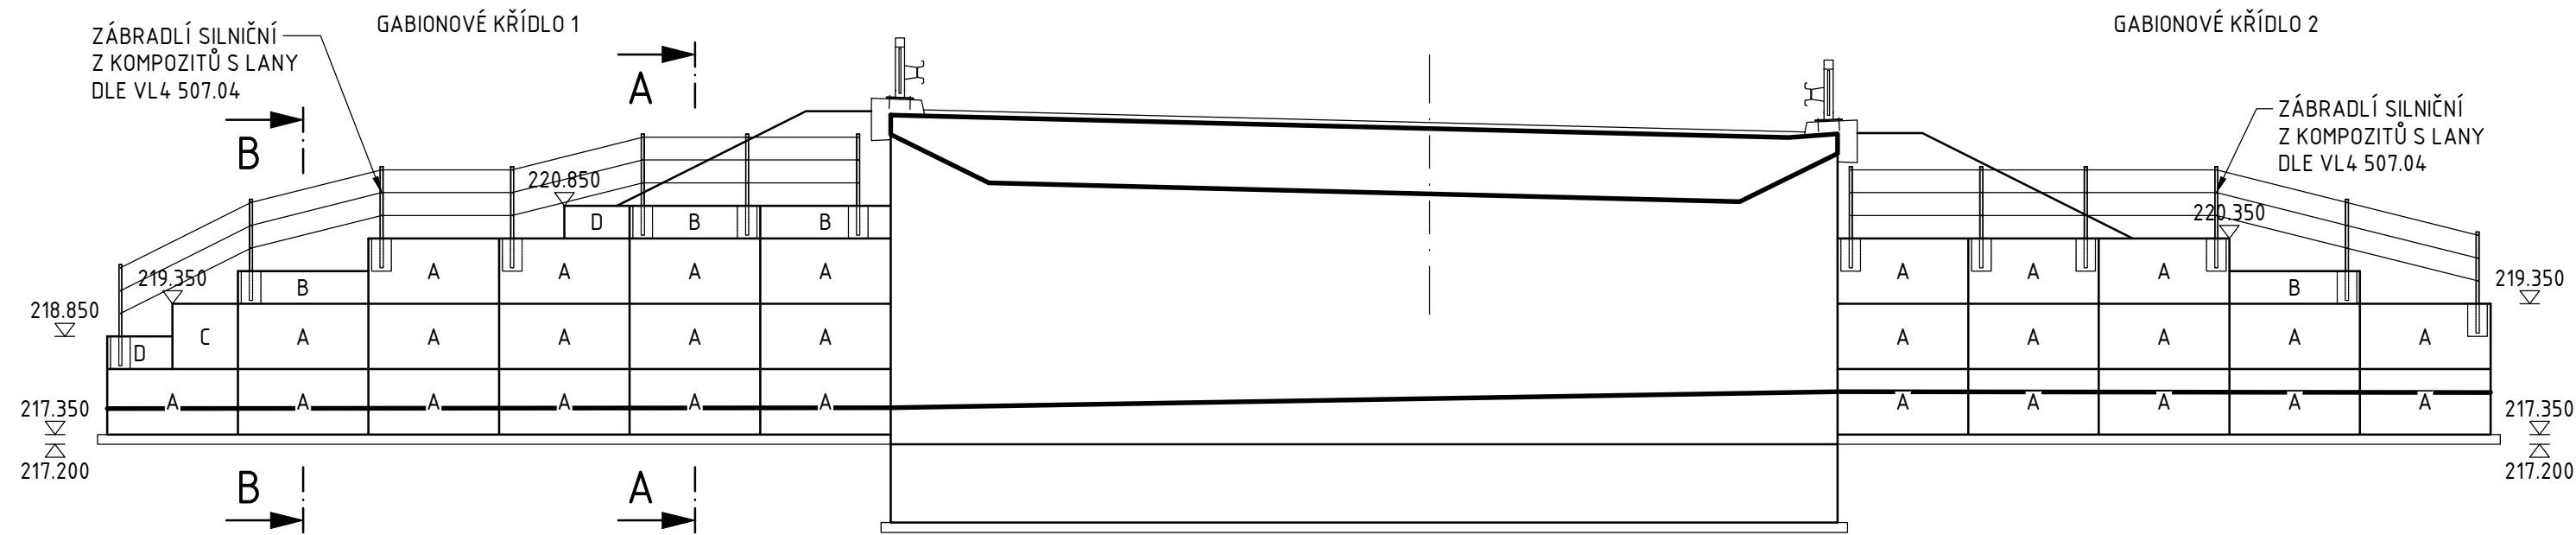

PŘÍČNÉ ŘEZY 1:100

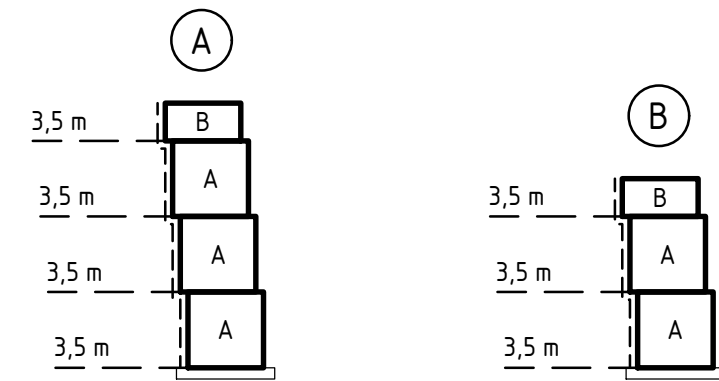


POZNÁMKY:




- NEDÍLNOU SOUČÁSTÍ VÝKRESU JSOU POZNÁMKY A SPECIFIKACE UVEDENÉ NA VÝKRESE POZNÁMEK A TECHNICKÝCH SPECIFIKACÍ

PŘÍČNÝ ŘEZ GABIONOVÝMI KŘÍDLY V LÍCI NK 1:100

PROTI SMĚRU STANIČENÍ

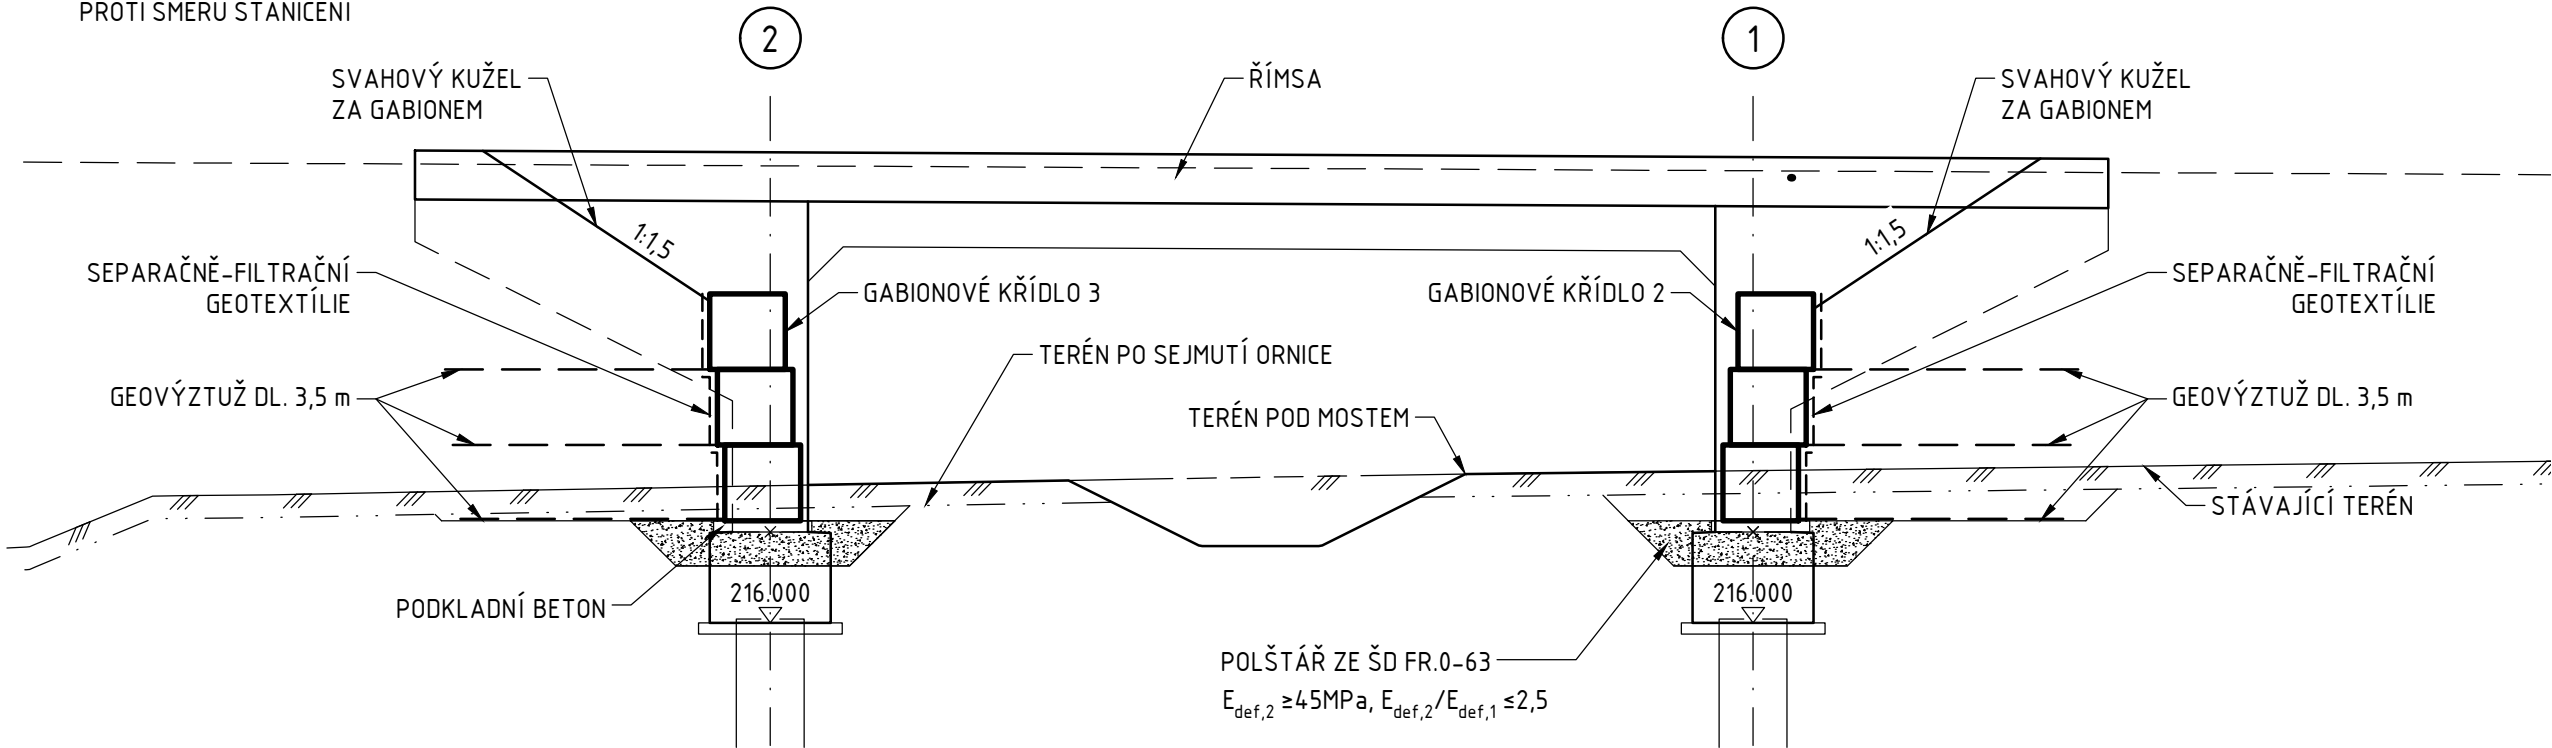

ROZVINUTÉ POHLEDY - OPĚRA 2 1:100

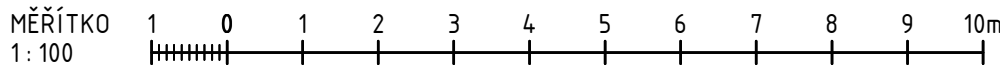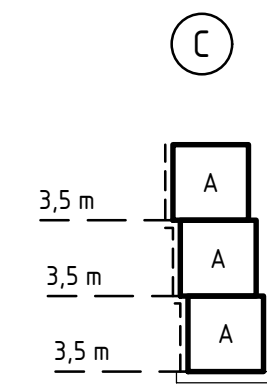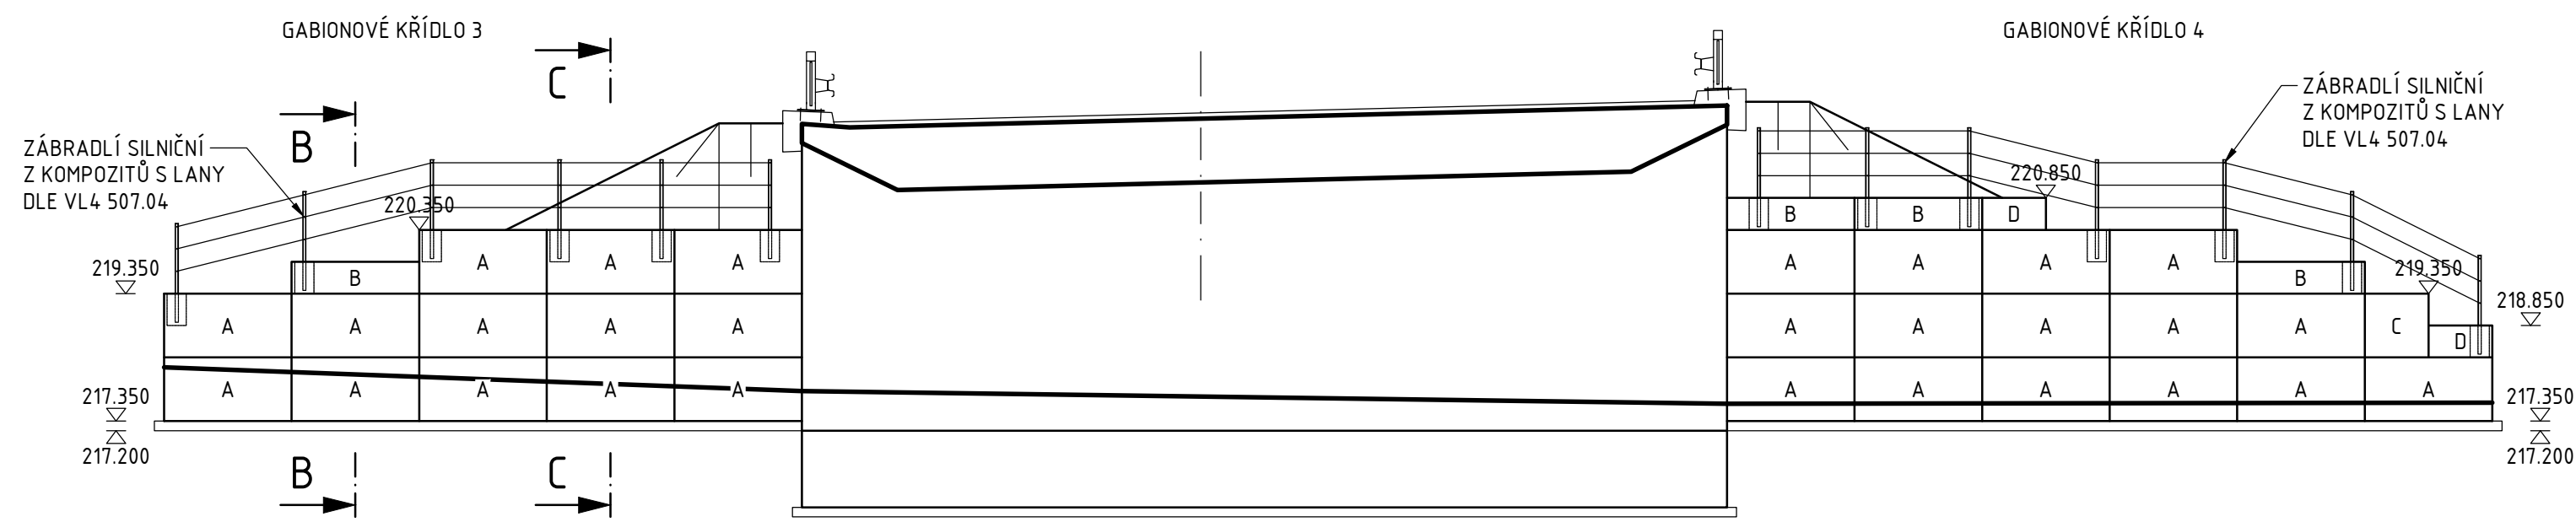

Souřadnicový systém: S-JTSK
Výškový systém: Bpv

SO 204 MOST NA I/16 PŘES SUKORADSKOU STOKU V KM 5,048

Objednatel:



Ředitelství silnic a dálnic s. p.
Čerčanská 2023/12, Krč, 140 00 Praha 4



Valbek, spol. s r.o.
Vaňurova 505/17
460 07 Liberec 3



Vypracoval	L. MARTÍNEK		Zak. číslo	21-L113-001
Zodp. projektant	ING. I. BELDA		Datum	02/2025
Tech. kontrola	ING. I. BELDA		Stupeň	PDPS
Akce	I/16 MLADÁ BOLESLAV - MARTINOVICE		Počet formátů	8x A4
Měřítko			1:100	
Příloha			Č. přílohy	Paré
			205	
GABIONOVÁ KŘÍDLA				