
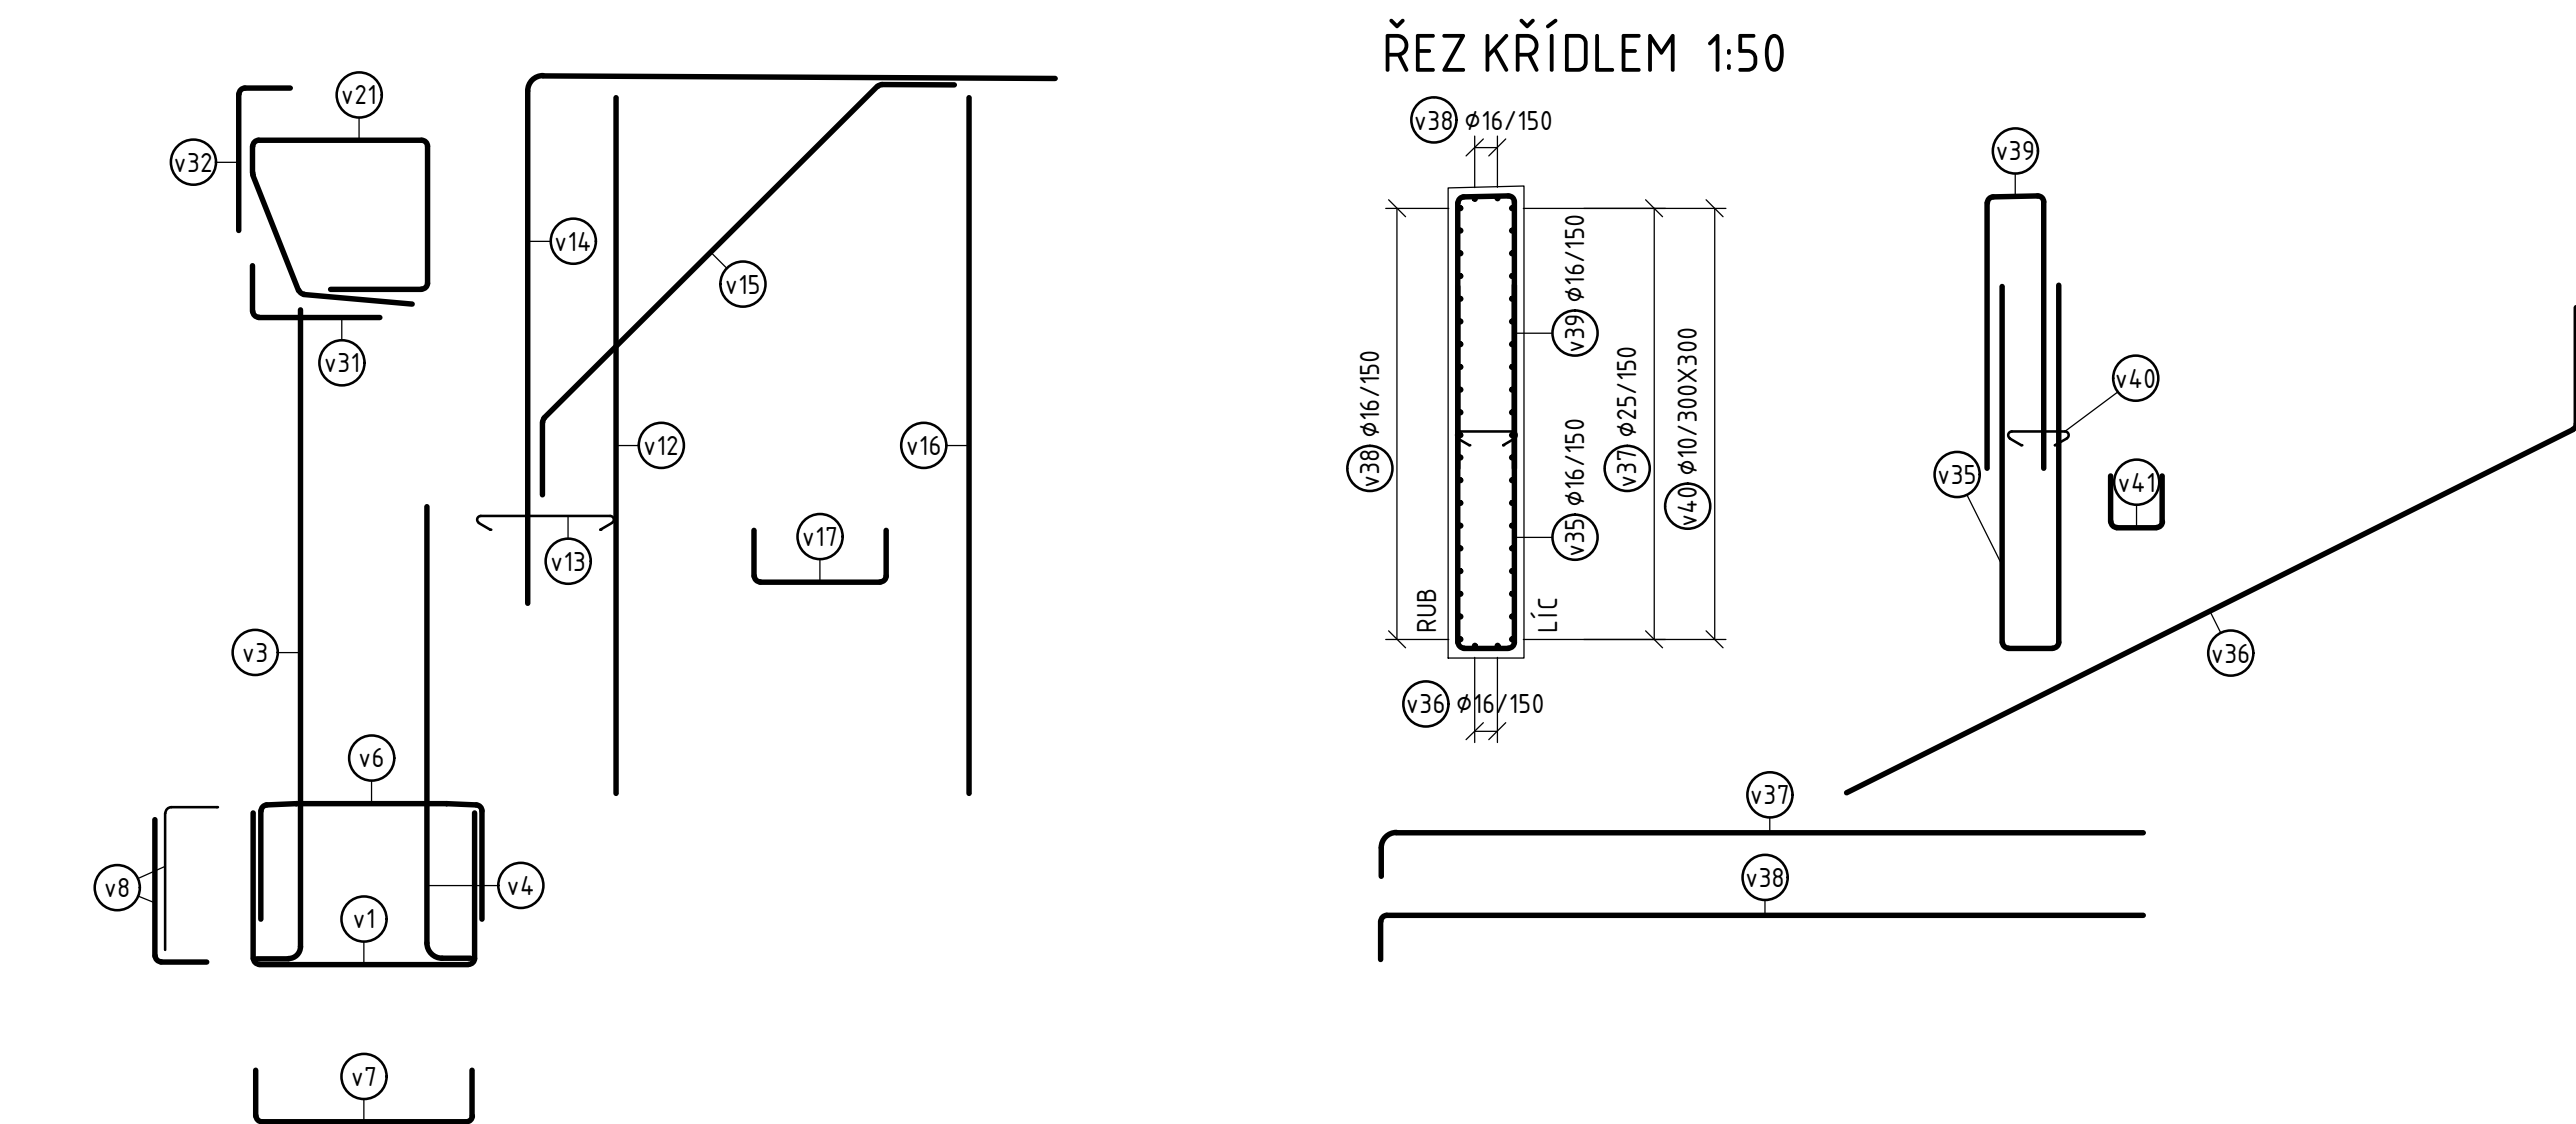
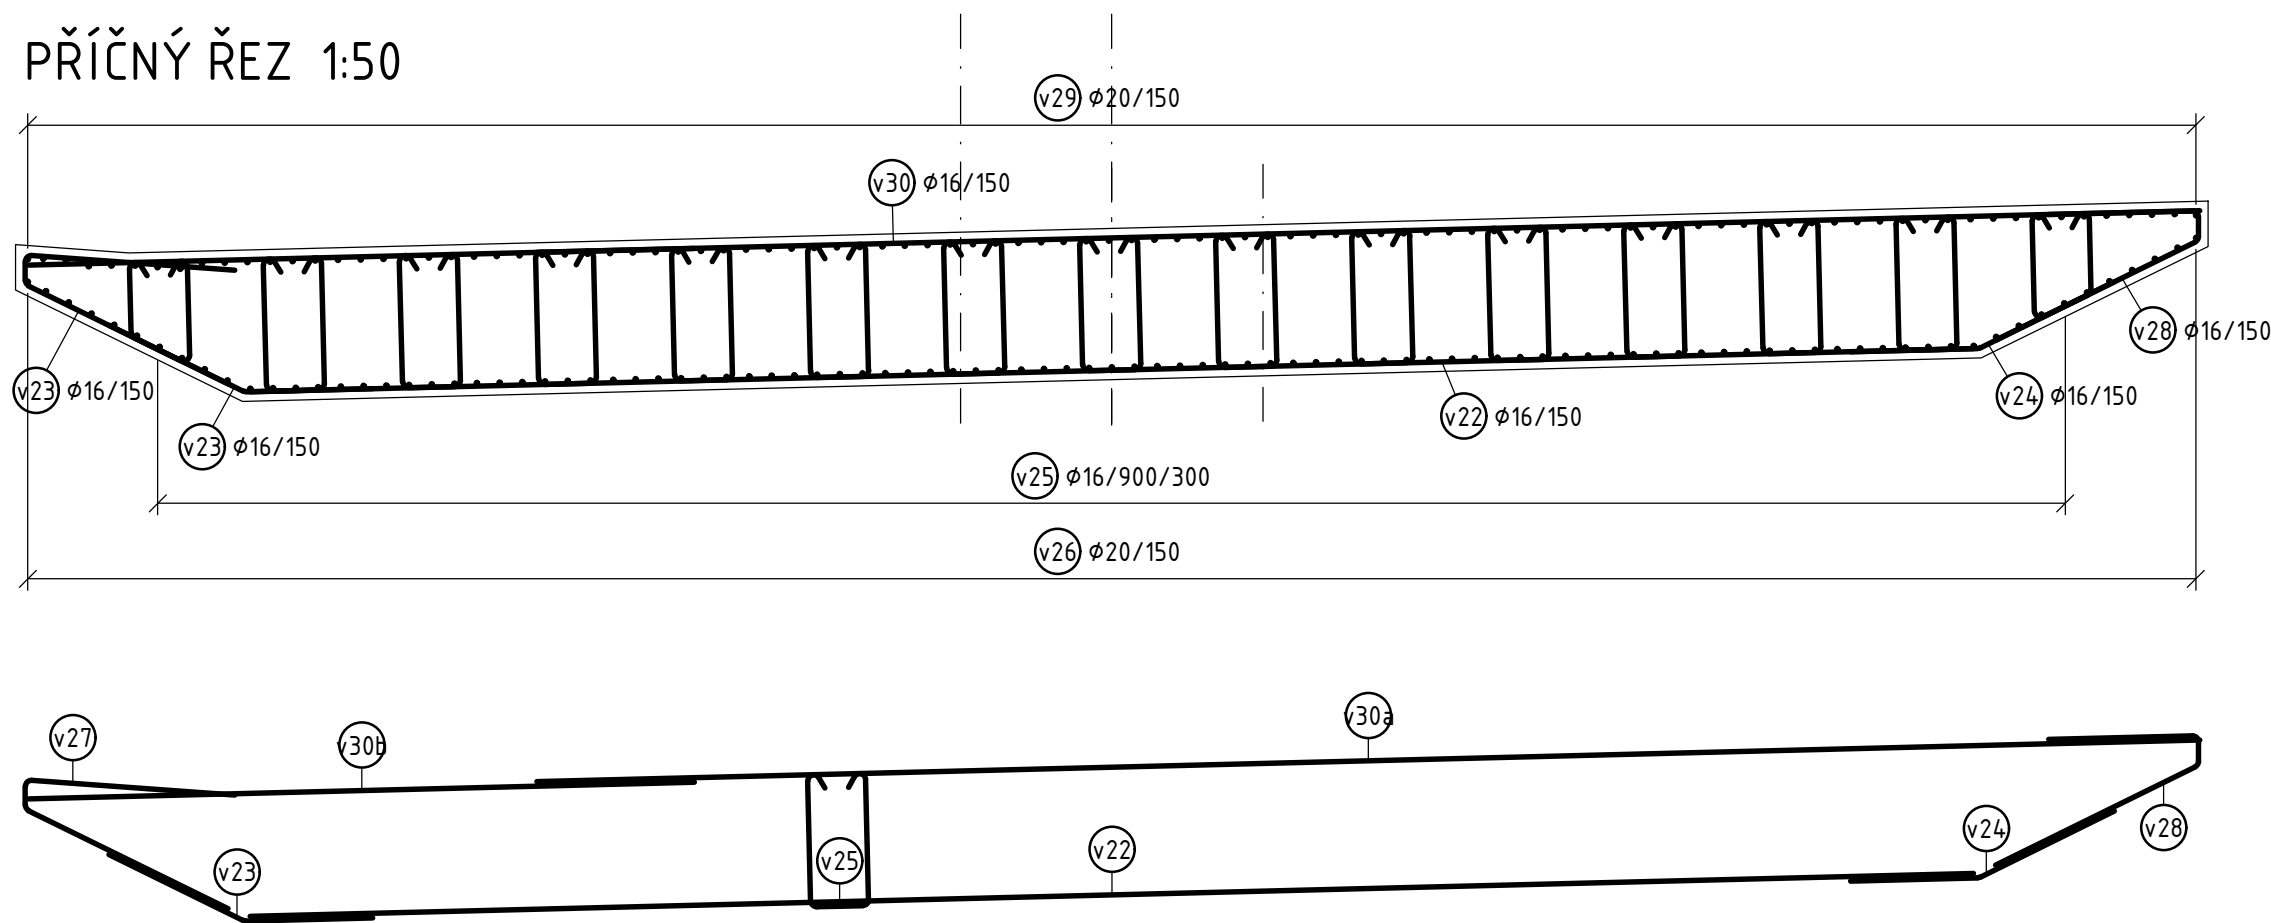


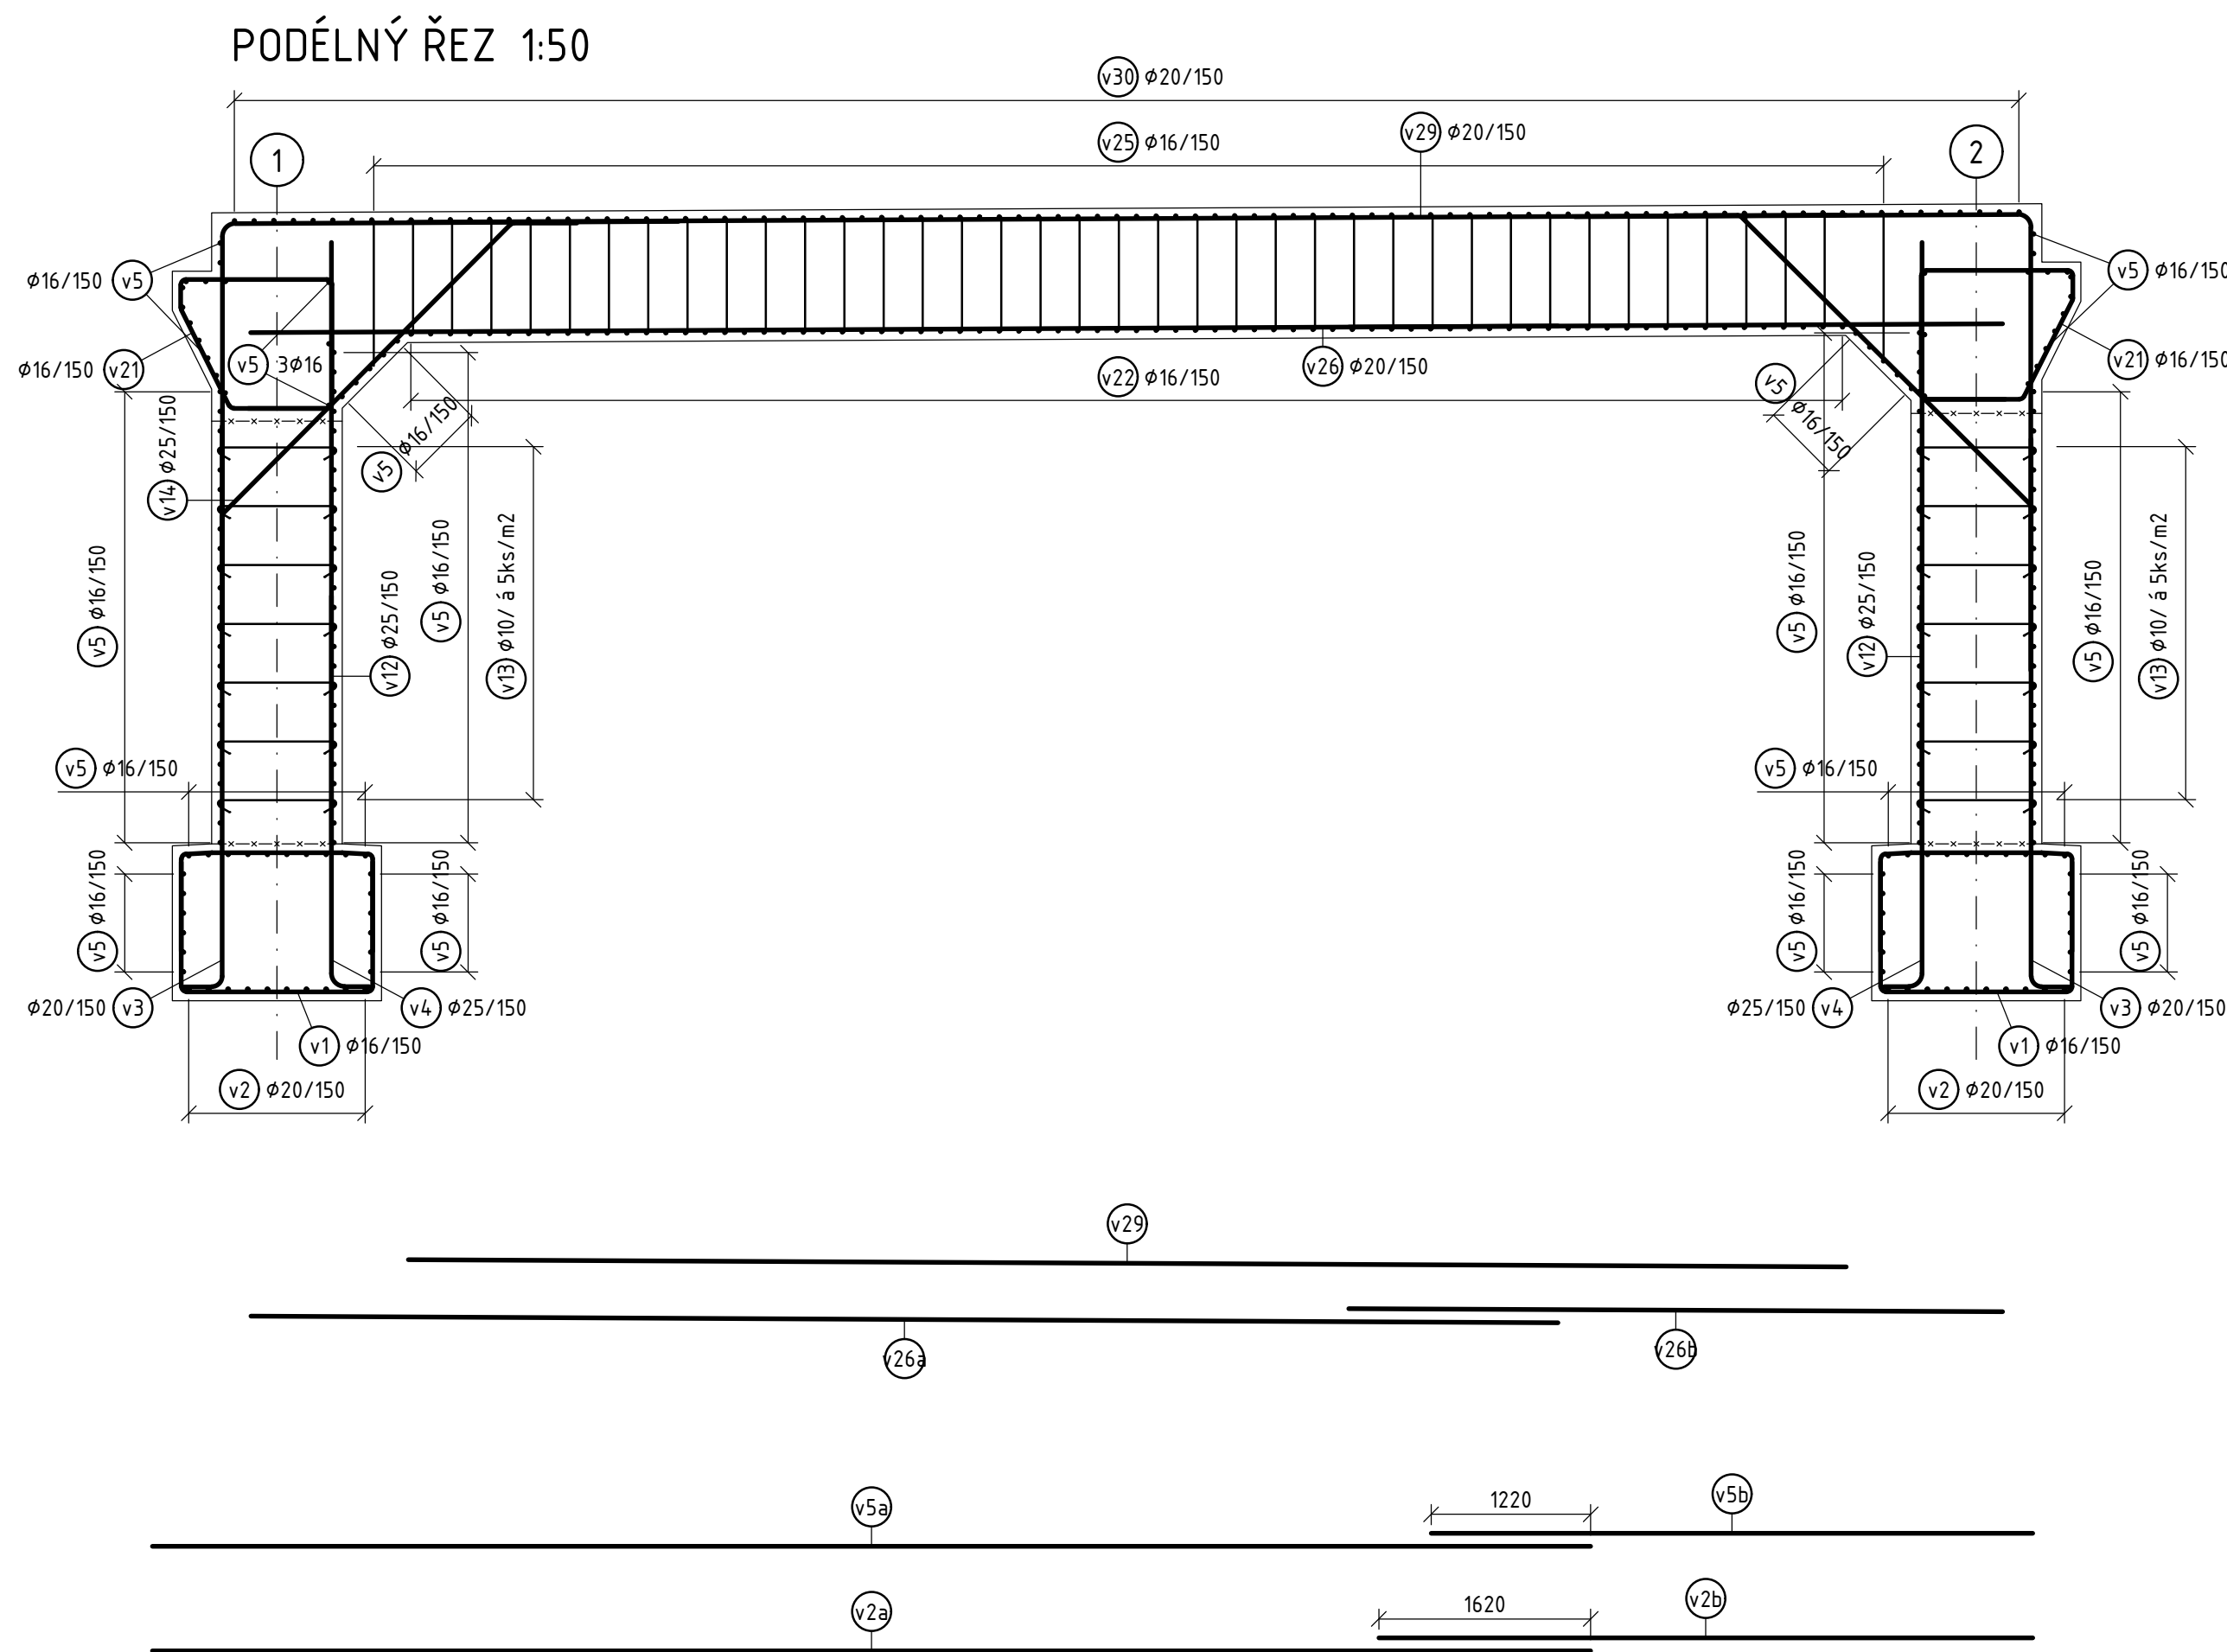

ODHAD MNOŽSTVÍ BETONÁŘSKÉ VÝZTUŽE SO 204	MNOŽSTVÍ VÝZTUŽE V %	MNOŽSTVÍ VÝZT. V KG/M3
VÝZTUŽ PILOT POD OPĚROU 01, D 900 mm	1.21%	95.0
VÝZTUŽ PILOT POD OPĚROU 02, D 900 mm	1.21%	95.0
VÝZTUŽ ZÁKLADŮ OPĚRY 01	2.93%	230.0
VÝZTUŽ ZÁKLADŮ OPĚRY 02	2.93%	230.0
VÝZTUŽ NOSNÉ KONSTRUKCE	1.27%	100.0
VÝZTUŽ ŘÍMS	1.78%	140.0
VÝZTUŽ PŘECHODOVÝCH DESEK	1.91%	150.0

POZNÁMKY:

- NEDÍLNOU SOUČÁSTÍ VÝKRESU JSOU POZNÁMKY A SPECIFIKACE UVEDENÉ NA VÝKRESE
POZNÁMEK A TECHNICKÝCH SPECIFIKACÍ

Souřadnicový systém: S-JTSK
Výškový systém: Bpv

SO 204 MOST NA I/16 PŘES SUKORADSKOU STOKU V KM 5,048

Objednatel:

Ředitelství silnic a dálnic s. p.
Čerčanská 2023/12, Krč, 140 00 Praha 4

Valbek, spol. s r.o.
Vaňurova 505/17
460 07 Liberec 3

	Vypracoval	L. MARTINEK		Zak. číslo	21-L113-001	
	Zodp. projektant	ING. I. BELDA		Datum	02/2025	
	Tech. kontrola	ING. I. BELDA		Stupeň	PDPS	
	Akce	I/16 MLADÁ BOLESLAV - MARTINOVICE			Počet formátů	8x A4
Zhotovitel: Valbek, spol. s r.o. Vaňurova 505/17 460 07 Liberec 3	Příloha	SCHÉMATICKÝ VÝKRES VÝZTUŽE			Měřítko	1:50
					Č. přílohy	Paré
301						

