


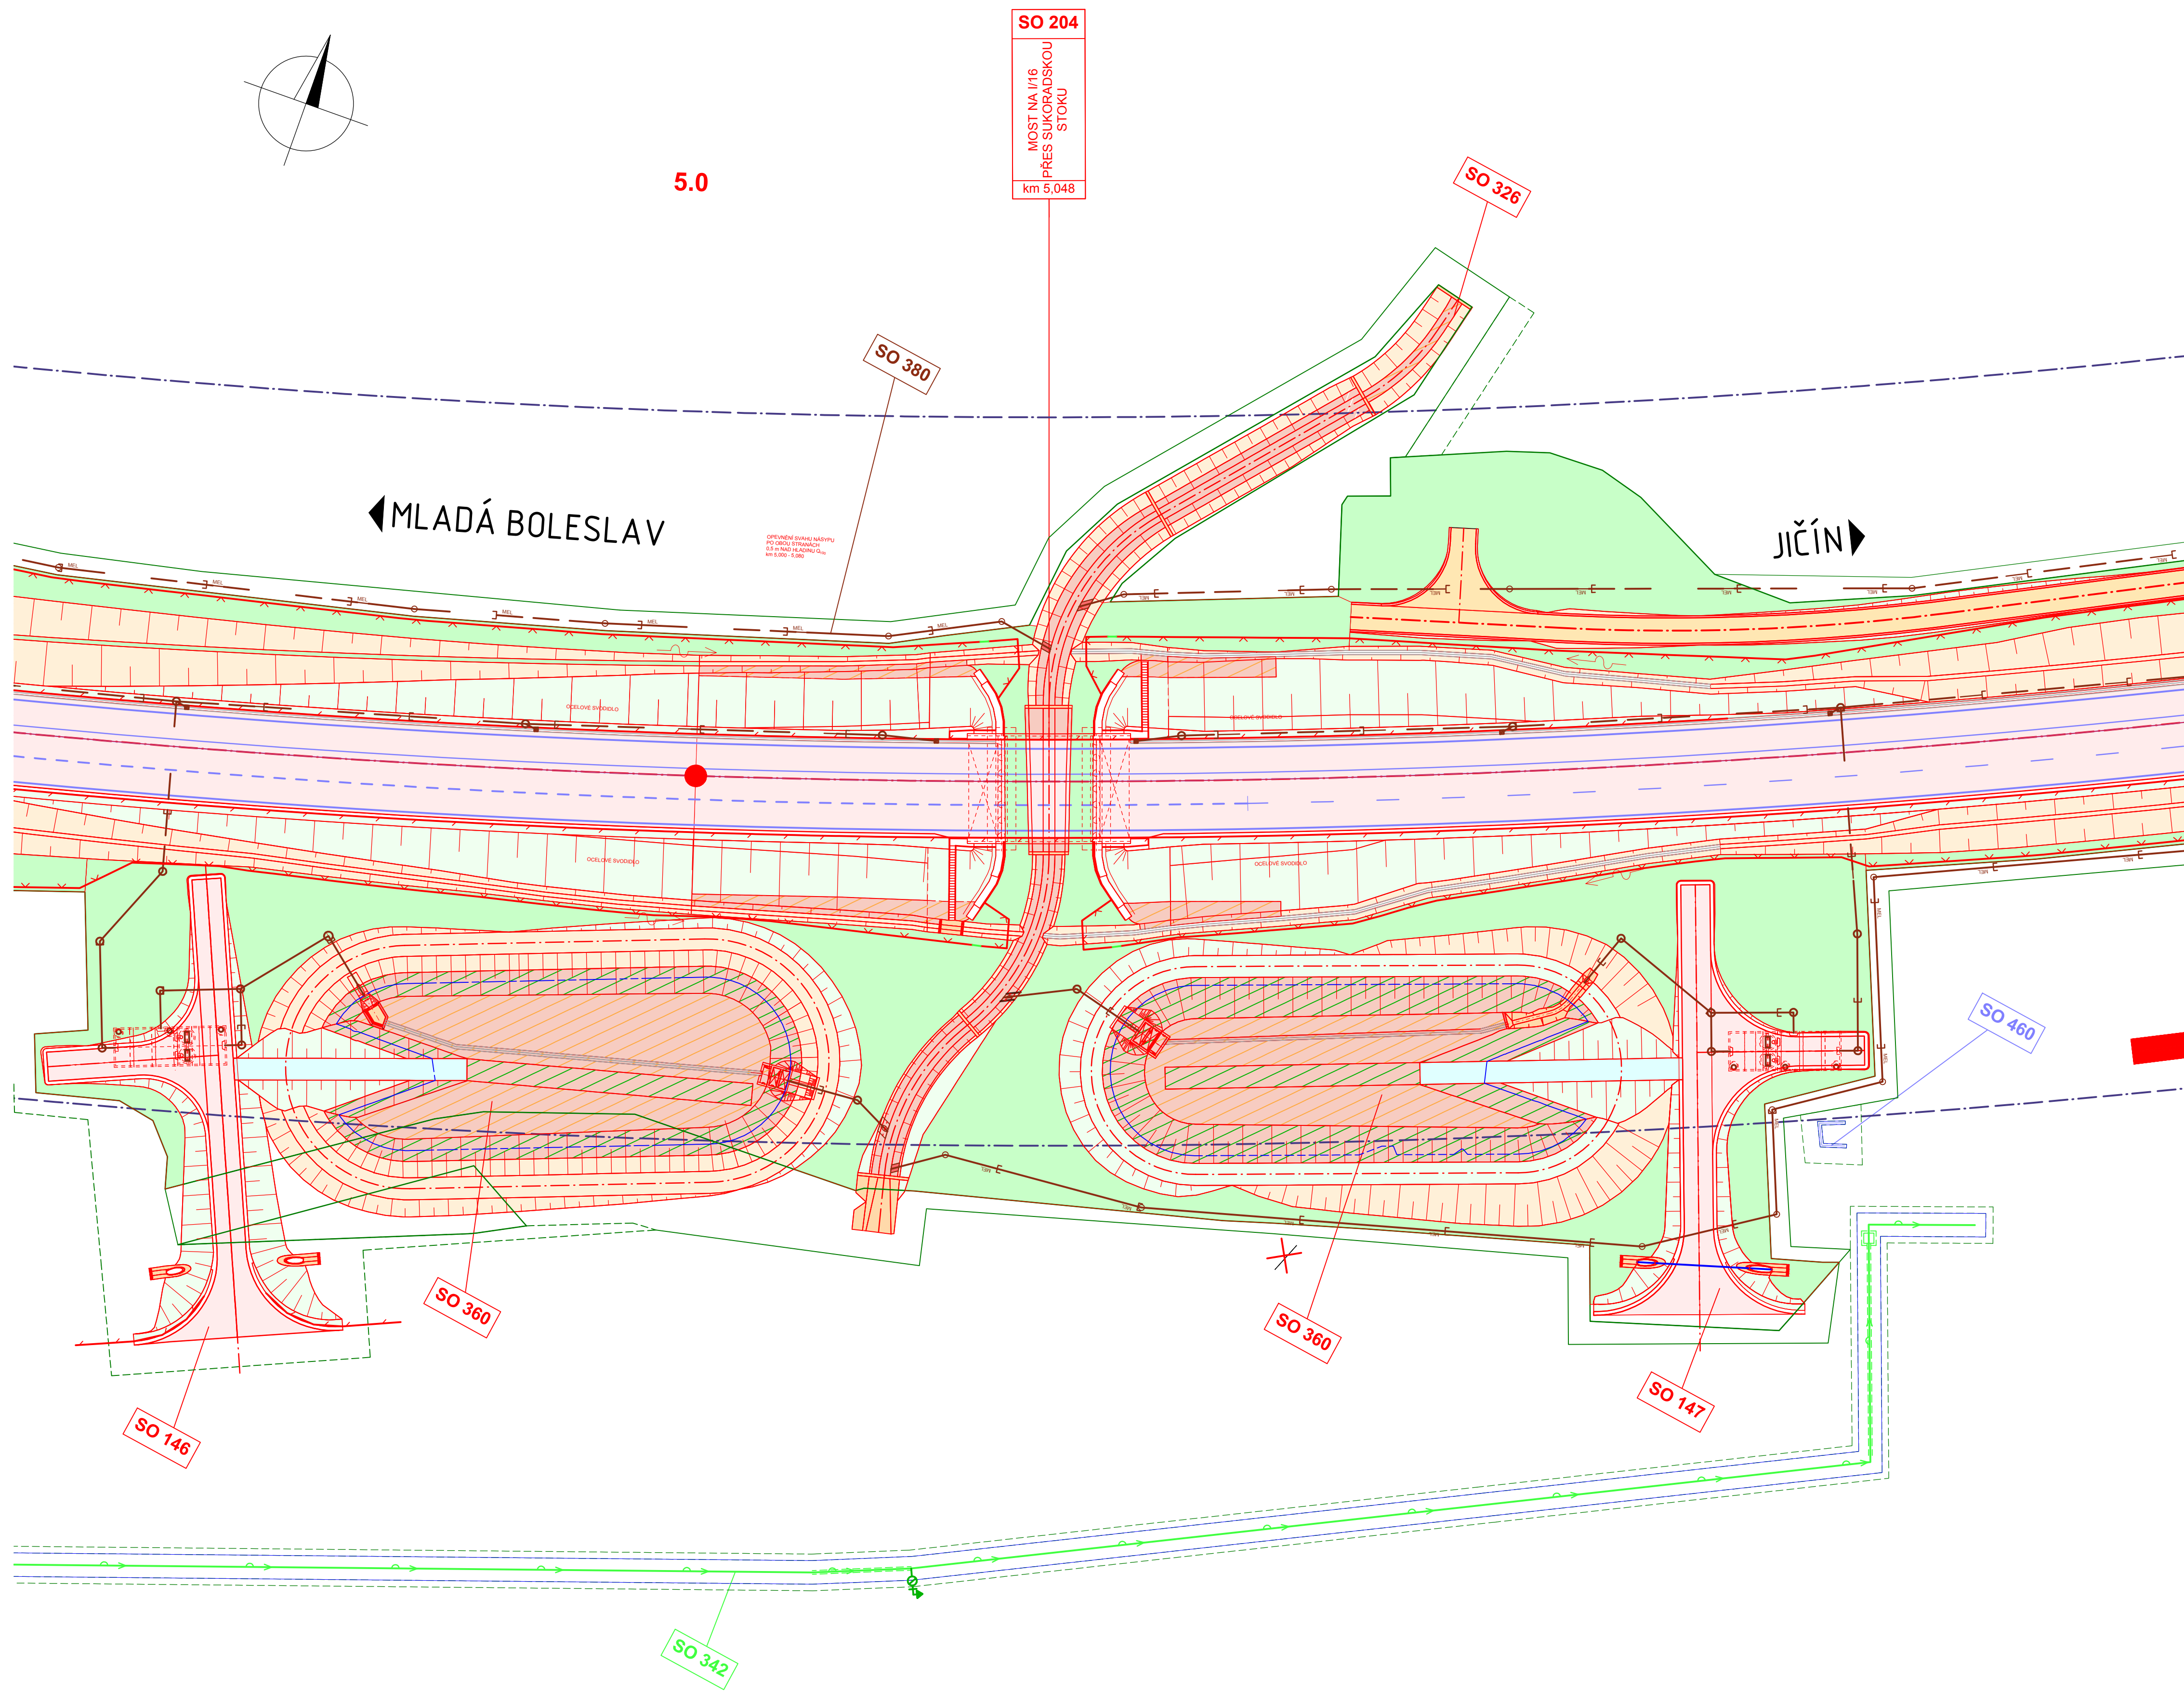

Souřadnicový systém: S-JTSK
Výškový systém: Bpv

SO 204 MOST NA I/16 PŘES SUKORADSKOU STOKU V KM 5,048

Objednatel:



Ředitelství silnic a dálnic s. p.
Čerčanská 2023/12, Krč, 140 00 Praha 4



Valbek, spol. s r.o.
Vaňurova 505/17
460 07 Liberec 3

	Vypracoval	ING. I. BELDA		Zak. číslo	21-L113-001	
	Zodp. projektant	ING. I. BELDA		Datum	02/2025	
	Tech. kontrola	ING. I. BELDA		Stupeň	PDPS	
	Akce	I/16 MLADÁ BOLESLAV - MARTINOVICE			Počet formátů	8x A4
					Měřítko	1:500
				Č. přílohy	Paré	
Zhotovitel: Valbek, spol. s r.o. Vaňurova 505/17 460 07 Liberec 3	Příloha	PŘEHLEDNÁ SITUACE			401	