



TVAR NOSNÉ KONSTRUKCE

PŮDORYS 1:150

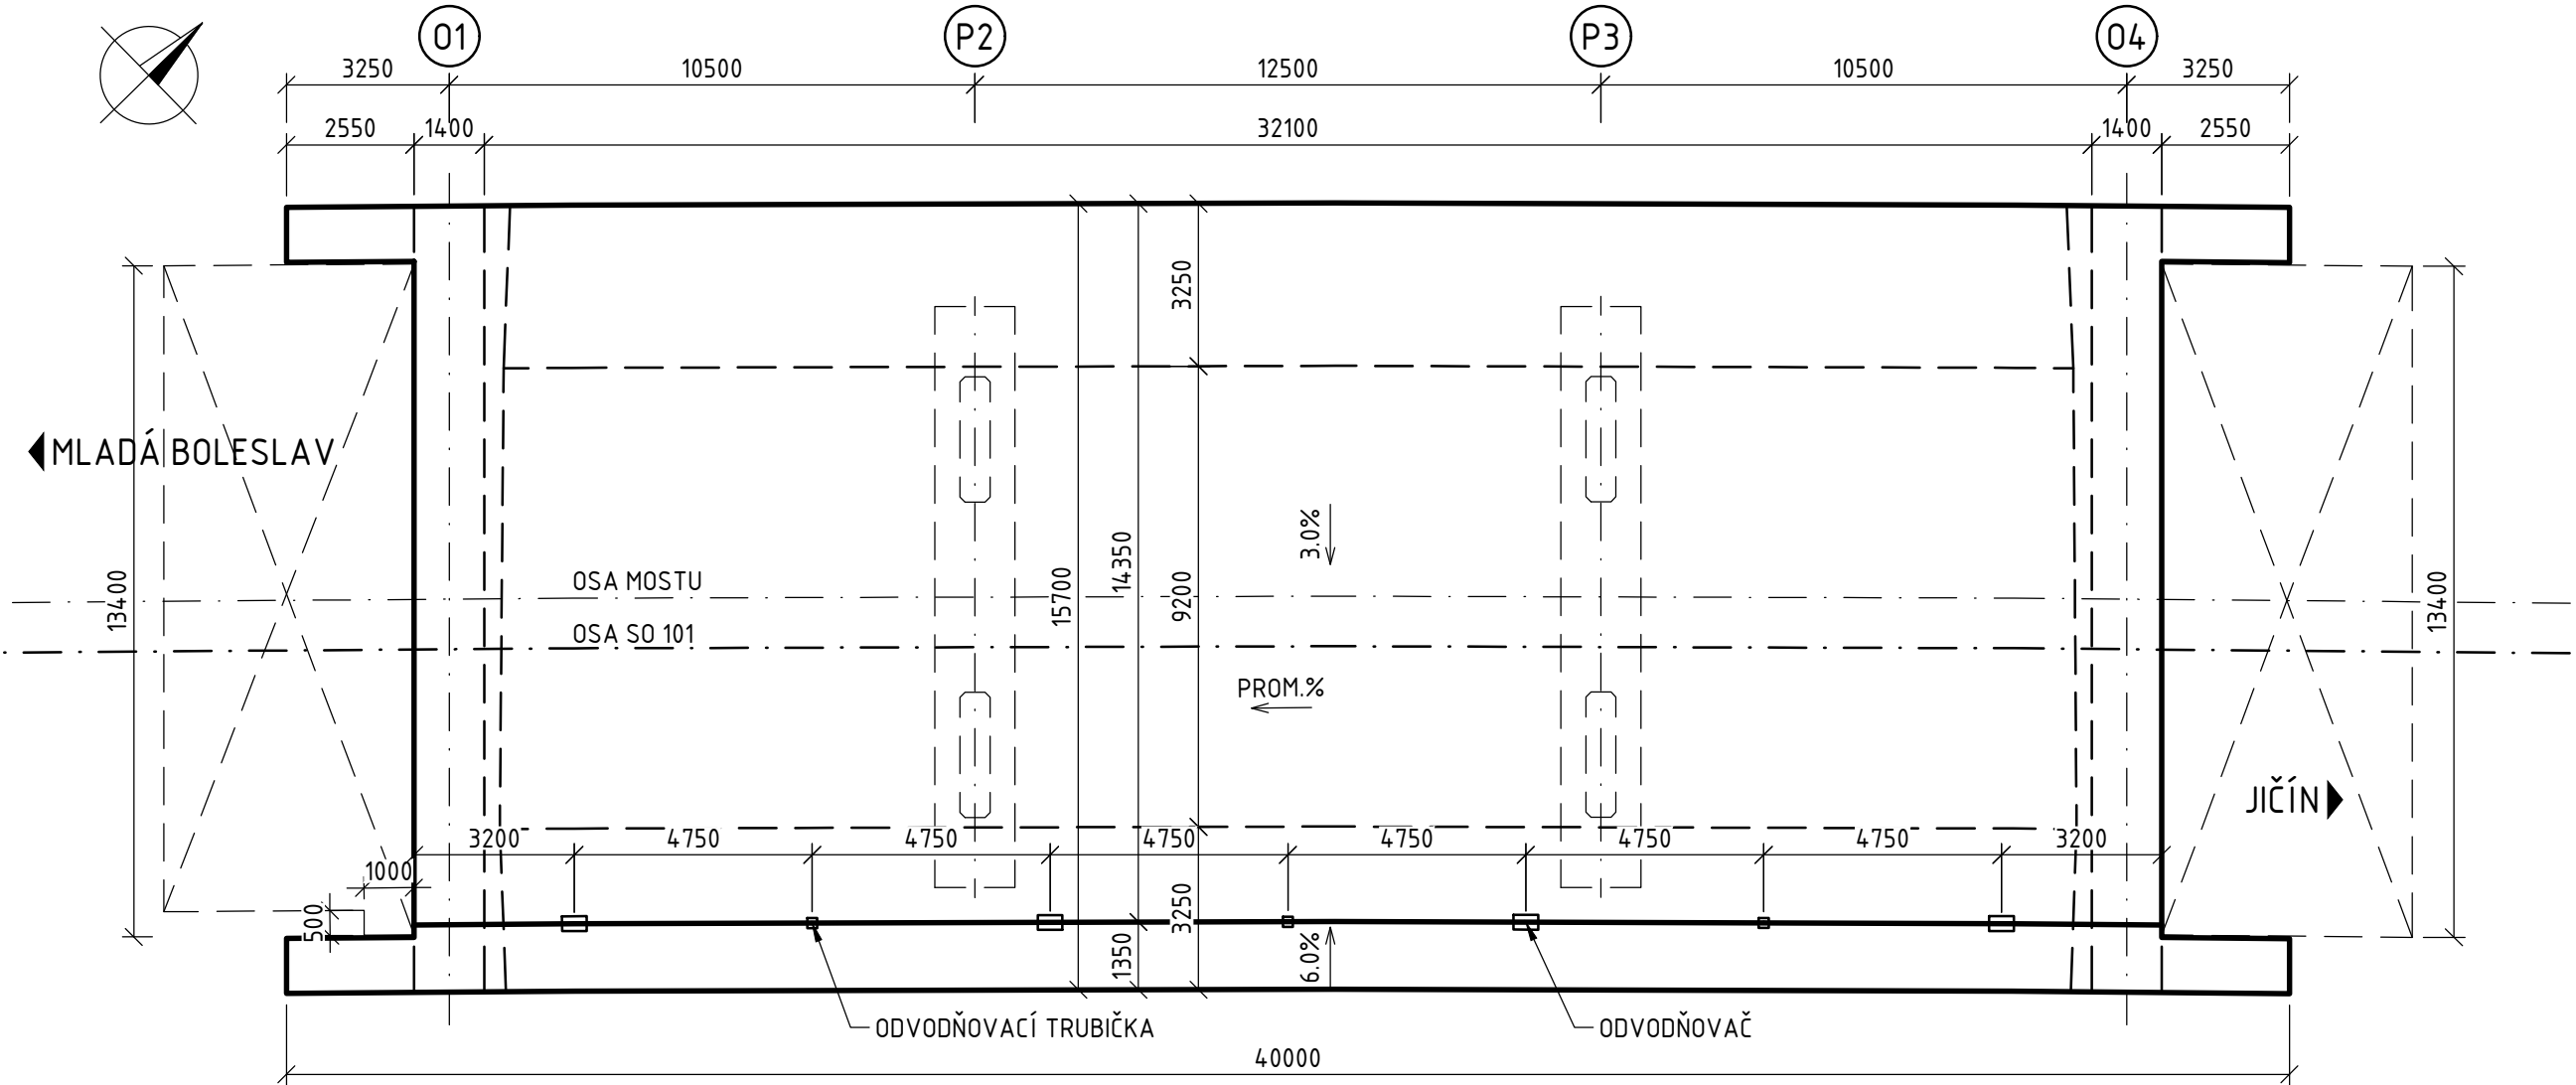


PODÉLNÝ ŘEZ 1:150

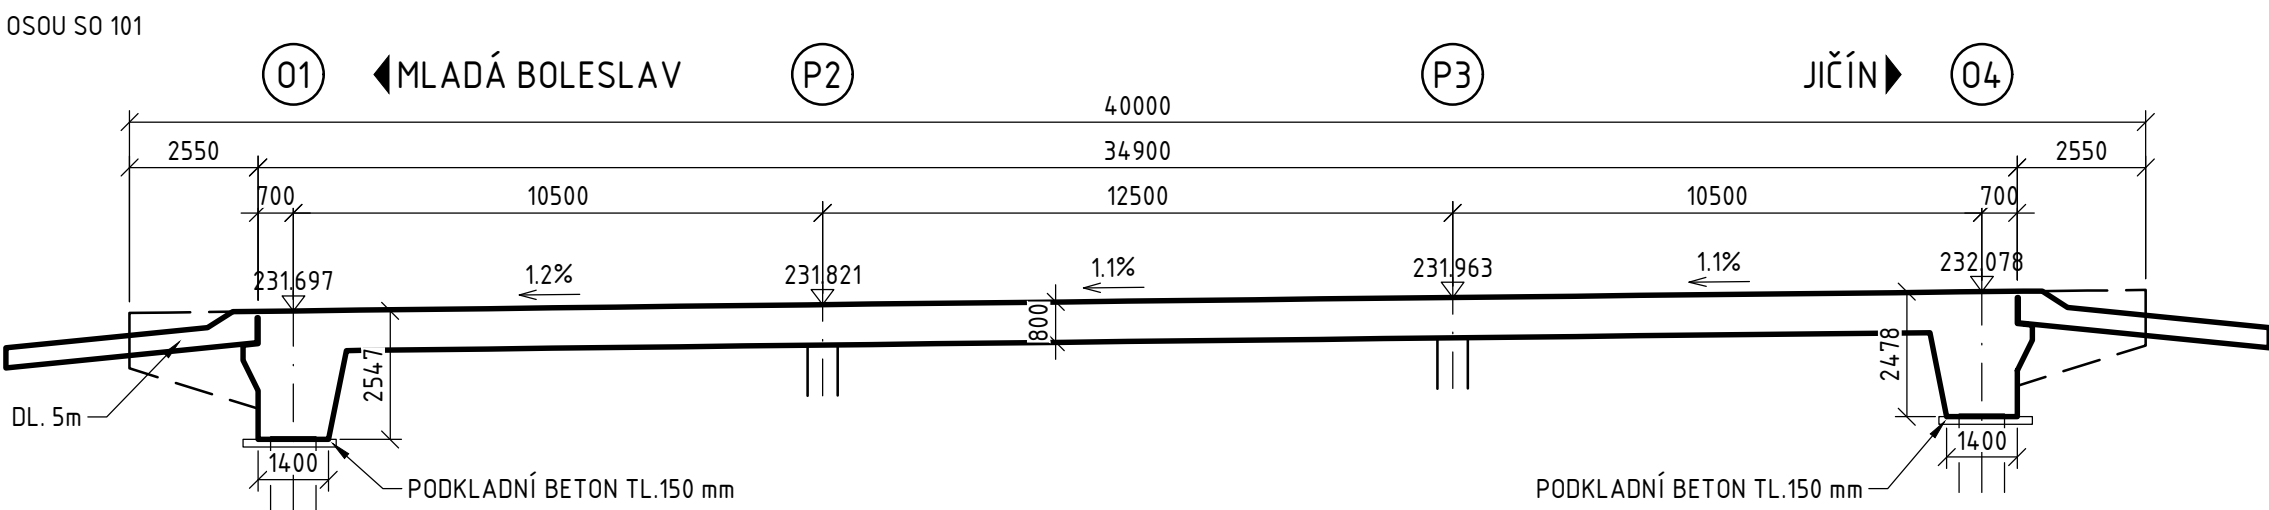


PŘECHODOVÉ OBLASTI


PODÉLNÝ ŘEZ 01 1:75

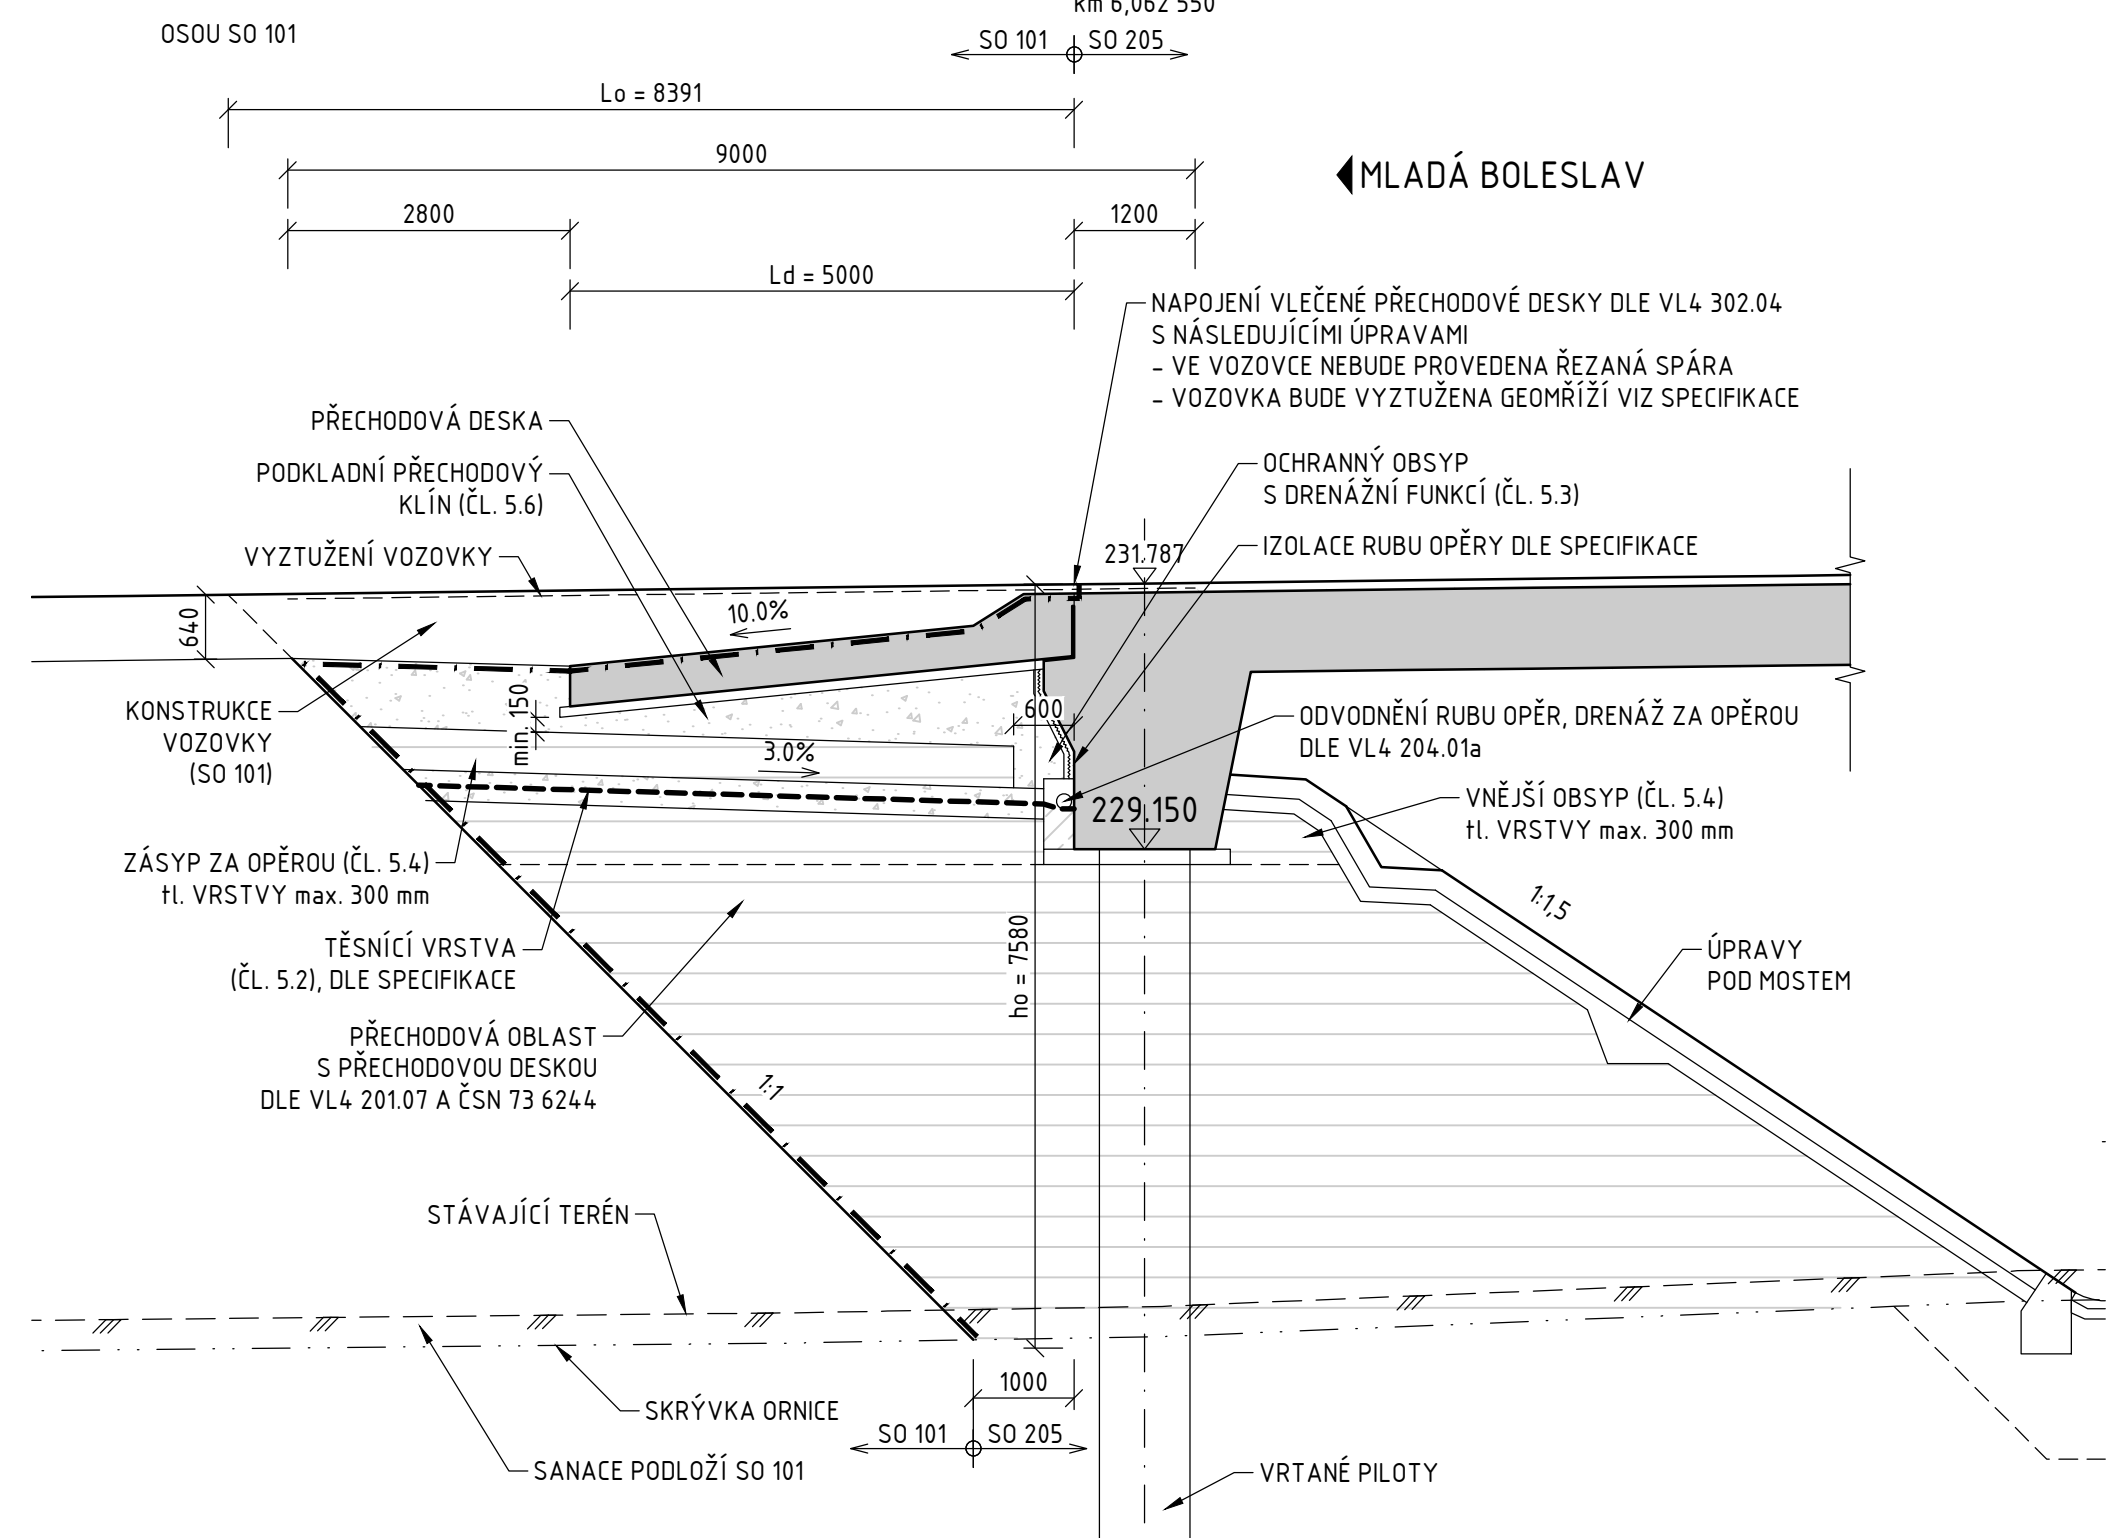


POHLED NA KŘÍDLO 01 VPRAVO 1:75

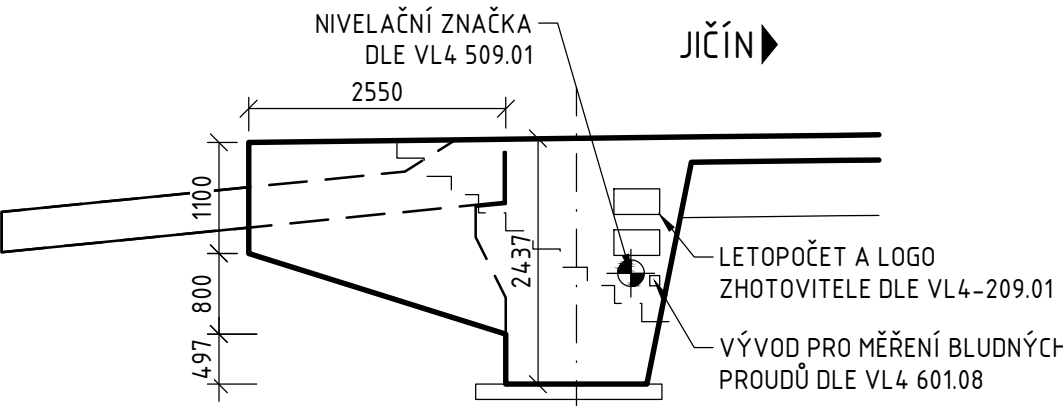


POHLED NA KŘÍDLO 04 VLEVO 1:75

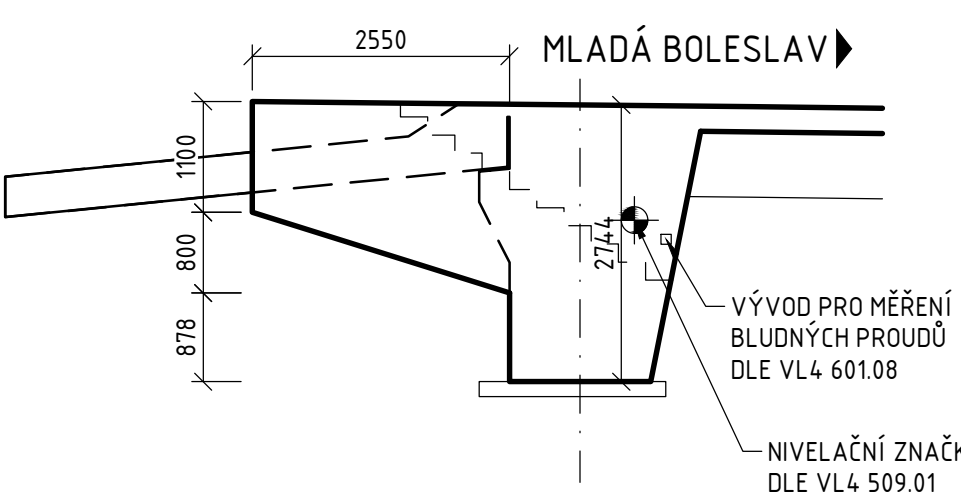


PŘÍČNÝ ŘEZ 1:75

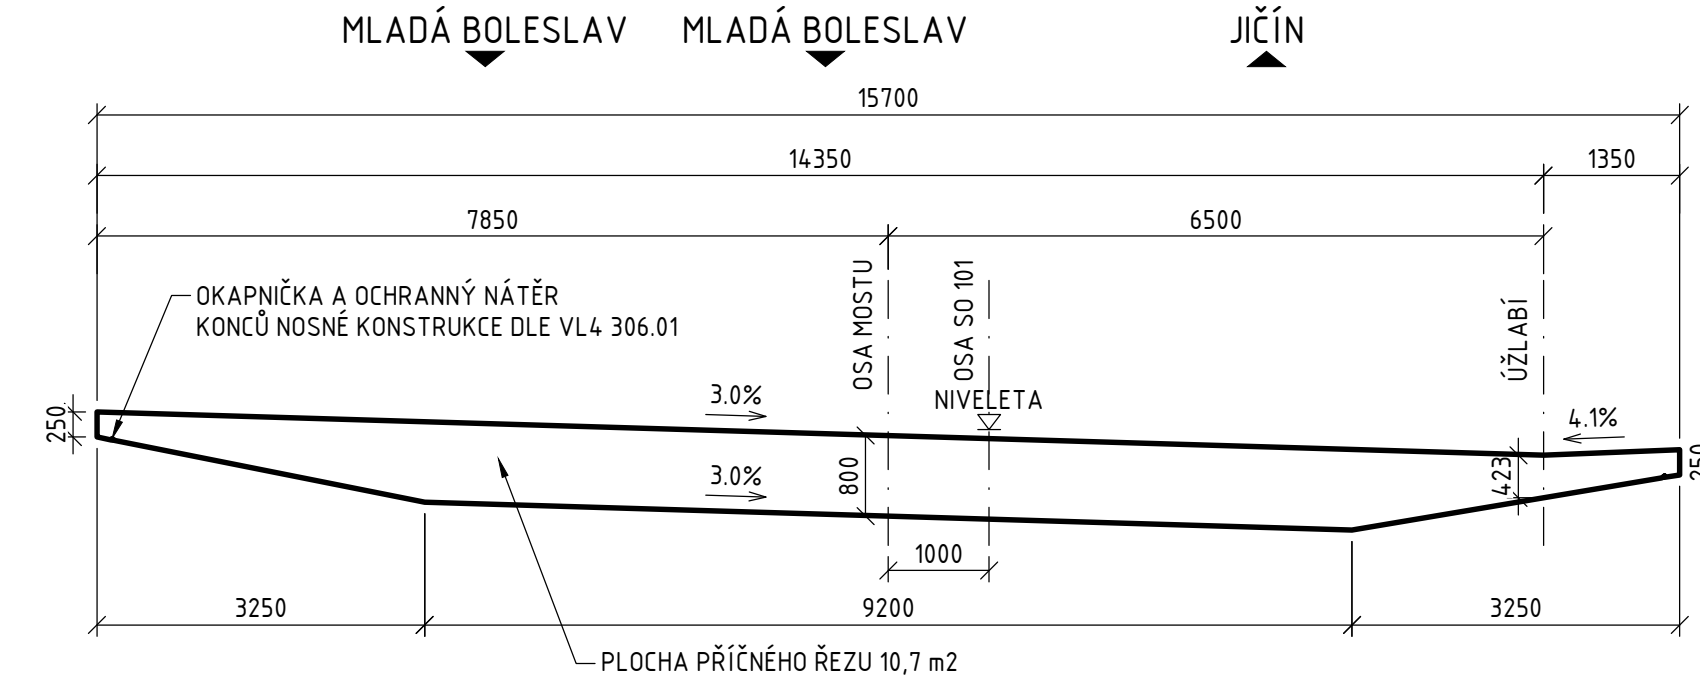


POHLED NA KŘÍDLO 01 VLEVO 1:75

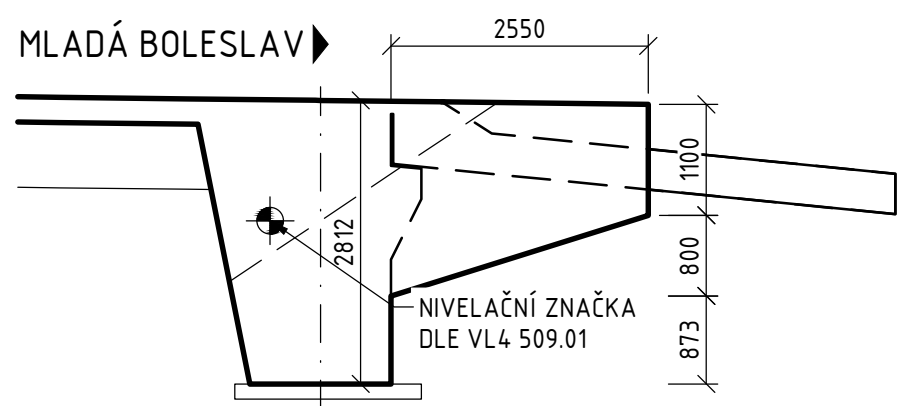


POHLED NA KŘÍDLO 04 VPRAVO 1:75

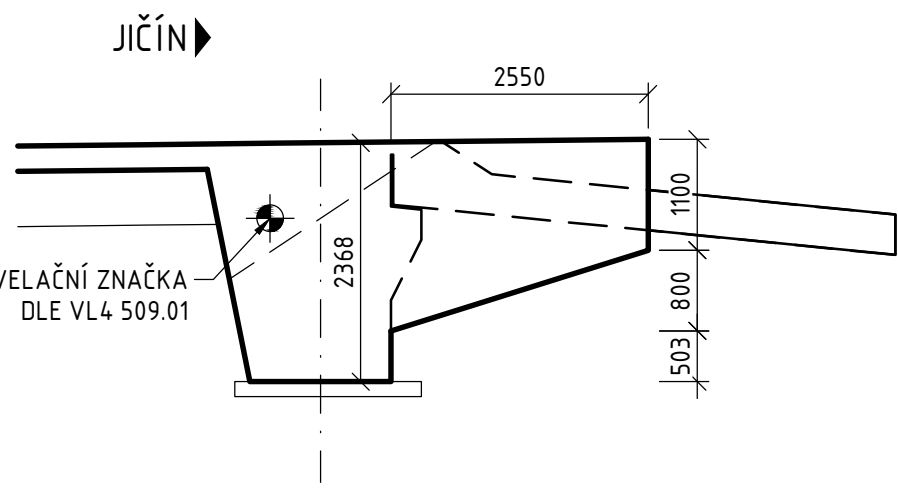

ŘEZ KŘÍDLEM 1:75

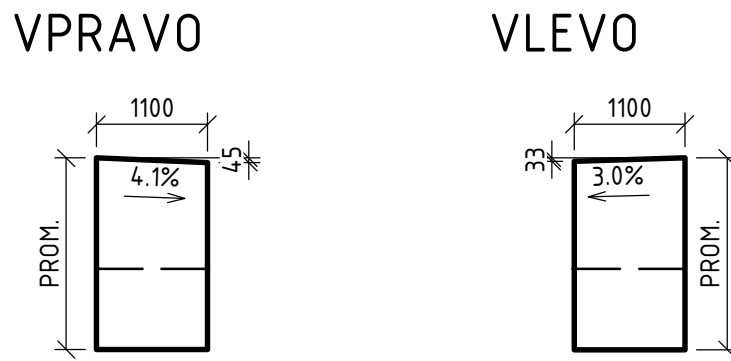



PODÉLNÝ ŘEZ PŘECHODOVOU DESKOU 1:50

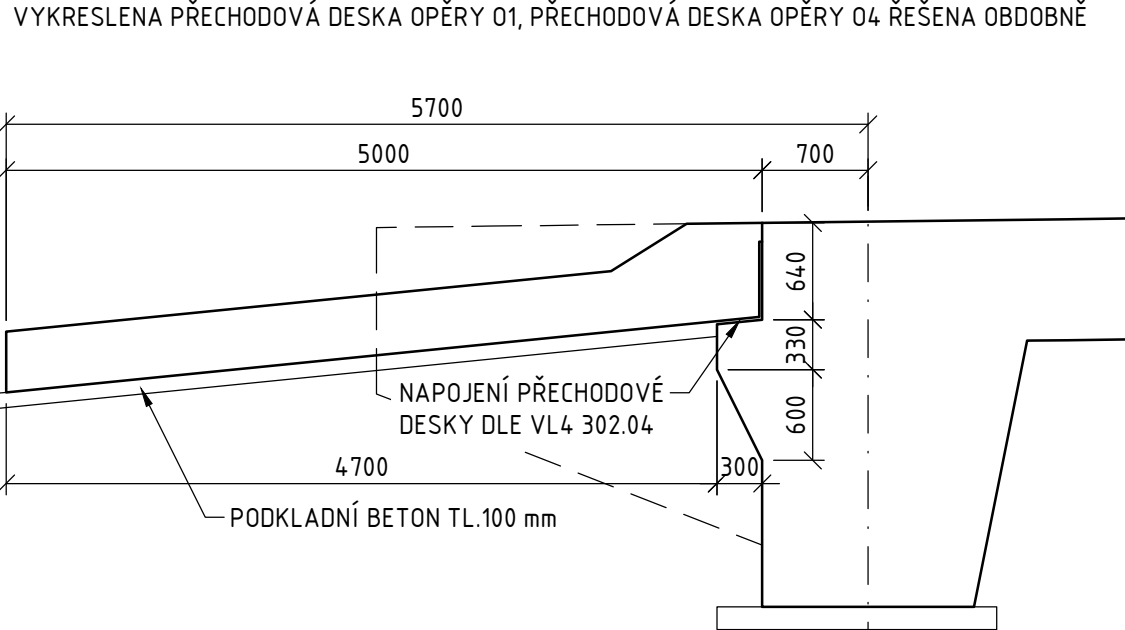

POZNÁMKY:

- NEDÍLNOU SOUČÁSTÍ VÝKRESU JSOU POZNÁMKY A SPECIFIKACE UVEDENÉ NA VÝKRESE POZNÁMEK A TECHNICKÝCH SPECIFIKACÍ

PODÉLNÝ ŘEZ 04 1:75


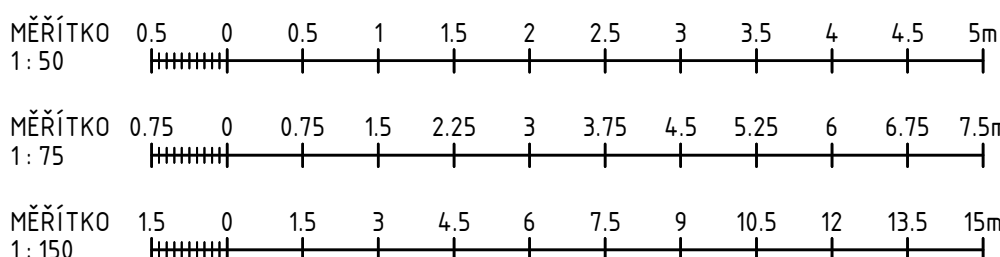
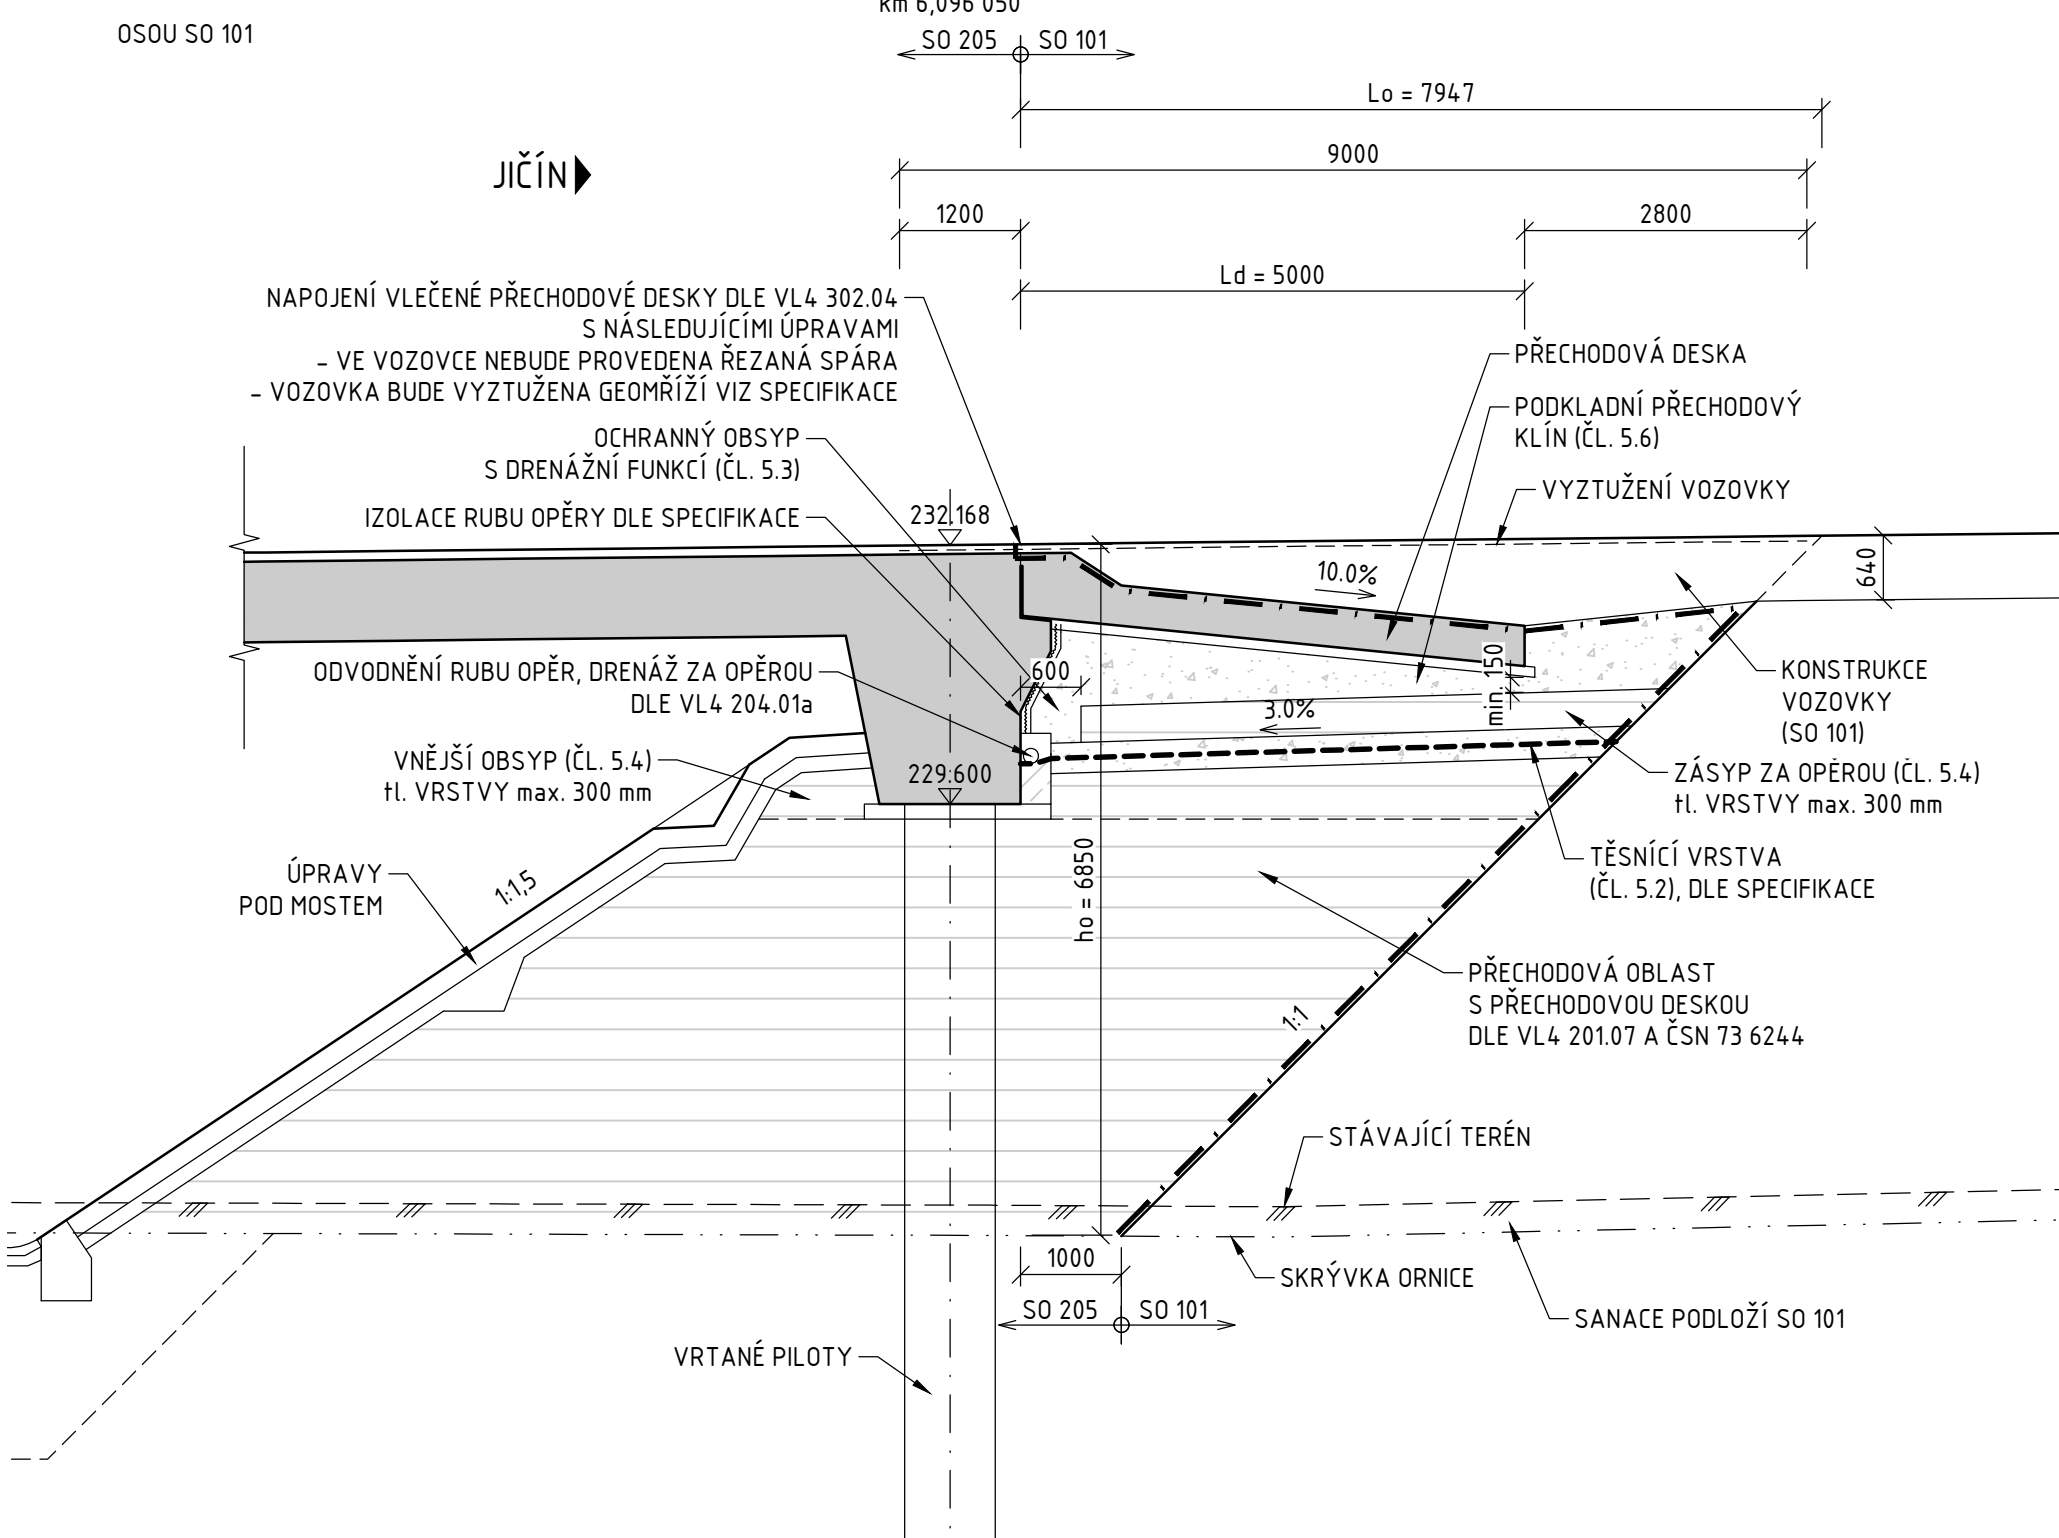


Souřadnicový systém: S-JTSK
Výškový systém: Bpv

SO 205 MOST NA I/16 PŘES PŘELOŽKU III/27612 V km 6,080

Objednatel:
ŘEDITELSTVÍ SILNIC A DÁLNIC
Ředitelství silnic a dálnic s. p.
Čerčanská 2023/12, Krč, 140 00 Praha 4

Valbek, spol. s r.o.
Vaňurova 505/17
460 07 Liberec 3

    Valbek	Vypracoval	ING. T. JAKUBÍČEK		Zak. číslo	21-L113-001
	Zodp. projektant	ING. I. BELDA		Datum	02/2025
	Tech. kontrola	ING. I. BELDA		Stupeň	PDPS
	Akce	I/16 MLADÁ BOLESLAV - MARTINOVICE			Počet formátů
Zhotovitel:		Příloha		Měřítko	1:150, 75, 50
Valbek, spol. s r.o. Vaňurova 505/17 460 07 Liberec 3		TVAR NOSNÉ KONSTRUKCE, PŘECHODOVÉ OBLASTI		Č. přílohy	Paré
					202