

PŘÍČNÝ ŘEZ 01 1:75

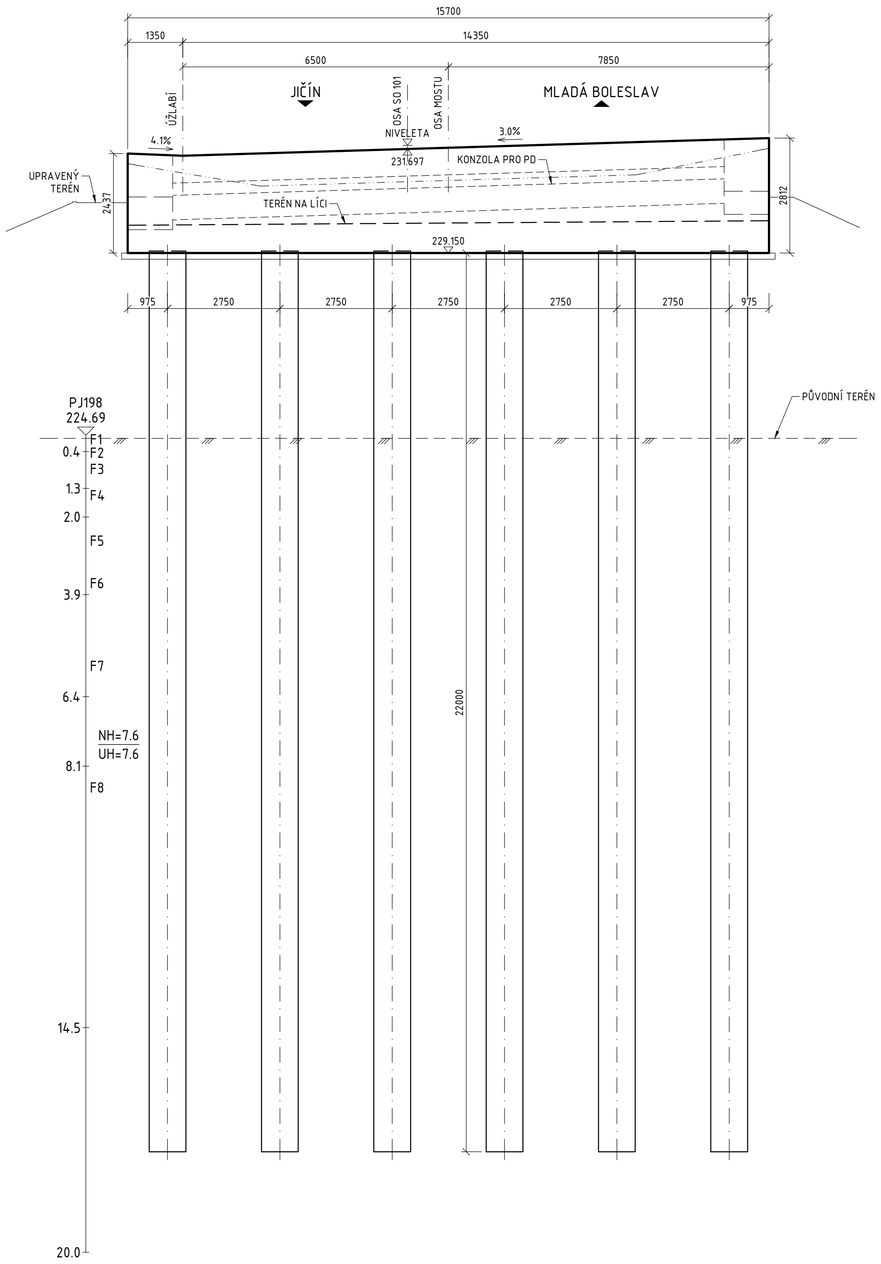

PŘÍČNÝ ŘEZ 04 1:75

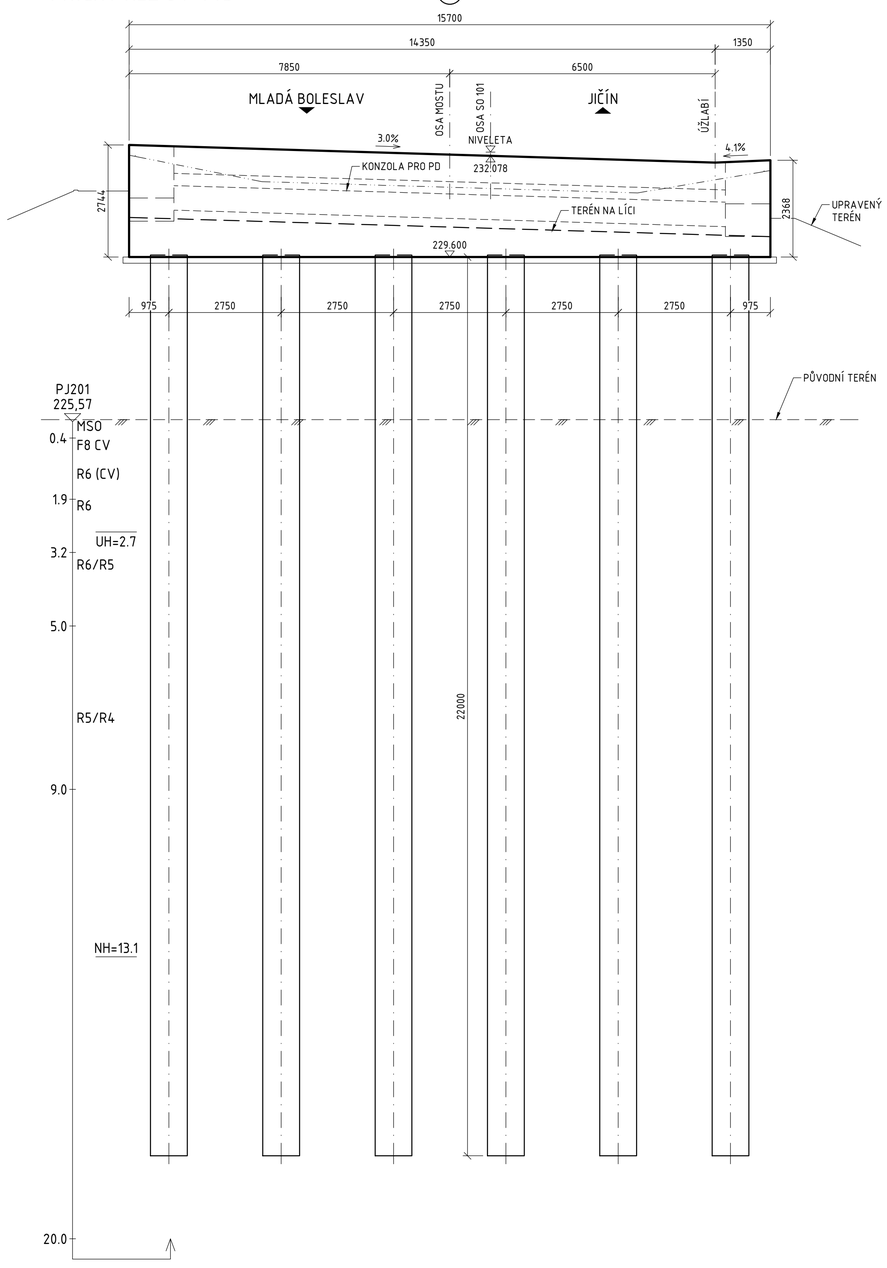

POZNÁMKY:

- NEDÍLNOU SOUČÁSTÍ VÝKRESU JSOU POZNÁMKY A SPECIFIKACE UVEDENÉ NA VÝKRESE POZNÁMEK A TECHNICKÝCH SPECIFIKACÍ

MĚŘÍTKO 1 : 75
0.75 0 0.75 1.5 2.25 3 3.75 4.5 5.25 6 6.75 7.5m

Souřadnicový systém: S-JTSK
Výškový systém: Bpv

SO 205 MOST NA I/16 PŘES PŘELOŽKU III/27612 V km 6,080

Objednatel:
ŘEDITELSTVÍ SILNIC A DÁLNIC
Ředitelství silnic a dálnic s. p.
Čerčanská 2023/12, Krč, 140 00 Praha 4

Valbek
Valbek, spol. s r.o.
Vaňurova 505/17
460 07 Liberec 3

Valbek	Vypracoval	ING. T. JAKUBÍČEK		Zak. číslo	21-LI13-001
	Zodp. projektant	ING. I. BELDA		Datum	02/2025
	Tech. kontrola	ING. I. BELDA		Stupeň	PDPS
	Akce	I/16 MLADÁ BOLESLAV - MARTINOVICE		Počet formátů	8 x A4
				Měřítko	1:75
				Č. přílohy	Paré
Zhotovitel: Valbek, spol. s r.o. Vaňurova 505/17 460 07 Liberec 3	Příloha	TVAR PŘÍČNÍKŮ		203	