



SCHÉMA ODVODNĚNÍ

PODÉLNÝ ŘEZ ODVODNĚNÍM 1:100

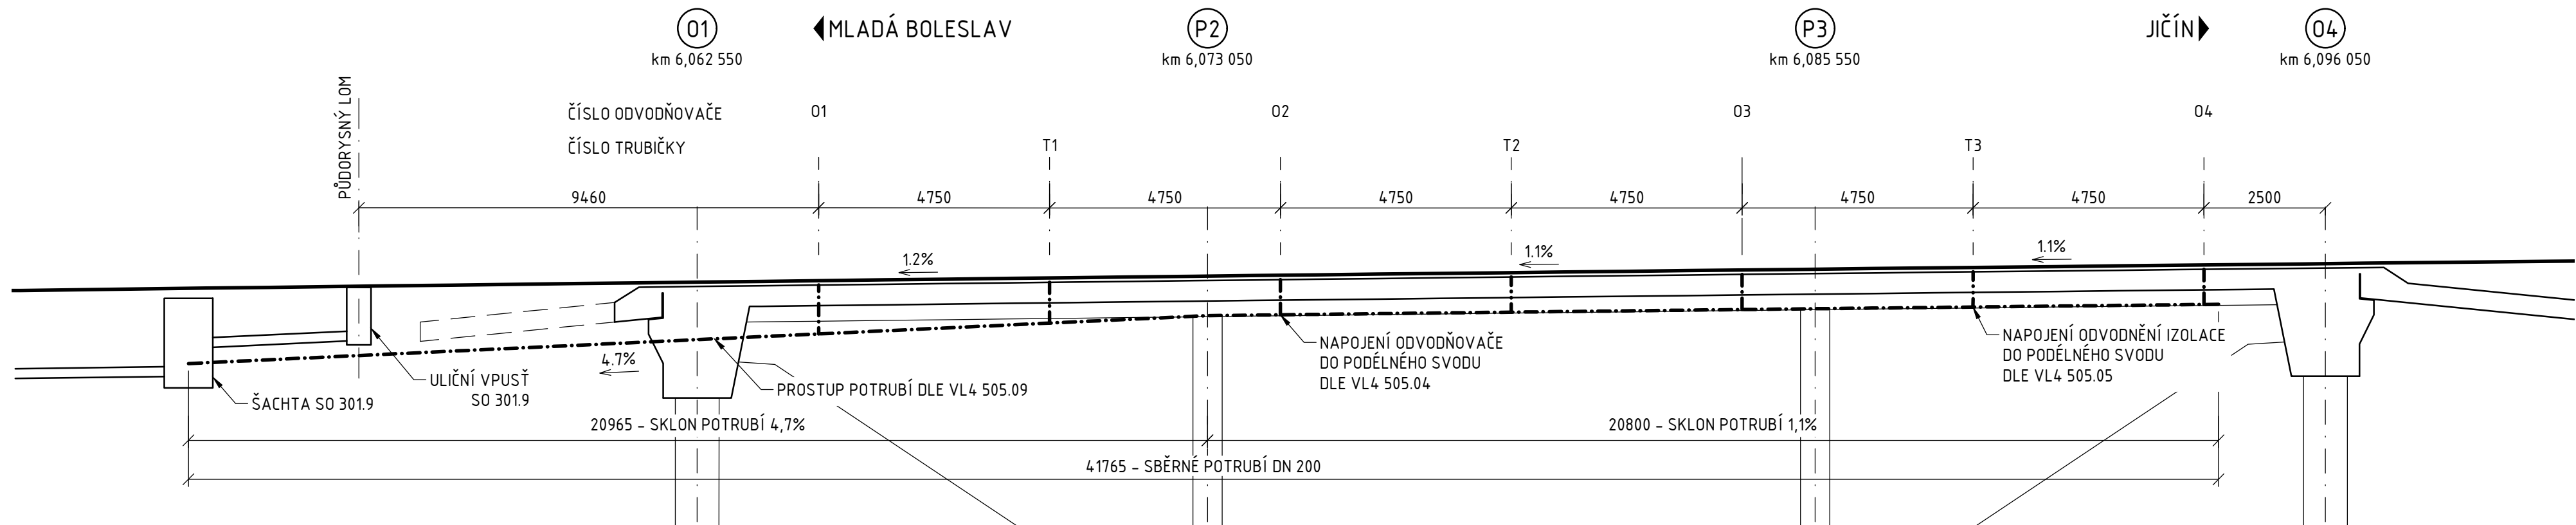


TVAR ŘÍMS

PŮDORYS 1:100

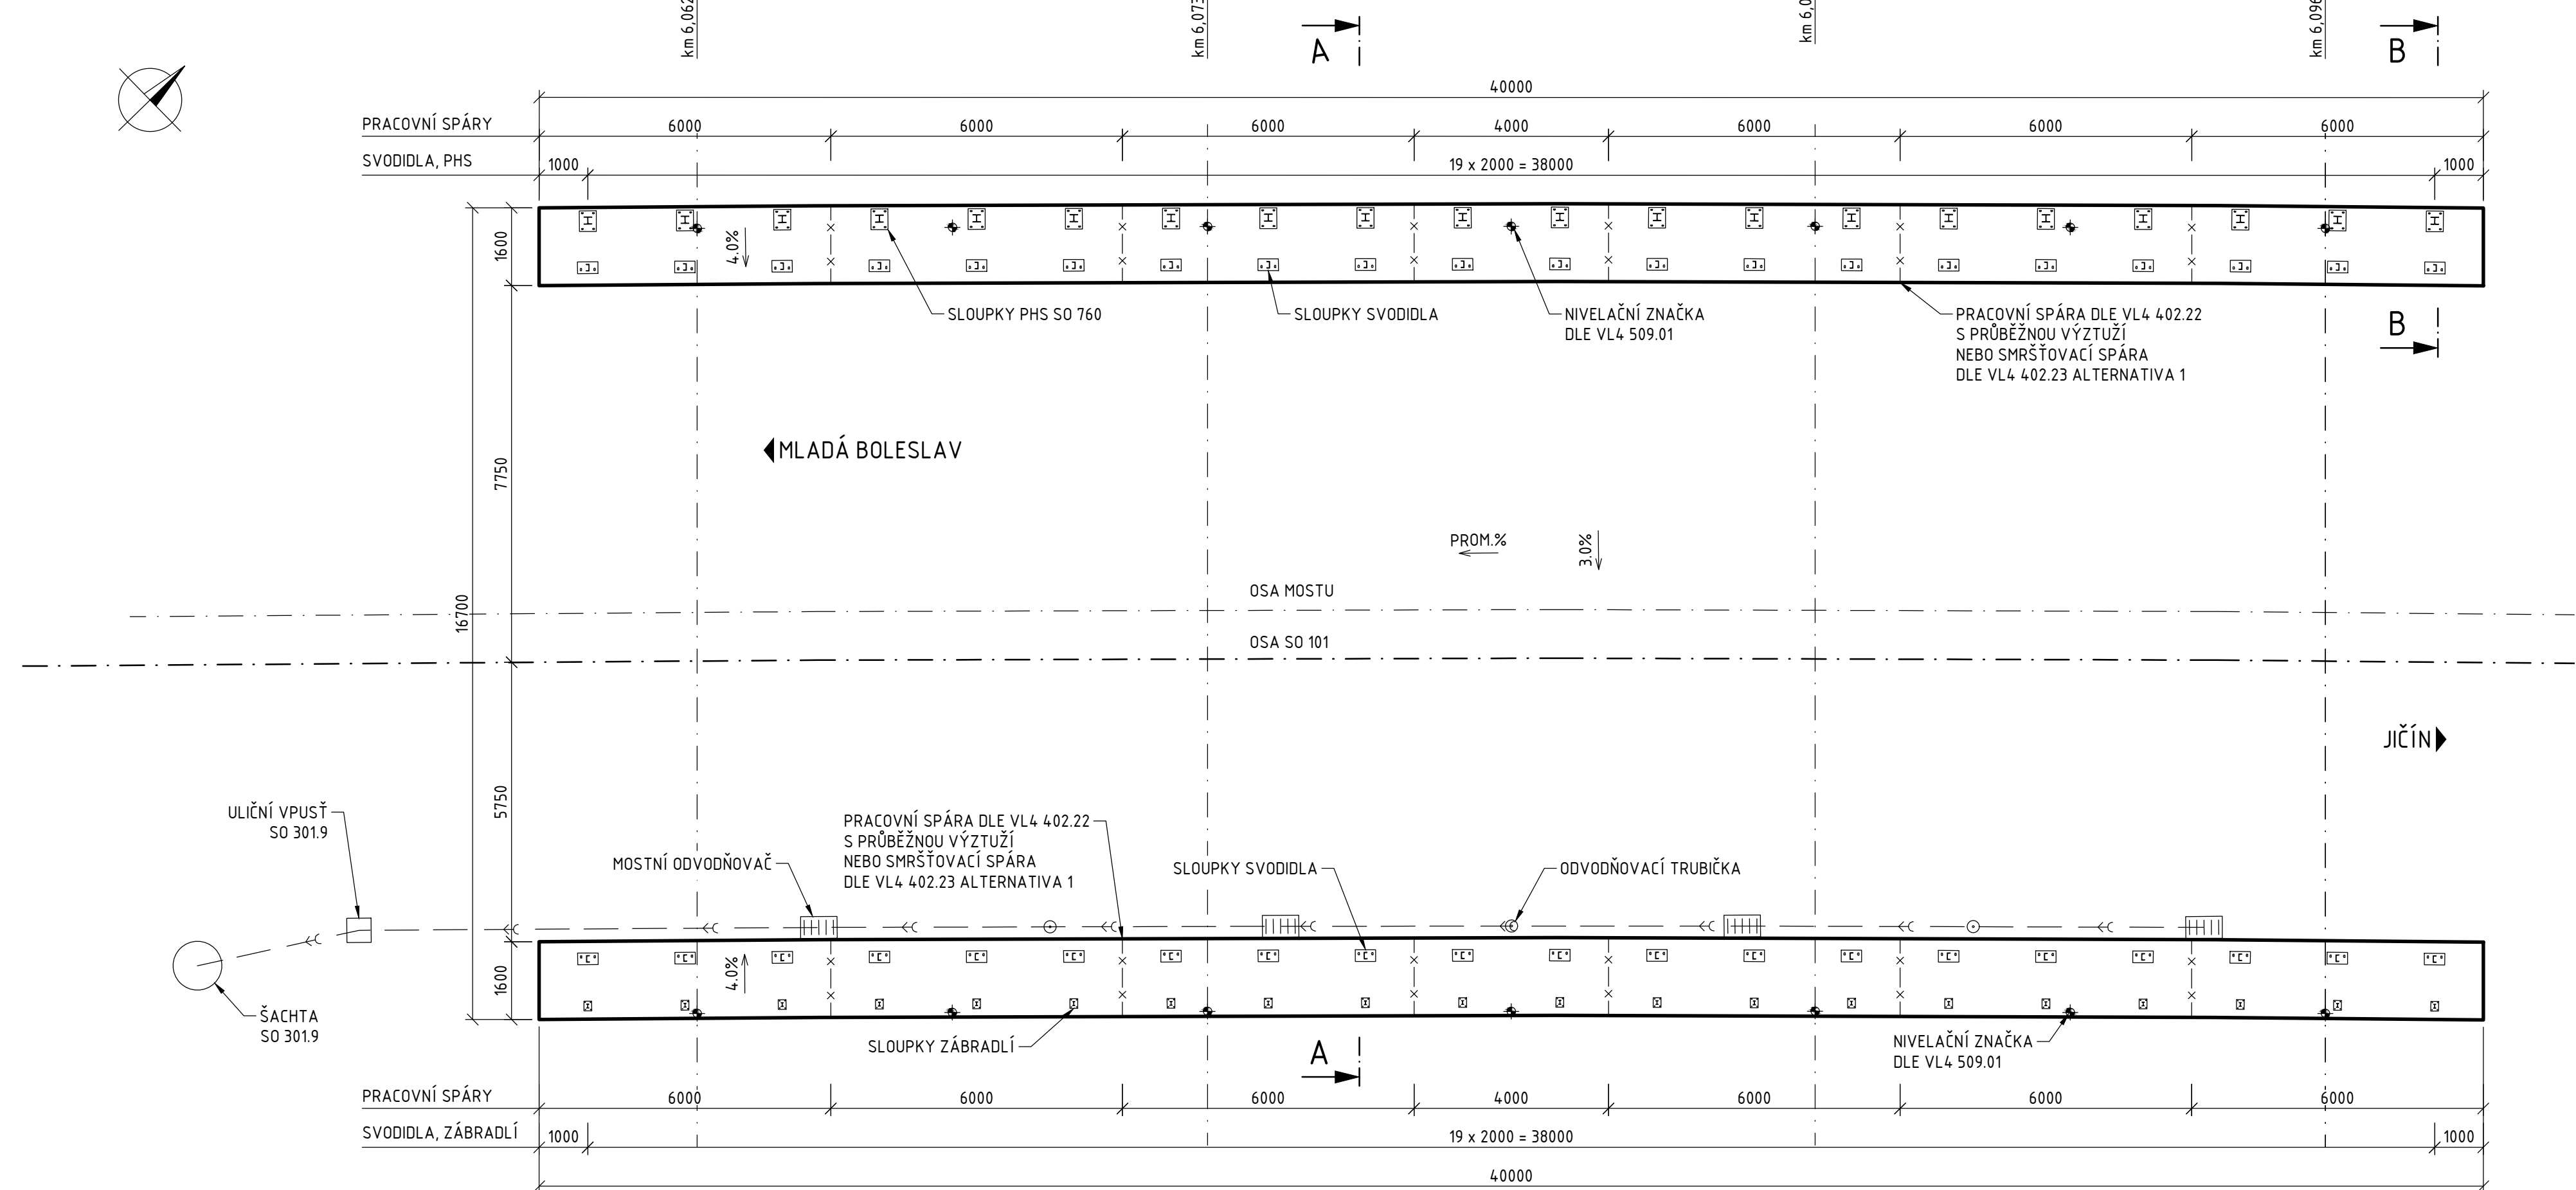


ŘEZ A-A 1:20

LEVÁ ŘÍMSA


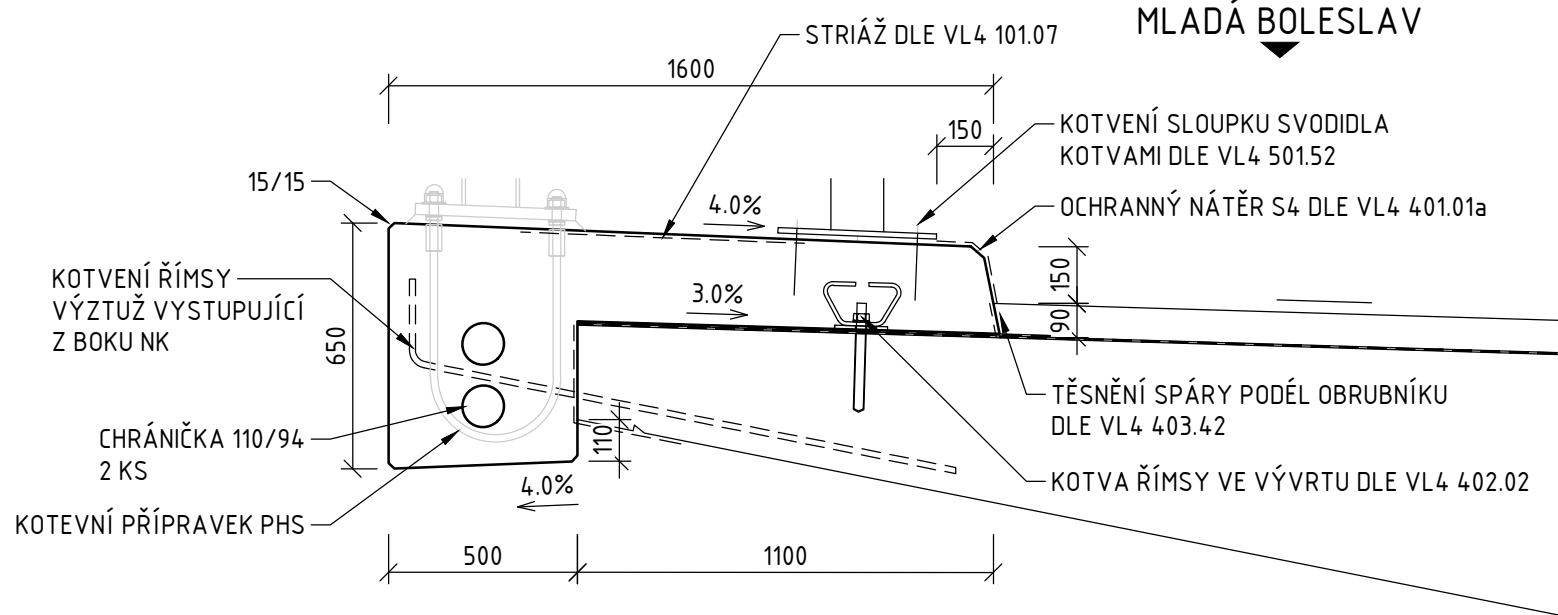


PRAVÁ ŘÍMSA

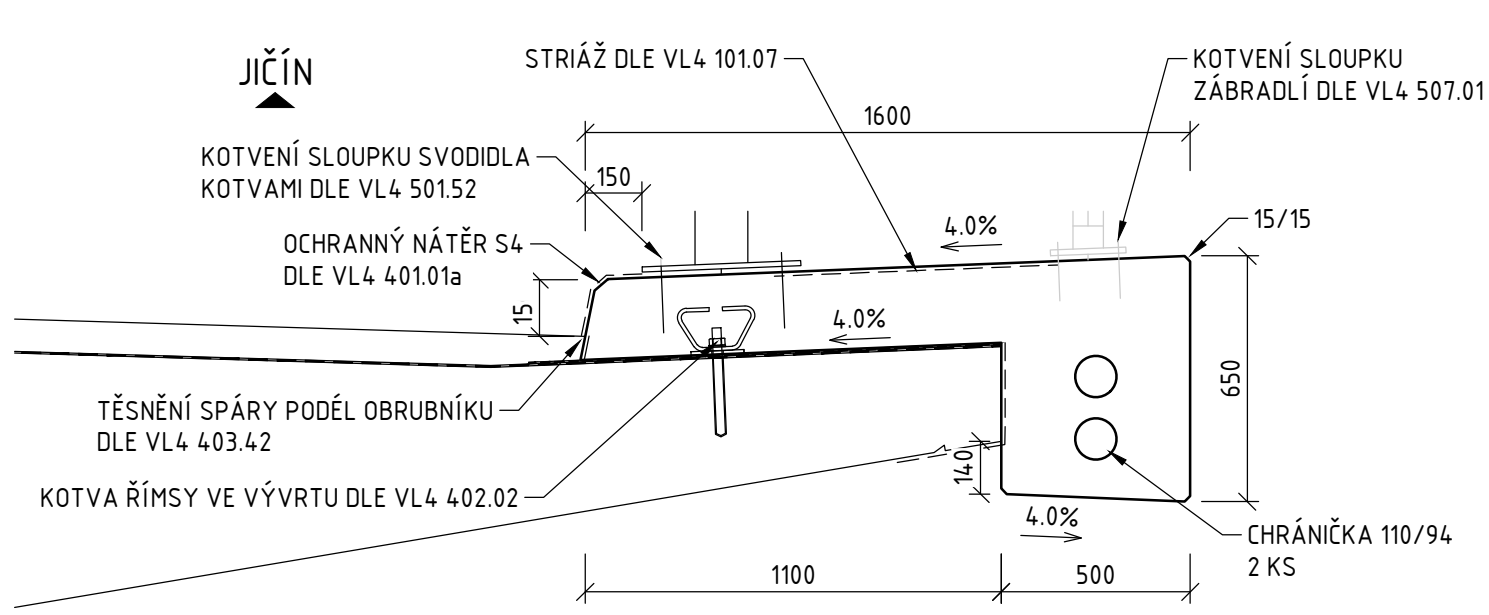


ŘEZ B-B 1:20


LEVÁ ŘÍMSA (PRAVÁ ŘÍMSA ODOBNĚ)

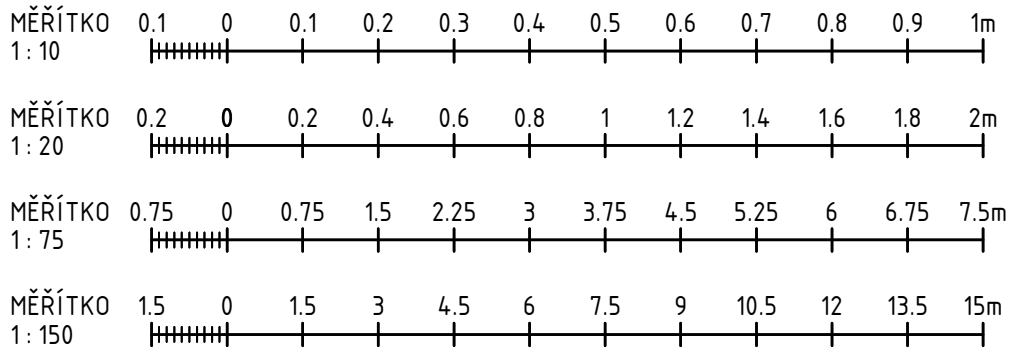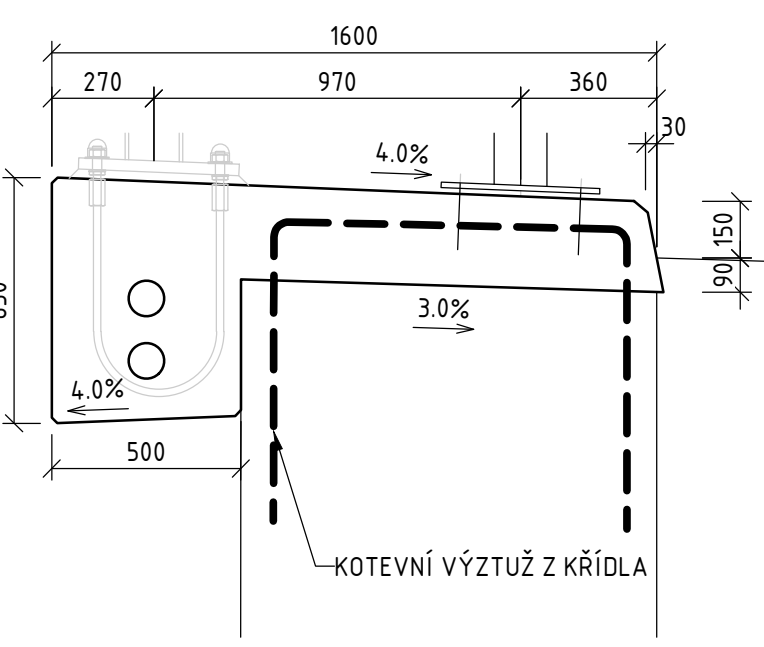

PŘÍČNÝ ŘEZ 1:75

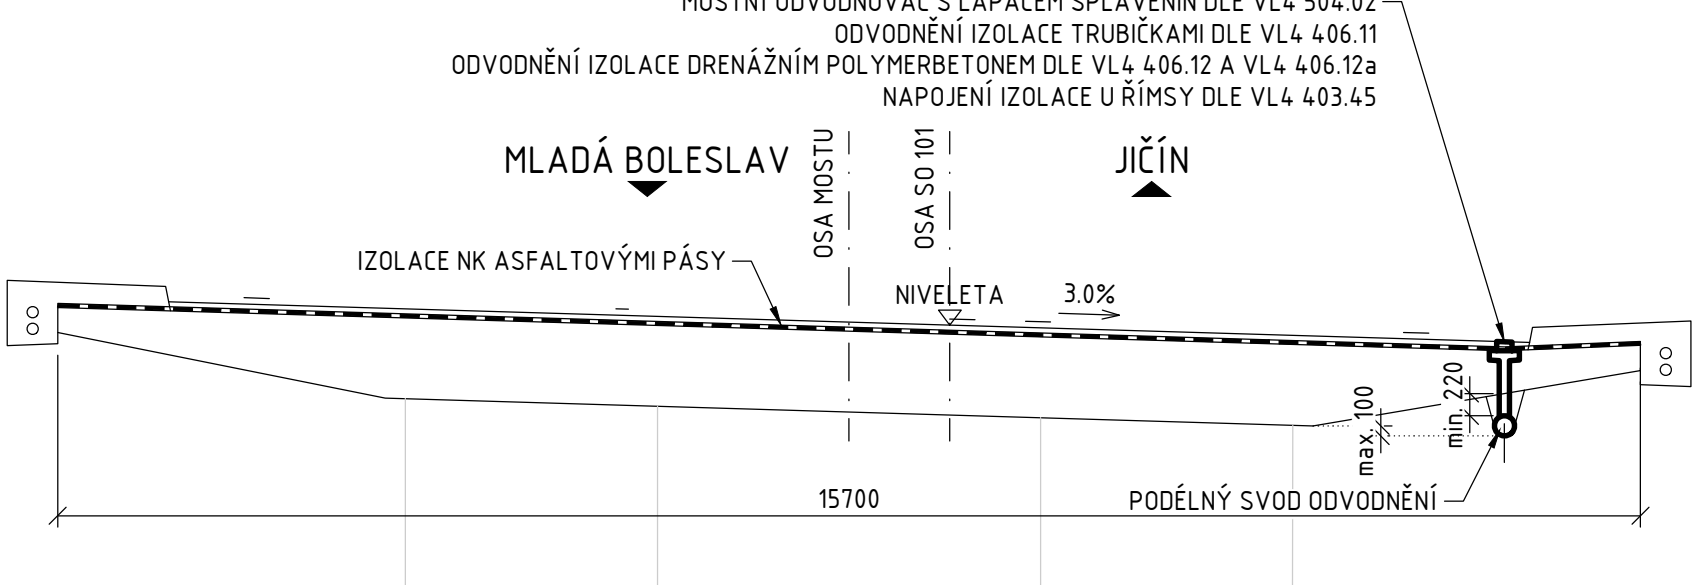

DETAIL KOTEVNÍHO PŘÍPRAVKU PHS 1:10

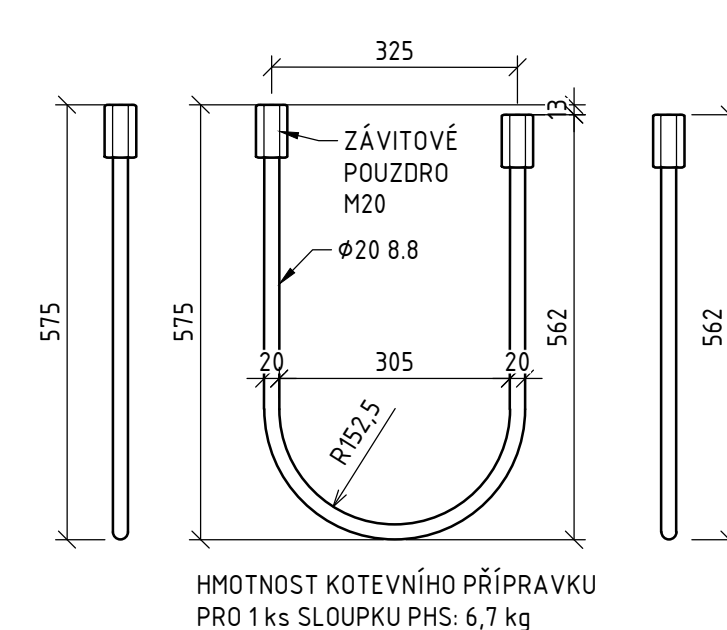

POZNÁMKY:

- NEDÍLNOU SOUČÁSTÍ VÝKRESU JSOU POZNÁMKY A SPECIFIKACE UVEDENÉ NA VÝKRESE POZNÁMEK A TECHNICKÝCH SPECIFIKACÍ

Souřadnicový systém: S-JTSK
Výškový systém: Bpv

SO 205 MOST NA I/16 PŘES PŘELOŽKU III/27612 V km 6,080

Objednatel:
ŘEDITELSTVÍ SILNIC A DÁLNIC
Ředitelství silnic a dálnic s. p.
Čerčanská 2023/12, Krč, 140 00 Praha 4

Valbek, spol. s r.o.
Vaňurova 505/17
460 07 Liberec 3

	Vypracoval	ING. T. JAKUBÍČEK	Zak. číslo	21-L113-001	
	Zodp. projektant	ING. I. BELDA	Datum	02/2025	
	Tech. kontrola	ING. I. BELDA	Stupeň	PDPS	
	Akce	I/16 MLADÁ BOLESLAV - MARTINOVICE			
Zhotovitel: Valbek, spol. s r.o. Vaňurova 505/17 460 07 Liberec 3	Příloha TVAR ŘÍMS, SCHÉMA ODVODNĚNÍ			Počet formátů	8 x A4
				Měřítko	1:100, 75, 20, 10
				Č. přílohy	Paré
204					