



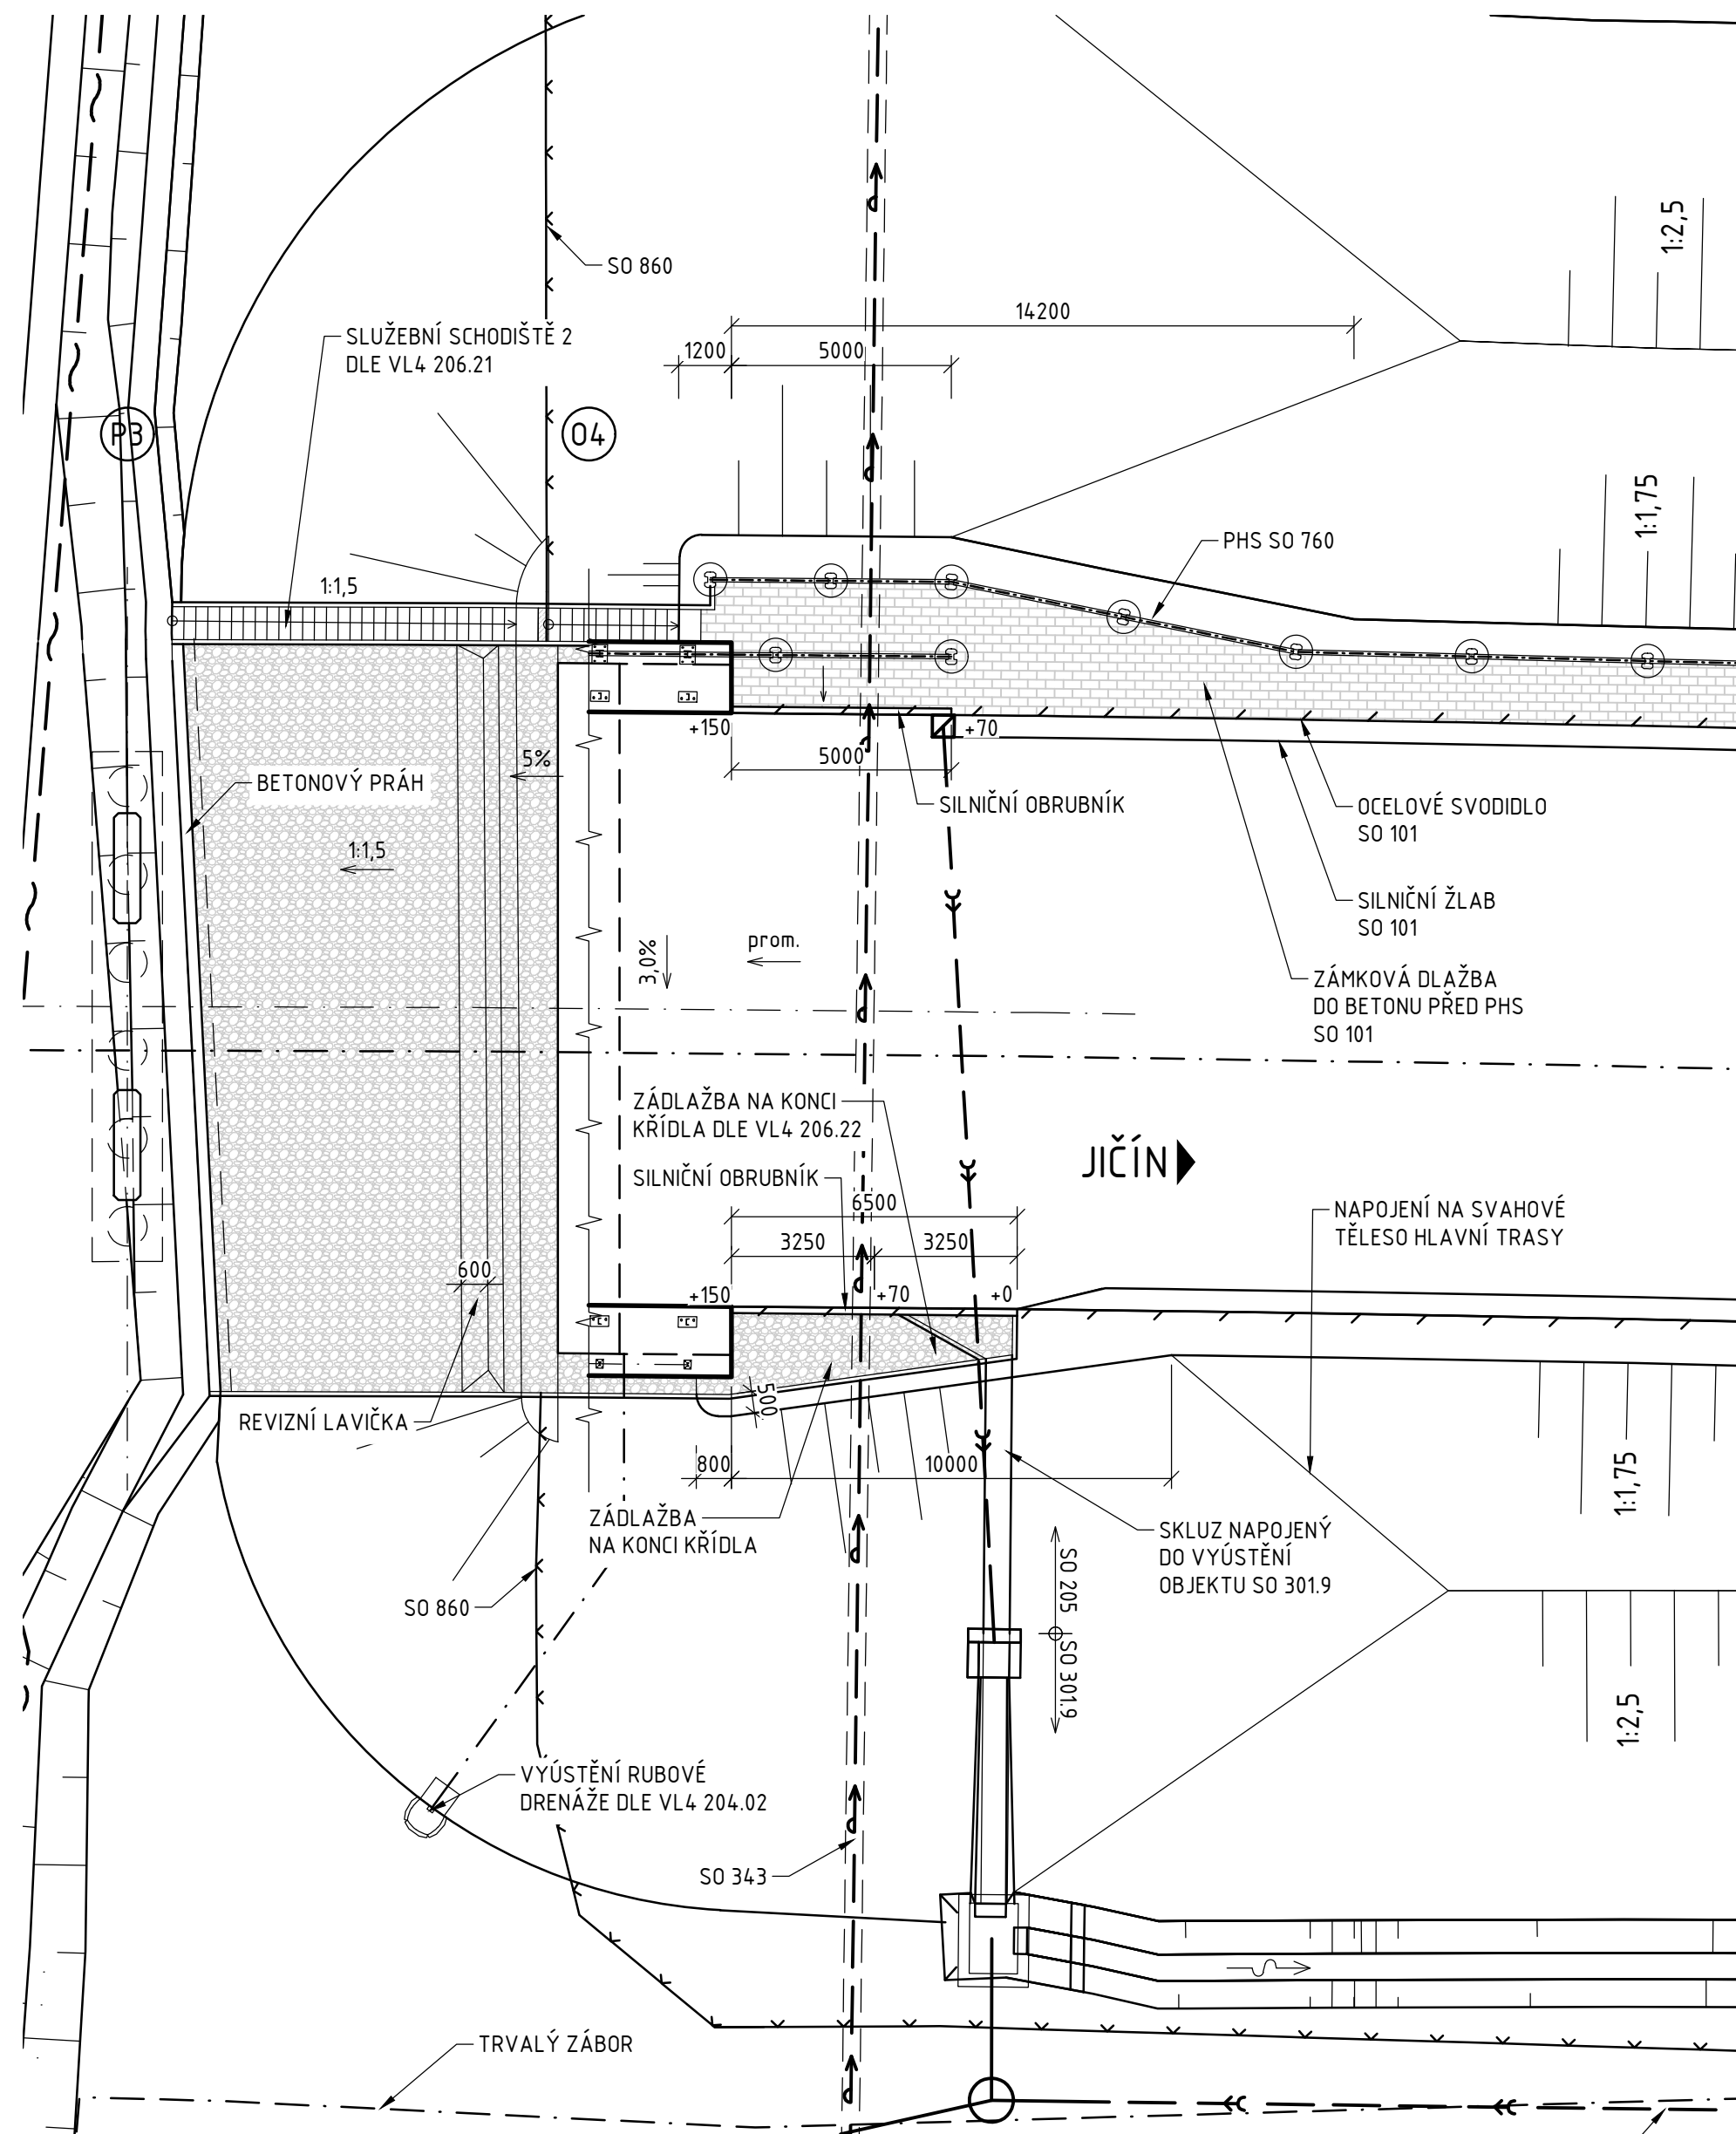

- NEDÍLNOU SOUČÁSTÍ VÝKRESU JSOU POZNÁMKY A SPECIFIKACE UVEDENÉ NA VÝKRESE
POZNÁMEK A TECHNICKÝCH SPECIFIKACÍ

SCHODIŠTĚ 1 – PODÉLNÝ ŘEZ 1:75

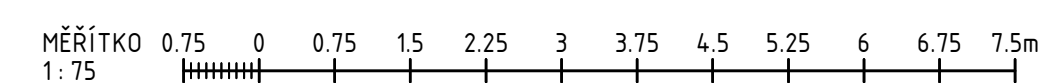

SO 205 MOST NA I/16 PŘES PŘELOŽKU III/27612 V km 6,080



Vypracoval	ING. T. JAKUBÍČEK		Zak. číslo	21-L1-101-001
Zodp. projektant	ING. I. BELDA		Datum	02/2025
Tech. kontrola	ING. I. BELDA		Stupeň	PDPS
Akce			Počet formátů	8 x A4
I/16 MLADÁ BOLESLAV - MARTINOVICE			Měřítko	1:150, 75

Zhotovitel:
Valbek, spol. s r.o.
Vaňurova 505/17
460 07 Liberec 3

Příloha
ÚPRAVY POD MOSTEM, SLUŽEBNÍ SCHODIŠTĚ

205