

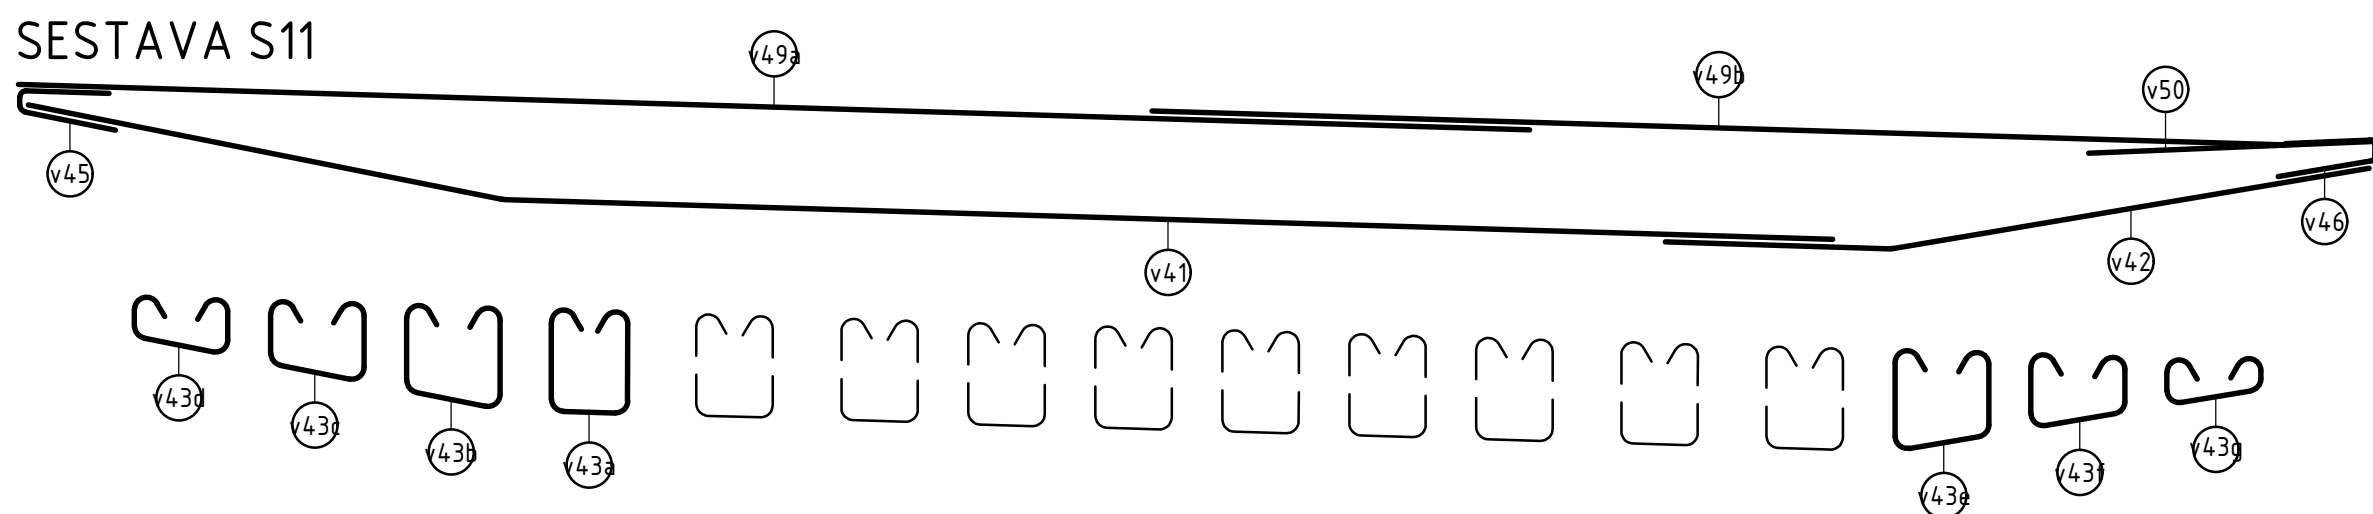
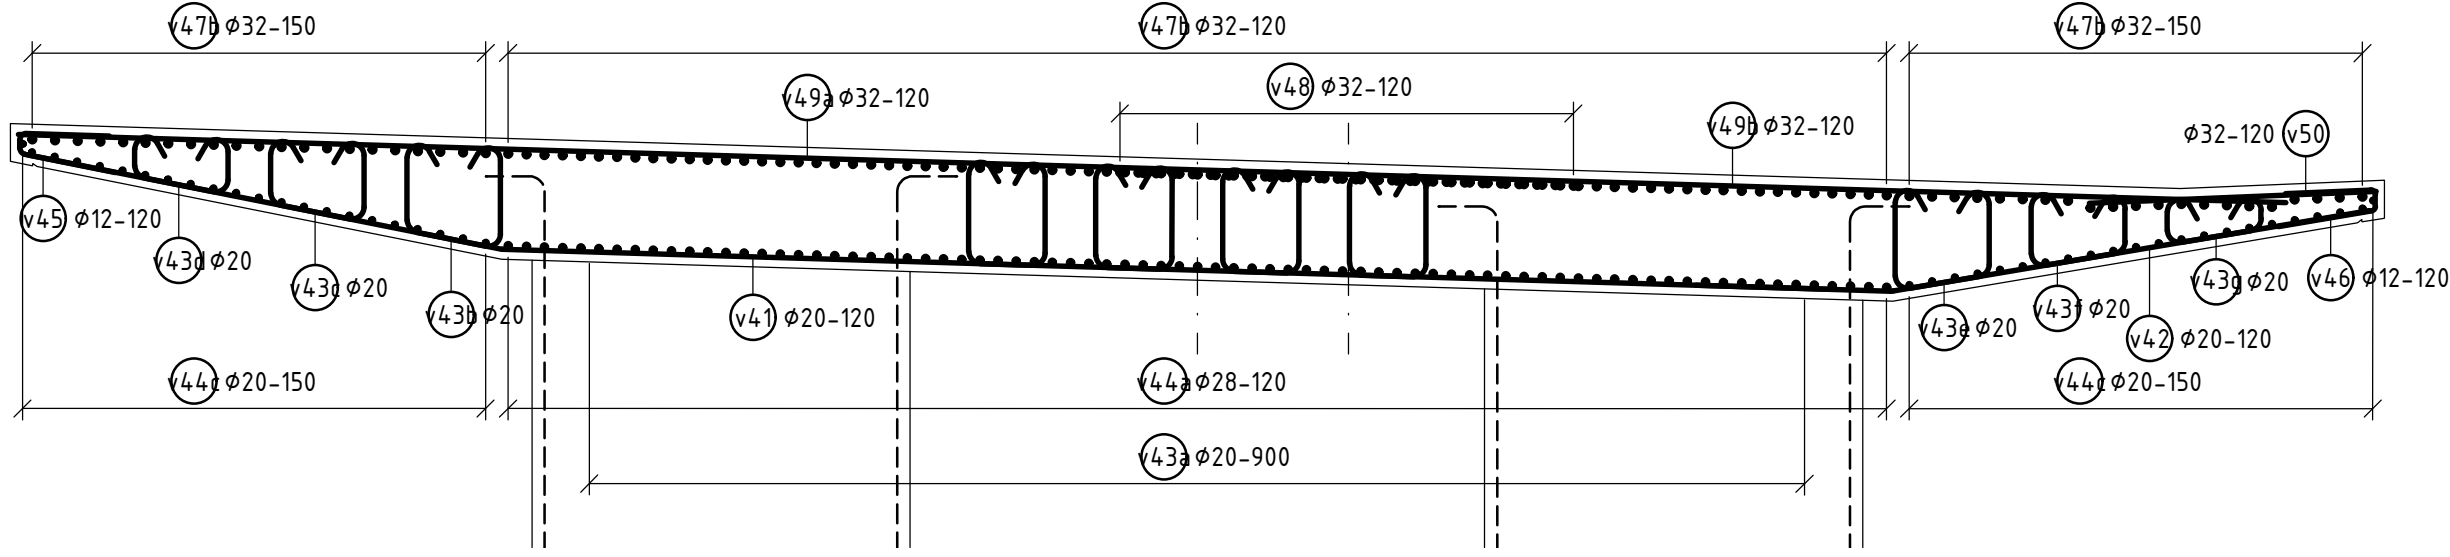


SCHÉMA VÝZTUŽE NOSNÉ KONSTRUKCE  
PŘÍČNÝ ŘEZ NAD PODPOROU 1:50

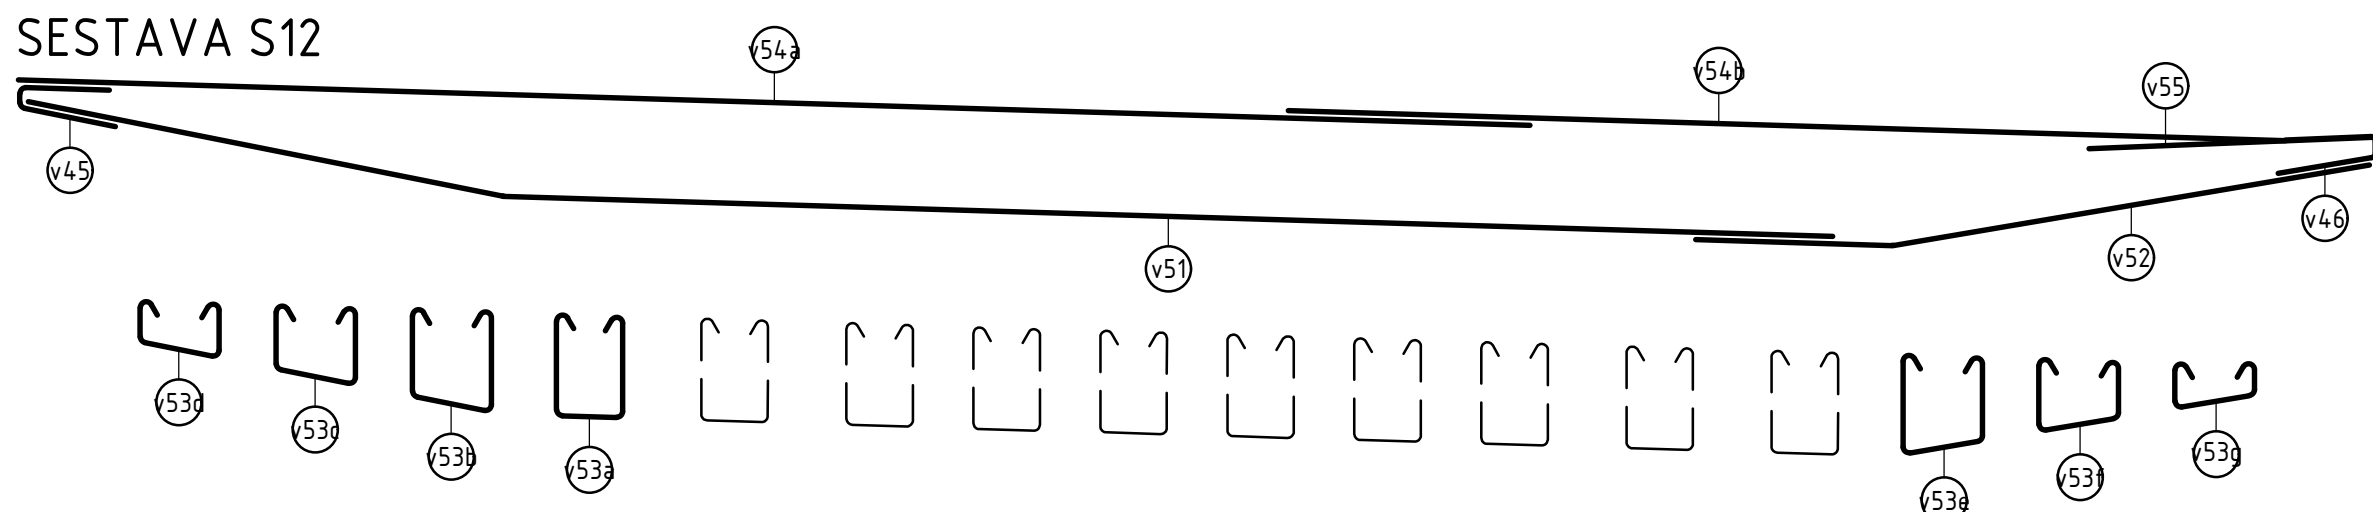

PŘÍČNÝ ŘEZ V POLI 1:50

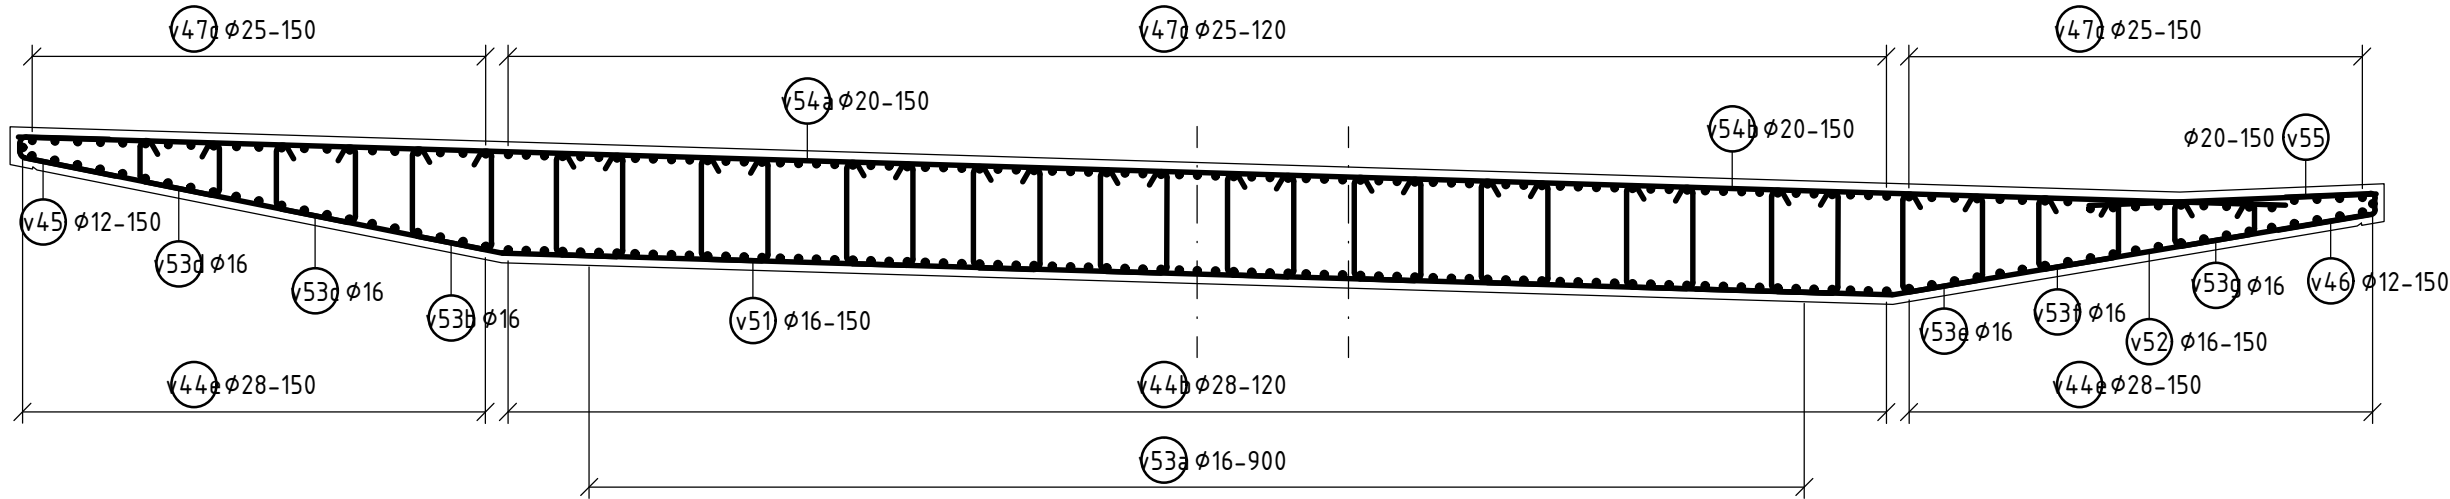

PŘÍČNÝ ŘEZ NAD OPĚROU 1:50



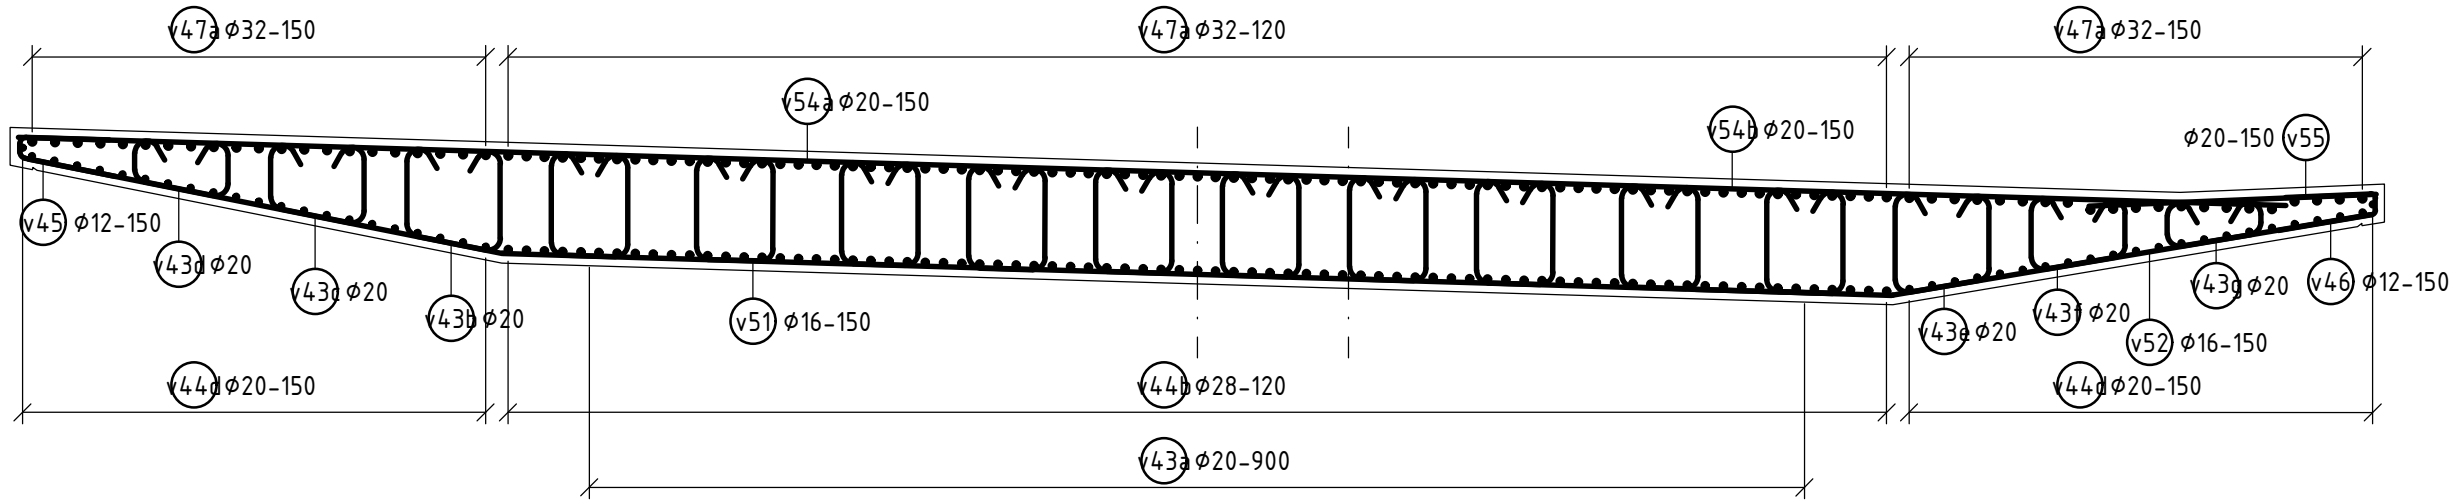


SCHÉMA VÝZTUŽE PŘÍČNÍKU 1:50

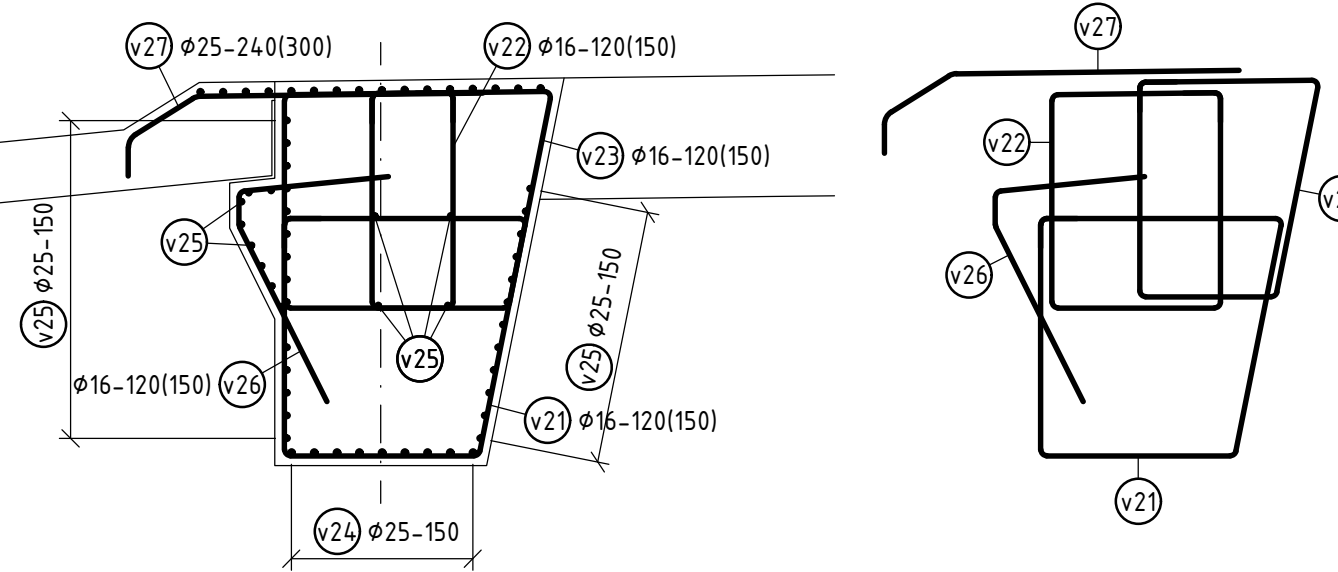

ŘEZ KŘÍDLEM 1:50

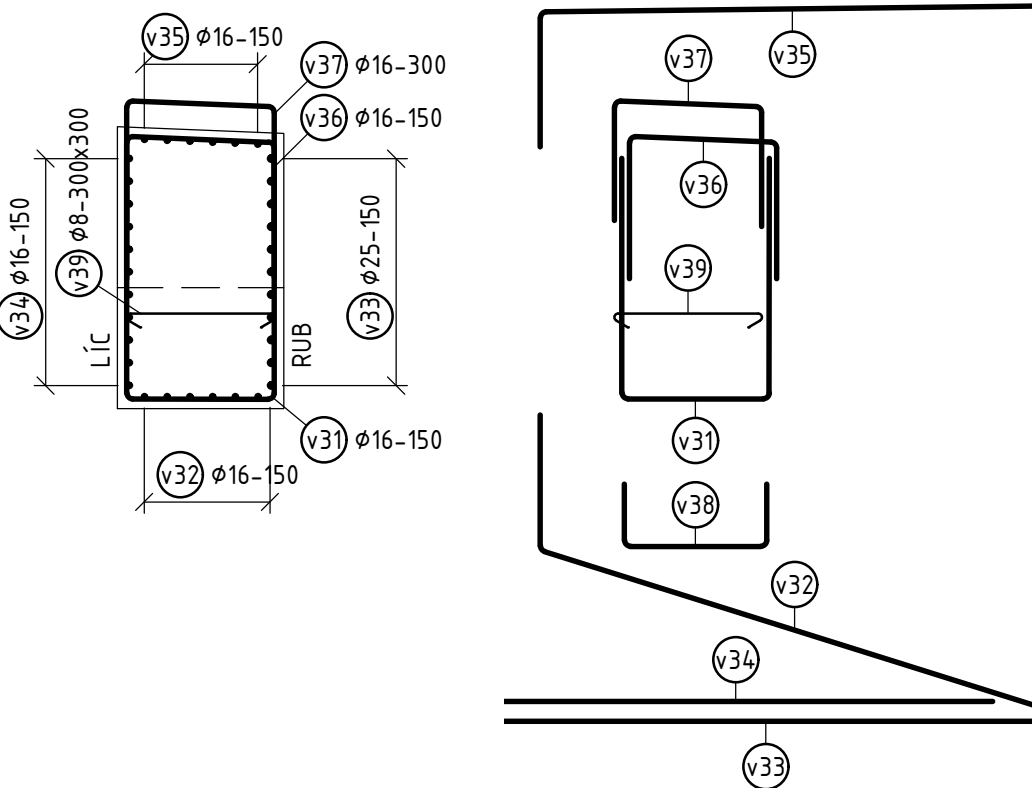

PODÉLNÝ ŘEZ 1:100



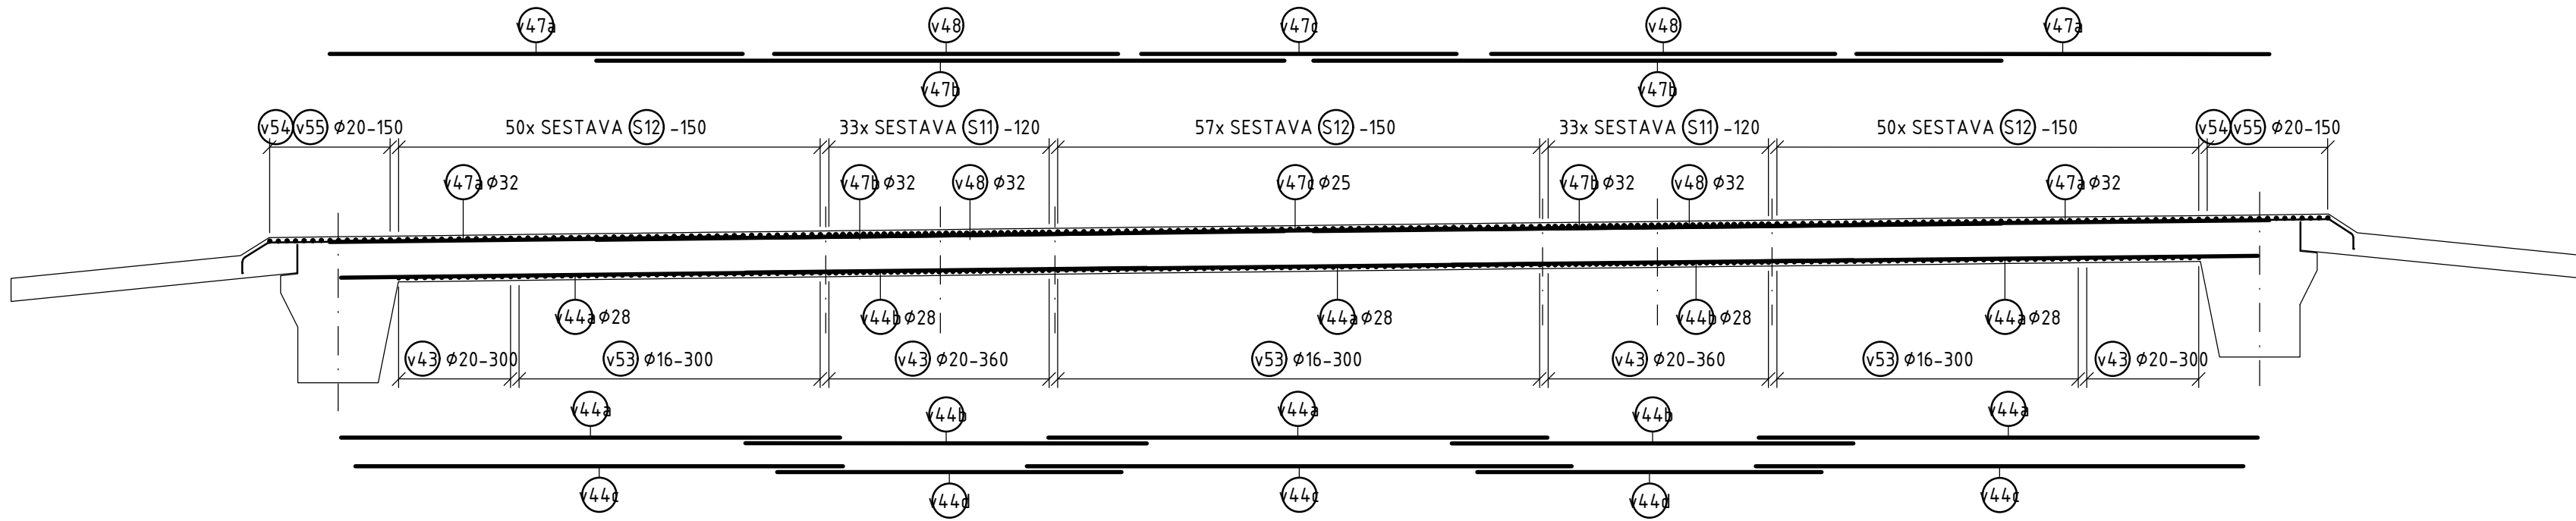



SCHÉMA VÝZTUŽE PILÍŘE 1:50

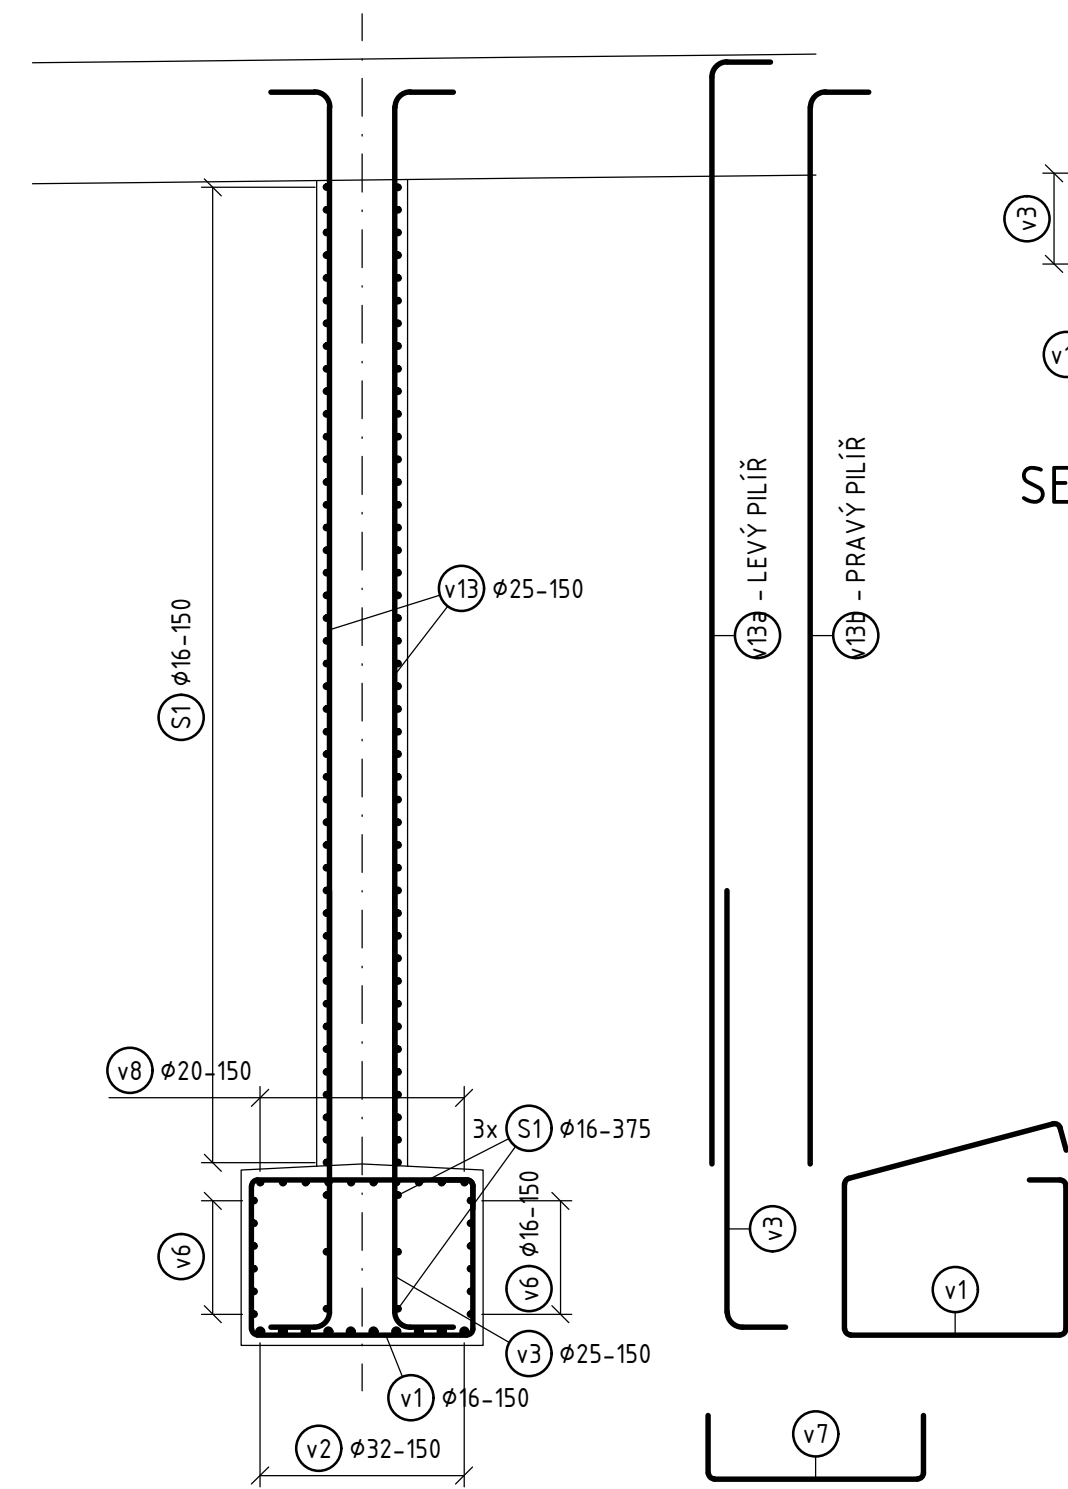


PŮDORYS DŘÍKU PILÍŘE 1:25

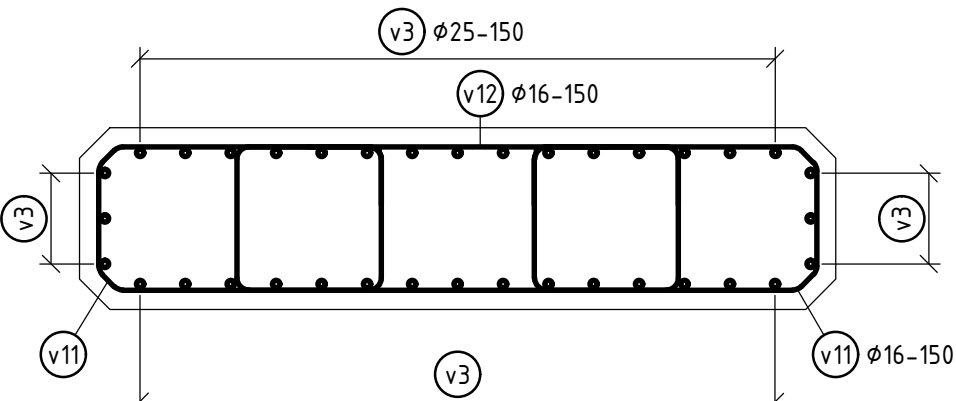

SESTAVA S1

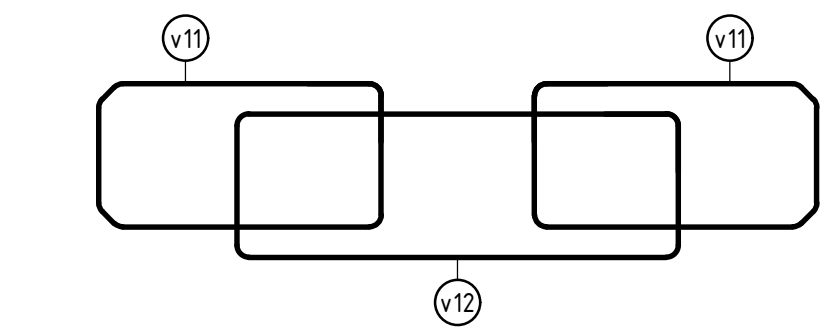

SESTAVA S1 V ZÁKLADU PILÍŘE 1:25

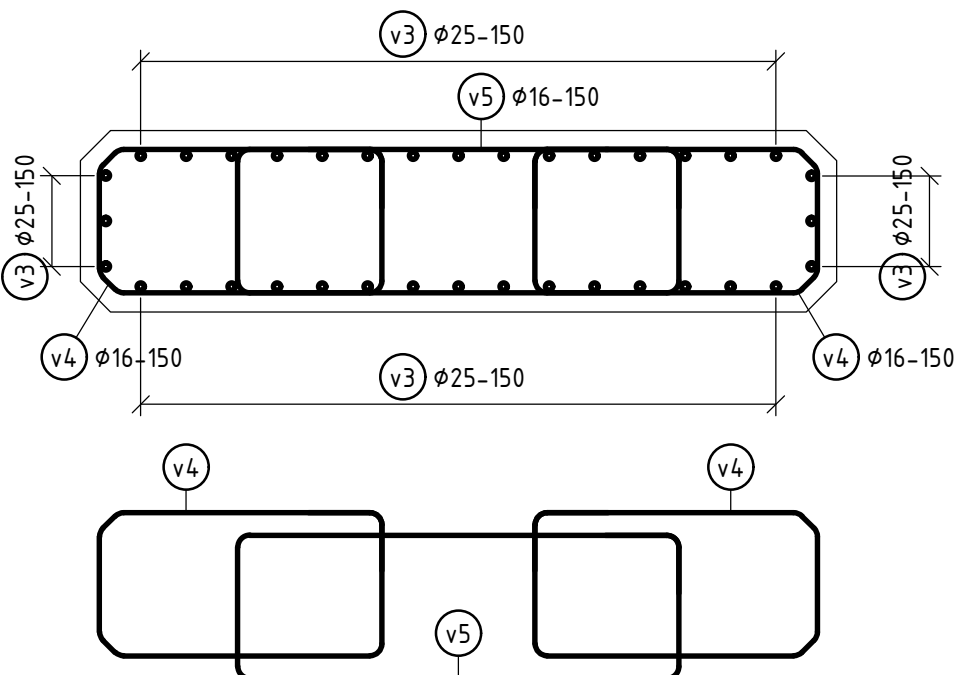

| ODHAD MNOŽSTVÍ BETONÁŘSKÉ VÝZTUŽE SO 205 | MNOŽSTVÍ VÝZTUŽE V % | MNOŽSTVÍ VÝZT.V KG/M3 |
|------------------------------------------|----------------------|-----------------------|
| VÝZTUŽ PILOT POD OPĚROU 01, D 900 mm     | 3.31%                | 260.0                 |
| VÝZTUŽ PILOT POD OPĚROU 04, D 900 mm     | 3.31%                | 260.0                 |
| VÝZTUŽ PILOT POD PILÍŘEM P2, D 900 mm    | 1.15%                | 90.0                  |
| VÝZTUŽ PILOT POD PILÍŘEM P3, D 900 mm    | 1.15%                | 90.0                  |
| VÝZTUŽ ZÁKLADŮ PILÍŘE P2                 | 3.18%                | 250.0                 |
| VÝZTUŽ ZÁKLADŮ PILÍŘE P3                 | 3.18%                | 250.0                 |
| VÝZTUŽ PILÍŘE P2                         | 3.18%                | 250.0                 |
| VÝZTUŽ PILÍŘE P3                         | 3.18%                | 250.0                 |
| VÝZTUŽ NOSNÉ KONSTRUKCE                  | 2.68%                | 210.0                 |
| VÝZTUŽ ŘÍMS                              | 1.78%                | 140.0                 |
| VÝZTUŽ PŘECHODOVÝCH DESEK                | 1.66%                | 130.0                 |

POZNÁMKY:

- NEDÍLNOU SOUČÁSTÍ VÝKRESU JSOU POZNÁMKY A SPECIFIKACE UVEDENÉ NA VÝKRESE POZNÁMEK A TECHNICKÝCH SPECIFIKACÍ

Souřadnicový systém: S-JTSK  
Výškový systém: Bpv

SO 205 MOST NA I/16 PŘES PŘELOŽKU III/27612 V km 6,080

Objednatel:



Ředitelství silnic a dálnic s. p.  
Čerčanská 2023/12, Krč, 140 00 Praha 4



Valbek, spol. s r.o.  
Vaňurova 505/17  
460 07 Liberec 3



Zhotovitel:  
Valbek, spol. s r.o.  
Vaňurova 505/17  
460 07 Liberec 3

Vypracoval  
Zodp. projektant  
Tech. kontrola  
Akce

L.MARTINEK  
ING. I. BELDA  
ING. I. BELDA  
I/16 MLADÁ BOLESLAV - MARTINOVICE

Zak. číslo  
Datum  
Stupeň  
Počet formátů  
Měřítko  
Č. přílohy

21-L113-001  
02/2025  
PDPS  
8 x A4  
1:100, 50, 25  
Paré

301