


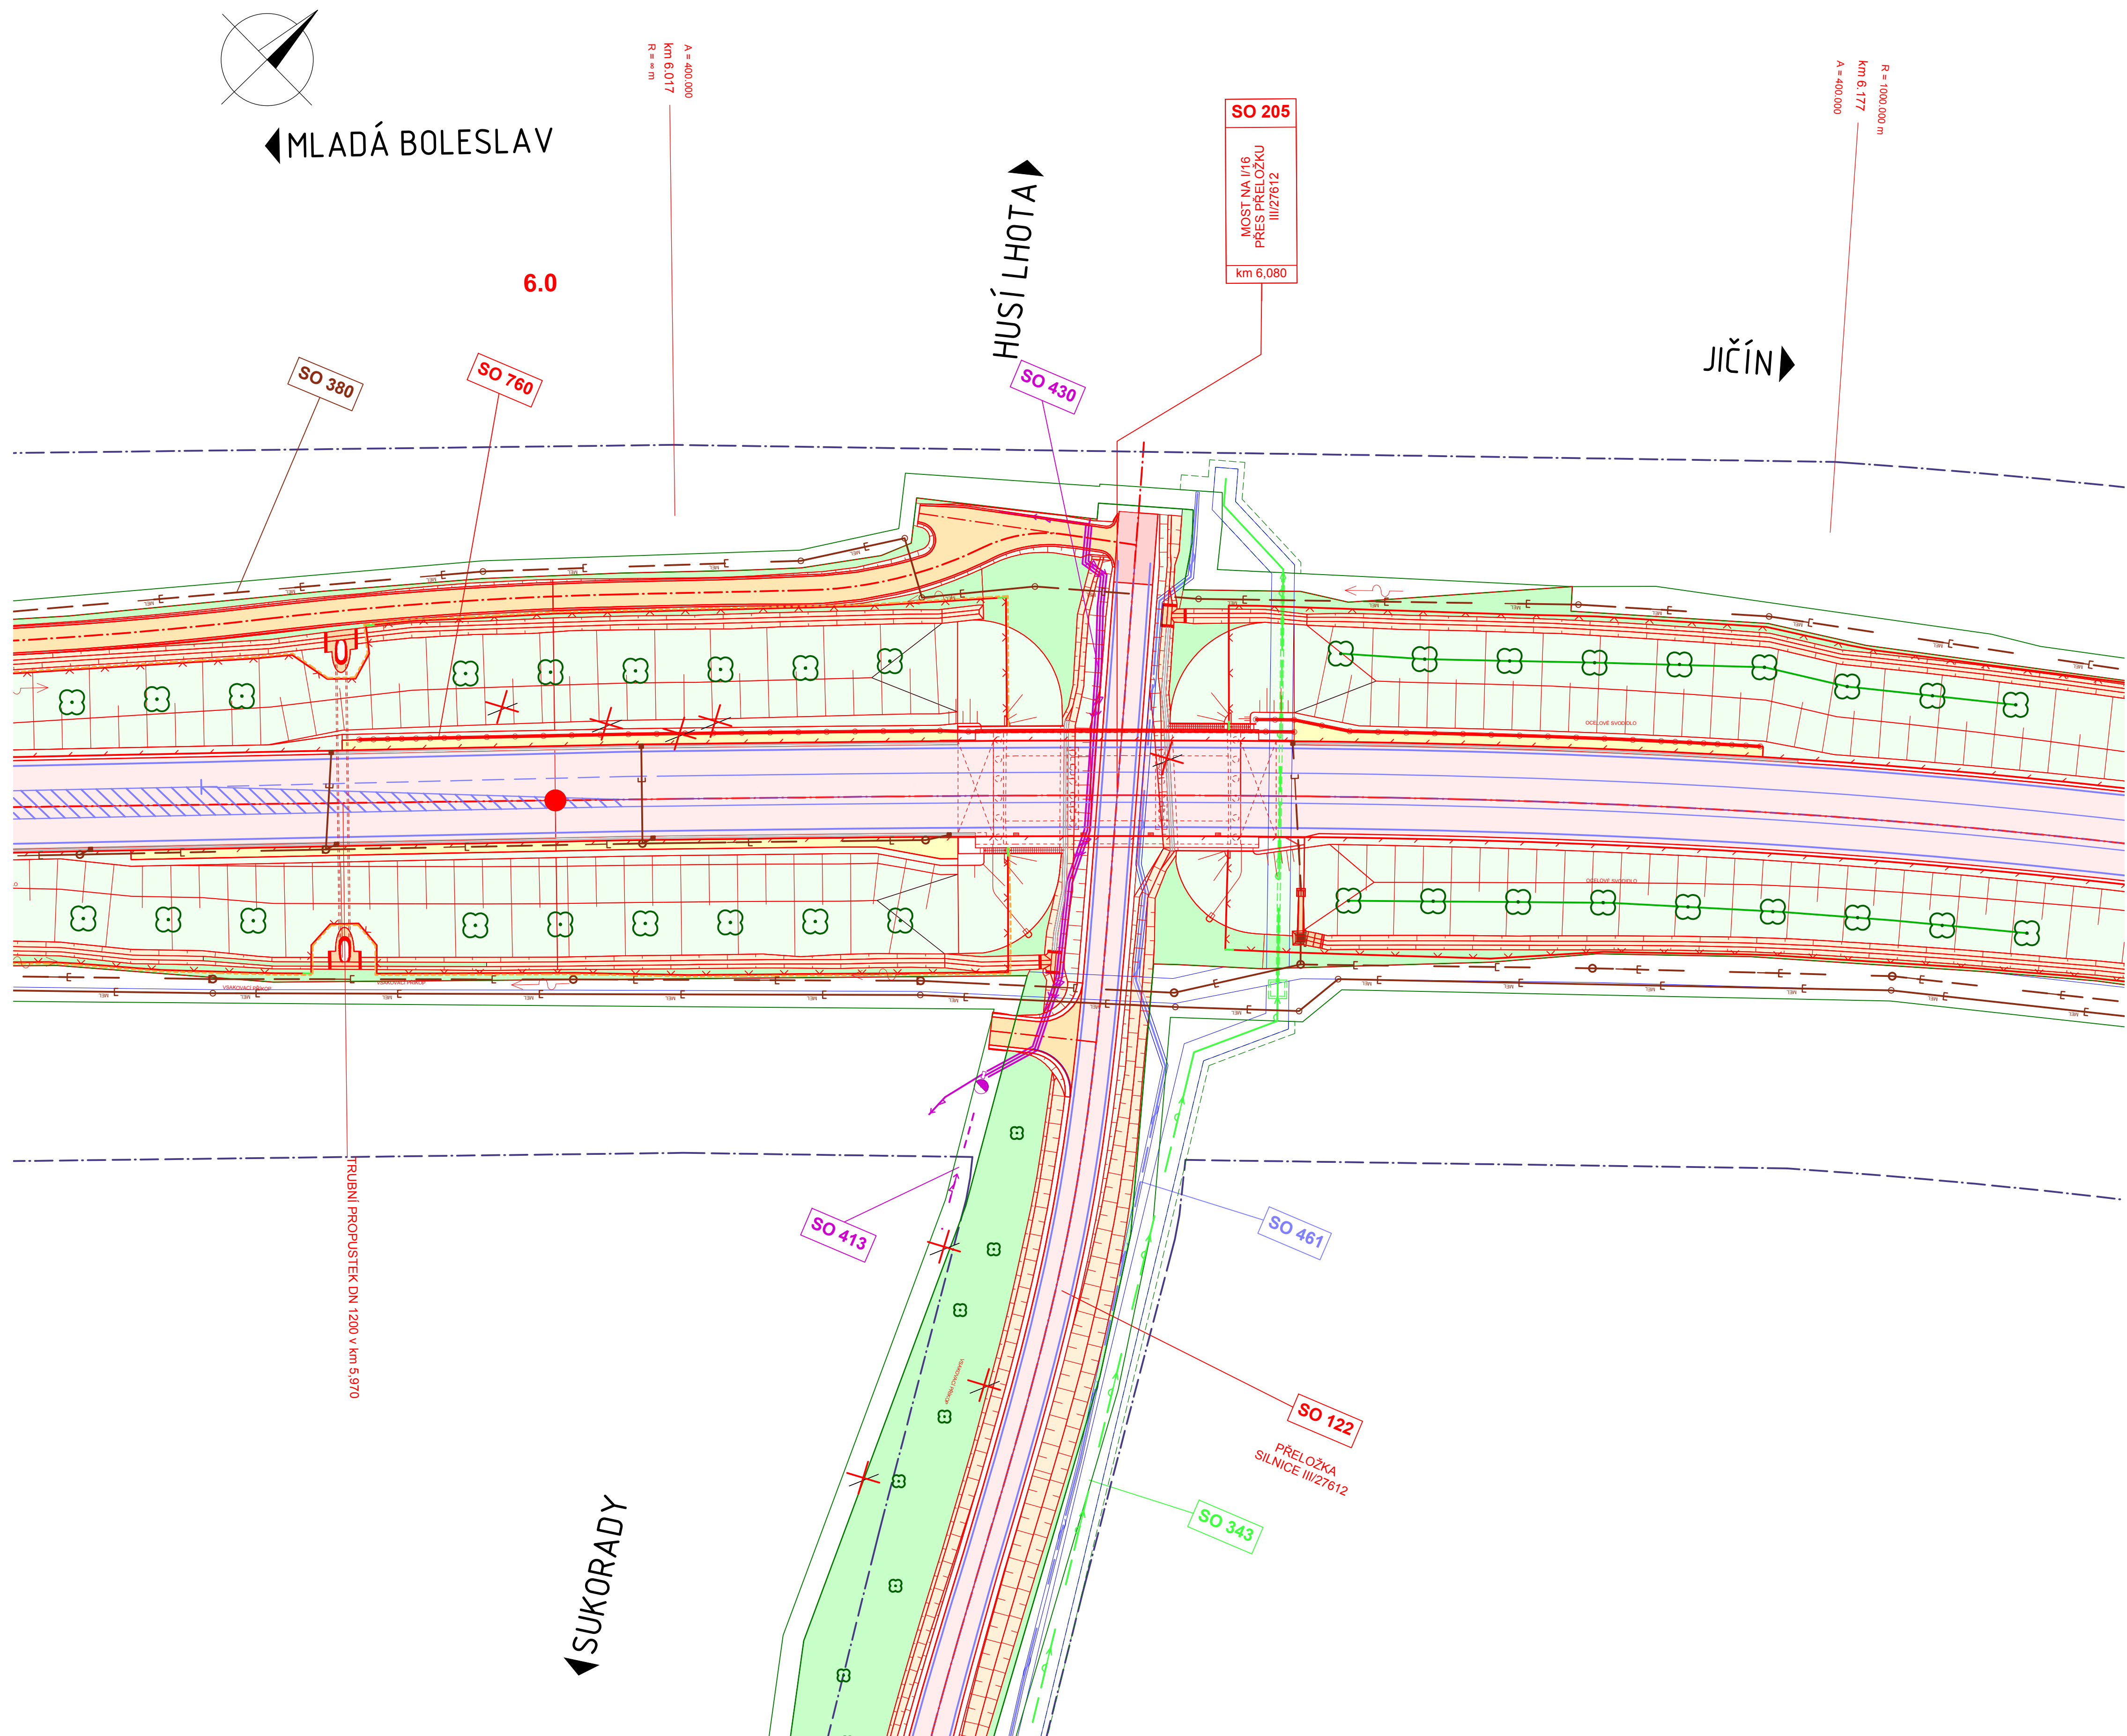

Souřadnicový systém: S-JTSK
Výškový systém: Bpv

SO 205 MOST NA I/16 PŘES PŘELOŽKU III/27612 V km 6,080

Objednatel:



Ředitelství silnic a dálnic s. p.
Čerčanská 2023/12, Krč, 140 00 Praha 4



Valbek, spol. s r.o.
Vaňurova 505/17
460 07 Liberec 3



Vypracoval	ING. I. BELDA	<i>[Signature]</i>	Zak. číslo	21-L113-001
Zodp. projektant	ING. I. BELDA	<i>[Signature]</i>	Datum	02/2025
Tech. kontrola	ING. I. BELDA	<i>[Signature]</i>	Stupeň	PDPS
Akce	I/16 MLADÁ BOLESLAV - MARTINOVICE			Počet formátů
				8 x A4
			Měřítko	1:500
			C. přílohy	Paré
Zhotovitel:	Příloha			401
Valbek, spol. s r.o. Vaňurova 505/17 460 07 Liberec 3	PŘEHLEDNÁ SITUACE			