



PŮDORYS 1:200

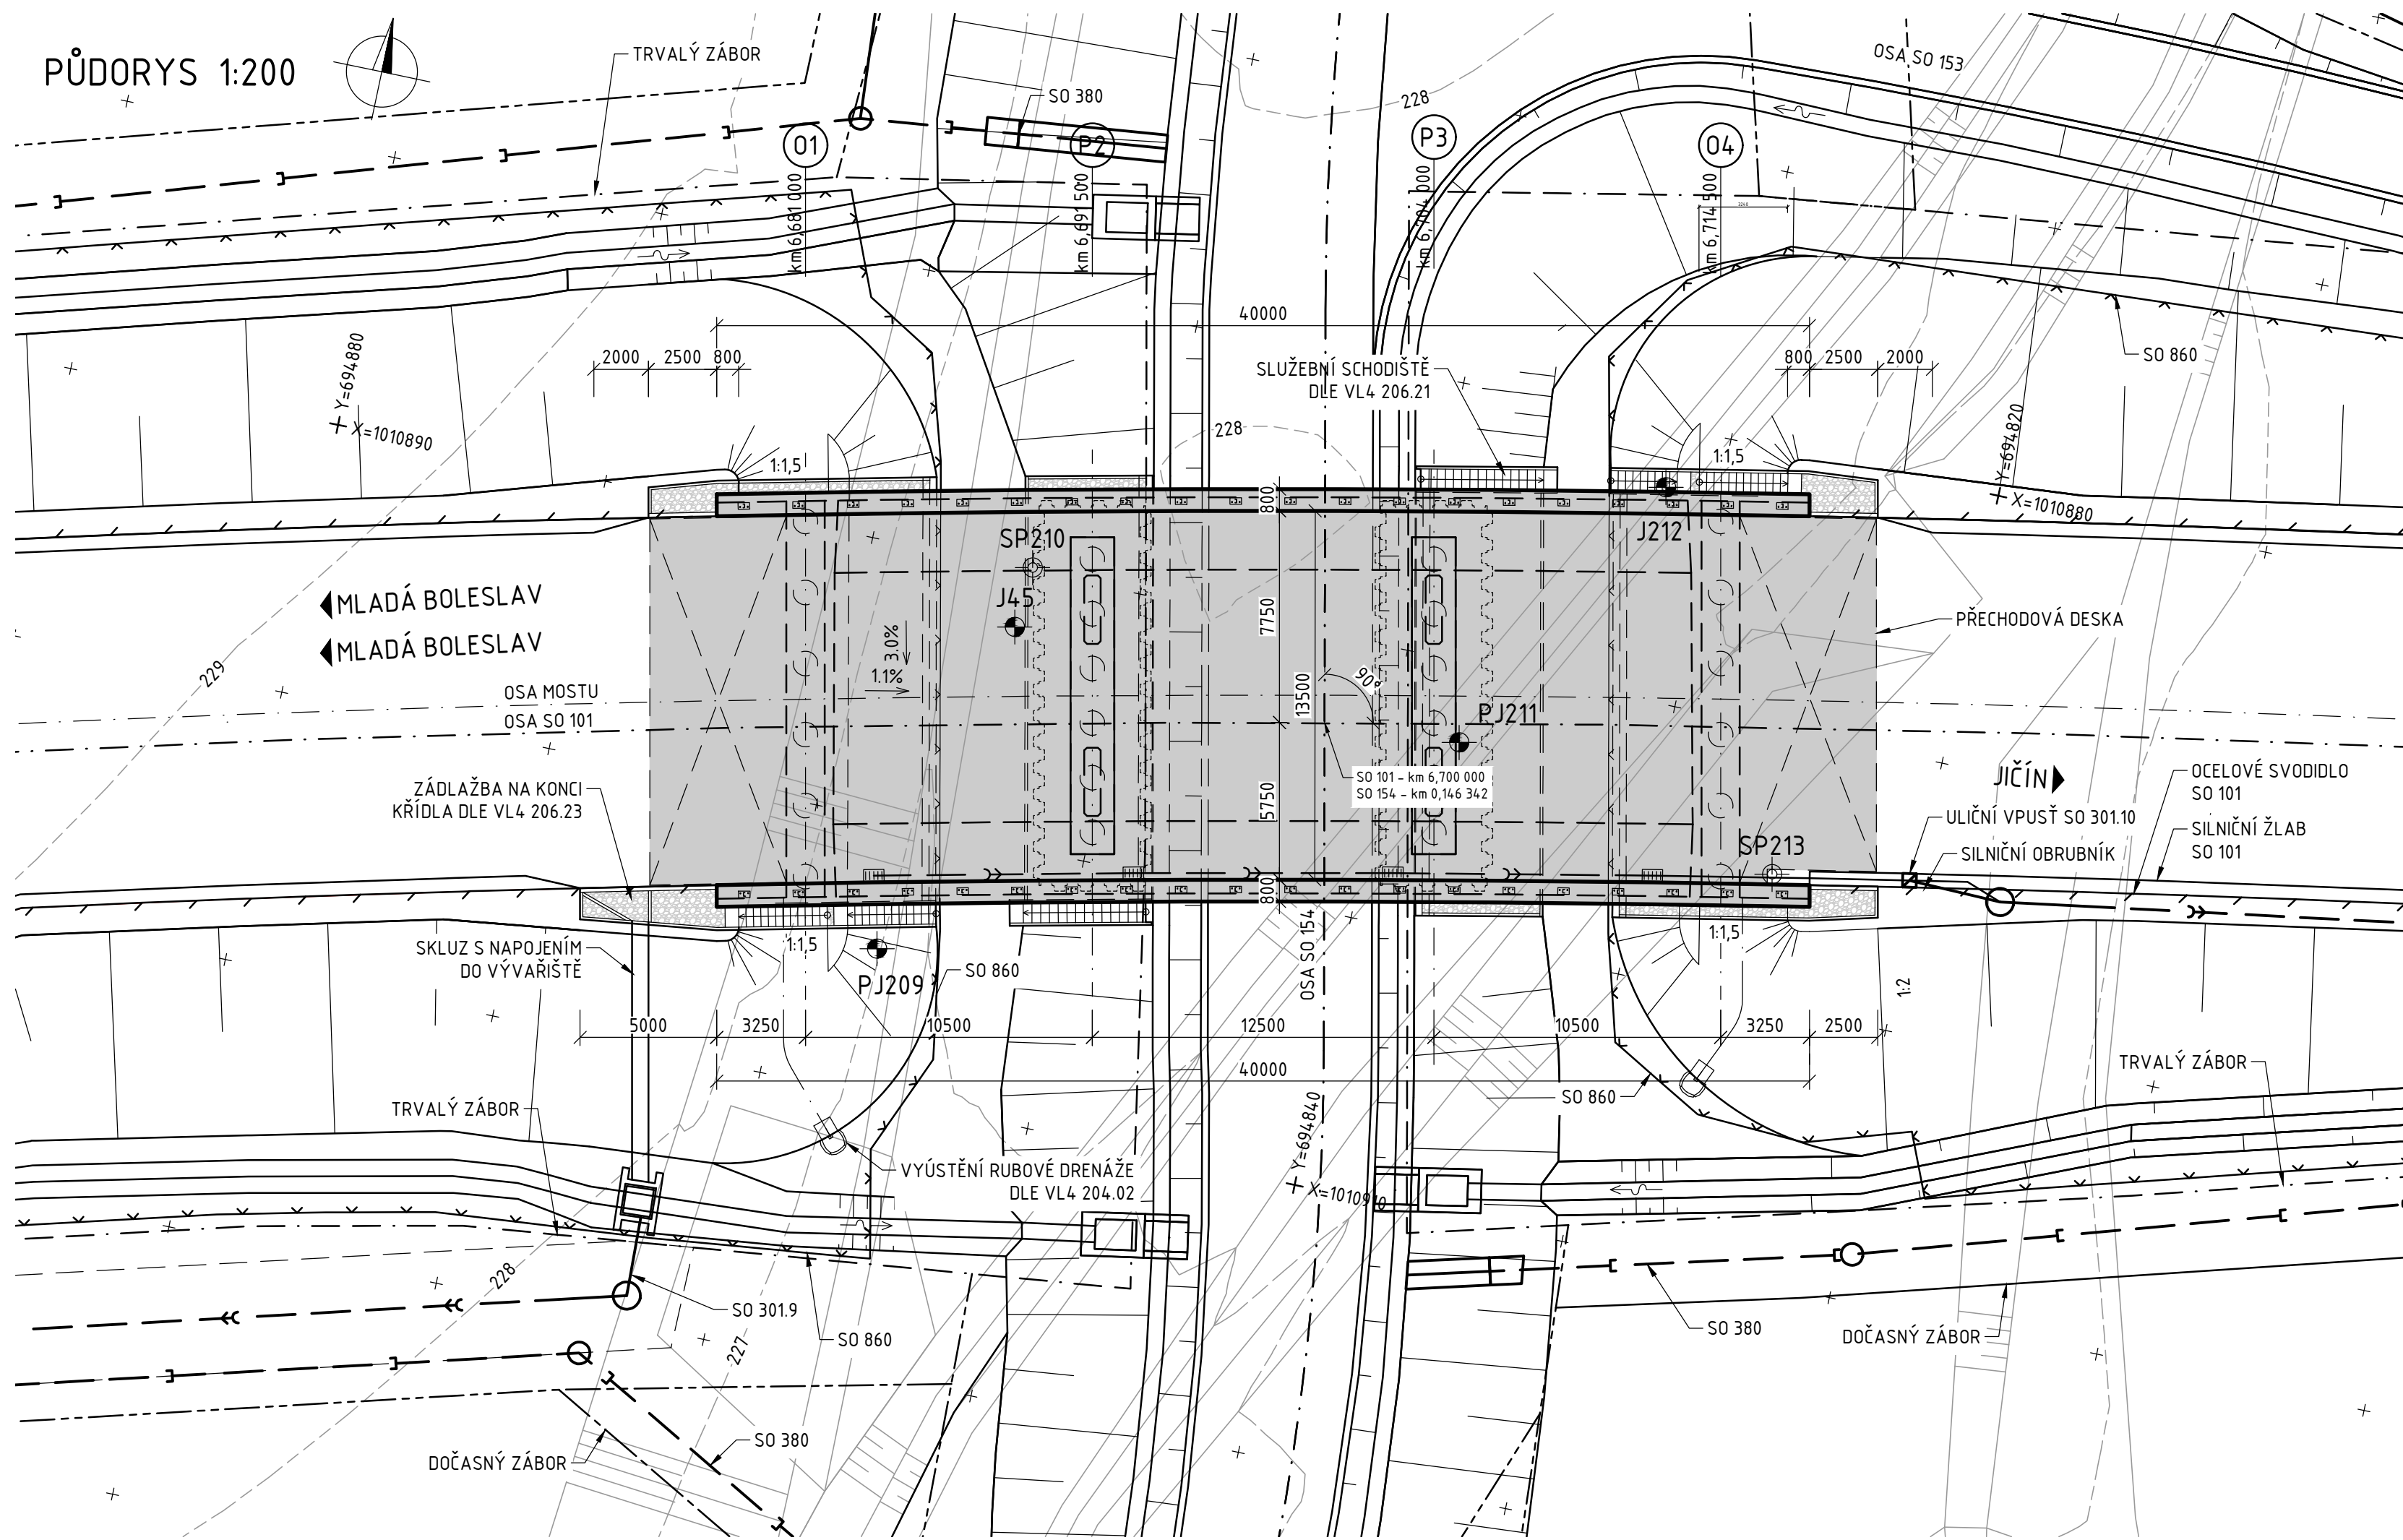


PODÉLNÝ ŘEZ 1:200

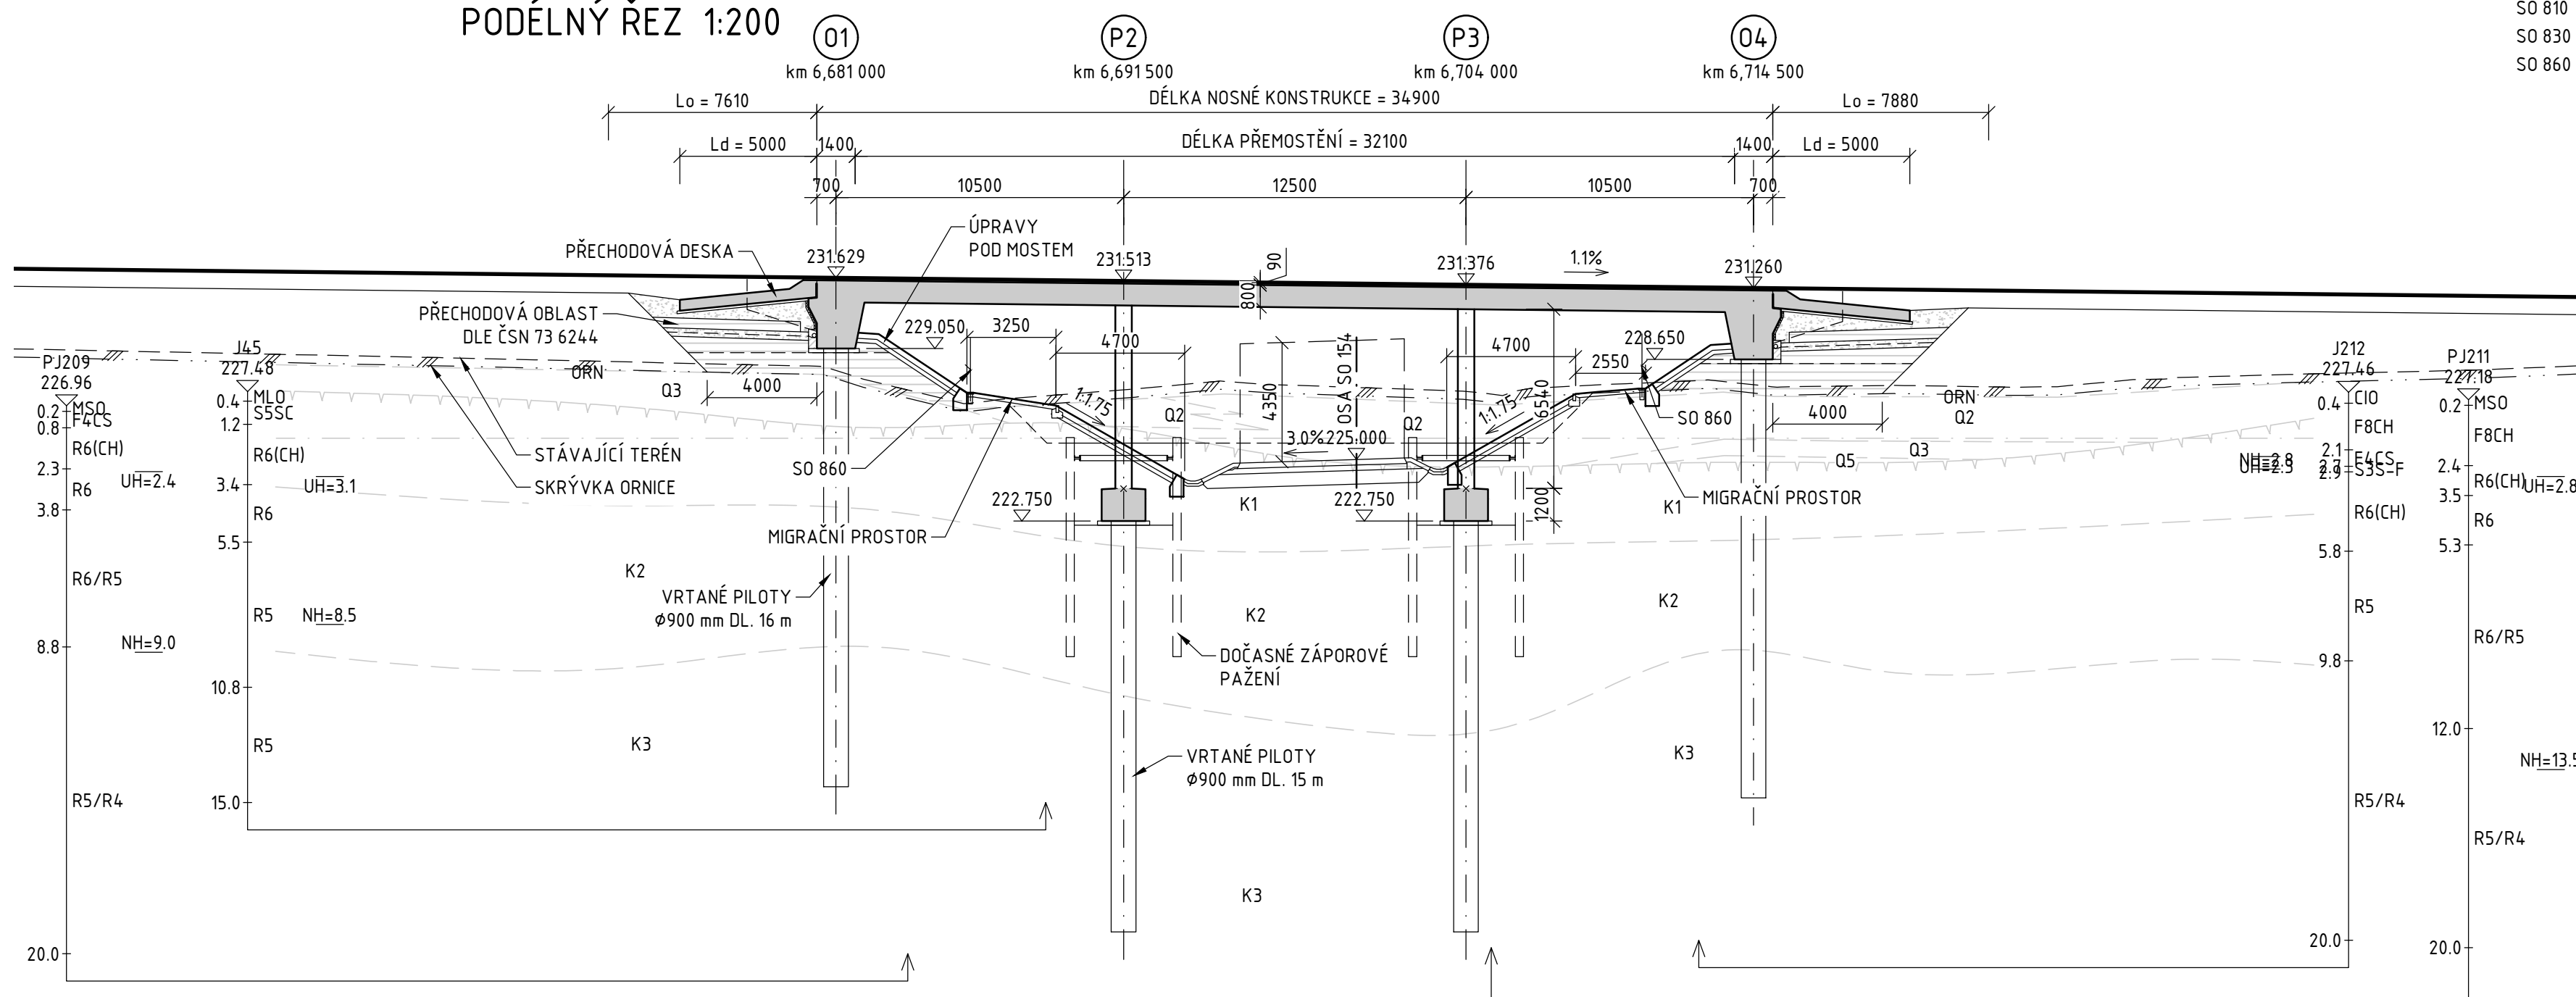


MĚŘÍTKO 0.75 0 0.75 1.5 2.25 3 3.75 4.5 5.25 6 6.75 7.5m

MĚŘÍTKO 1:200 2 0 2 4 6 8 10 12 14 16 18 20m

VZOROVÝ PŘÍČNÝ ŘEZ 1:75

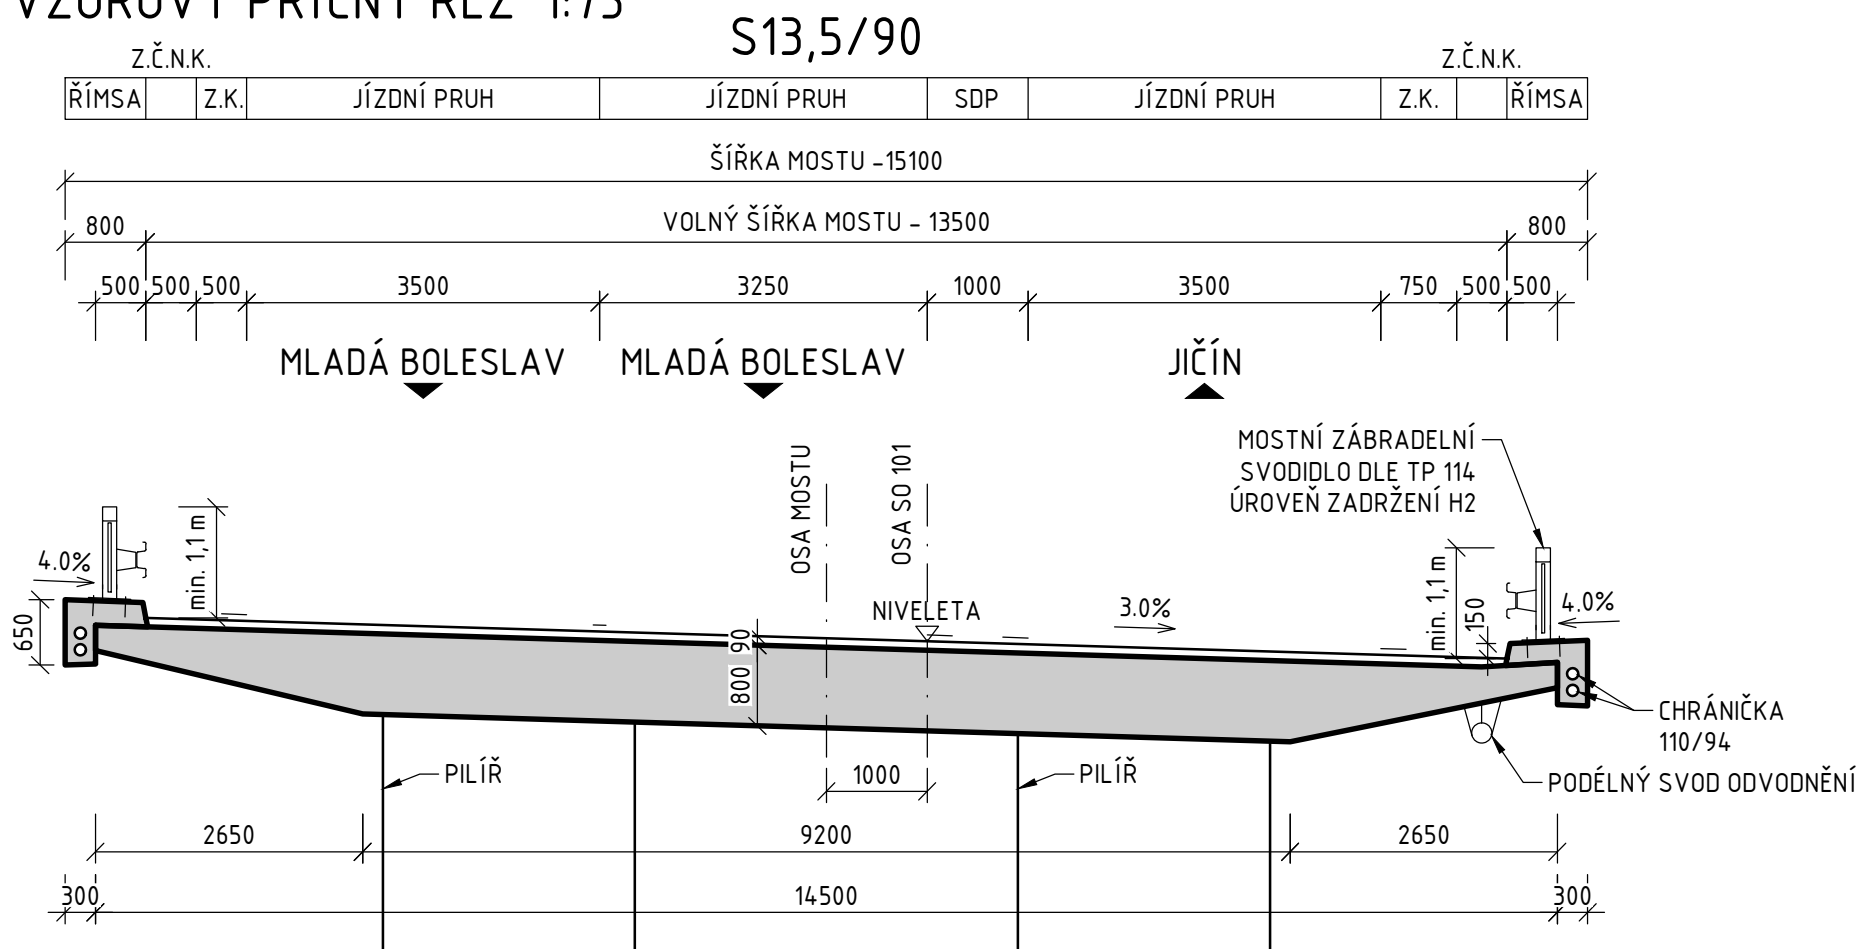

VÝŠKOVÉ VEDENÍ SO 101

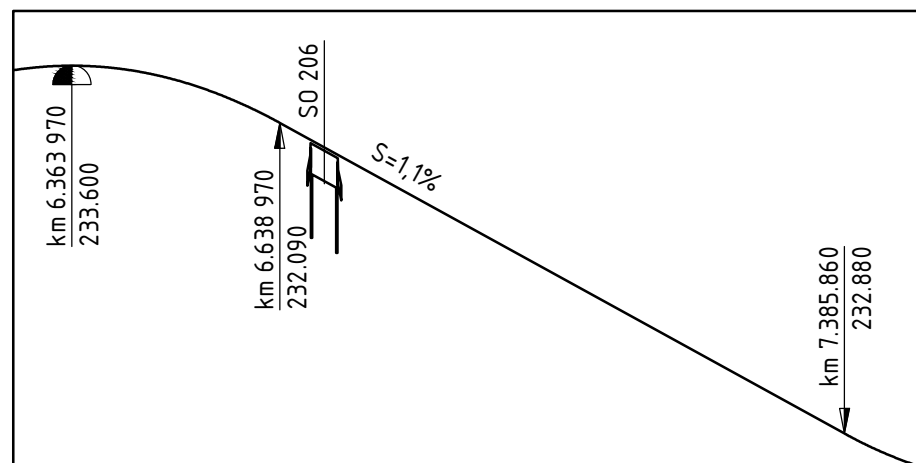

SMĚROVÉ VEDENÍ SO 101

STANIČNÍ	X	Y	PARAMETR
km 6.177 346	695 303.843	1011 125.796	R = 1000 m
km 6.821 454	694 722.312	1010 875.696	

SOUVISEJÍCÍ OBJEKTY:

- SO 020 PŘÍPRAVA ÚZEMÍ
- SO 101 SILNICE I/16 MLADÁ BOLES LAV - MARTINOVICE
- SO 153 PŘÍSTUPY NA POZEMKY K.Ú. SUKORADY U MLADÉ BOLES LAVI
- SO 154 PŘELOŽKA POLNÍ CESTY V KM 6,700
- SO 190 DOPRAVNÍ ZNAČENÍ
- SO 301.x ODVODNĚNÍ I/16
- SO 380 ÚPRAVY MELIORACÍ ZÚ - KÚ
- SO 801 VEGETAČNÍ ÚPRAVY
- SO 810 KÁČENÍ ZELENĚ
- SO 830 REKULTIVACE PLOCH DOČASNÉHO ZÁBORU
- SO 860 OPLOČENÍ

LEGENDA

- TRVALÝ ZÁBOR
- DOČASNÝ ZÁBOR nad 1 rok
- DOČASNÝ ZÁBOR do 1 roku

Souřadnicový systém: S-JTSK
Výškový systém: Bpv

SO 206 MOST NA I/16 PŘES PŘELOŽKU POLNÍ CESTY V KM 6,700

Objednatel:



Ředitelství silnic a dálnic s. p.
Čerčanská 2023/12, Krč, 140 00 Praha 4



Valbek, spol. s r.o.
Vaňurova 505/17
460 07 Liberec 3



Vypracoval: ING. I. BELDA Zak. číslo: 21-L113-001 Z odp. projektant: ING. I. BELDA Datum: 02/2025 Tech. kontrola: ING. I. BELDA Stupeň: PDPS Akce: I/16 MLADÁ BOLES LAV - MARTINOVICE Počet formátů: 8x A4 Měřítko: 1:200,75 Č. přílohy: Paré Zhotovitel: Valbek, spol. s r.o. Vaňurova 505/17 460 07 Liberec 3 Příloha: PŮDORYS, PODÉLNÝ ŘEZ, VZOROVÝ PŘÍČNÝ ŘEZ 102
