

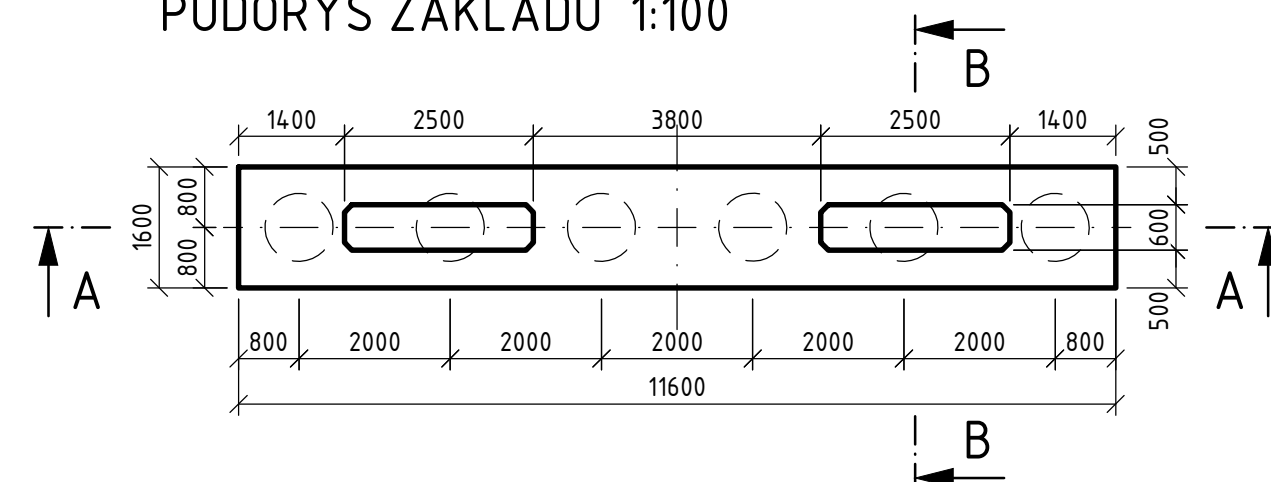
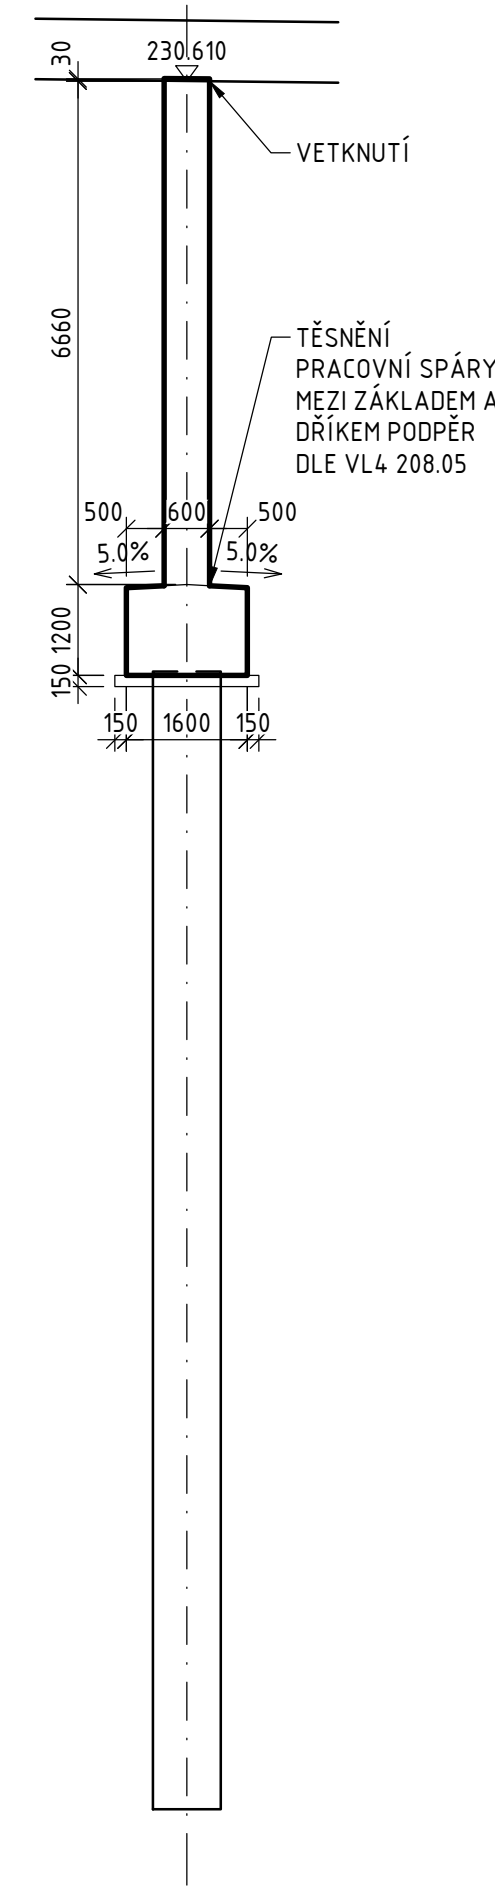
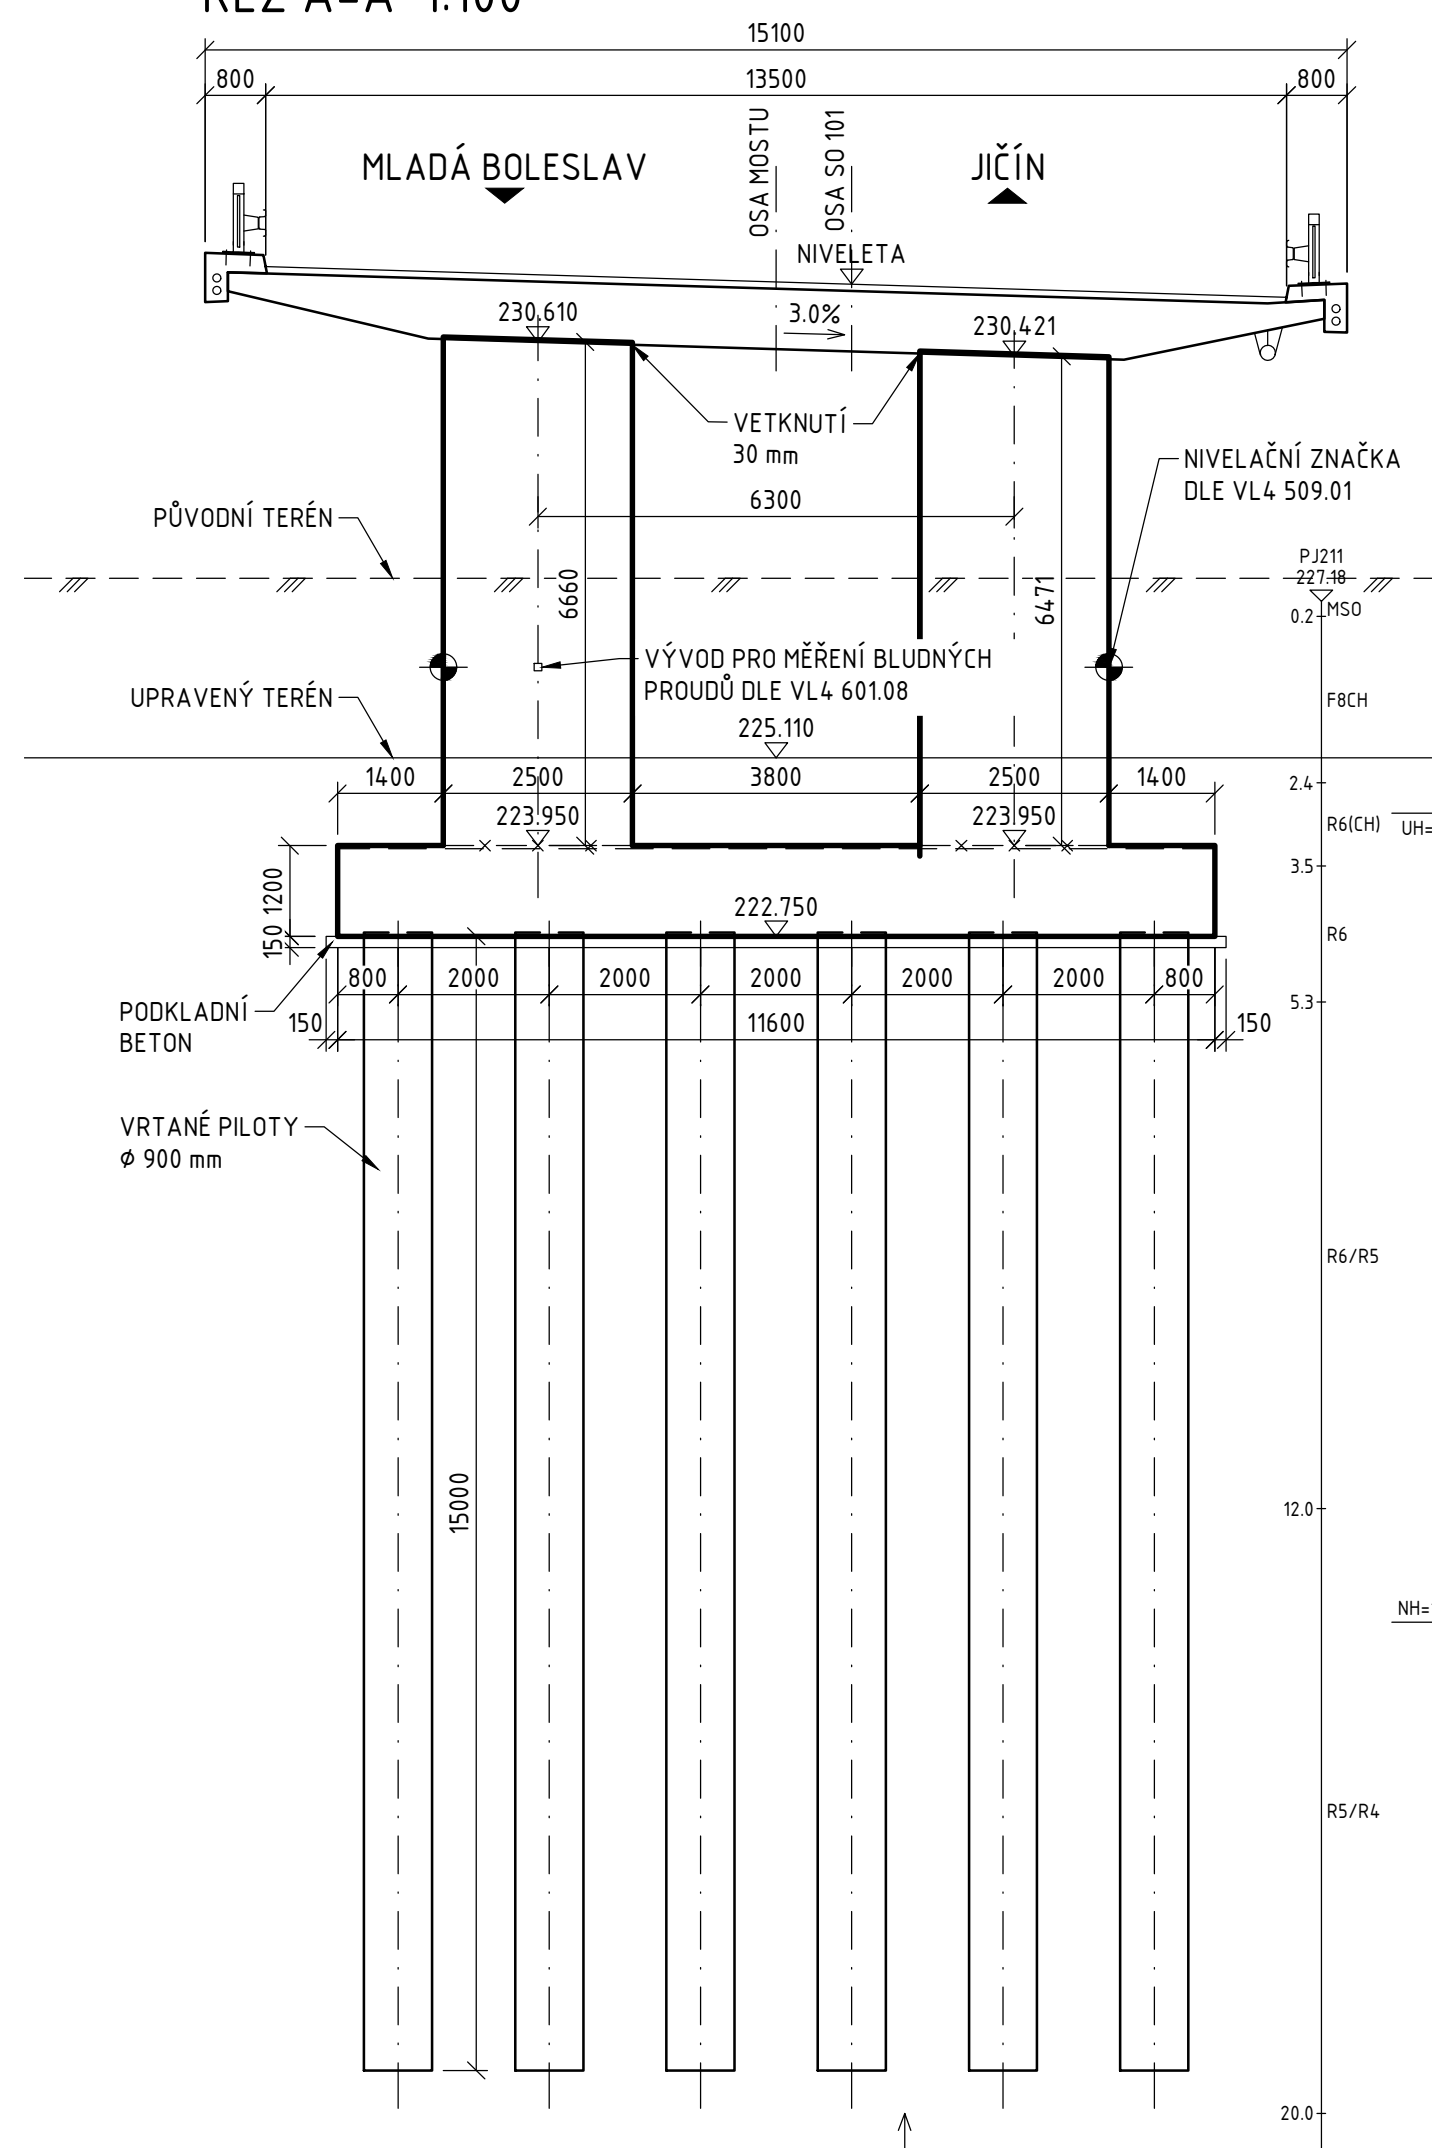
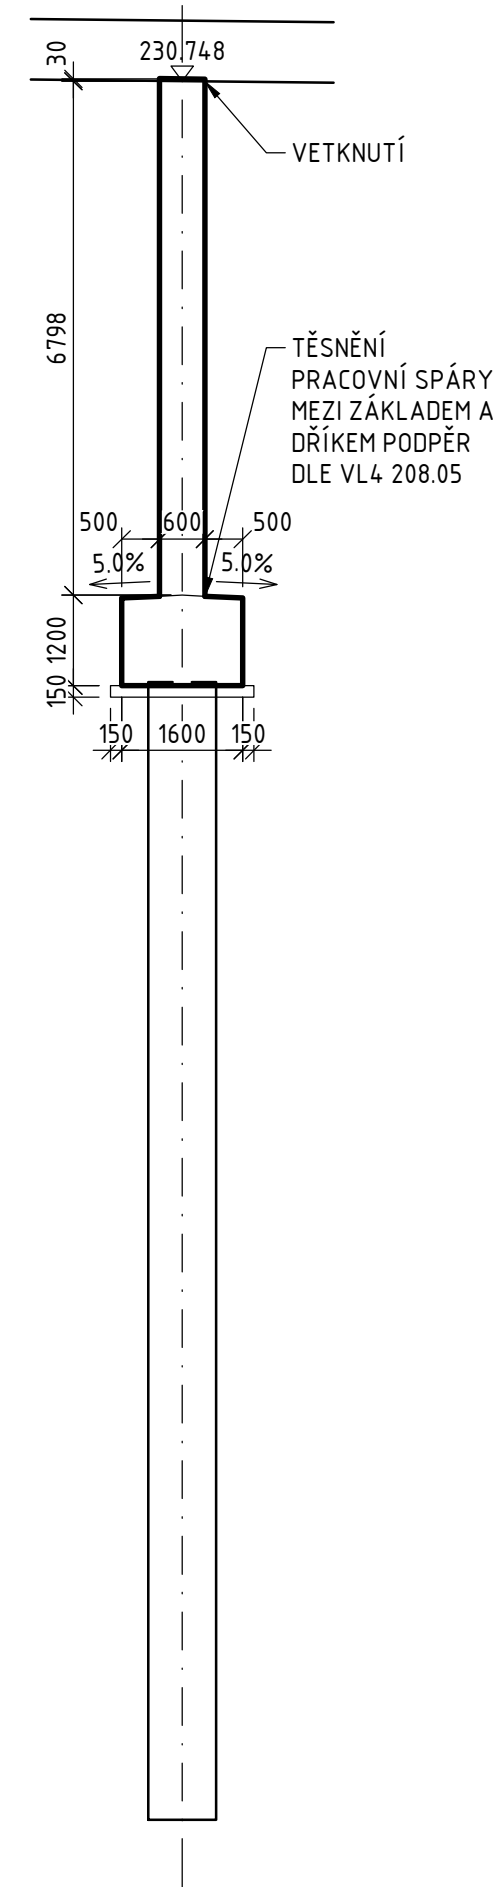
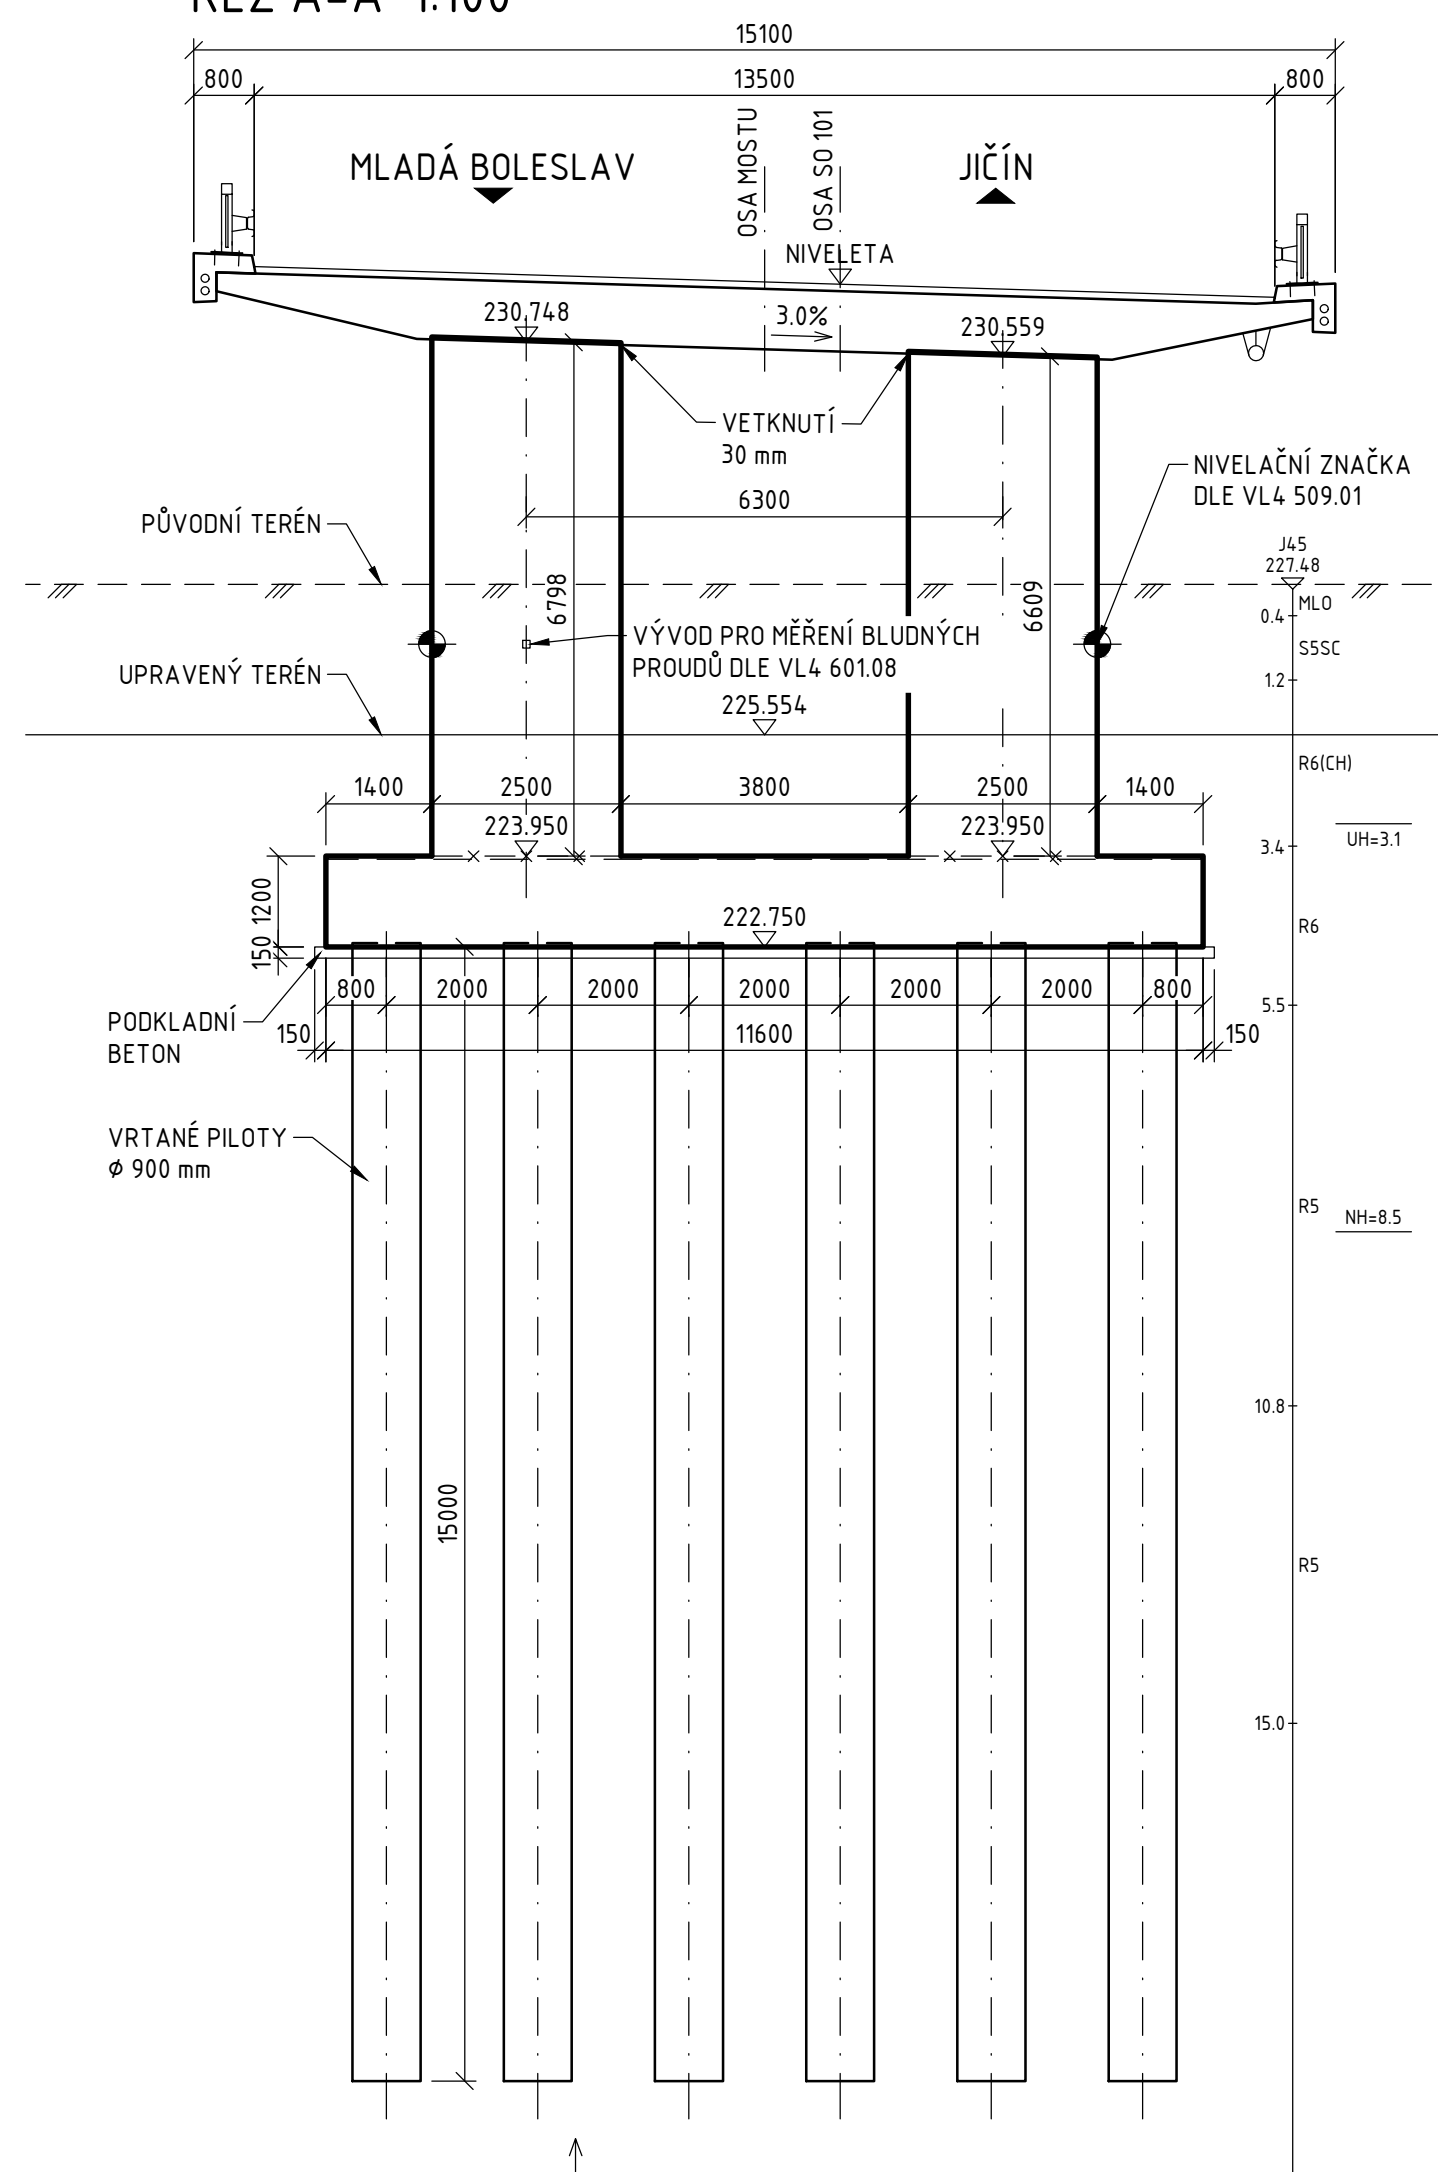


- VYTYČOVACÍ ODCHYLKY: VIZ PŘÍLOHA E.4.5.1- GVS - SEZNAM SOUŘADNIC
- NEDÍLNOU SOUČÁSTÍ VÝKRESU JSOU POZNÁMKY A SPECIFIKACE UVEDENÉ NA VÝKRESE POZNÁMEK
A TECHNICKÝCH SPECIFIKACÍ

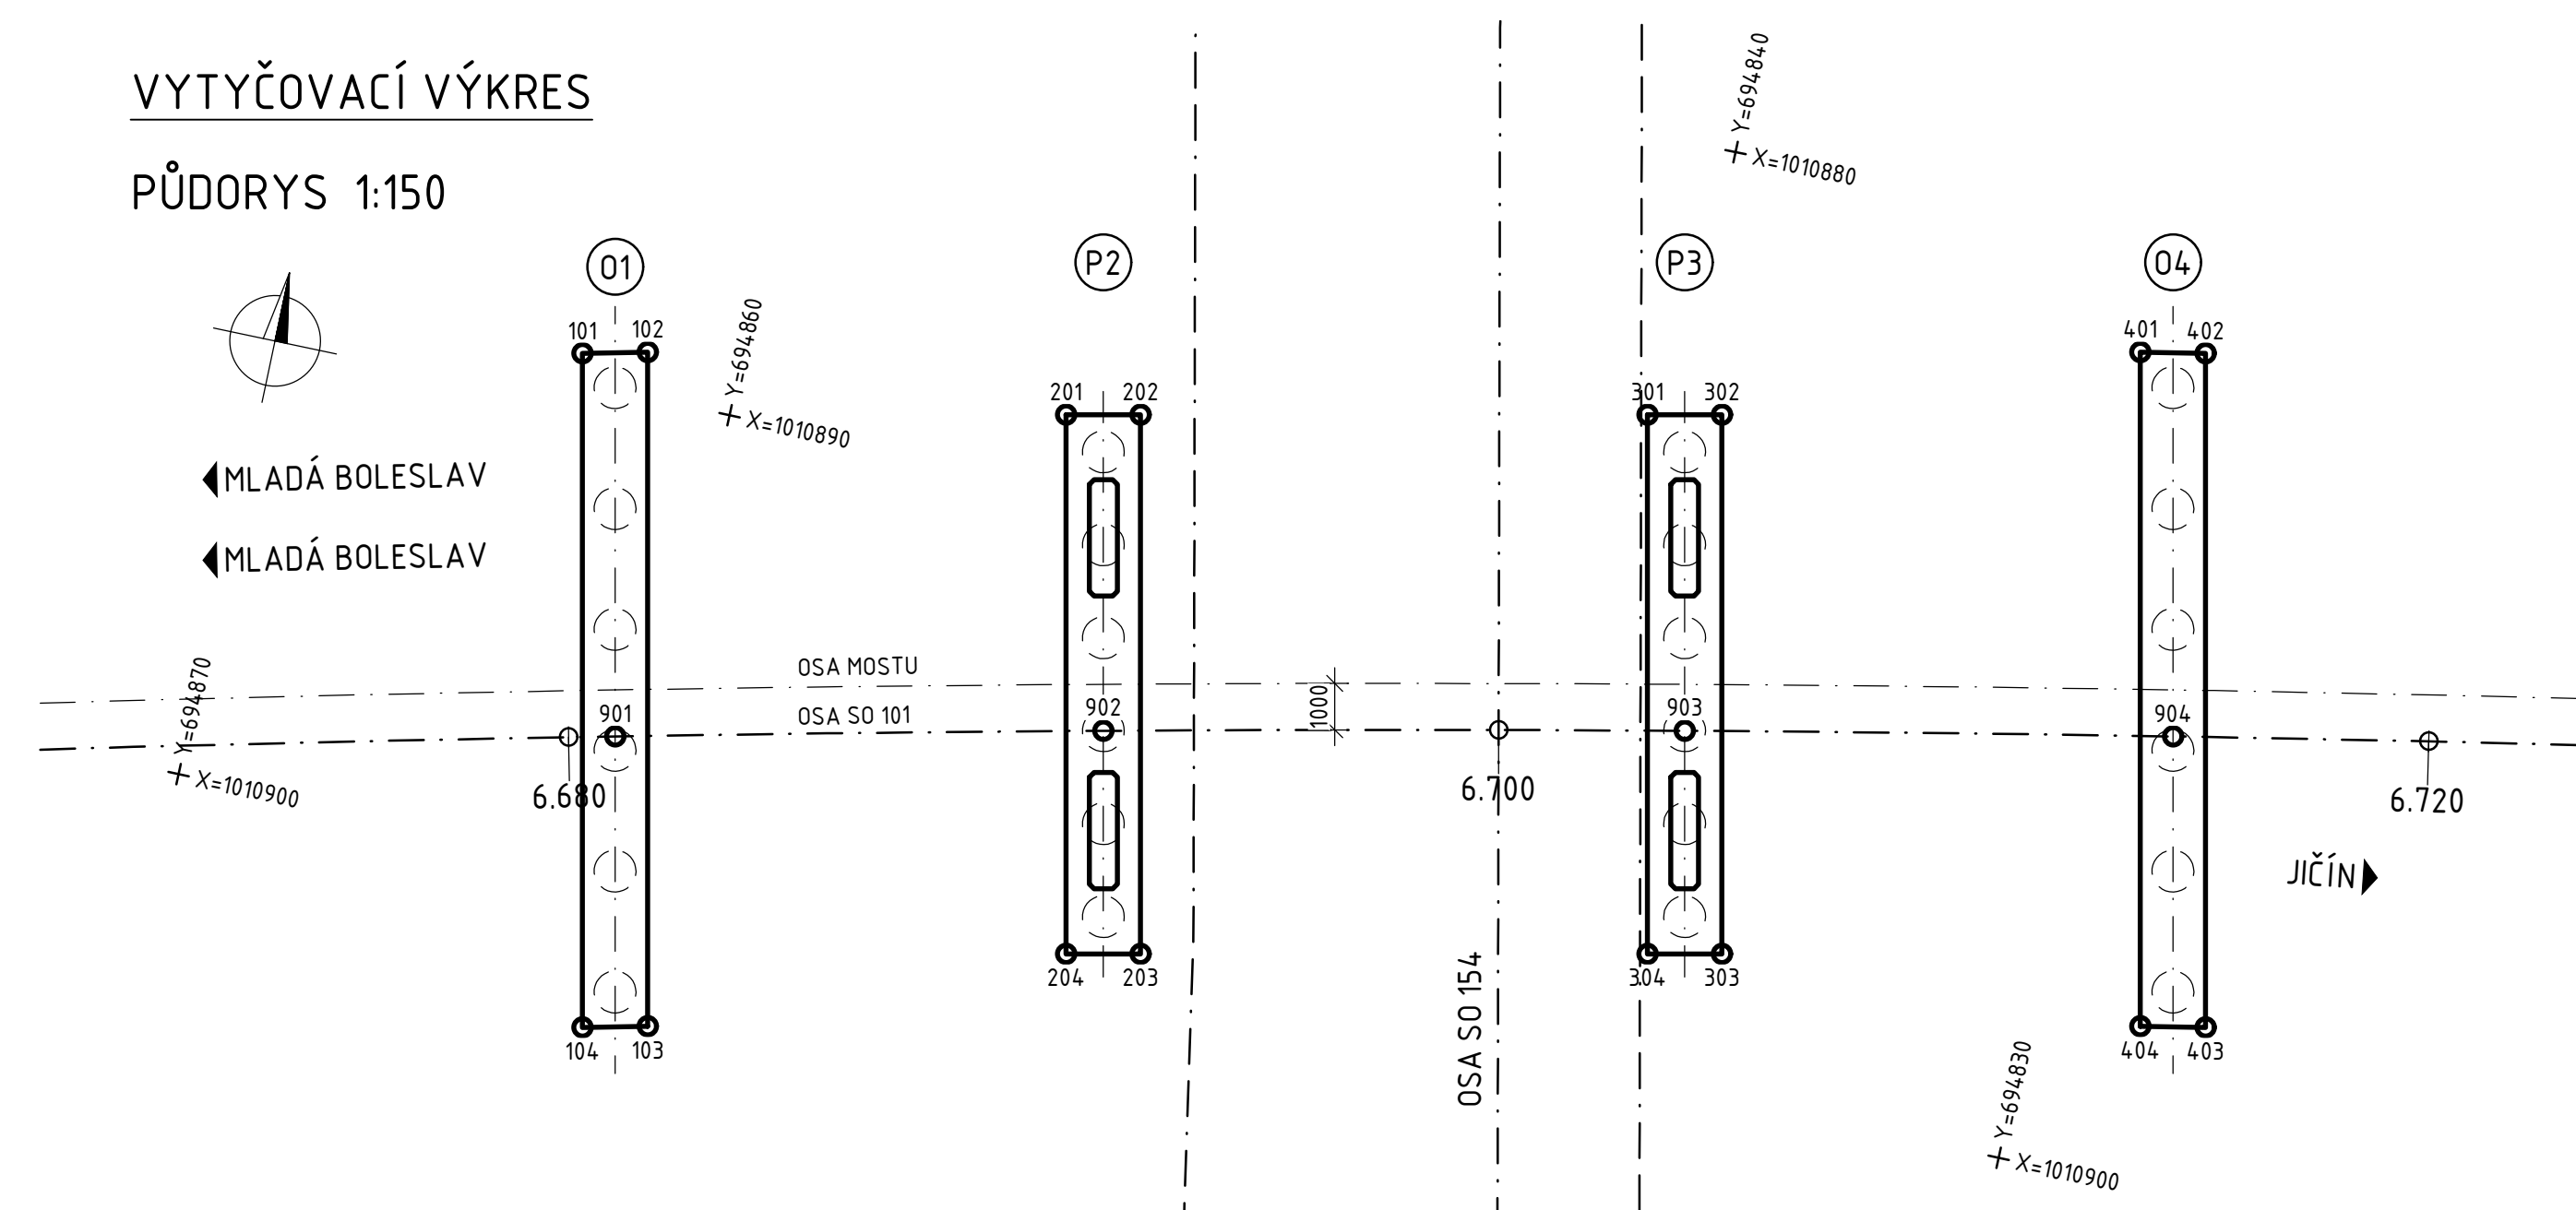

TRVALÝ ZÁBOR — — . — — . — — .
MOST LEŽÍ UVNITŘ TRVALÉHO I DOČASNÉHO ZÁBORU

B0D	γ [m]	X [m]	Z [m]
101	696.863.368	1010.889.351	229.050
102	696.862.003	1010.889.039	229.050
103	696.859.011	1010.903.229	229.050
104	696.860.376	1010.903.541	229.050
201	696.852.920	1010.888.495	222.750
202	696.851.355	1010.888.165	222.750
203	696.848.961	1010.889.516	222.750
204	696.850.527	1010.899.846	222.750
301	696.840.689	1010.885.916	222.750
302	696.839.124	1010.885.586	222.750
303	696.836.730	1010.896.937	222.750
304	696.838.296	1010.897.267	222.750
401	696.830.595	1010.882.147	228.650
402	696.829.220	1010.882.151	228.650
403	696.826.228	1010.896.341	228.650
404	696.827.603	1010.896.607	228.650
901	696.860.983	1010.897.269	-
902	696.850.734	1010.894.984	-
903	696.838.050	1010.892.405	-
904	696.828.205	1010.890.357	-

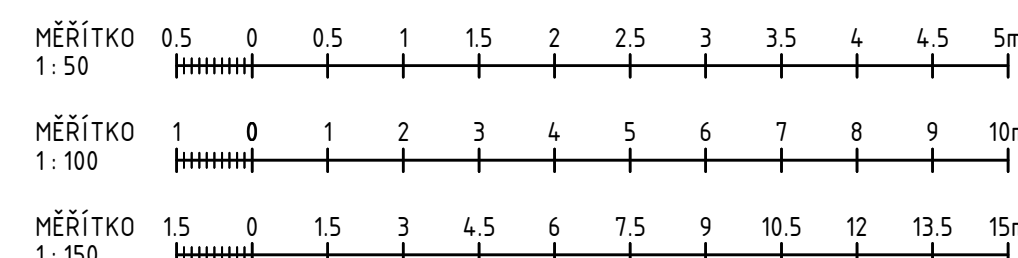

Souřadnicový systém: S-JTSK
Výškový systém: Bpv

SO 206 MOST NA I/16 PŘES PŘELOŽKU POLNÍ CESTY V KM 6,700

ŘEDITELSTVÍ
SILNIC
A DÁLNIC

Ředitelství silnic a dálnic s. p.
Čerčanská 2023/12, Krč, 140 00 Praha 4



Valbek, spol. s r.o.
Vaňurova 505/17
460 07 Liberec 3



Vypracoval	L. MARTÍNEK	<i>Martínek</i>
Zodp. projektant	ING. I. BELDA	<i>Belda</i>
Tech. kontrola	ING. I. BELDA	<i>Belda</i>
Akce		
I/16 MLADÁ BOLESLAV - MARTINOVICE		

Zhotovitel:
Valbek, spol. s r.
Vaňurova 505/1
460 07 Liberec 3

Příloha	PŘÍČNÉ ŘEZY, TVAR ZÁKLADŮ, SPODNÍ STAVBA, VYTYČENÍ
---------	---

201