

TVAR NOSNÉ KONSTRUKCE


PŮDORYS 1:150

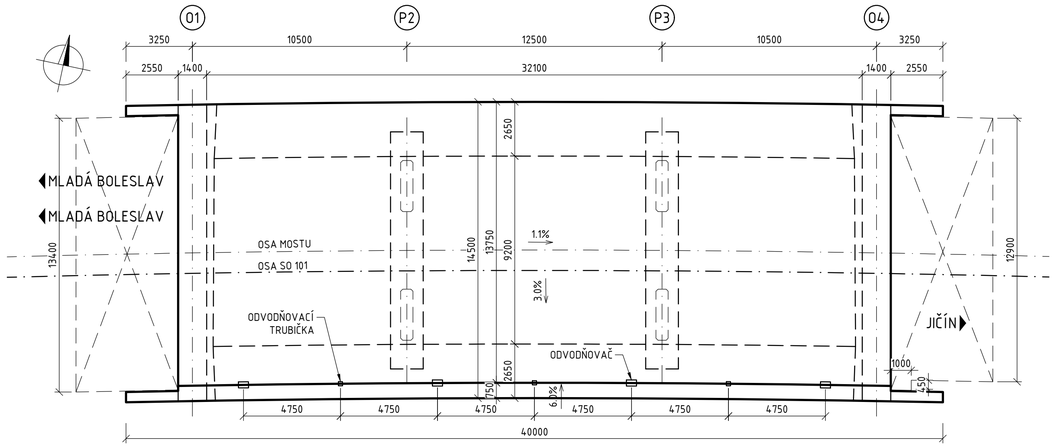


POHLED NA KŘÍDLO 01 VPRAVO 1:75

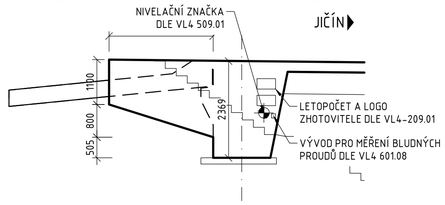


POHLED NA KŘÍDLO 01 VLEVO 1:75

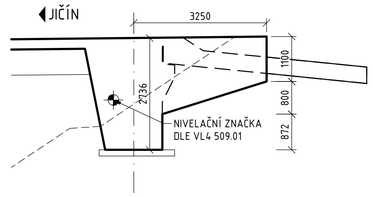


ŘEZ KŘÍDLEM 1:75

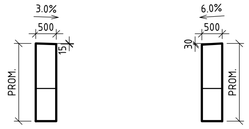

POHLED NA KŘÍDLO 04 VLEVO 1:75

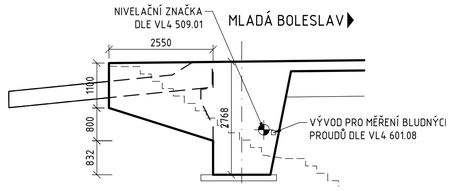


POHLED NA KŘÍDLO 04 VPRAVO 1:75

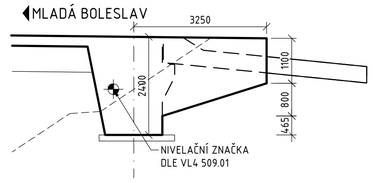


PODÉLNÝ ŘEZ PŘECHODOVOU DESKOU 1:50

VYKRESLENA PŘECHODOVÁ DESKA OPĚRY 01, PŘECHODOVÁ DESKA OPĚRY 04 ŘEŠENA OBDOBNĚ

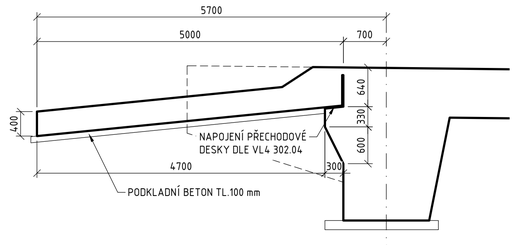


PODÉLNÝ ŘEZ 1:150

OSOU SO 101

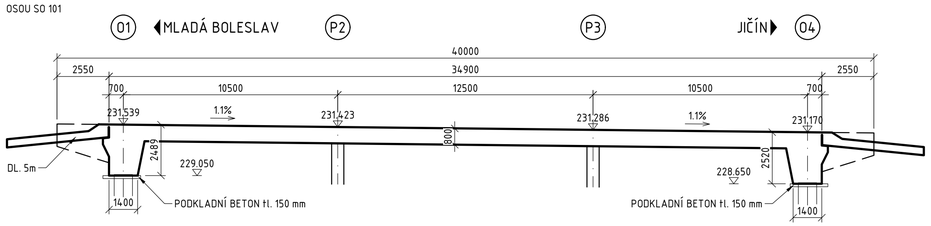

PŘÍČNÝ ŘEZ 1:75

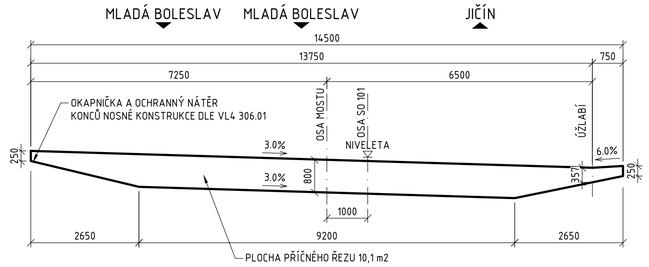


POZNÁMKY:

- NEDÍLNOU SOUČÁSTÍ VÝKRESU JSOU POZNÁMKY A SPECIFIKACE UVEDENÉ NA VÝKRESE POZNÁMEK A TECHNICKÝCH SPECIFIKACÍ

PŘECHODOVÉ OBLASTI


PODÉLNÝ ŘEZ 01 1:75

OSOU SO 101

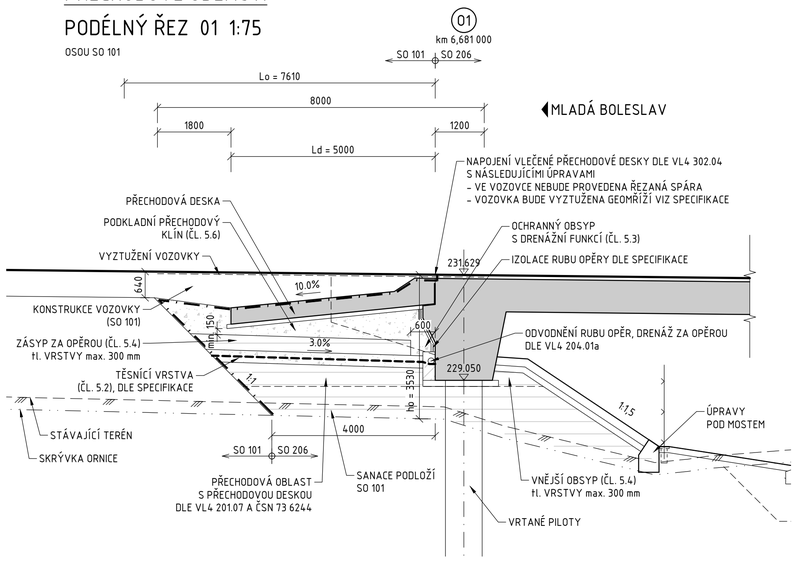

PODÉLNÝ ŘEZ 04 1:75

OSOU SO 101

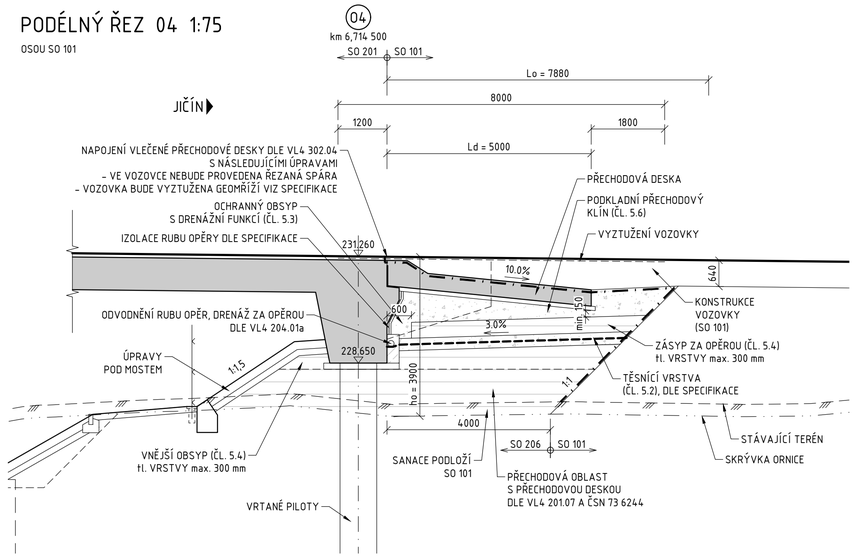

MĚŘÍTKO 1 : 50 — 0.5 0 0.5 1 1.5 2 2.5 3 3.5 4 4.5 5m

MĚŘÍTKO 1 : 75 — 0.75 0 0.75 1.5 2.25 3 3.75 4.5 5.25 6 6.75 7.5m

MĚŘÍTKO 1 : 150 — 1.5 0 1.5 3 4.5 6 7.5 9 10.5 12 13.5 15m

Souřadnicový systém: S-JTSK
Výškový systém: Bpv

SO 206 MOST NA I/16 PŘES PŘELOŽKU POLNÍ CESTY V KM 6,700

Objednatel:
ŘEDITELSTVÍ SILNIC A DÁLNIC
Ředitelství silnic a dálnic s. p.
Čerčanská 2023/12, Krč, 140 00 Praha 4

Valbek
Valbek, spol. s r.o.
Vaňurova 505/17
460 07 Liberec 3

Vypracoval	L. MARTÍNEK		Zak. číslo	21-LI13-001
Zodp. projektant	ING. I. BELDA		Datum	02/2025
Tech. kontrola	ING. I. BELDA		Stupeň	PDPS
Akce: I/16 MLADÁ BOLESLAV - MARTINOVICE			Počet formátů	8x A4
			Měřítko	1:150,75
			Č. přílohy	Paré
Zhotovitel: Valbek, spol. s r.o. Vaňurova 505/17 460 07 Liberec 3	Příloha: TVAR NOSNÉ KONSTRUKCE, PŘECHODOVÉ OBLASTI		202	