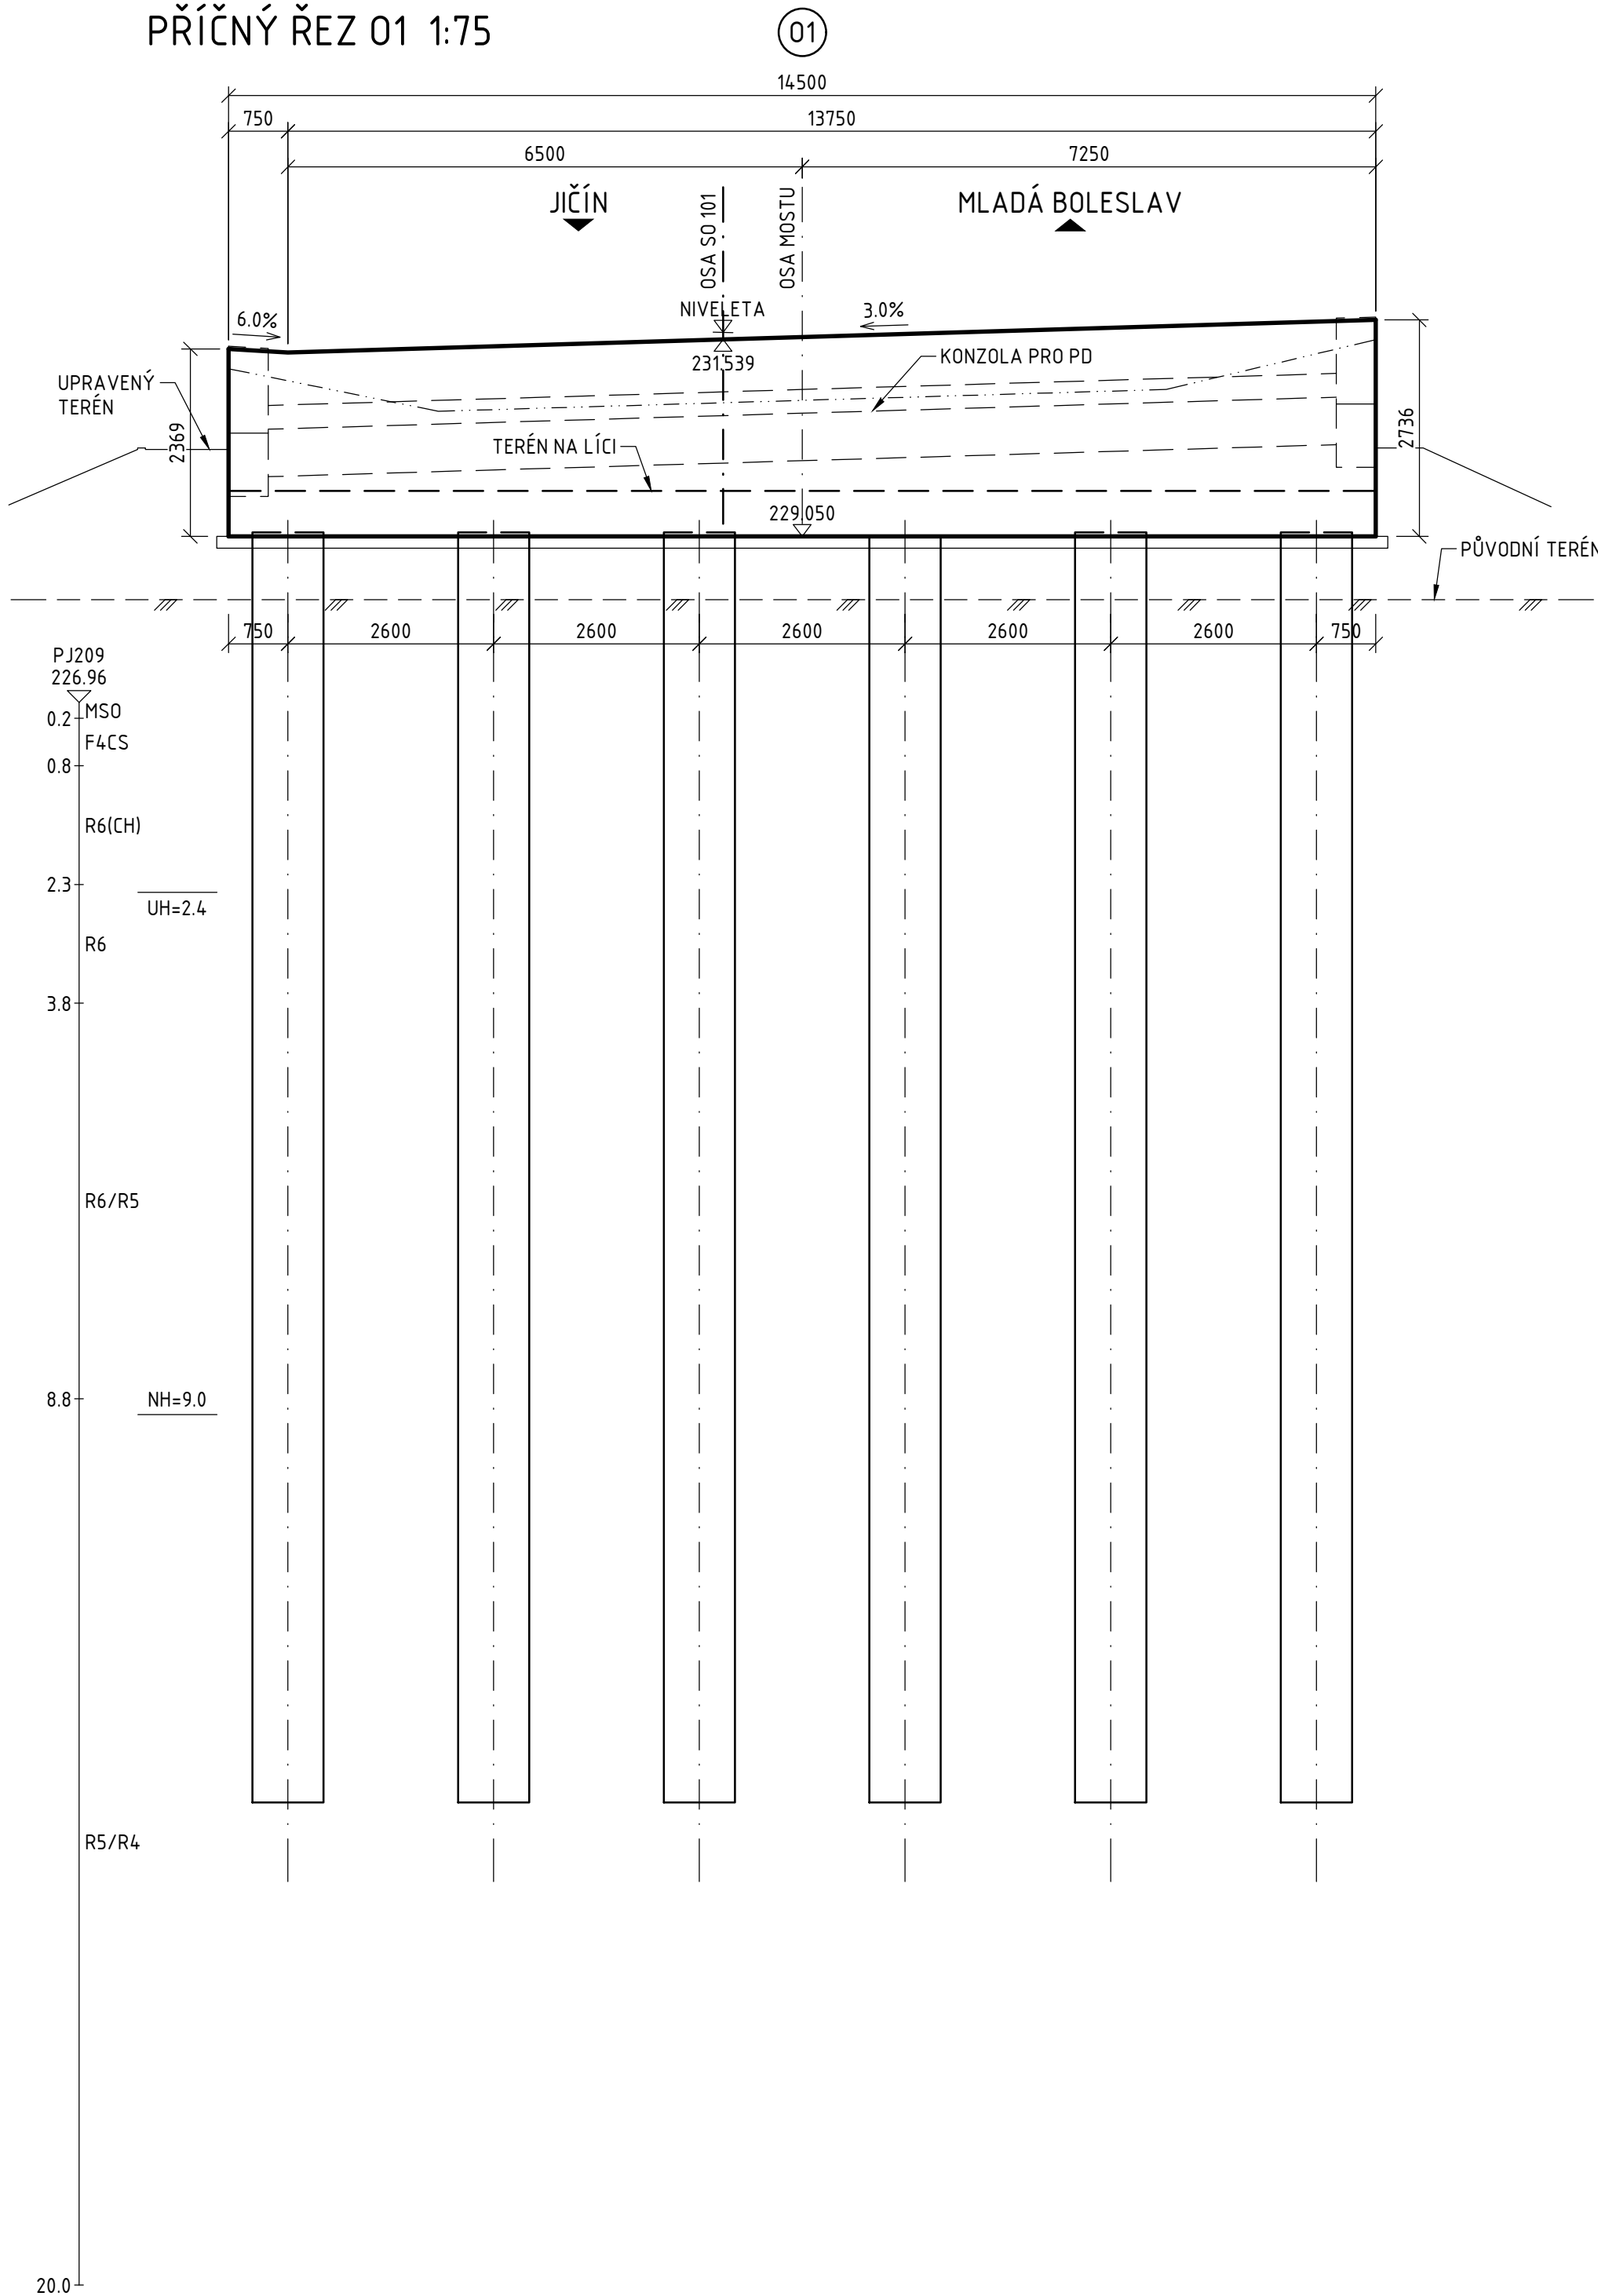
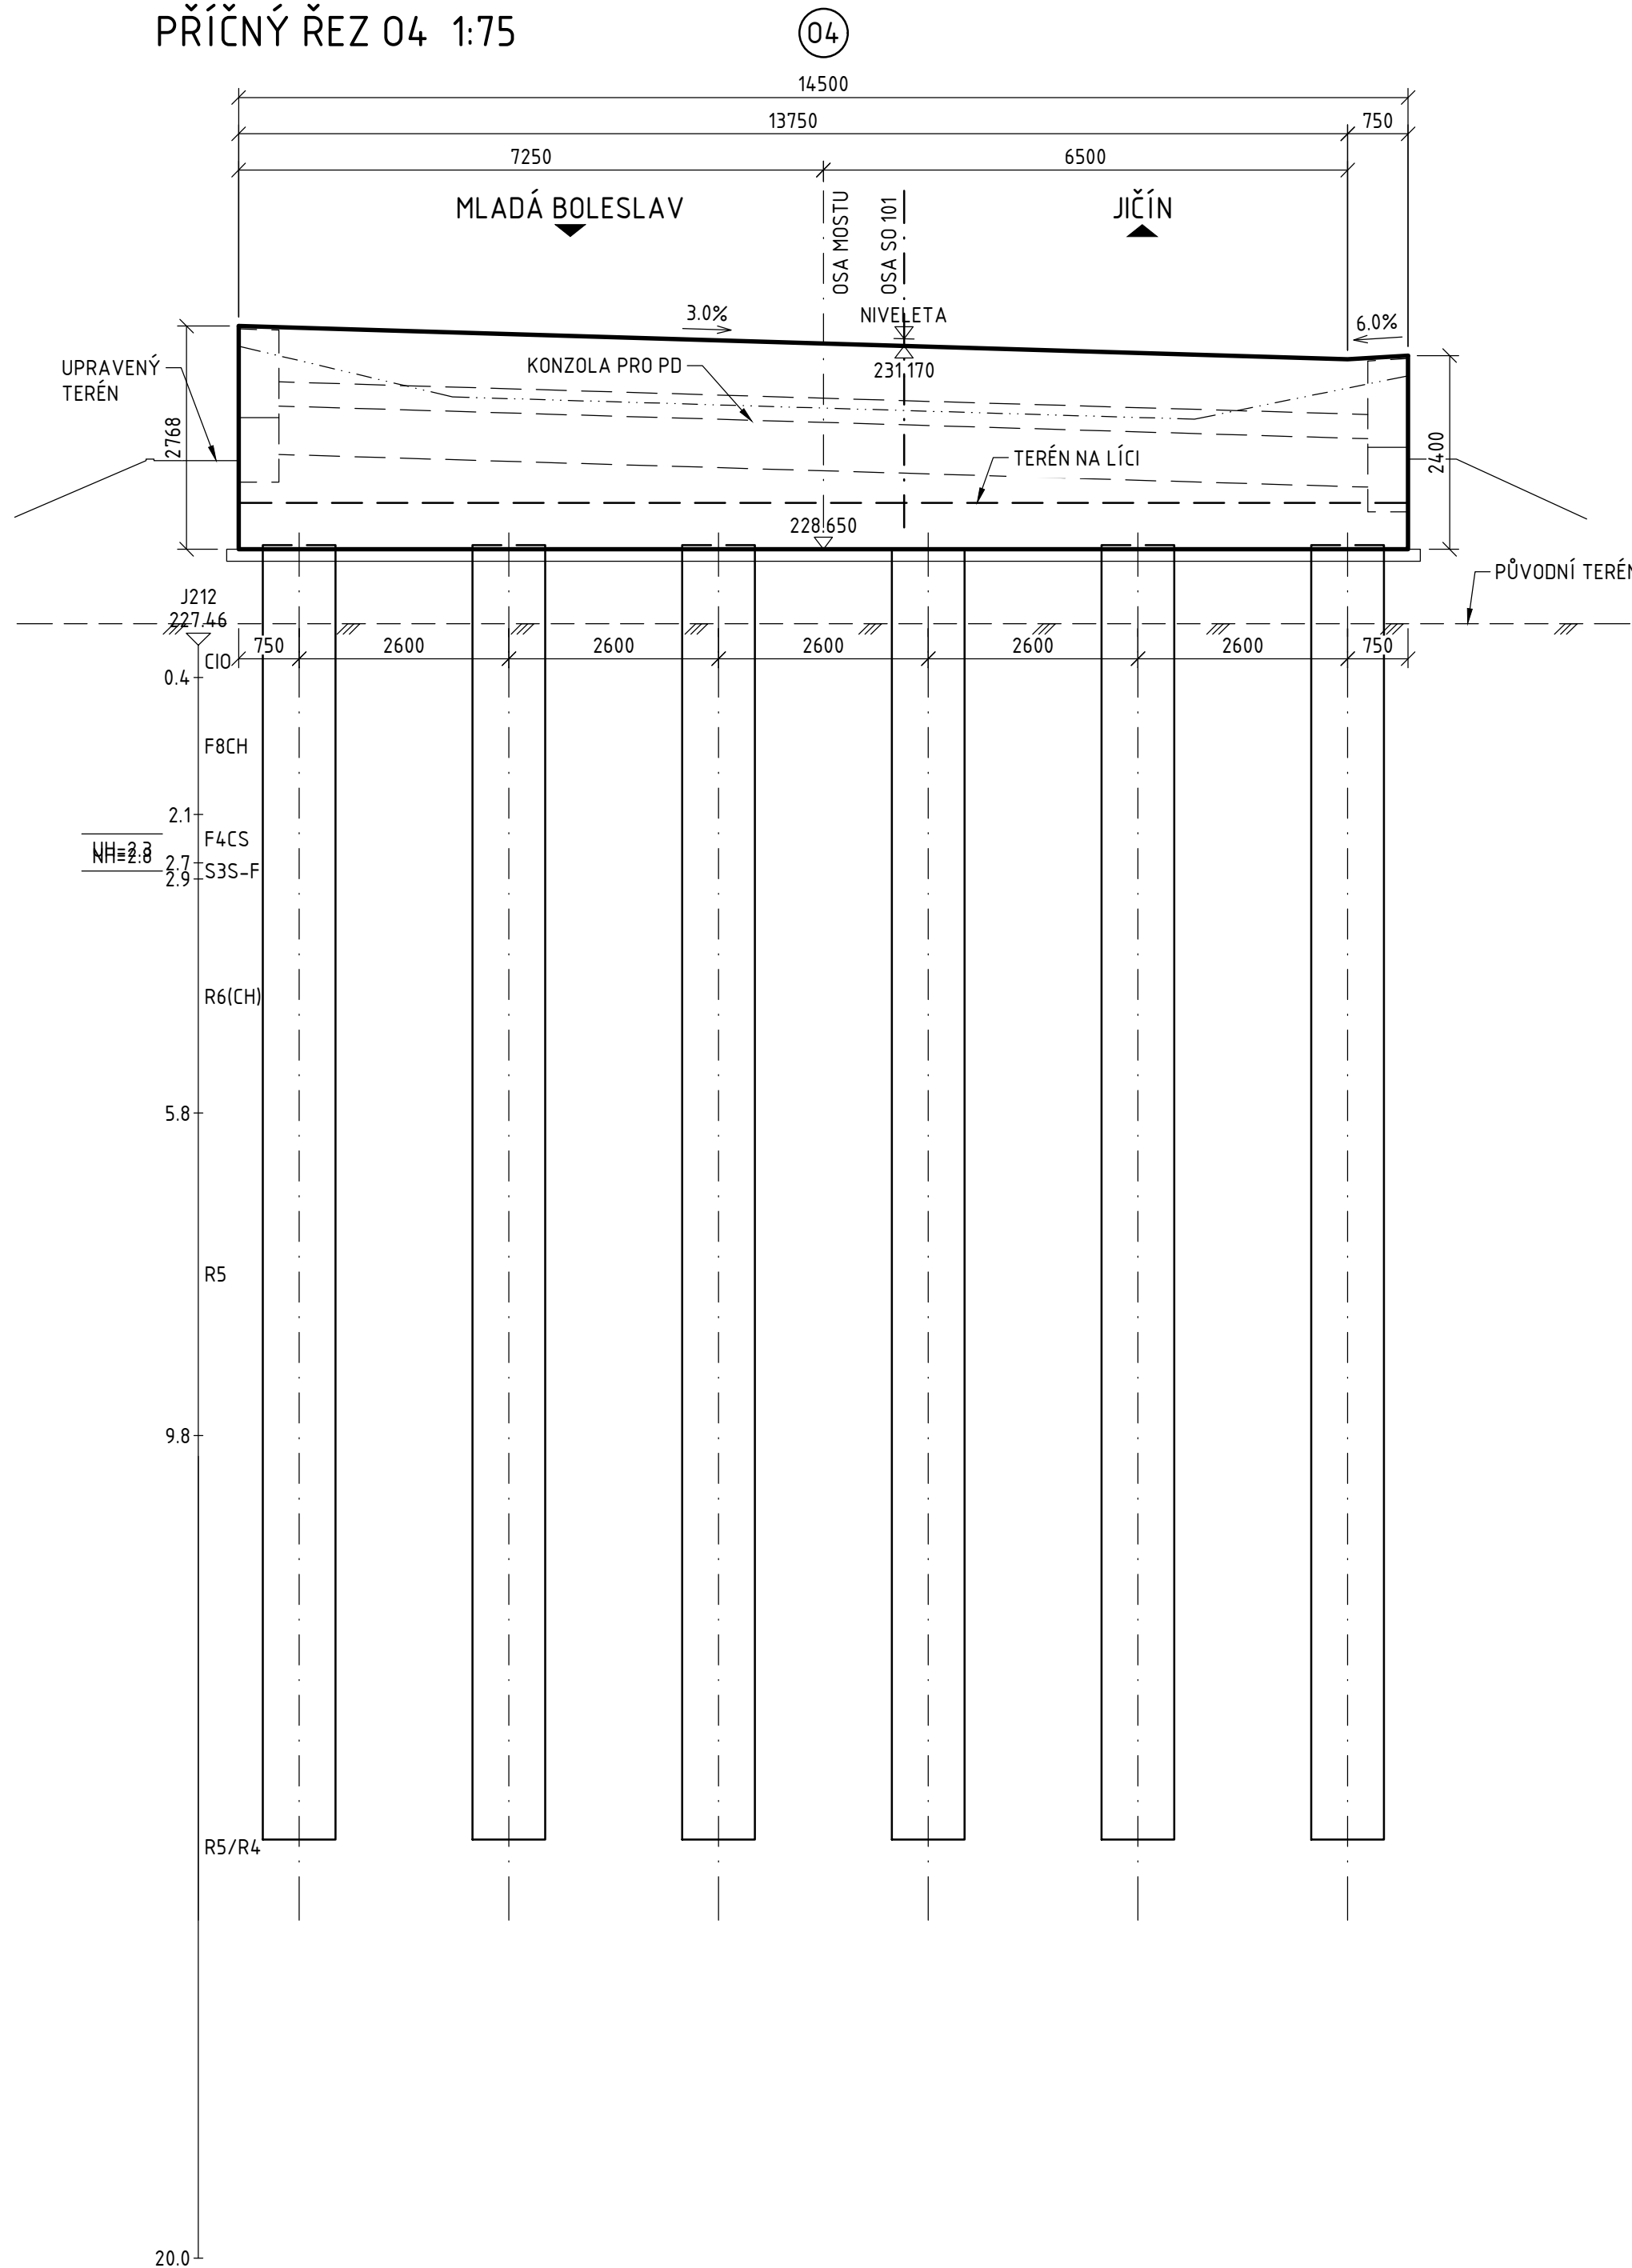


PŘÍČNÝ ŘEZ 01 1:75



PŘÍČNÝ ŘEZ 04 1:75



POZNÁMKY:
- NEDÍLNOU SOUČÁSTÍ VÝKRESU JSOU POZNÁMKY A SPECIFIKACE UVEDENÉ NA VÝKRESE POZNÁMEK A TECHNICKÝCH SPECIFIKACÍ

Souřadnicový systém: S-JTSK
Výškový systém: Bpv

SO 206 MOST NA I/16 PŘES PŘELOŽKU POLNÍ CESTY V KM 6,700

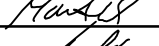
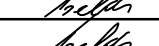
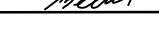
Objednatel:

**Ředitelství silnic a dálnic**
Čerčanská 2023/12, Krč, 140 00 Praha 4

Ředitelství silnic a dálnic s. p.
Čerčanská 2023/12, Krč, 140 00 Praha 4

**Valbek**

Valbek, spol. s r.o.
Vaňurova 505/17
460 07 Liberec 3

 Valbek	Vypracoval	L. MARTÍNEK		Zak. číslo	21-L113-001
	Zodp. projektant	ING. I. BELDA		Datum	02/2025
	Tech. kontrola	ING. I. BELDA		Stupeň	PDPS
	Akce	I/16 MLADÁ BOLESLAV - MARTINOVICE		Počet formátů	8x A4
Zhotovitel:		Příloha		Měřítko	1:75
Valbek, spol. s r.o.		TVAR PŘÍČNÍKŮ		Č. přílohy	Paré
Vaňurova 505/17				203	
460 07 Liberec 3					