




SCHÉMA ODVODNĚNÍ
PODÉLNÝ ŘEZ ODVODNĚNÍM 1:100

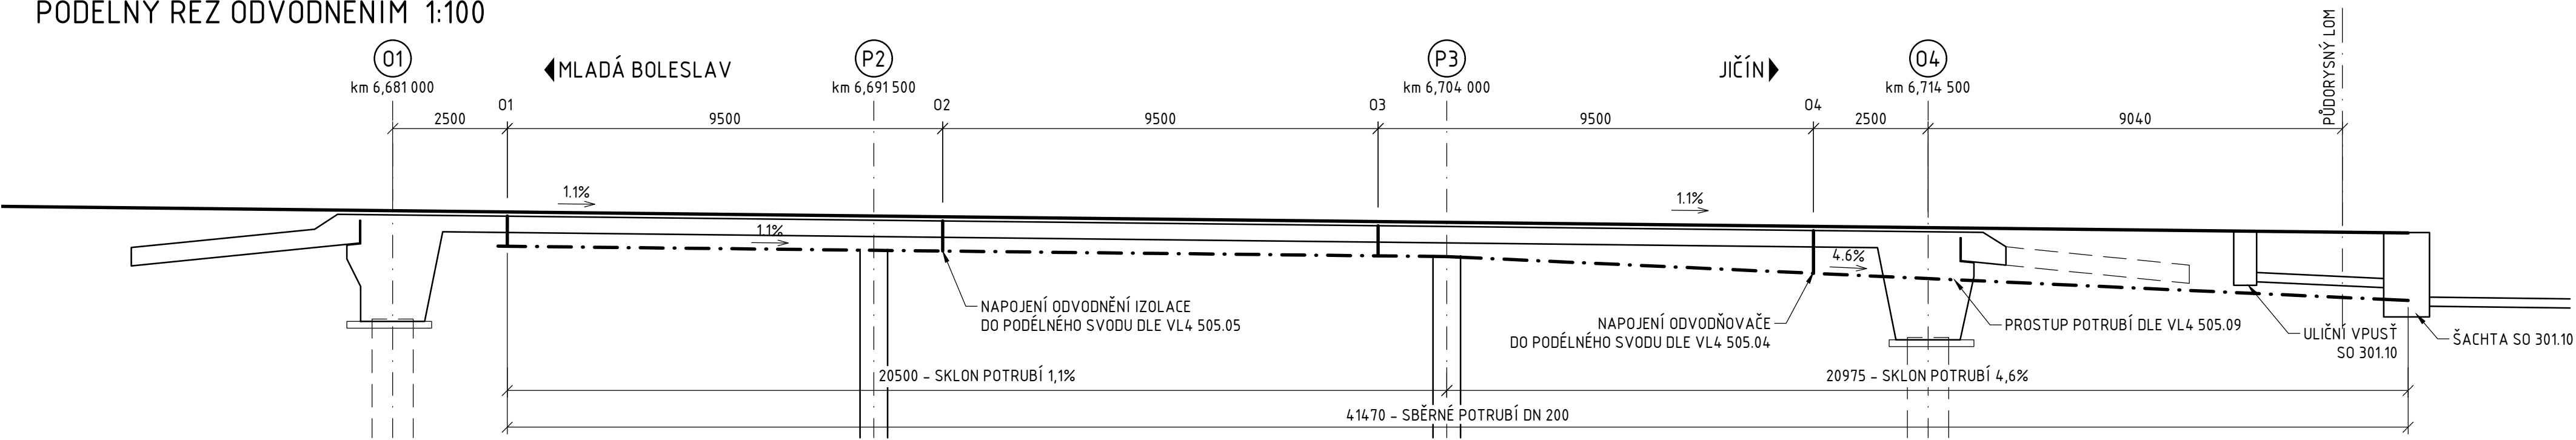



TVAR ŘÍMS
PŮDORYS 1:100

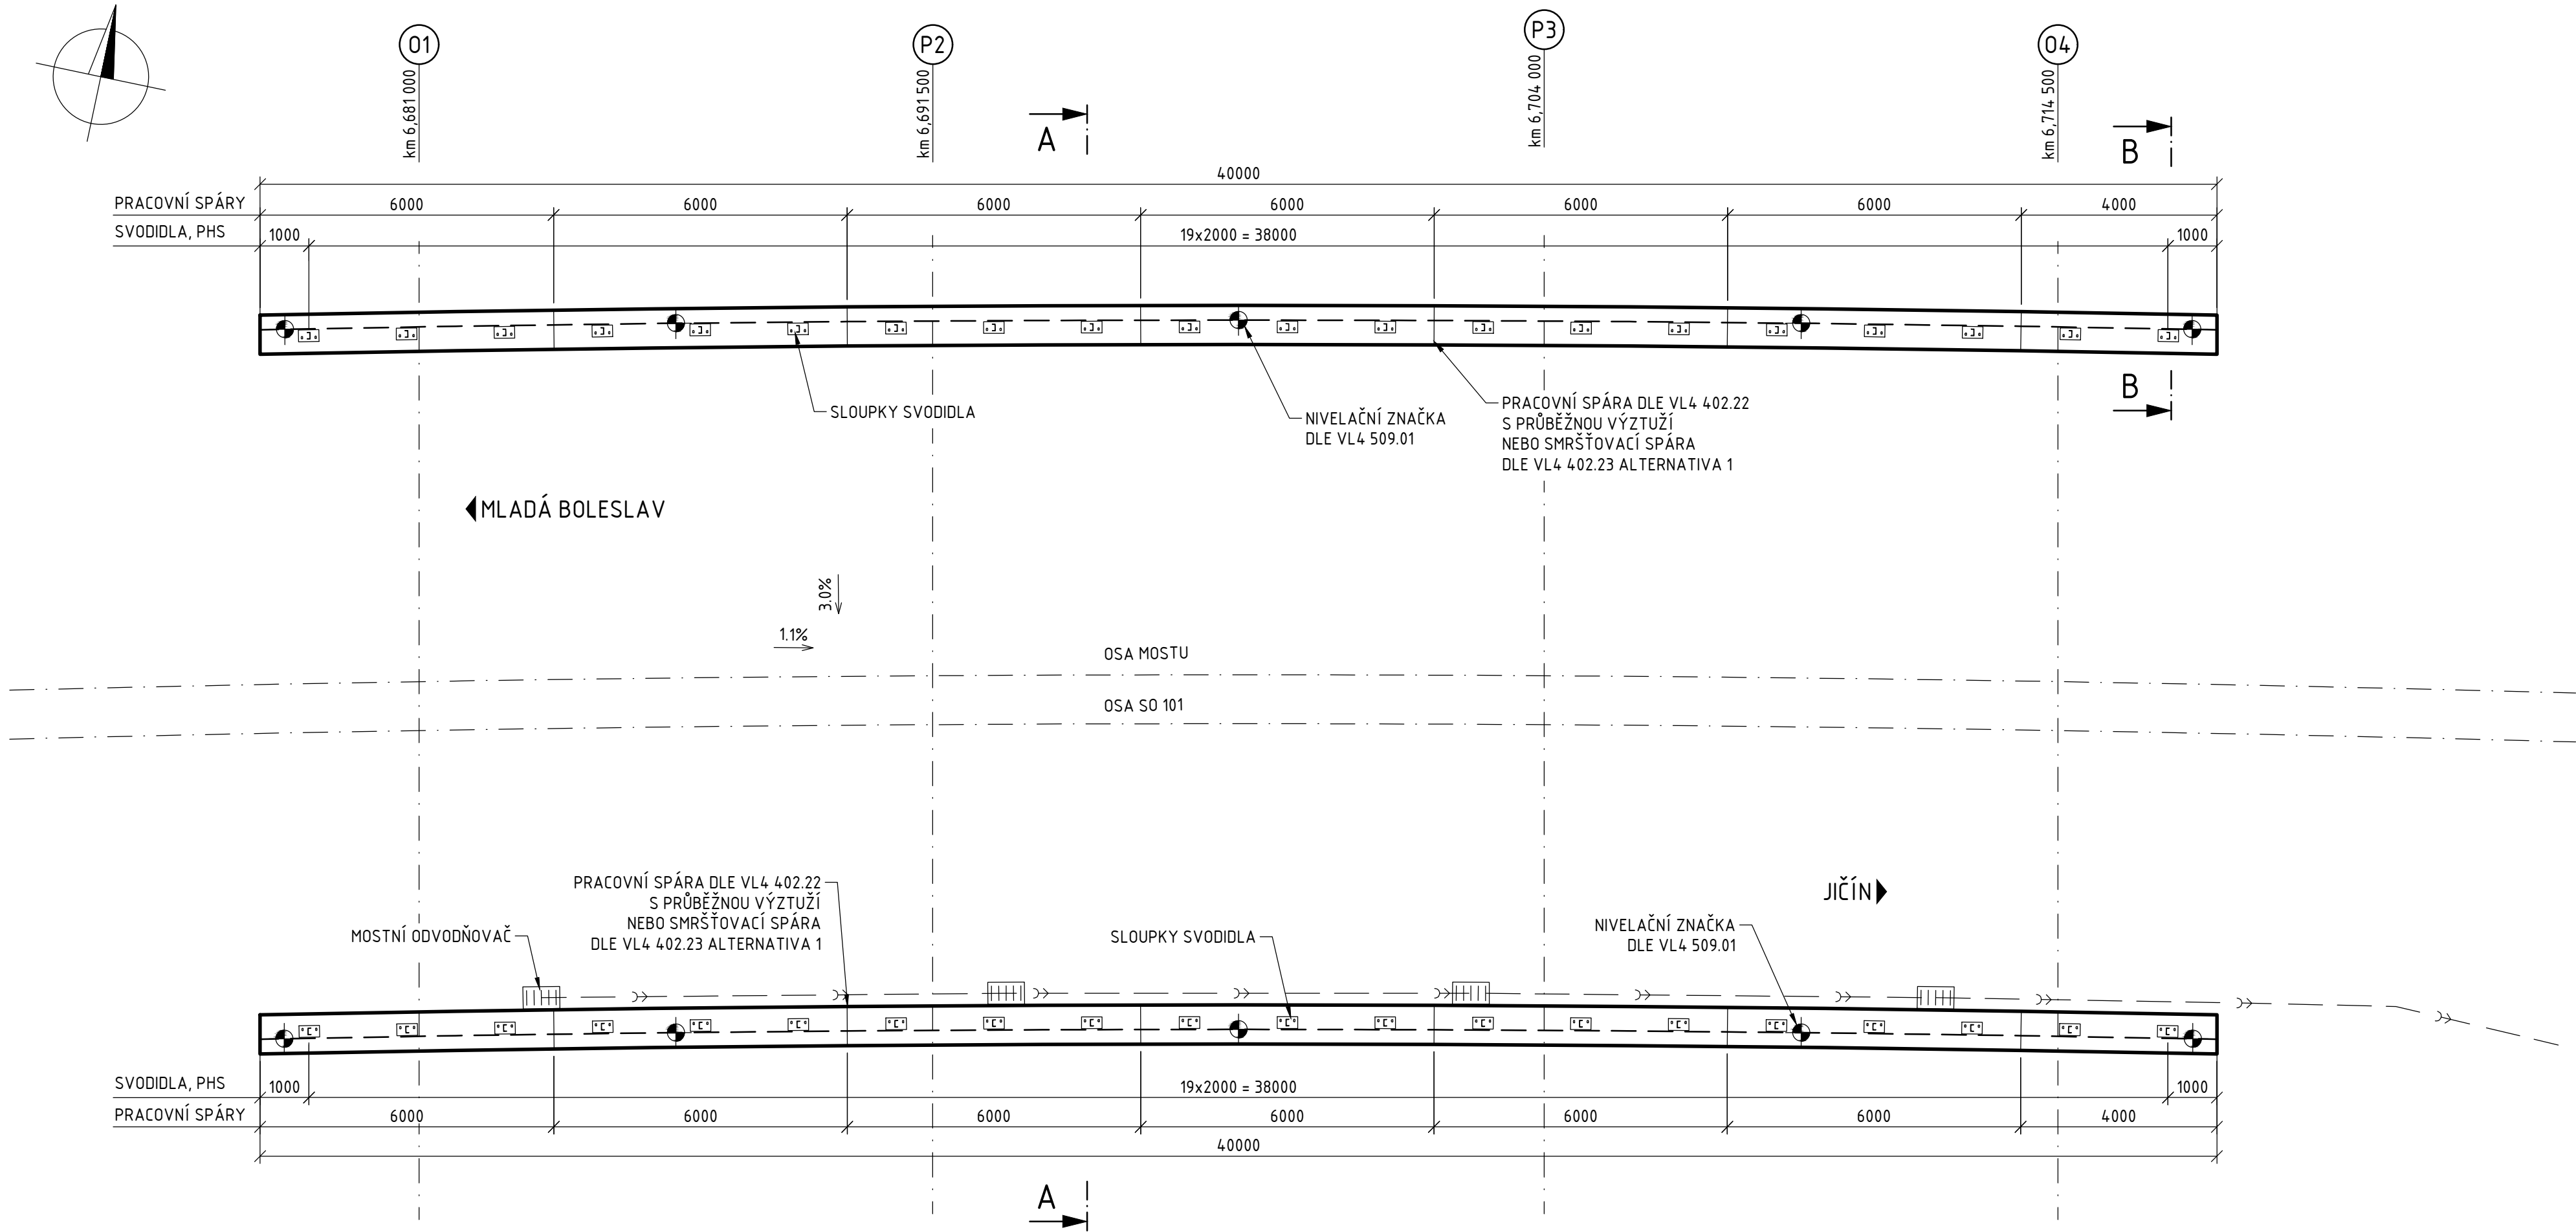


ŘEZ A-A 1:20
LEVÁ ŘÍMSA

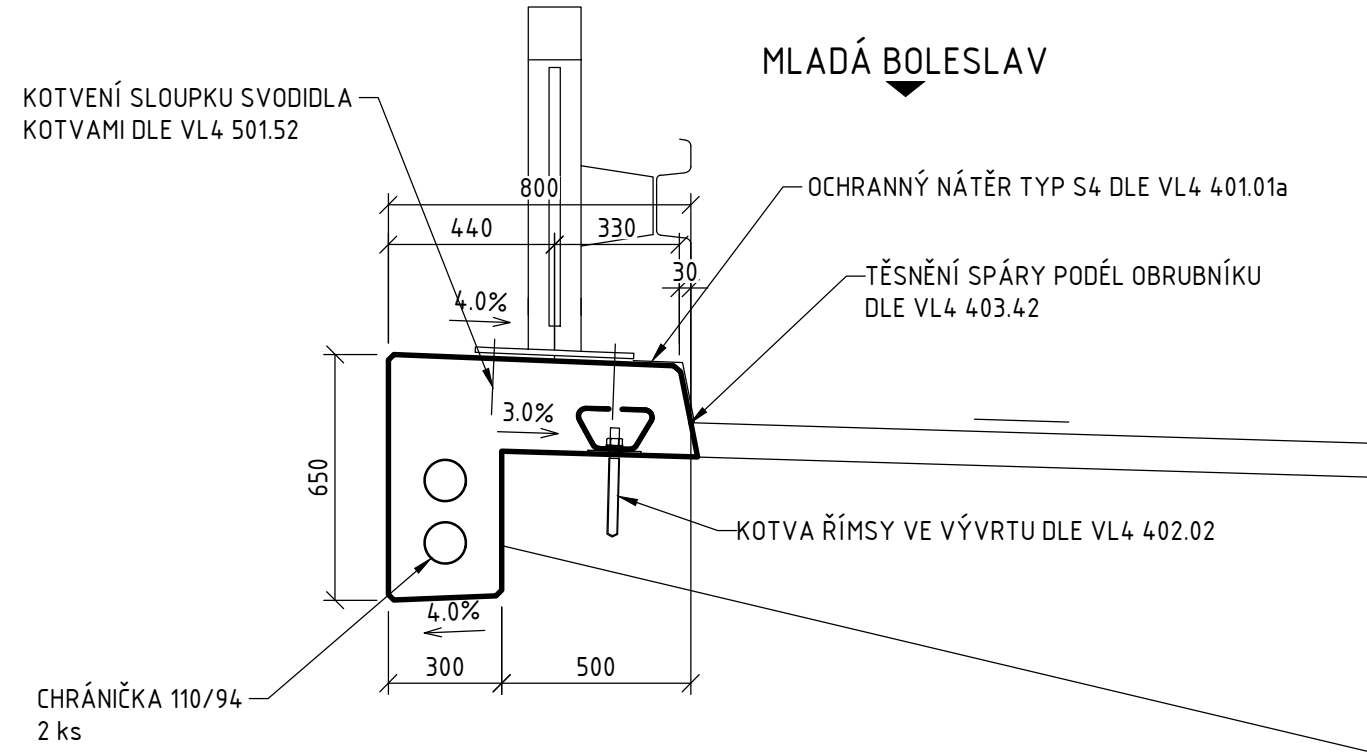

PRAVÁ ŘÍMSA

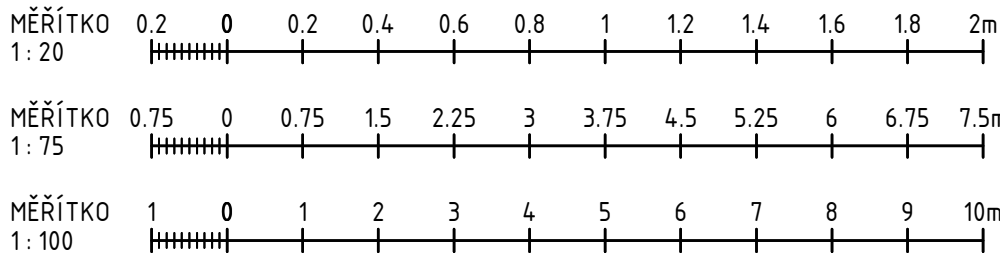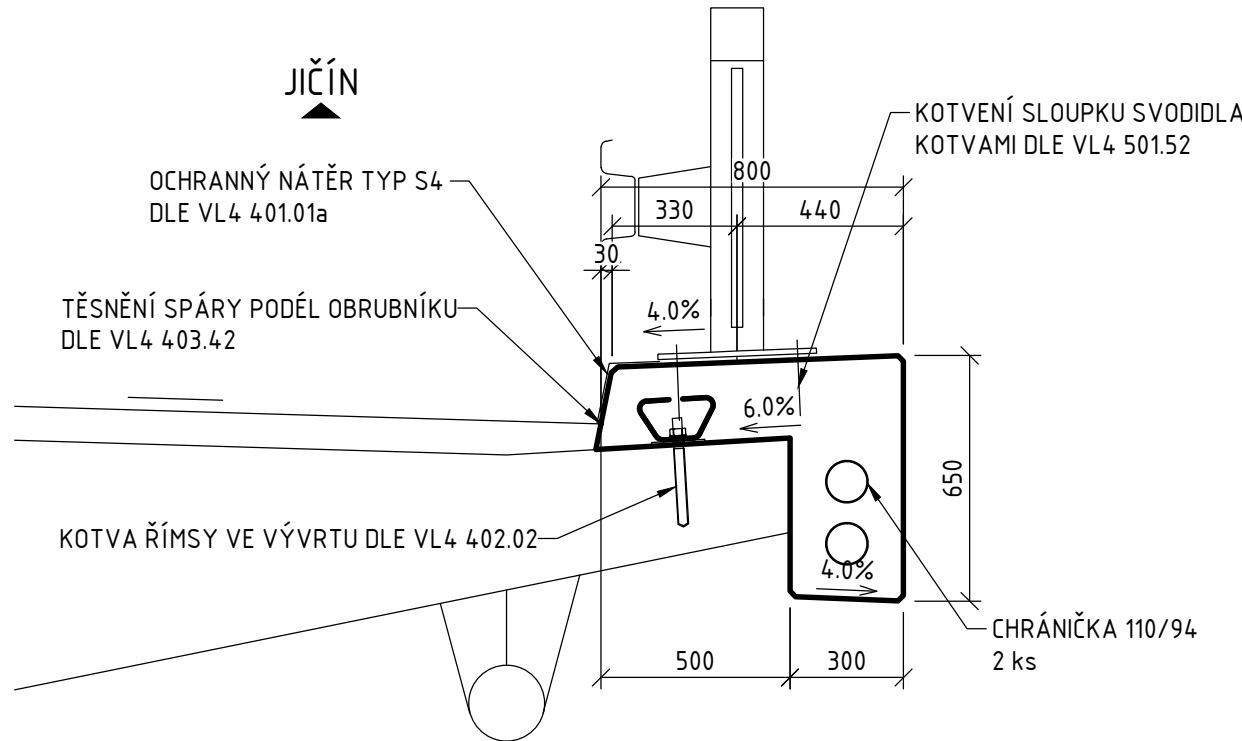


VZOROVÝ PŘÍČNÝ ŘEZ 1:75

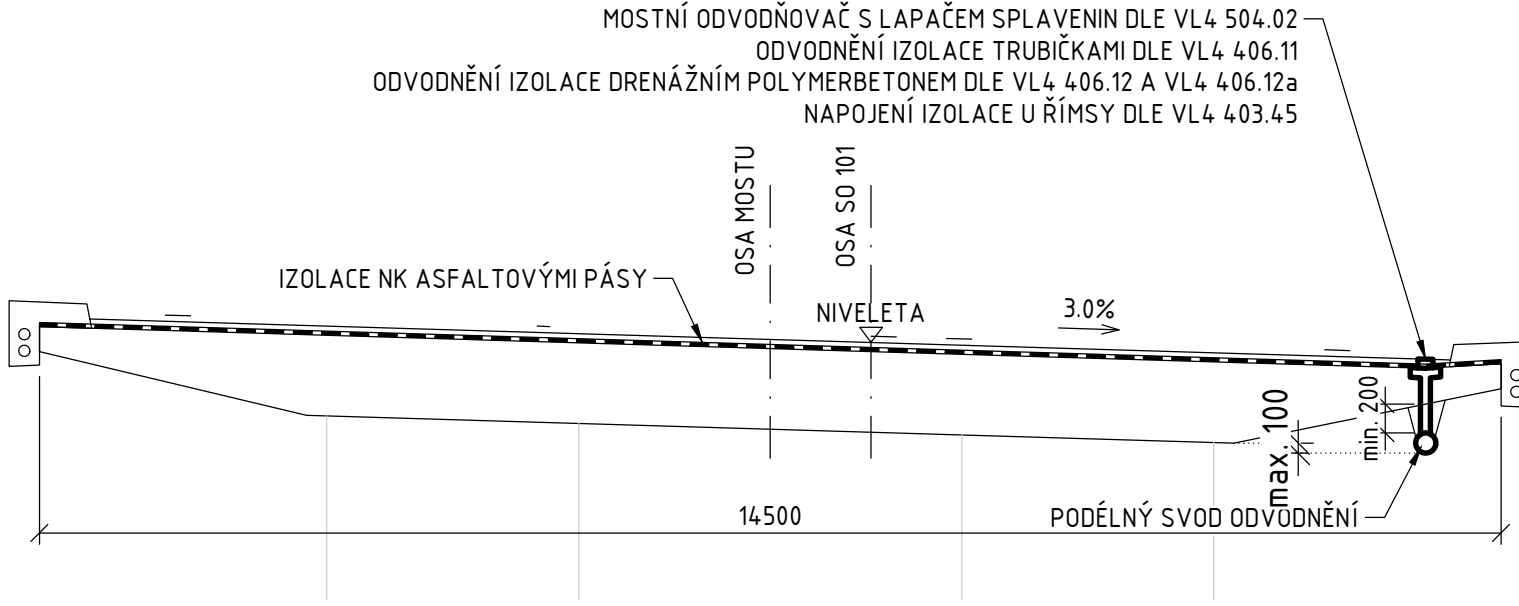

ŘEZ B-B 1:20

LEVÁ ŘÍMSA (PRAVÁ ŘÍMSA ODBOBNĚ)

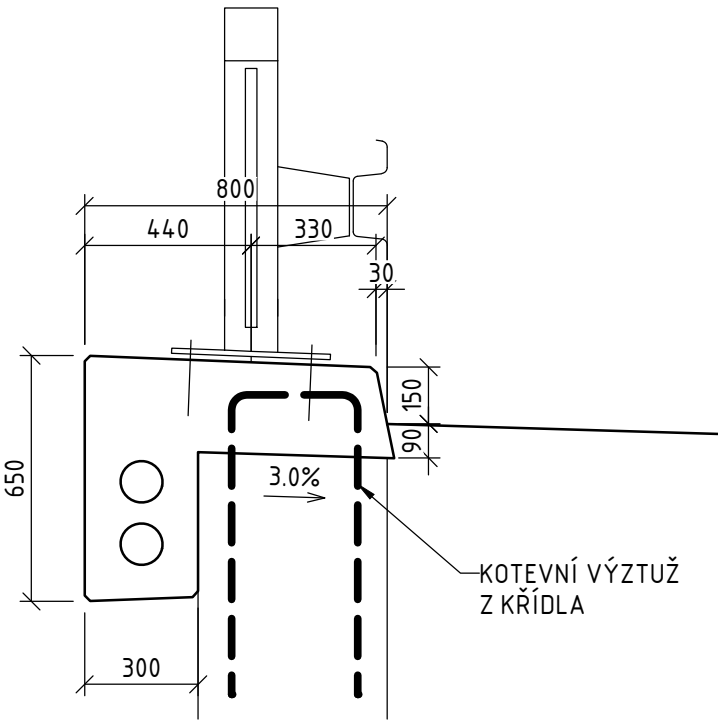

LEGENDA:

— — — — — PRACOVNÍ SPÁRA

POZNÁMKY:

- NEDÍLNOU SOUČÁSTÍ VÝKRESU JSOU POZNÁMKY A SPECIFIKACE UVEDENÉ NA VÝKRESU
POZNÁMEK A TECHNICKÝCH SPECIFIKACÍ

Souřadnicový systém: S-JTSK
Výškový systém: Bpv

SO 206 MOST NA I/16 PŘES PŘELOŽKU POLNÍ CESTY V KM 6,700

Objednatel:



Ředitelství silnic a dálnic s. p.
Čerčanská 2023/12, Krč, 140 00 Praha 4



Valbek, spol. s r.o.
Vaňurova 505/17
460 07 Liberec 3



Vypracoval	ING. I. BELDA		Zak. číslo	21-L113-001	
Zodp. projektant	ING. I. BELDA		Datum	02/2025	
Tech. kontrola	ING. I. BELDA		Stupeň	PDPS	
Akce	I/16 MLADÁ BOLESLAV - MARTINOVICE			Počet formátů	8x A4
				Měřítko	1:100,75,20
				Č. přílohy	Paré
Příloha	TVAR ŘÍMS, SCHÉMA ODVODNĚNÍ			204	