




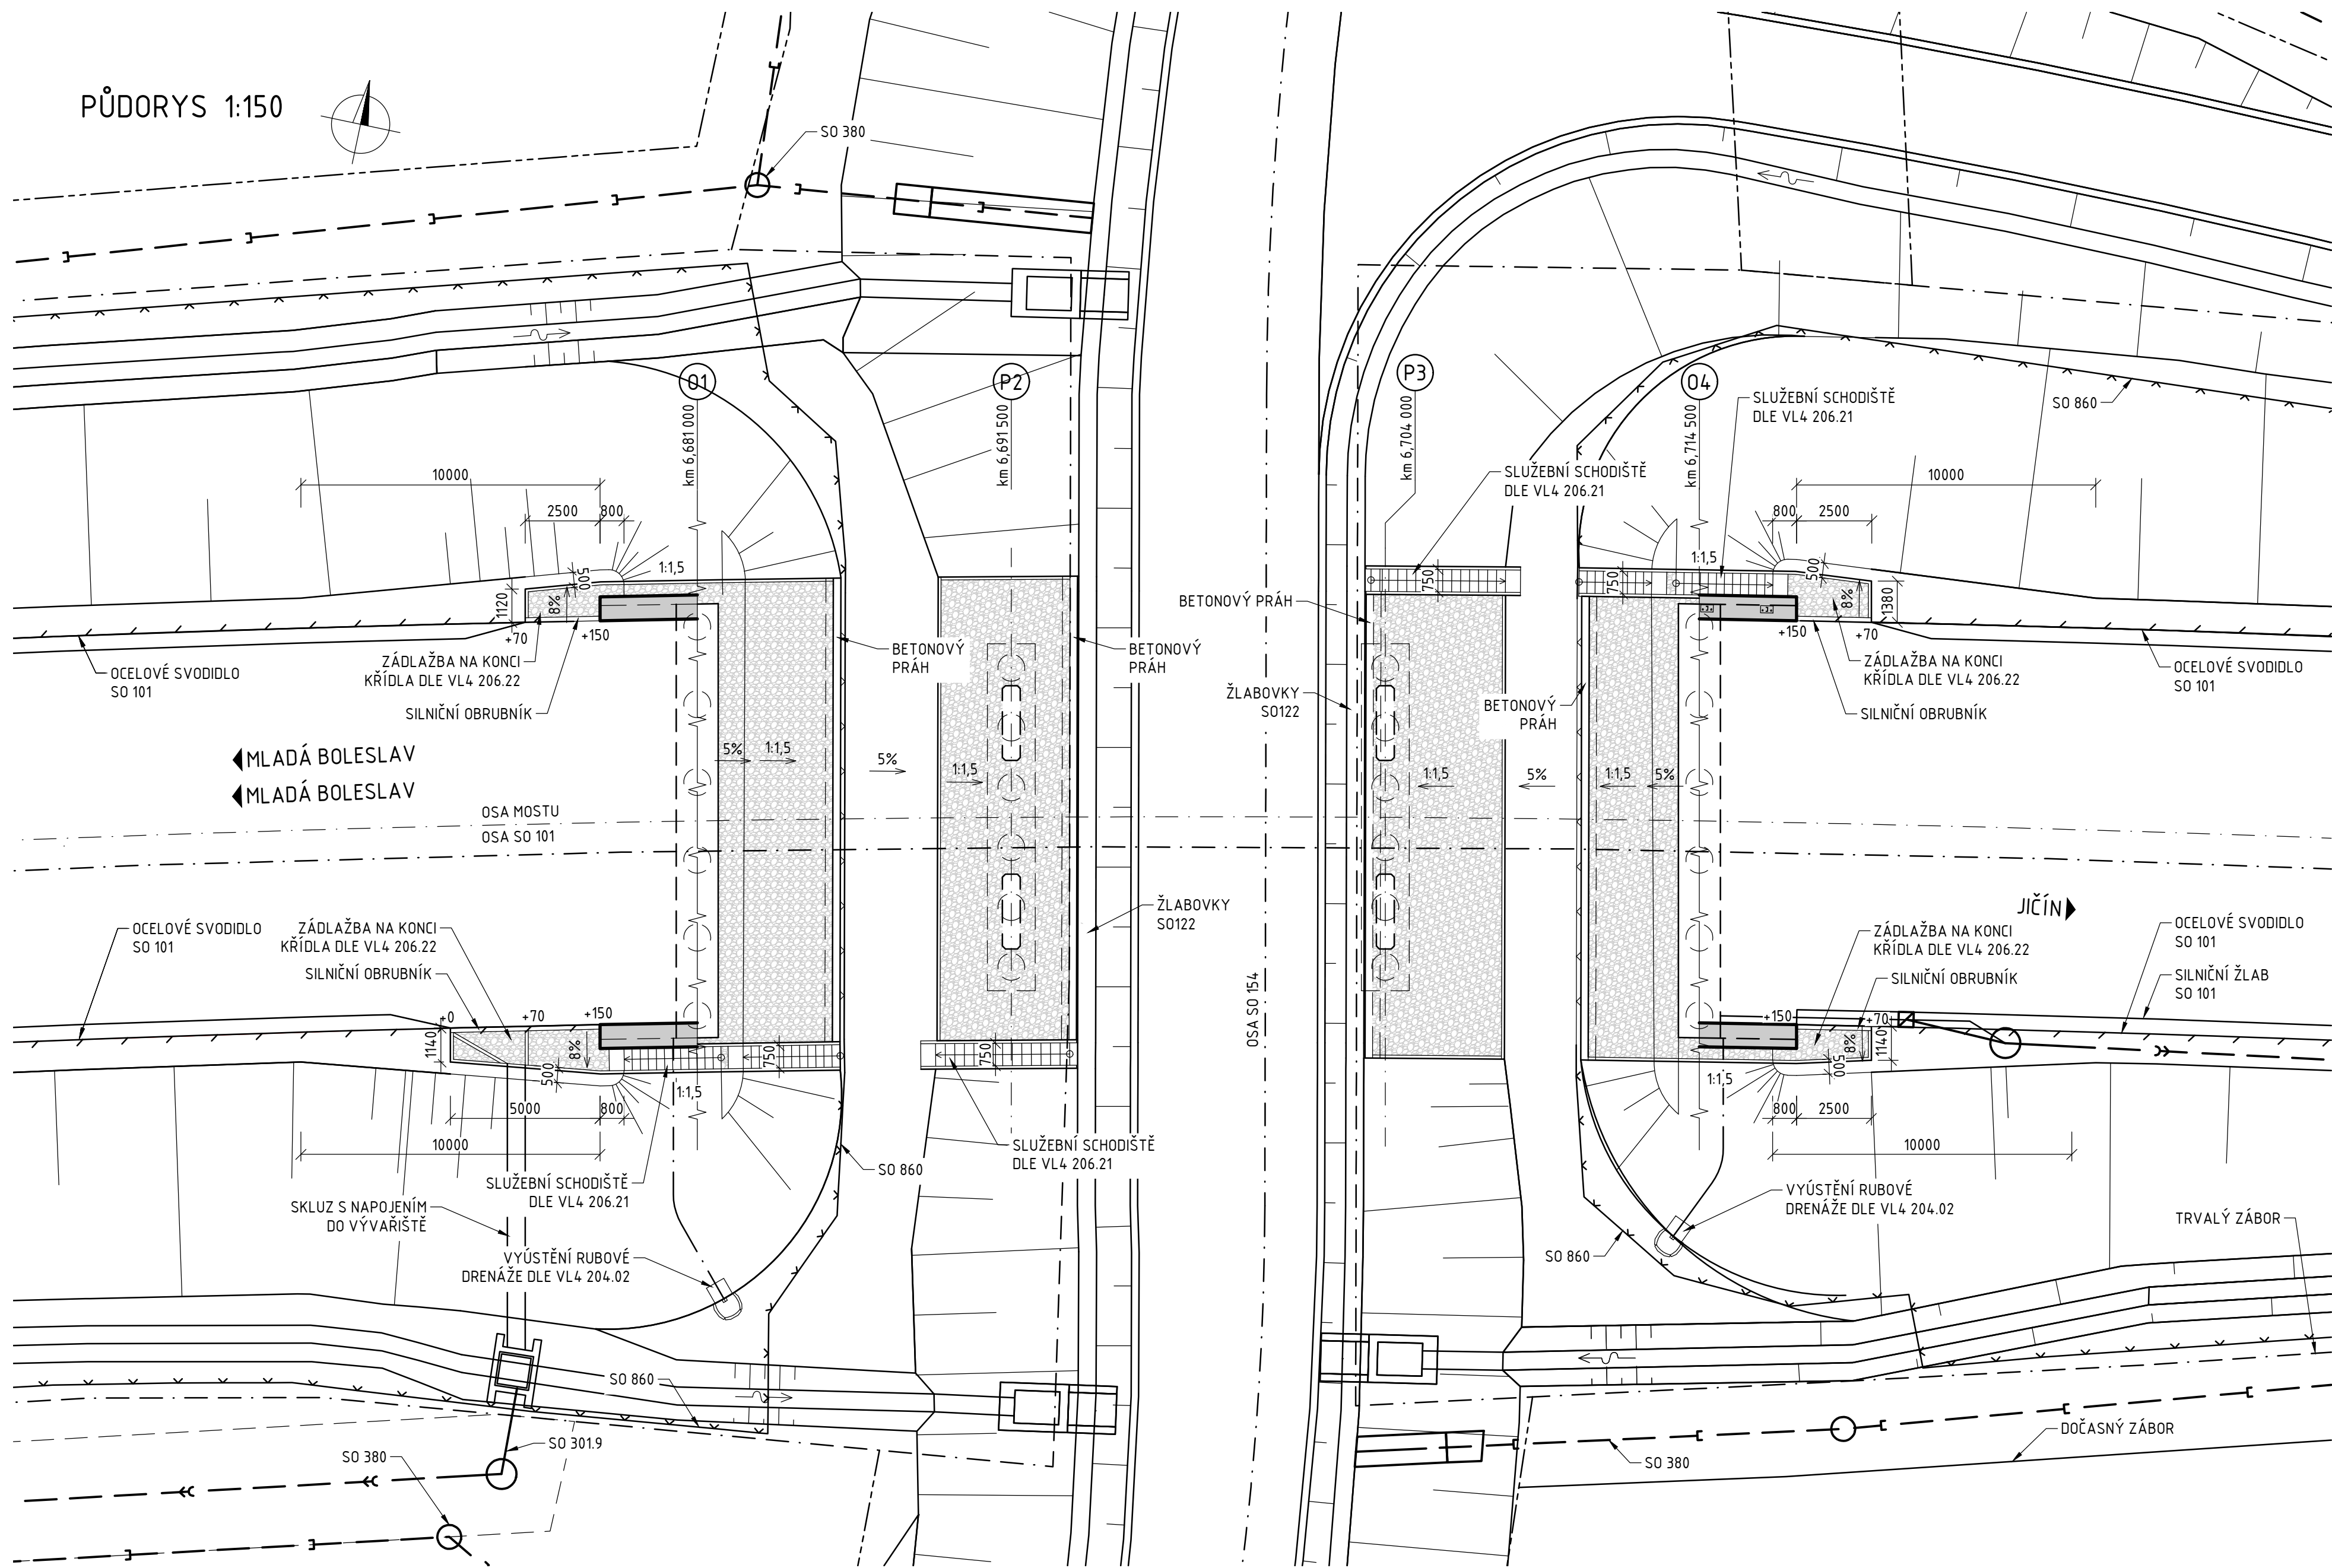


SLUŽEBNÍ SCHODIŠTĚ

SCHODIŠTĚ 1 - PODÉLNÝ ŘEZ 1:75

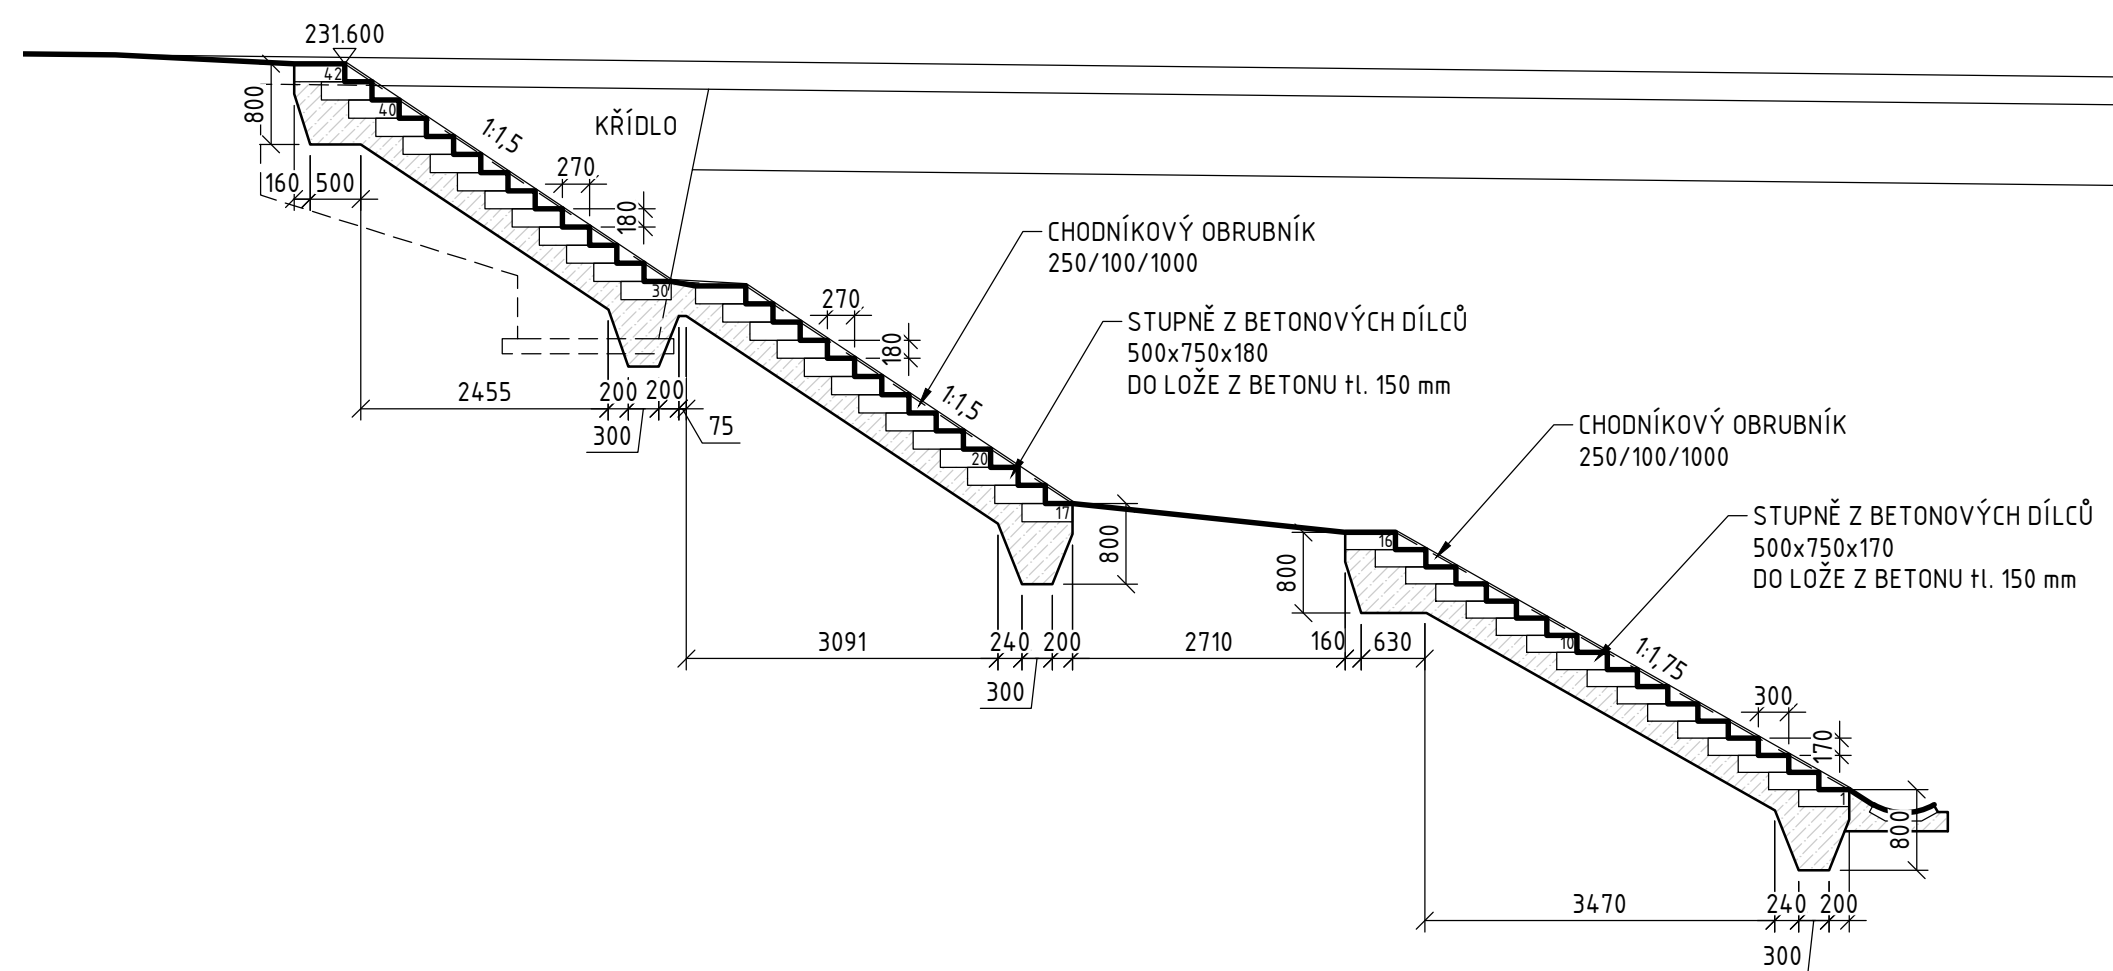


SCHODIŠTĚ 2 - PODÉLNÝ ŘEZ 1:75

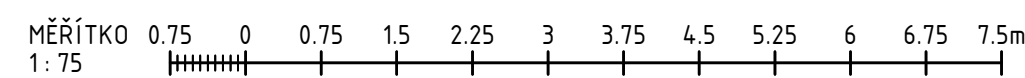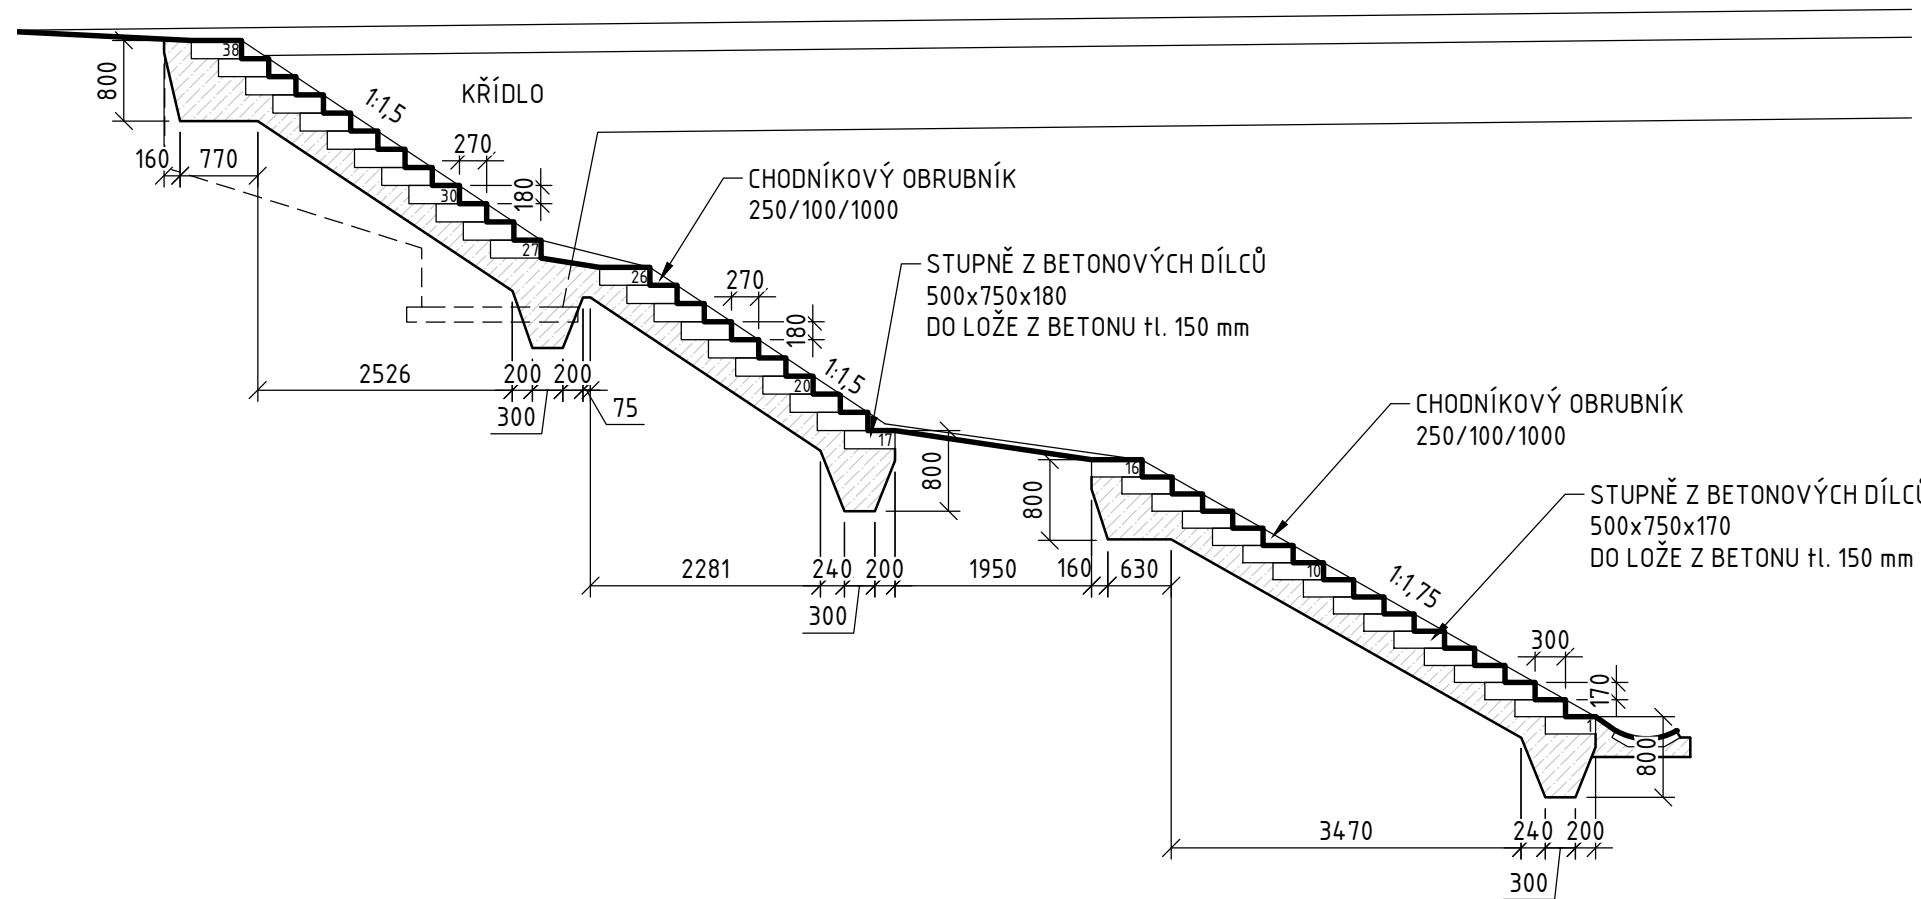


OPEVNĚNÍ SVAHU OPĚRY 01

1:75

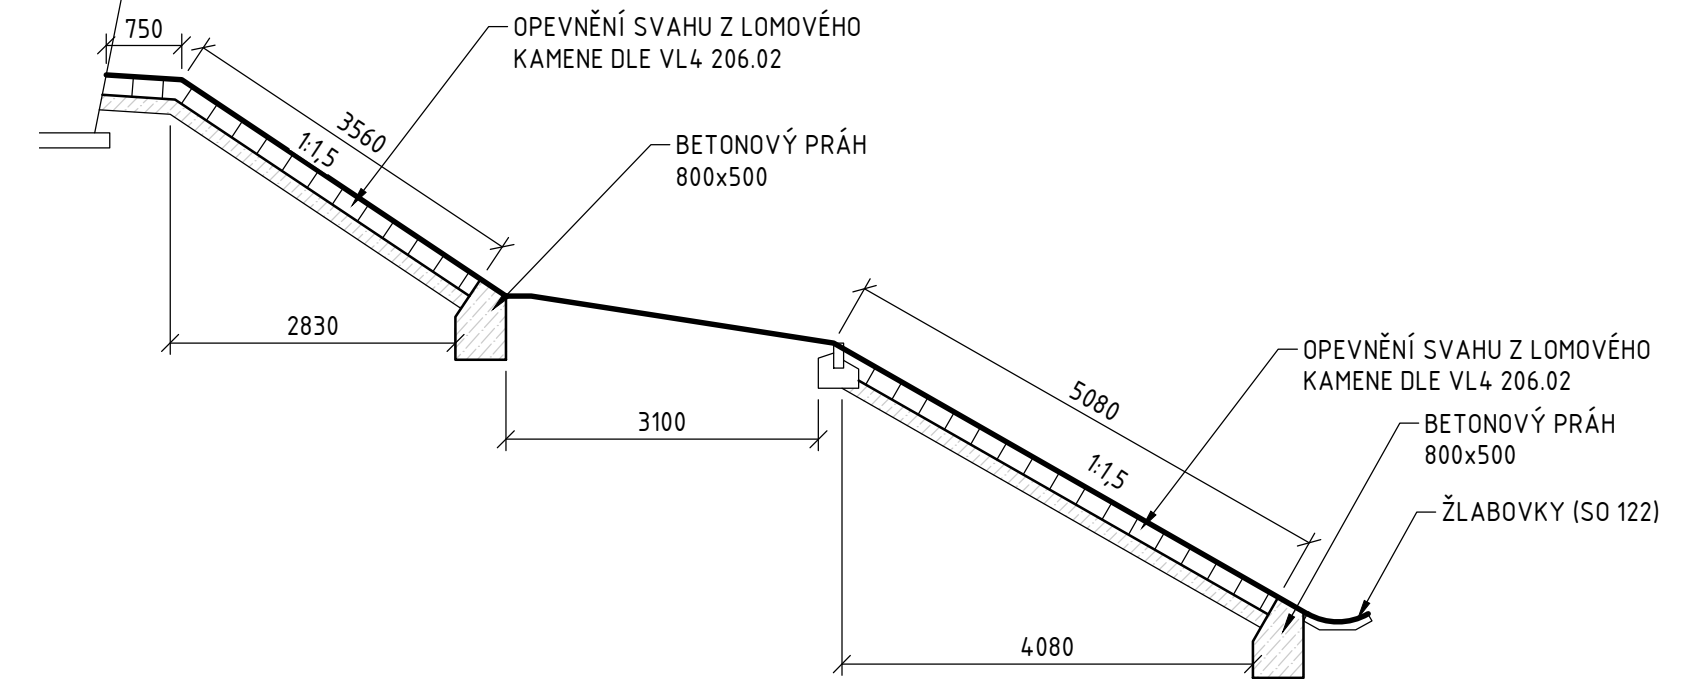

OPEVNĚNÍ SVAHU OPĚRY 04

1:75

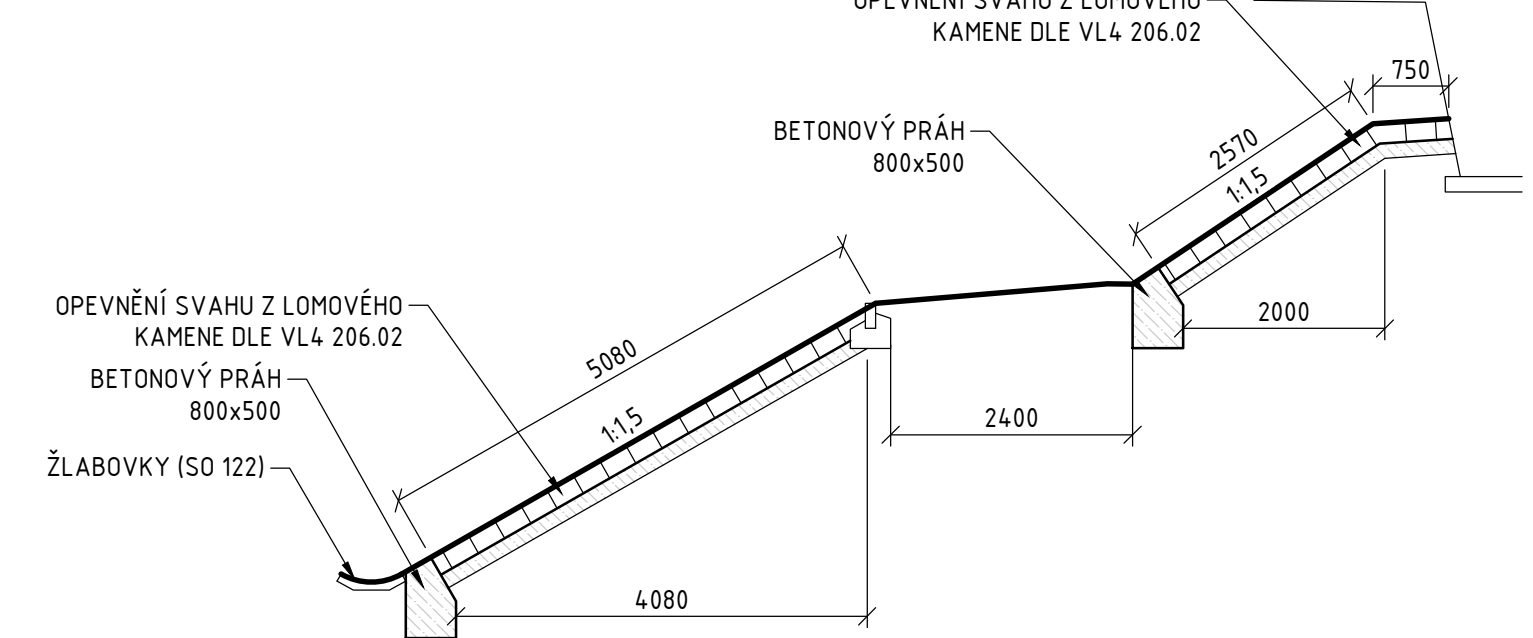

POZNÁMKY:

- NEDÍLNOU SOUČÁSTÍ VÝKRESU JSOU POZNÁMKY A SPECIFIKACE UVEDENÉ NA VÝKRESE POZNÁMEK A TECHNICKÝCH SPECIFIKACÍ

Souřadnicový systém: S-JTSK
Výškový systém: Bpv

SO 206 MOST NA I/16 PŘES PŘELOŽKU POLNÍ CESTY V KM 6,700

Objednatel:



Ředitelství silnic a dálnic s. p.
Čerčanská 2023/12, Krč, 140 00 Praha 4



Valbek, spol. s r.o.
Vaňurova 505/17
460 07 Liberec 3



Vypracoval	L. MARTÍNEK	Zak. číslo	21-L113-001
Zodp. projektant	ING. I. BELDA	Datum	02/2025
Tech. kontrola	ING. I. BELDA	Stupeň	PDPS
Akce	I/16 MLADÁ BOLESLAV - MARTINOVICE	Počet formátů	8x A4
Měřítko	1:150, 75	Č. přílohy	Paré
Zhotovitel:	Příloha	205	

Zhotovitel:
Valbek, spol. s r.o.
Vaňurova 505/17
460 07 Liberec 3

ÚPRAVY POD MOSTEM