



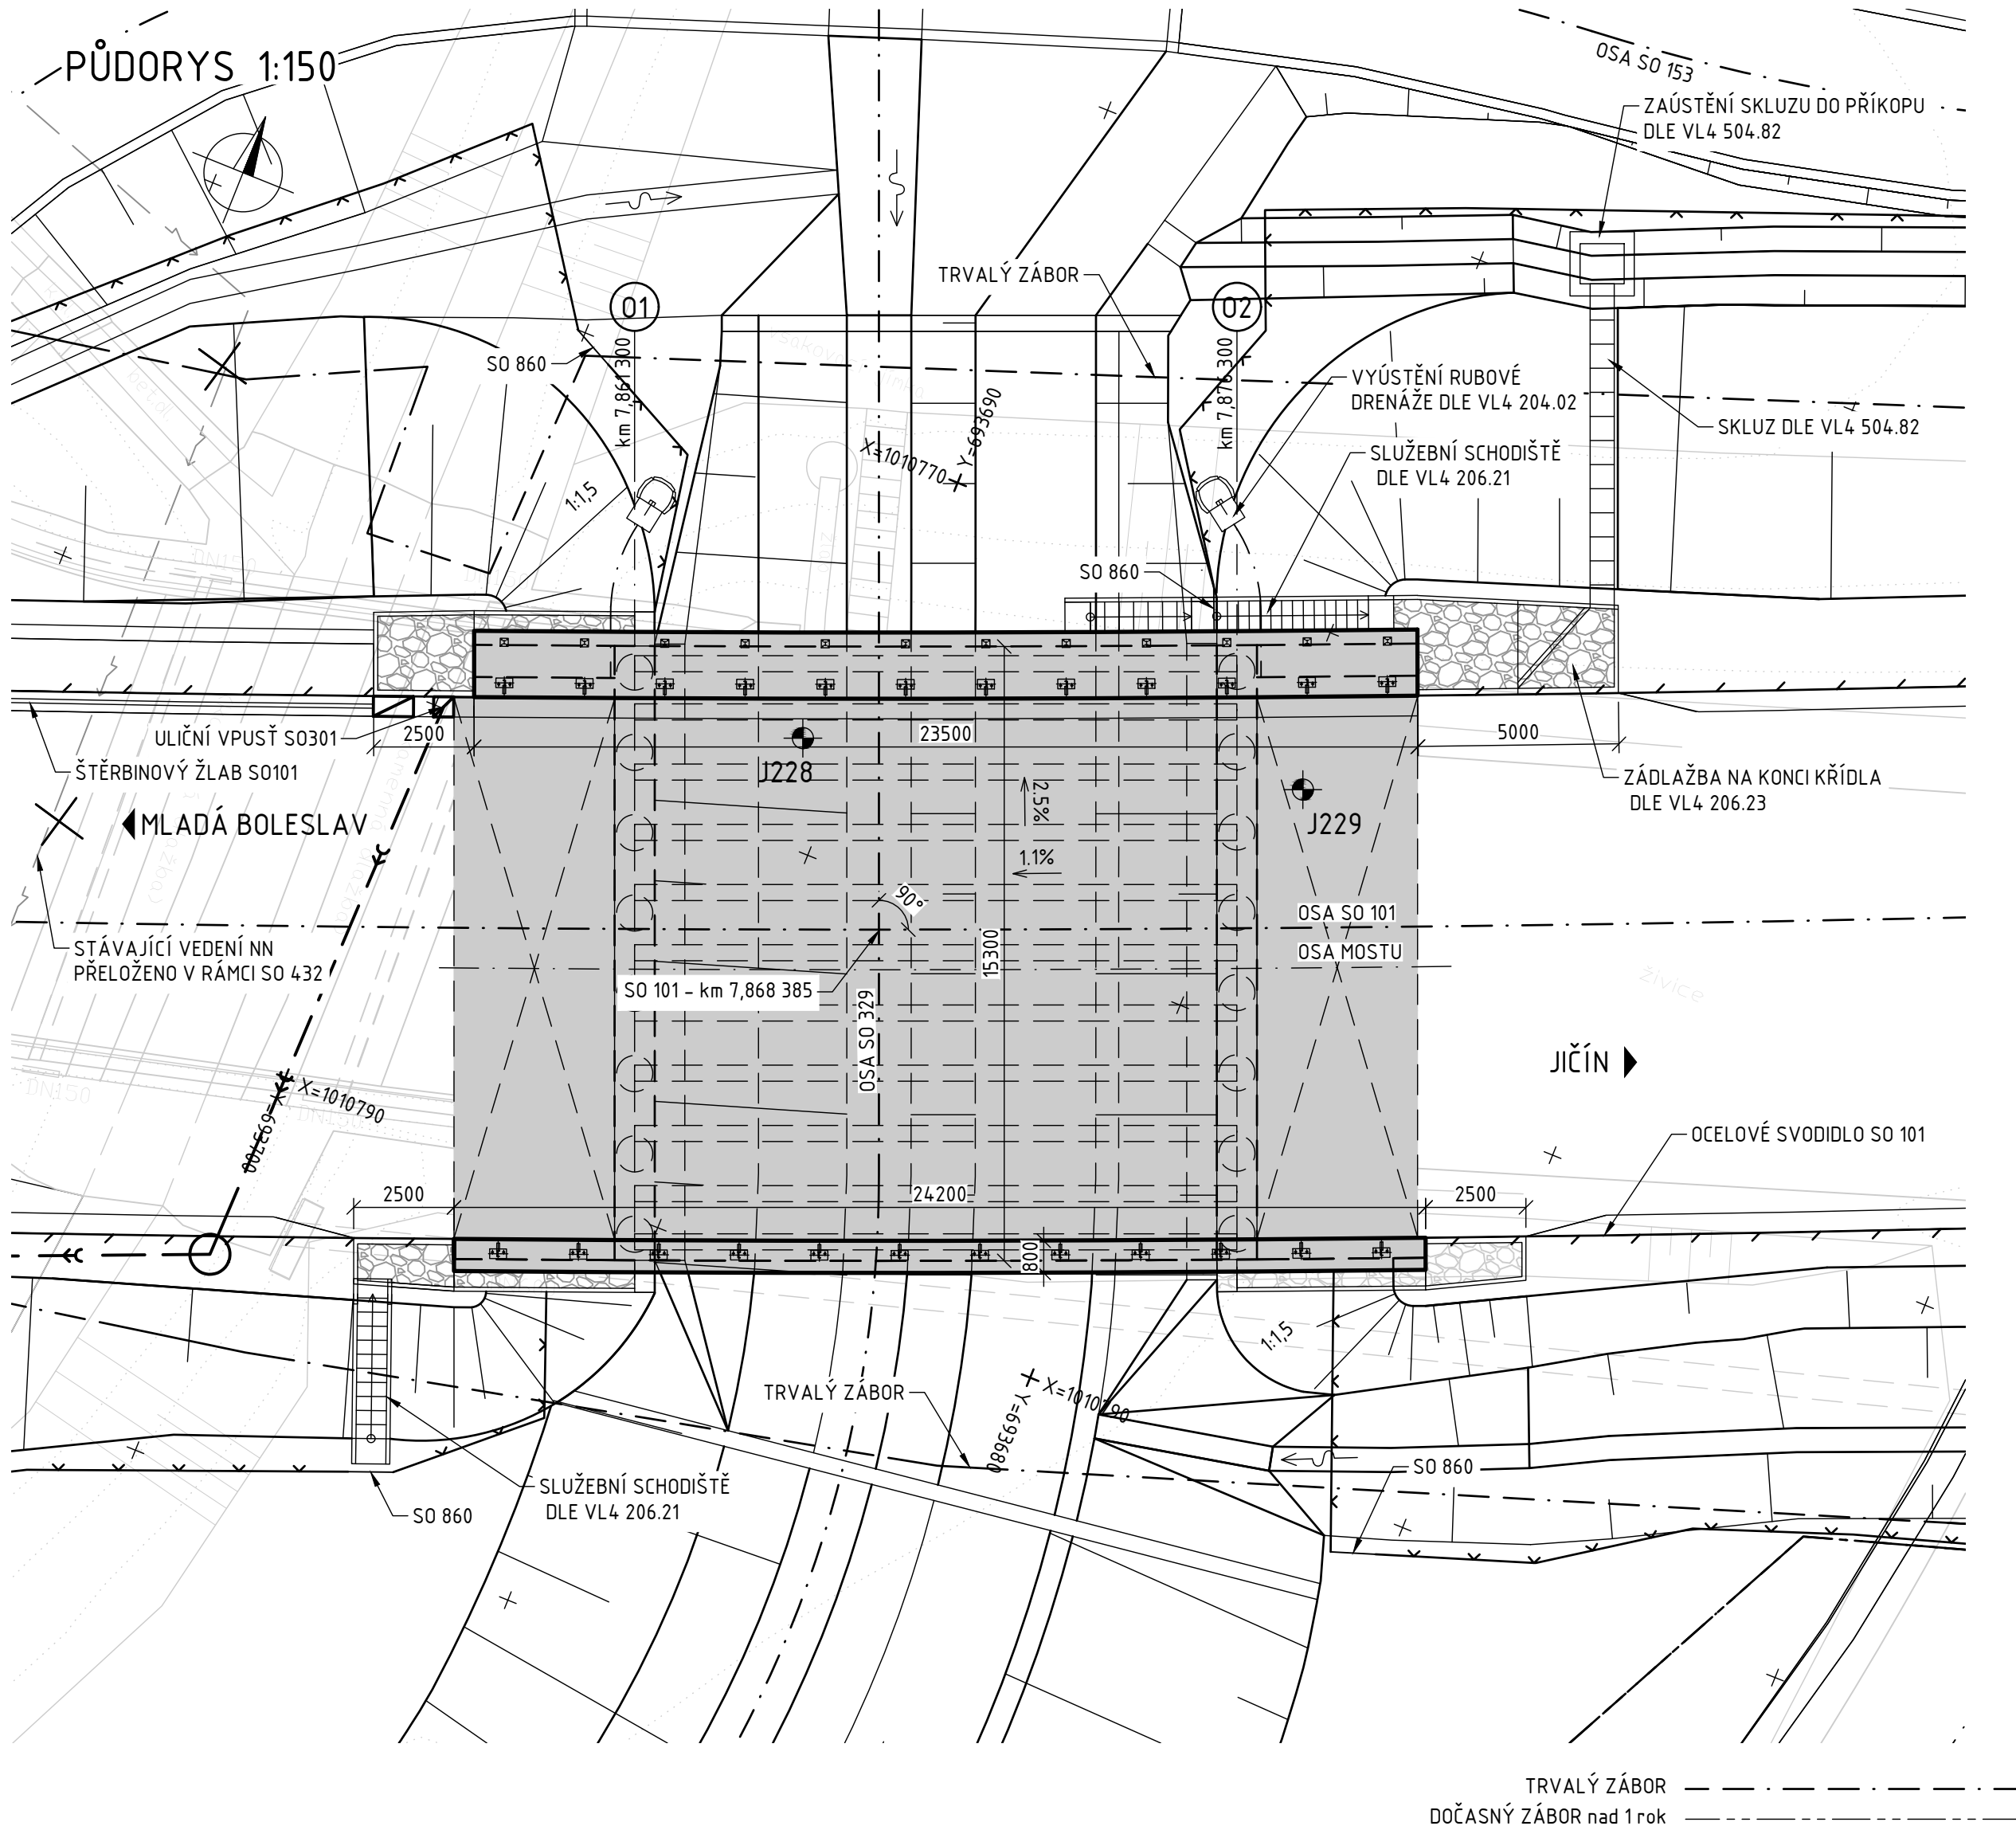


VZOROVÝ PŘÍČNÝ ŘEZ 1:75

-V POLI

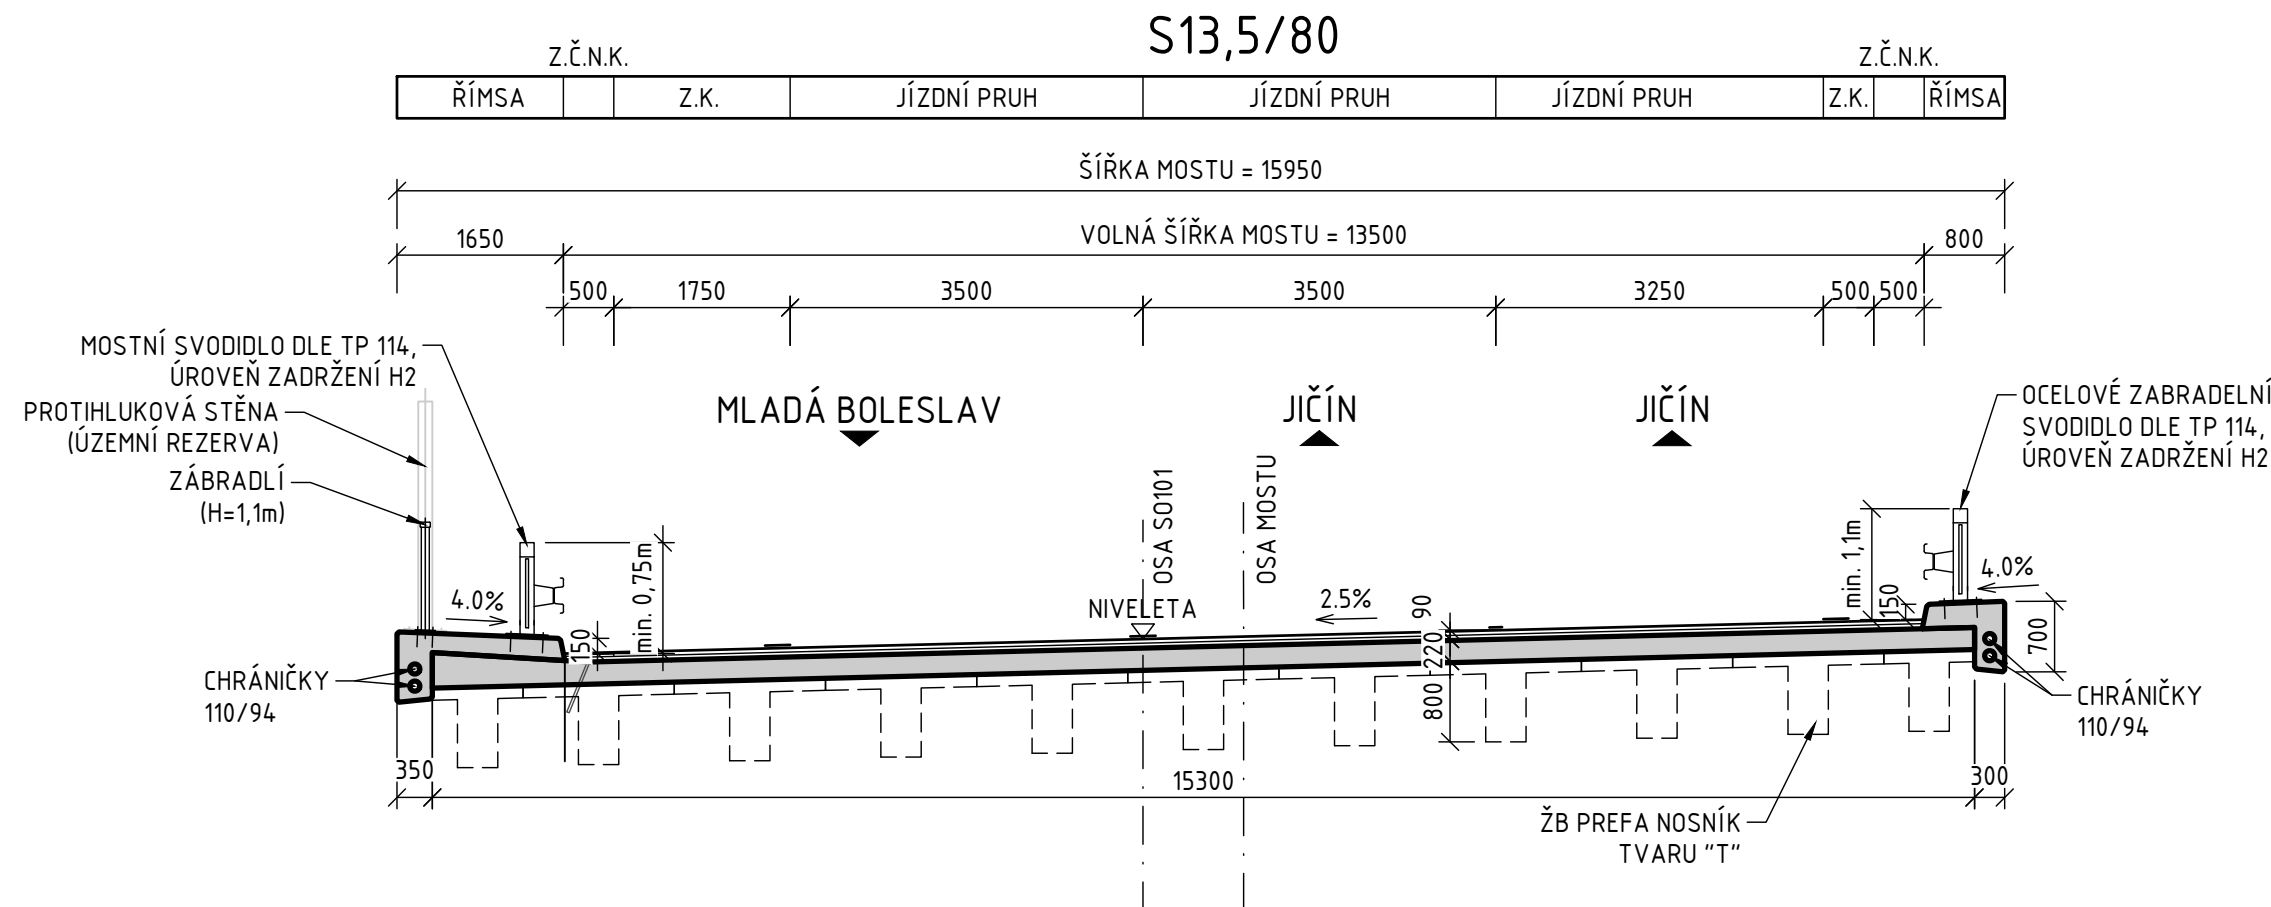

VÝŠKOVÉ VEDENÍ SO 101

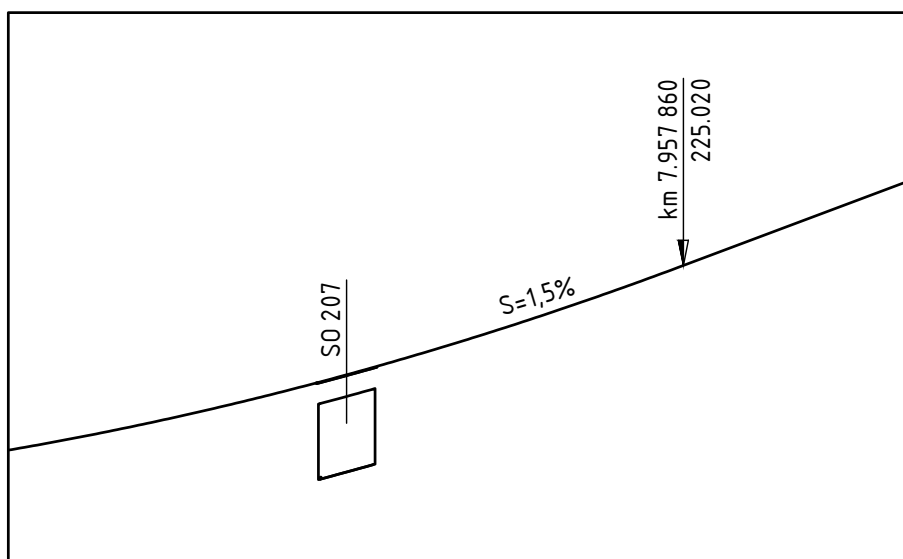

SMĚROVÉ VEDENÍ SO 101


STANIČENÍ	X	Y	PARAMETR
km 7.503 01	694 041.004	1 010 864.136	R = -1200 m
km 8.007 14	693 561.346	1 010 721.438	

POZNÁMKY:

- NEDÍLNOU SOUČÁSTÍ VÝKRESU JSOU POZNÁMKY A SPECIFIKACE UVEDENÉ NA VÝKRESE POZNÁMEK A TECHNICKÝCH SPECIFIKACÍ

PODÉLNÝ ŘEZ 1:150

OSO1 SO 101

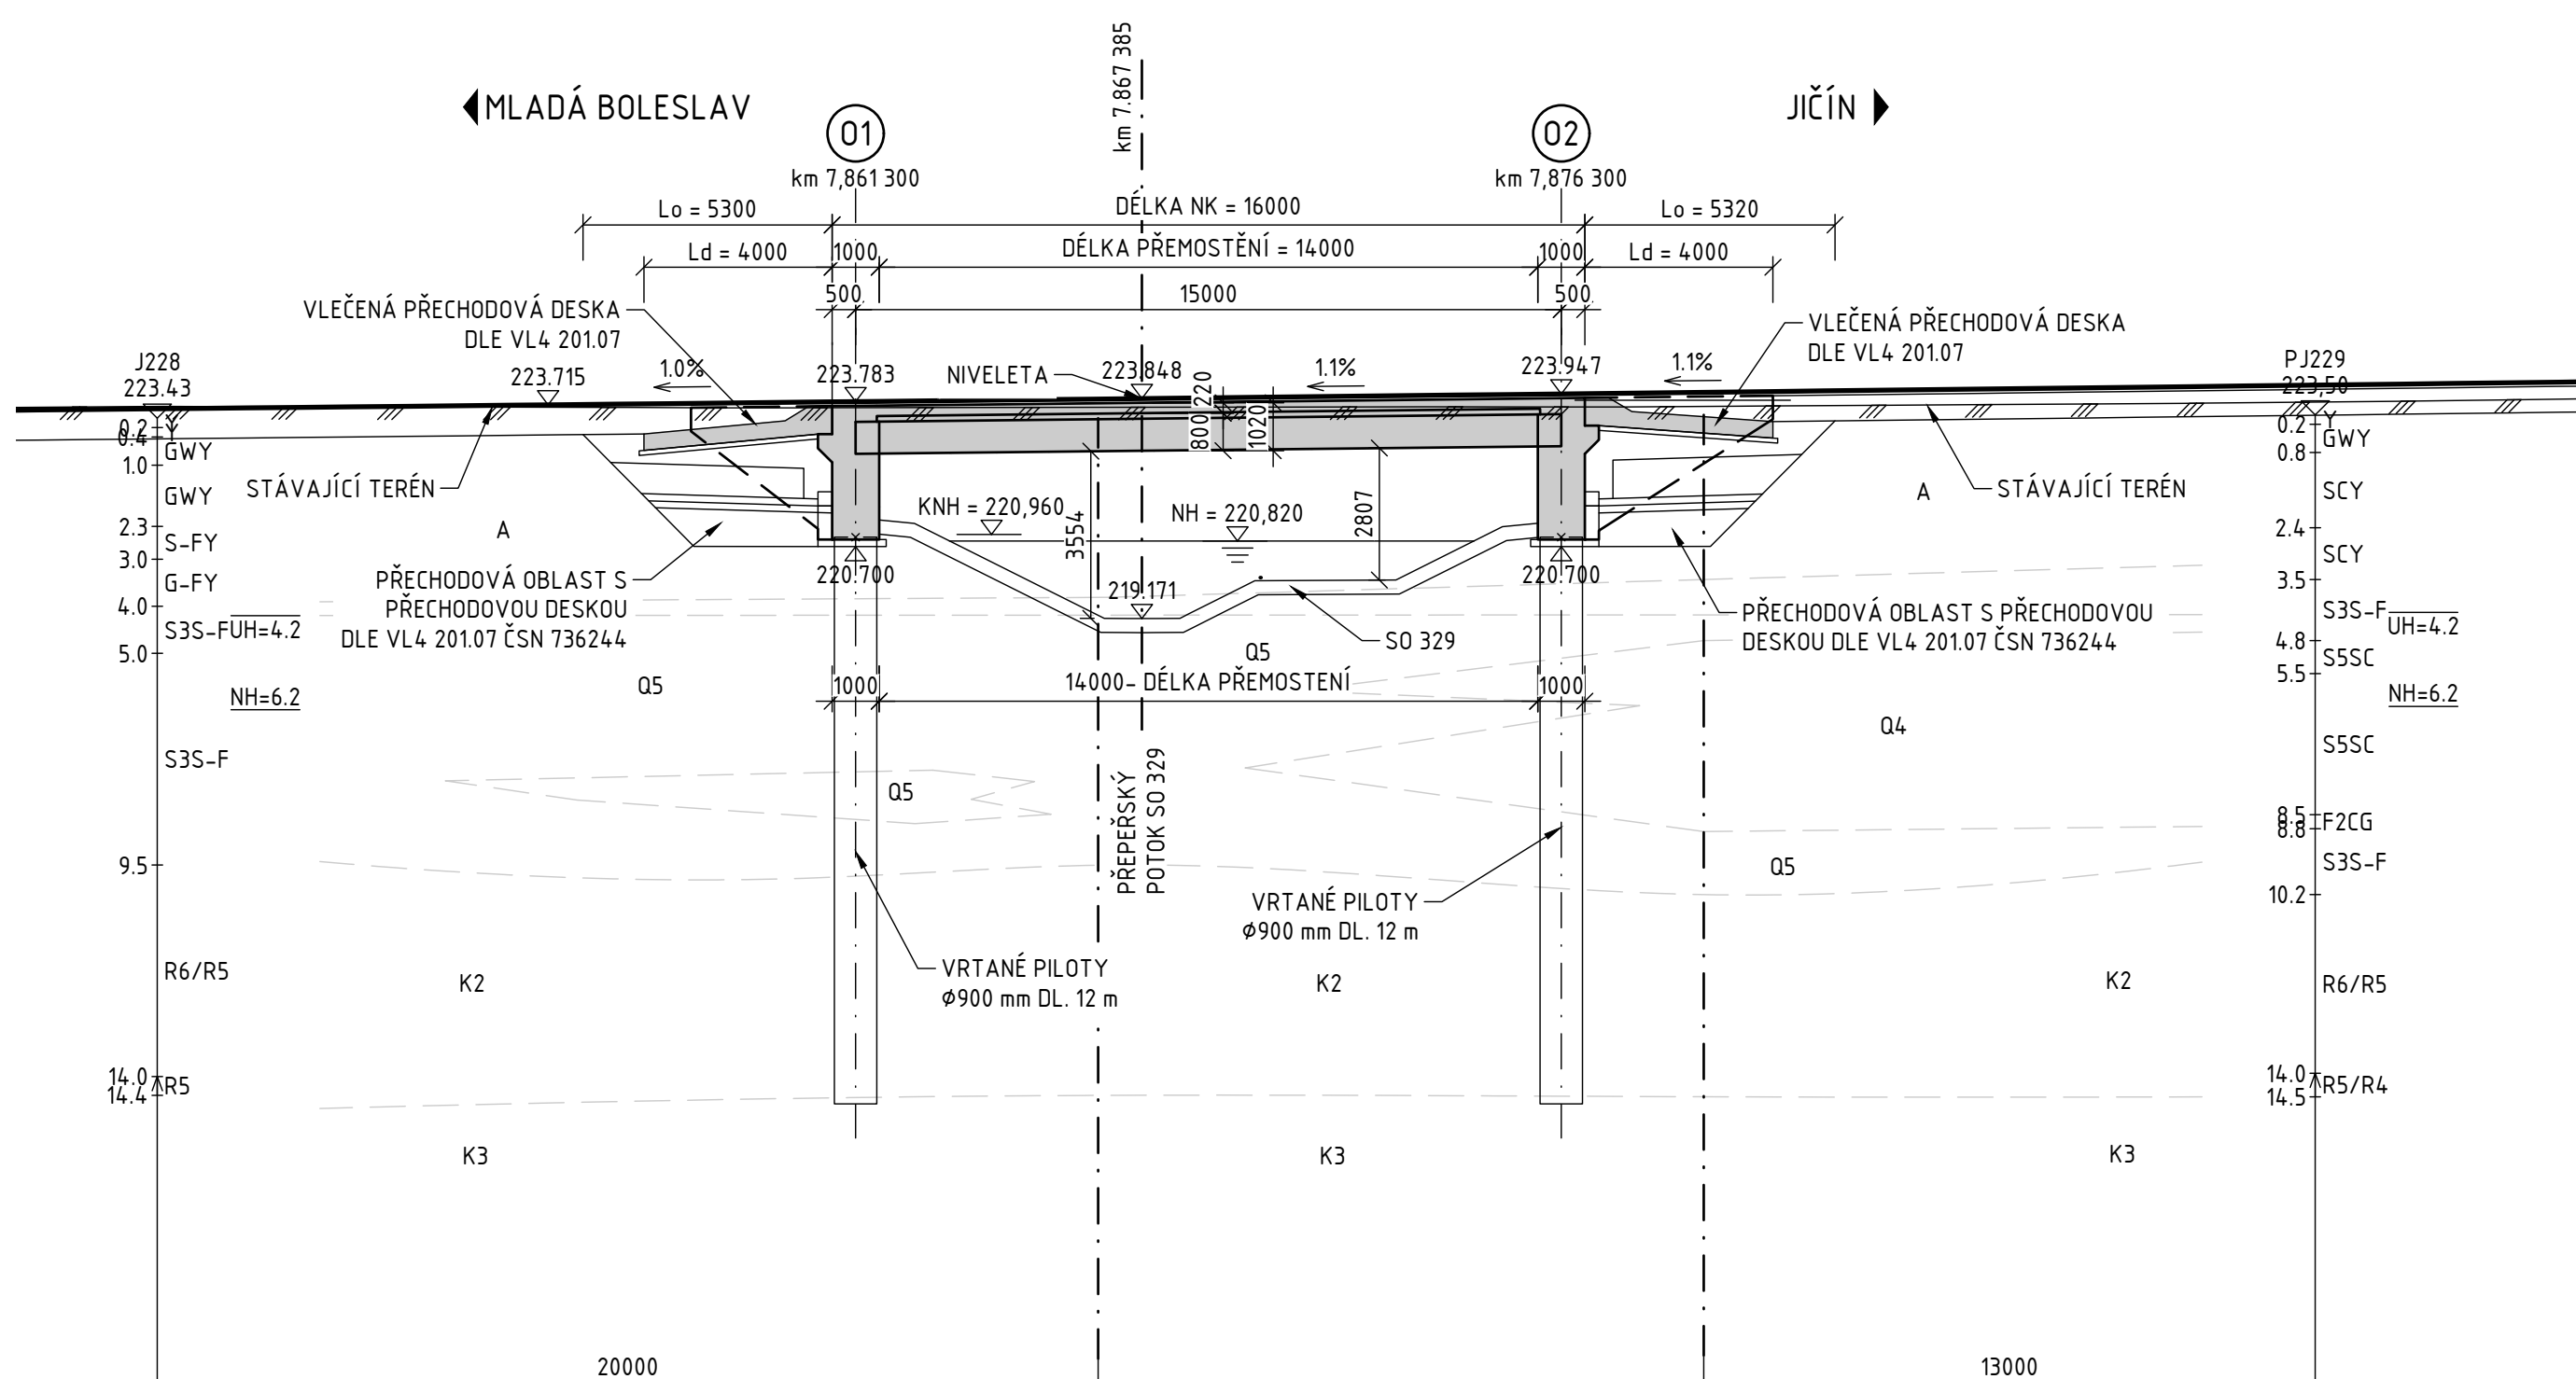

SOUVISEJÍCÍ OBJEKTY:

- SO 020 PRÍPRAVA ÚZEMÍ
- SO 101 SILNICE I/16 MLADÁ BOLESLAV - MARTINOVICE
- SO 153 PŘÍSTUPY NA POZEMKY V K.Ú. SUKORADY U MLADÉ BOLESLAVI
- SO 171 PROVIZORNÍ PŘELOŽKA I/16
- SO 190 DOPRAVNÍ ZNAČENÍ
- SO 301x ODVODNĚNÍ I/16
- SO 329 ÚPRAVA PŘEPĚŘSKÉHO POTOKA
- SO 432 PŘELOŽKA KABELOVÉHO VEDENÍ NN KM 7,845
- SO 801 VEGETAČNÍ ÚPRAVY
- SO 810 KÁČENÍ ZELENĚ
- SO 830 REKULTIVACE PLOCH DOČASNEHO ZÁBORU
- SO 860 OPLOCENÍ

Souřadnicový systém: S-JTSK
Výškový systém: Bpv

SO 207 MOST NA I/16 PŘES PŘEPĚŘSKÝ POTOK V KM 7,870



Ředitelství silnic a dálnic s. p.
Čerčanská 2023/12, Krč, 140 00 Praha 4



Valbek, spol. s r.o.
Vaňurova 505/17
460 07 Liberec 3



Zhotovitel:
Valbek, spol. s r.o.
Vaňurova 505/17
460 07 Liberec 3

Příloha
PŮDORYS, PODÉLNÝ ŘEZ,
VZOROVÝ PŘÍČNÝ ŘEZ

102