



PŮDORYS 1:100

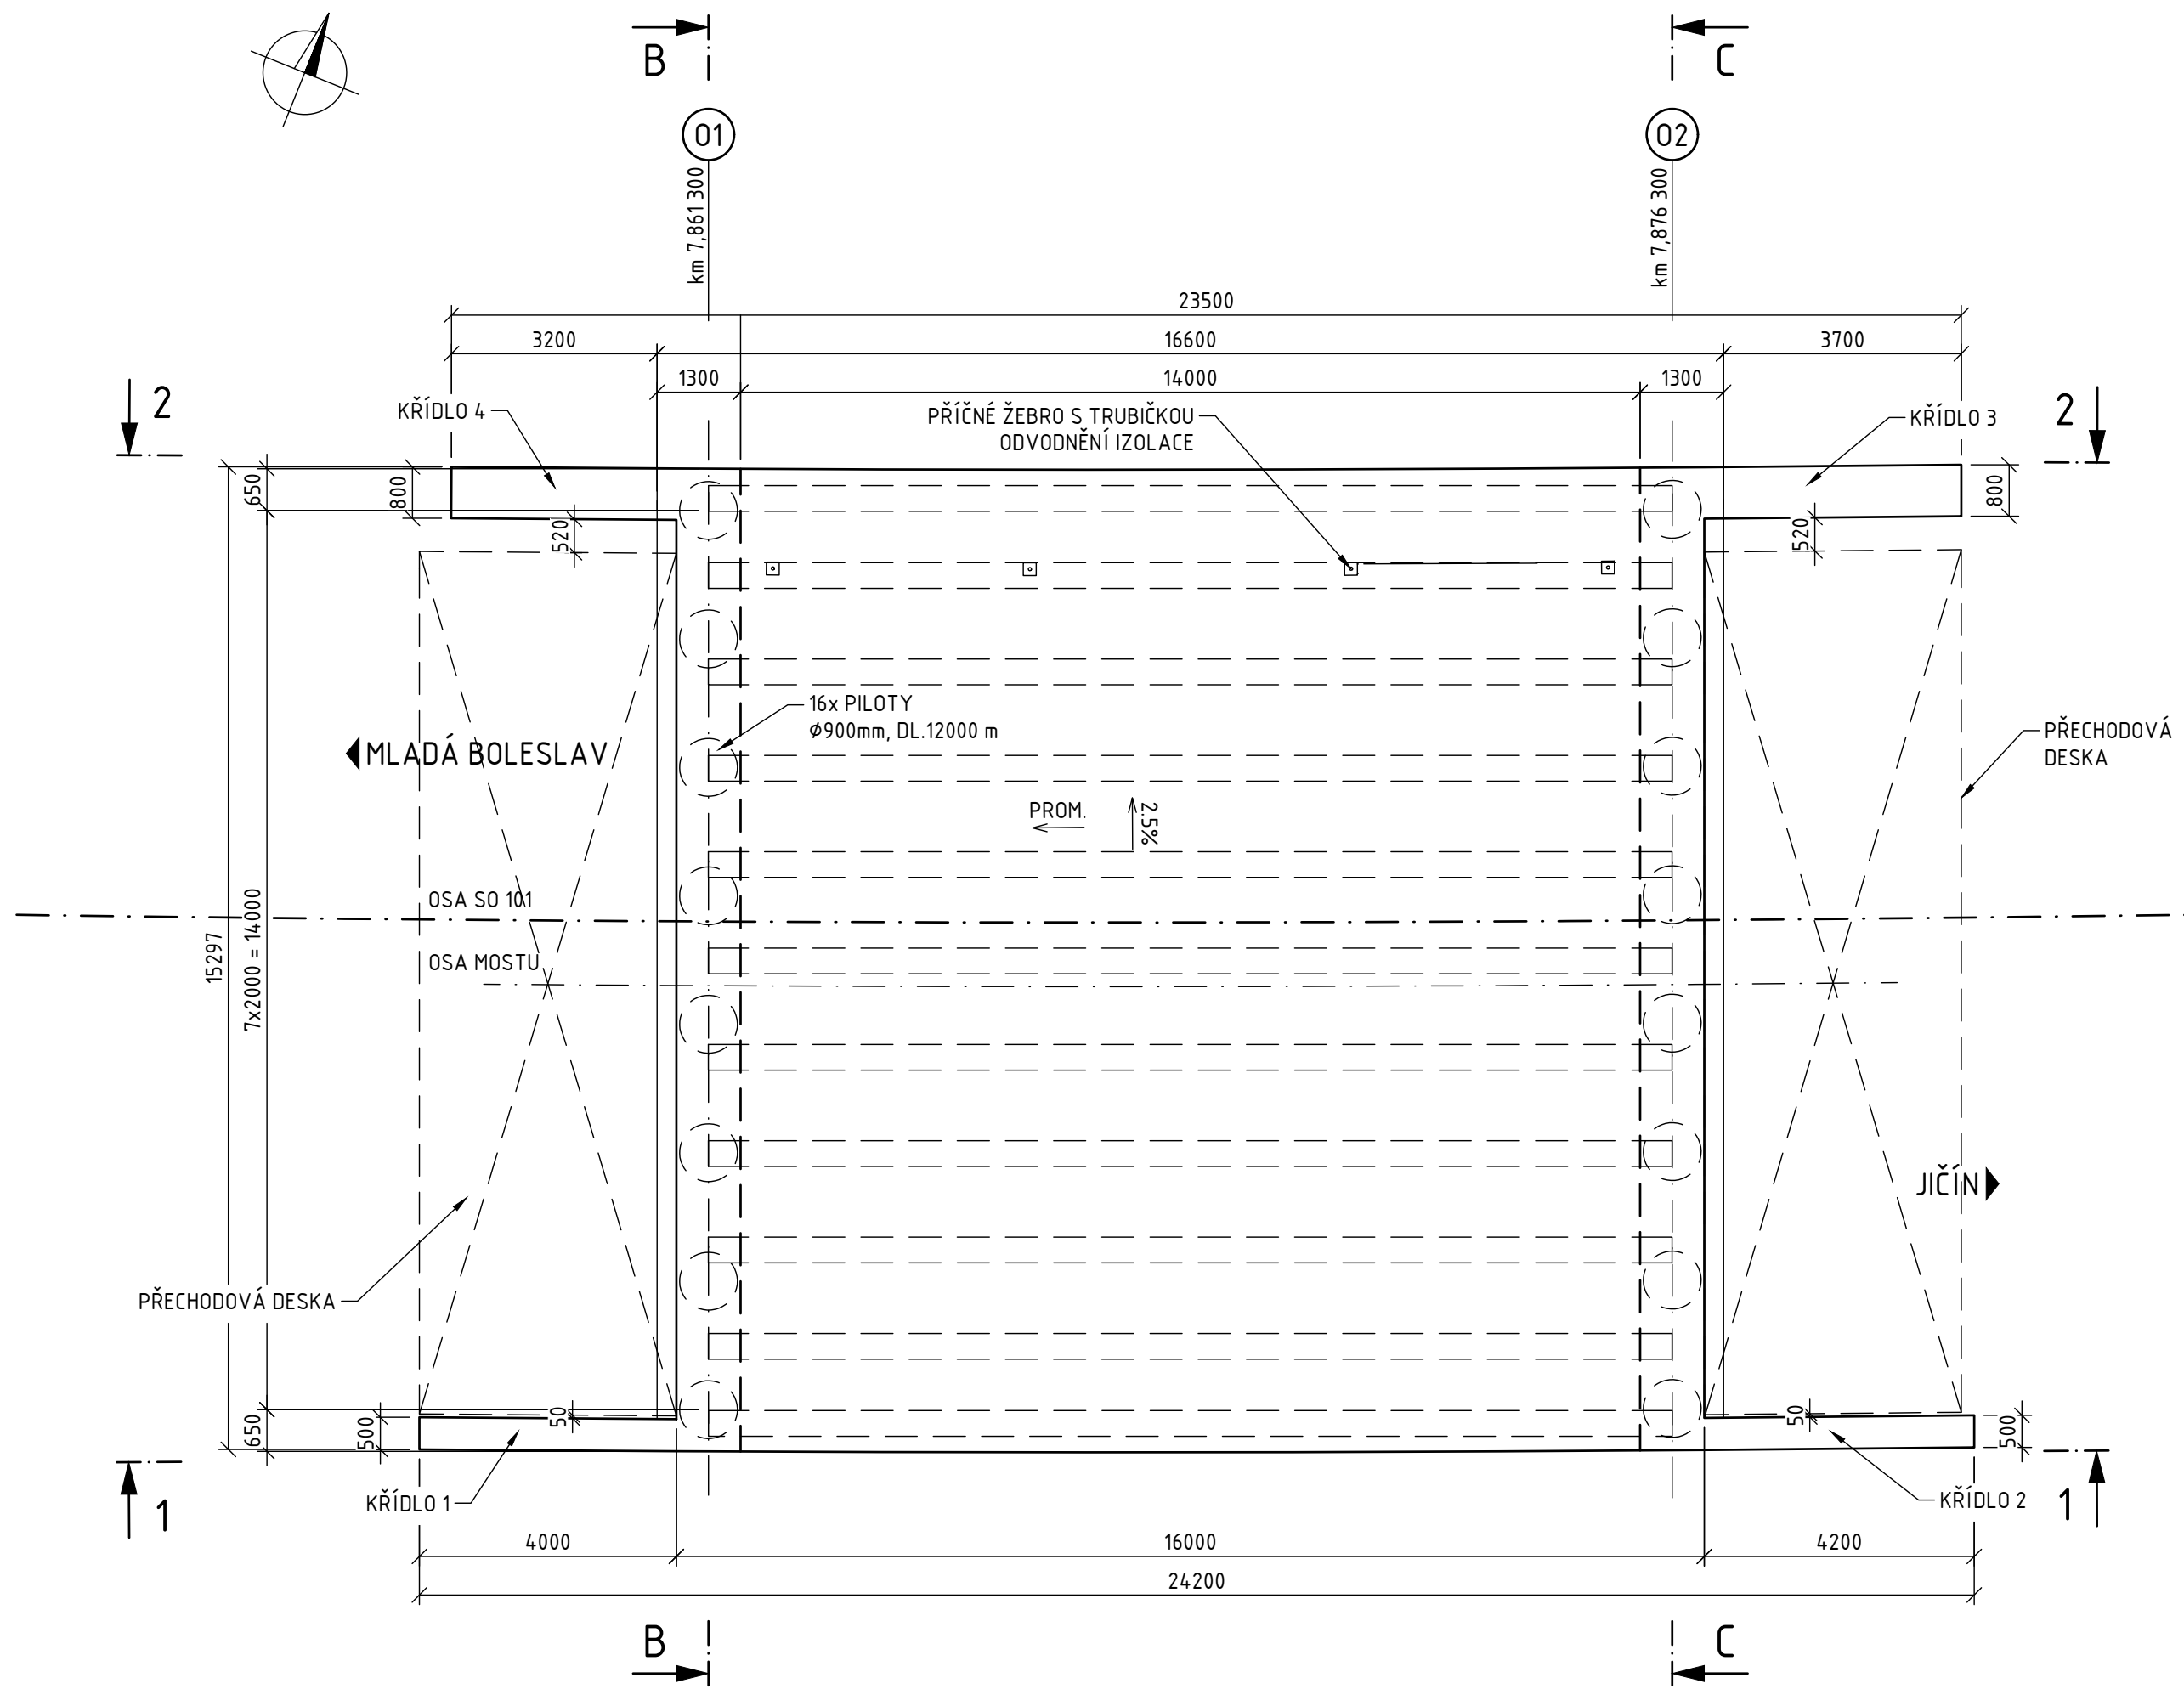


PODÉLNÝ ŘEZ 1:100

OSOU SO 101

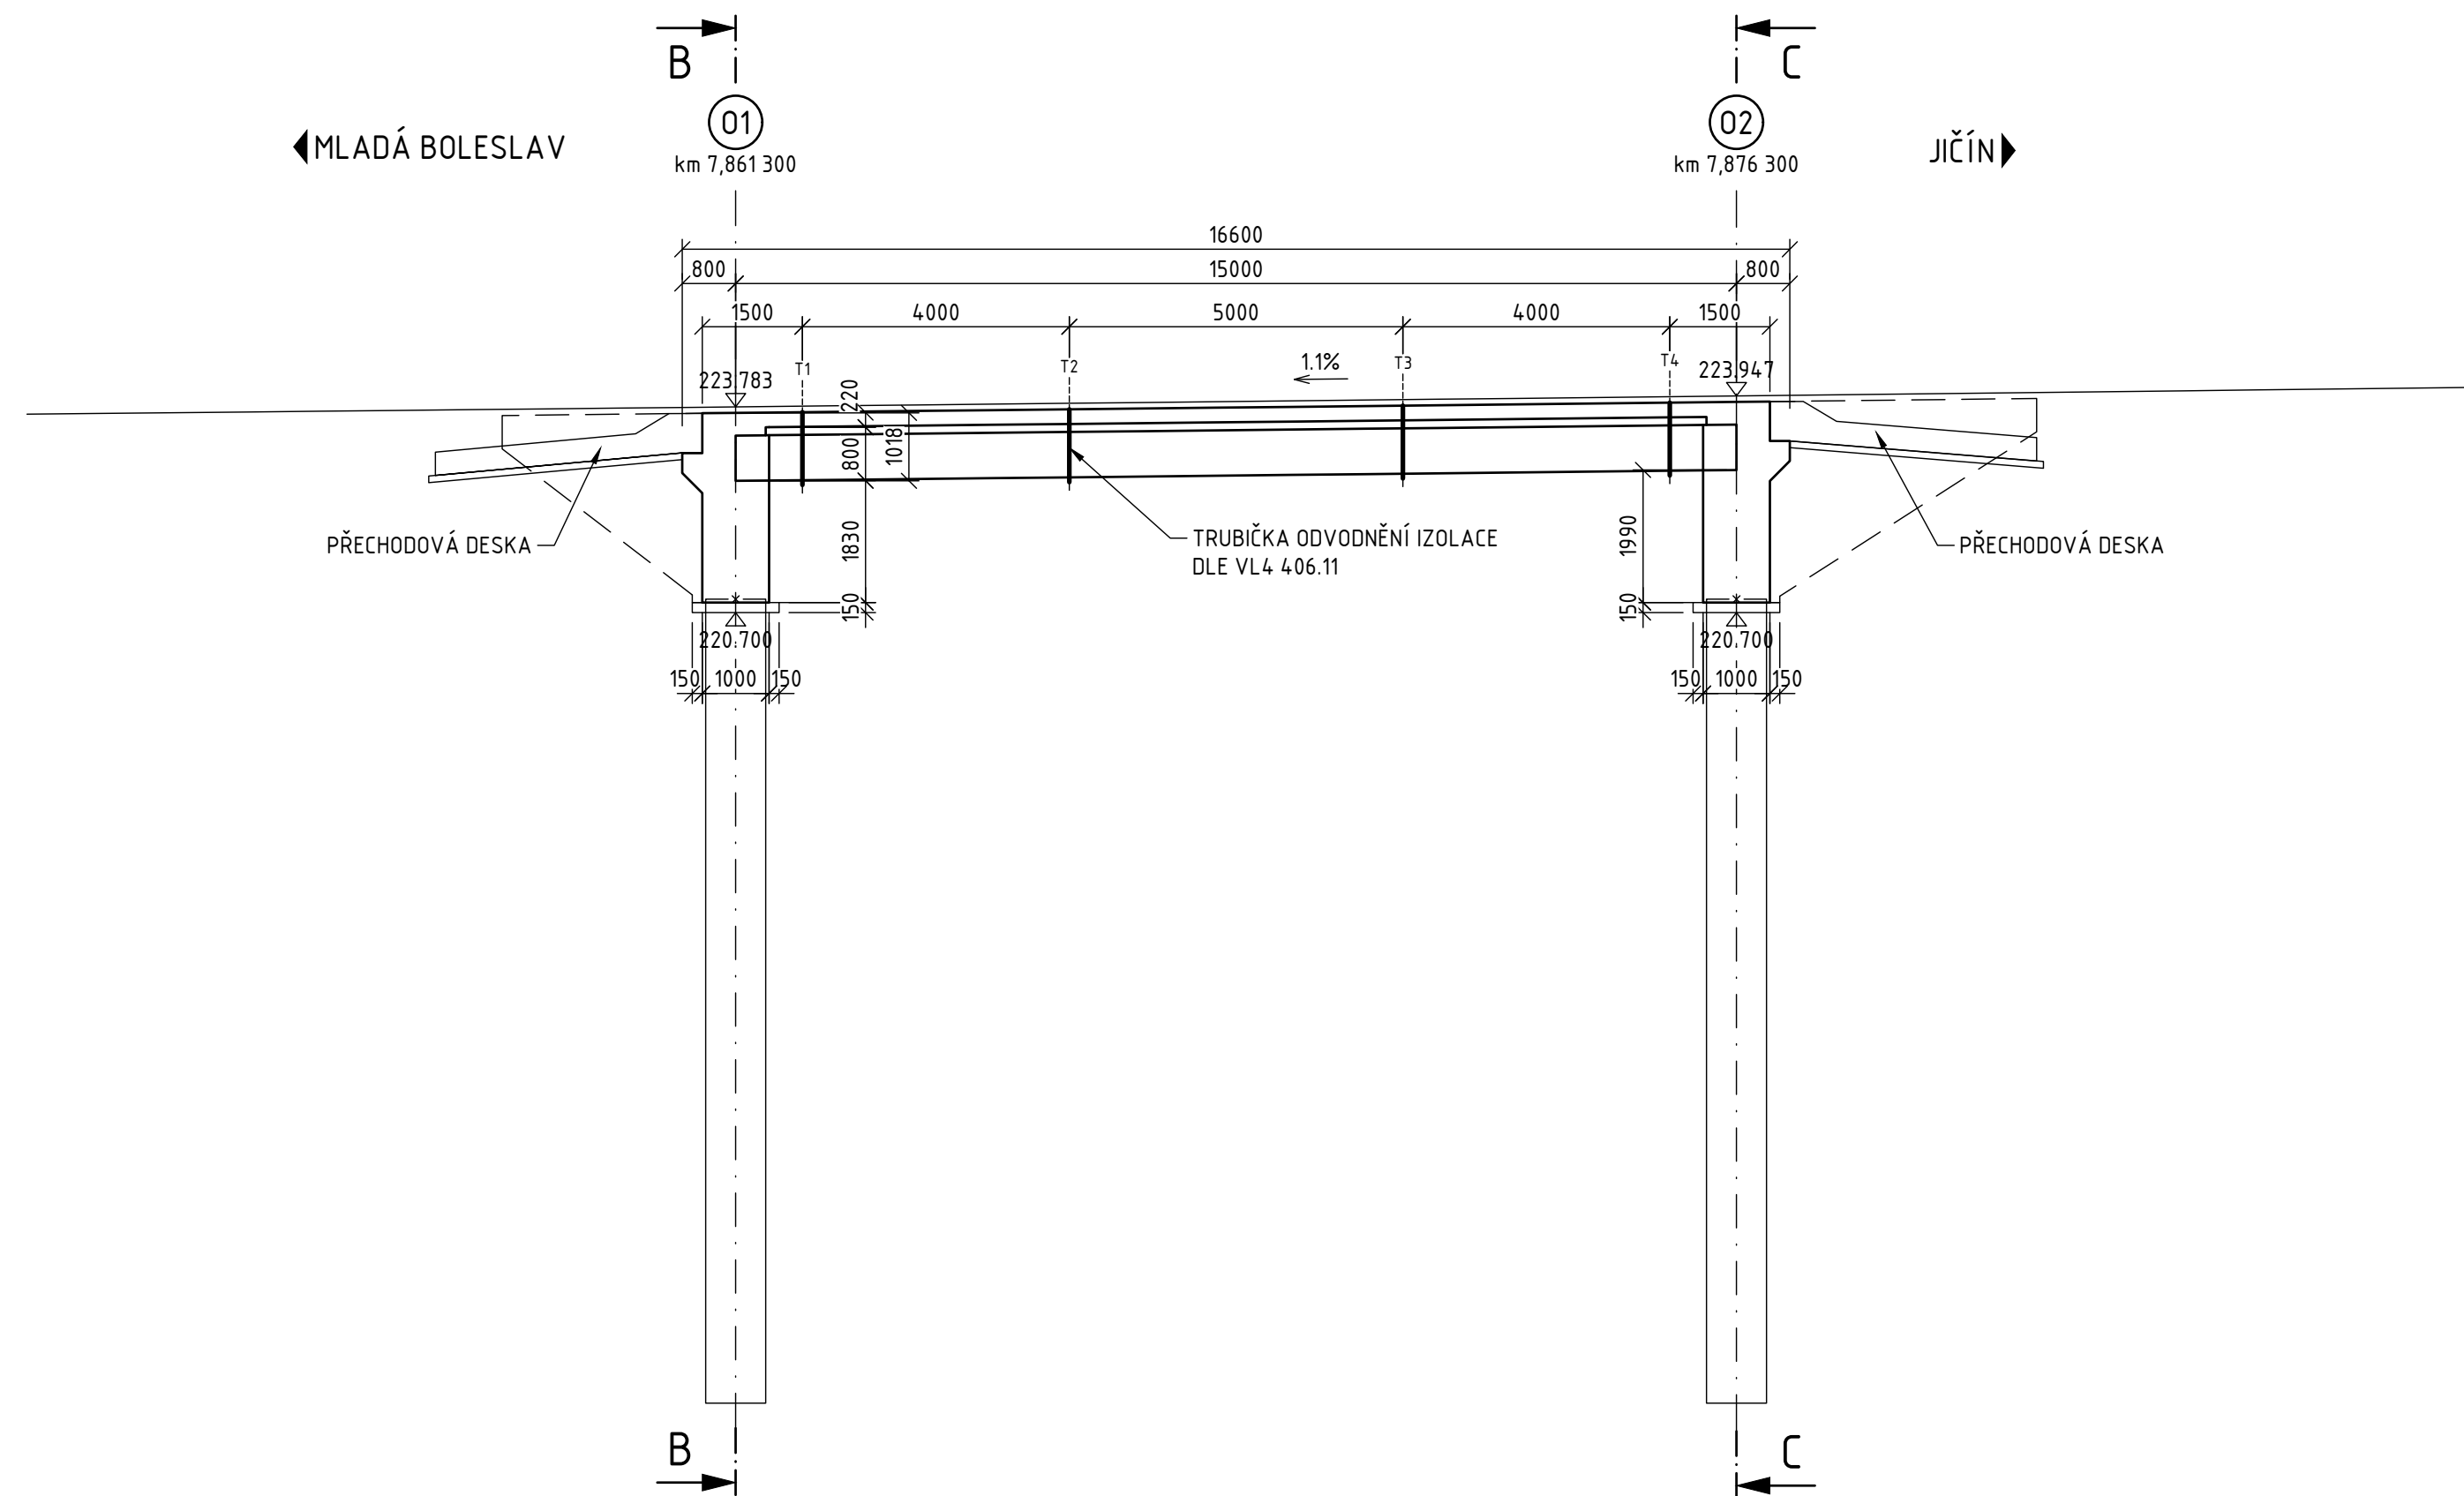


VZOROVÝ PŘÍČNÝ ŘEZ 1:50

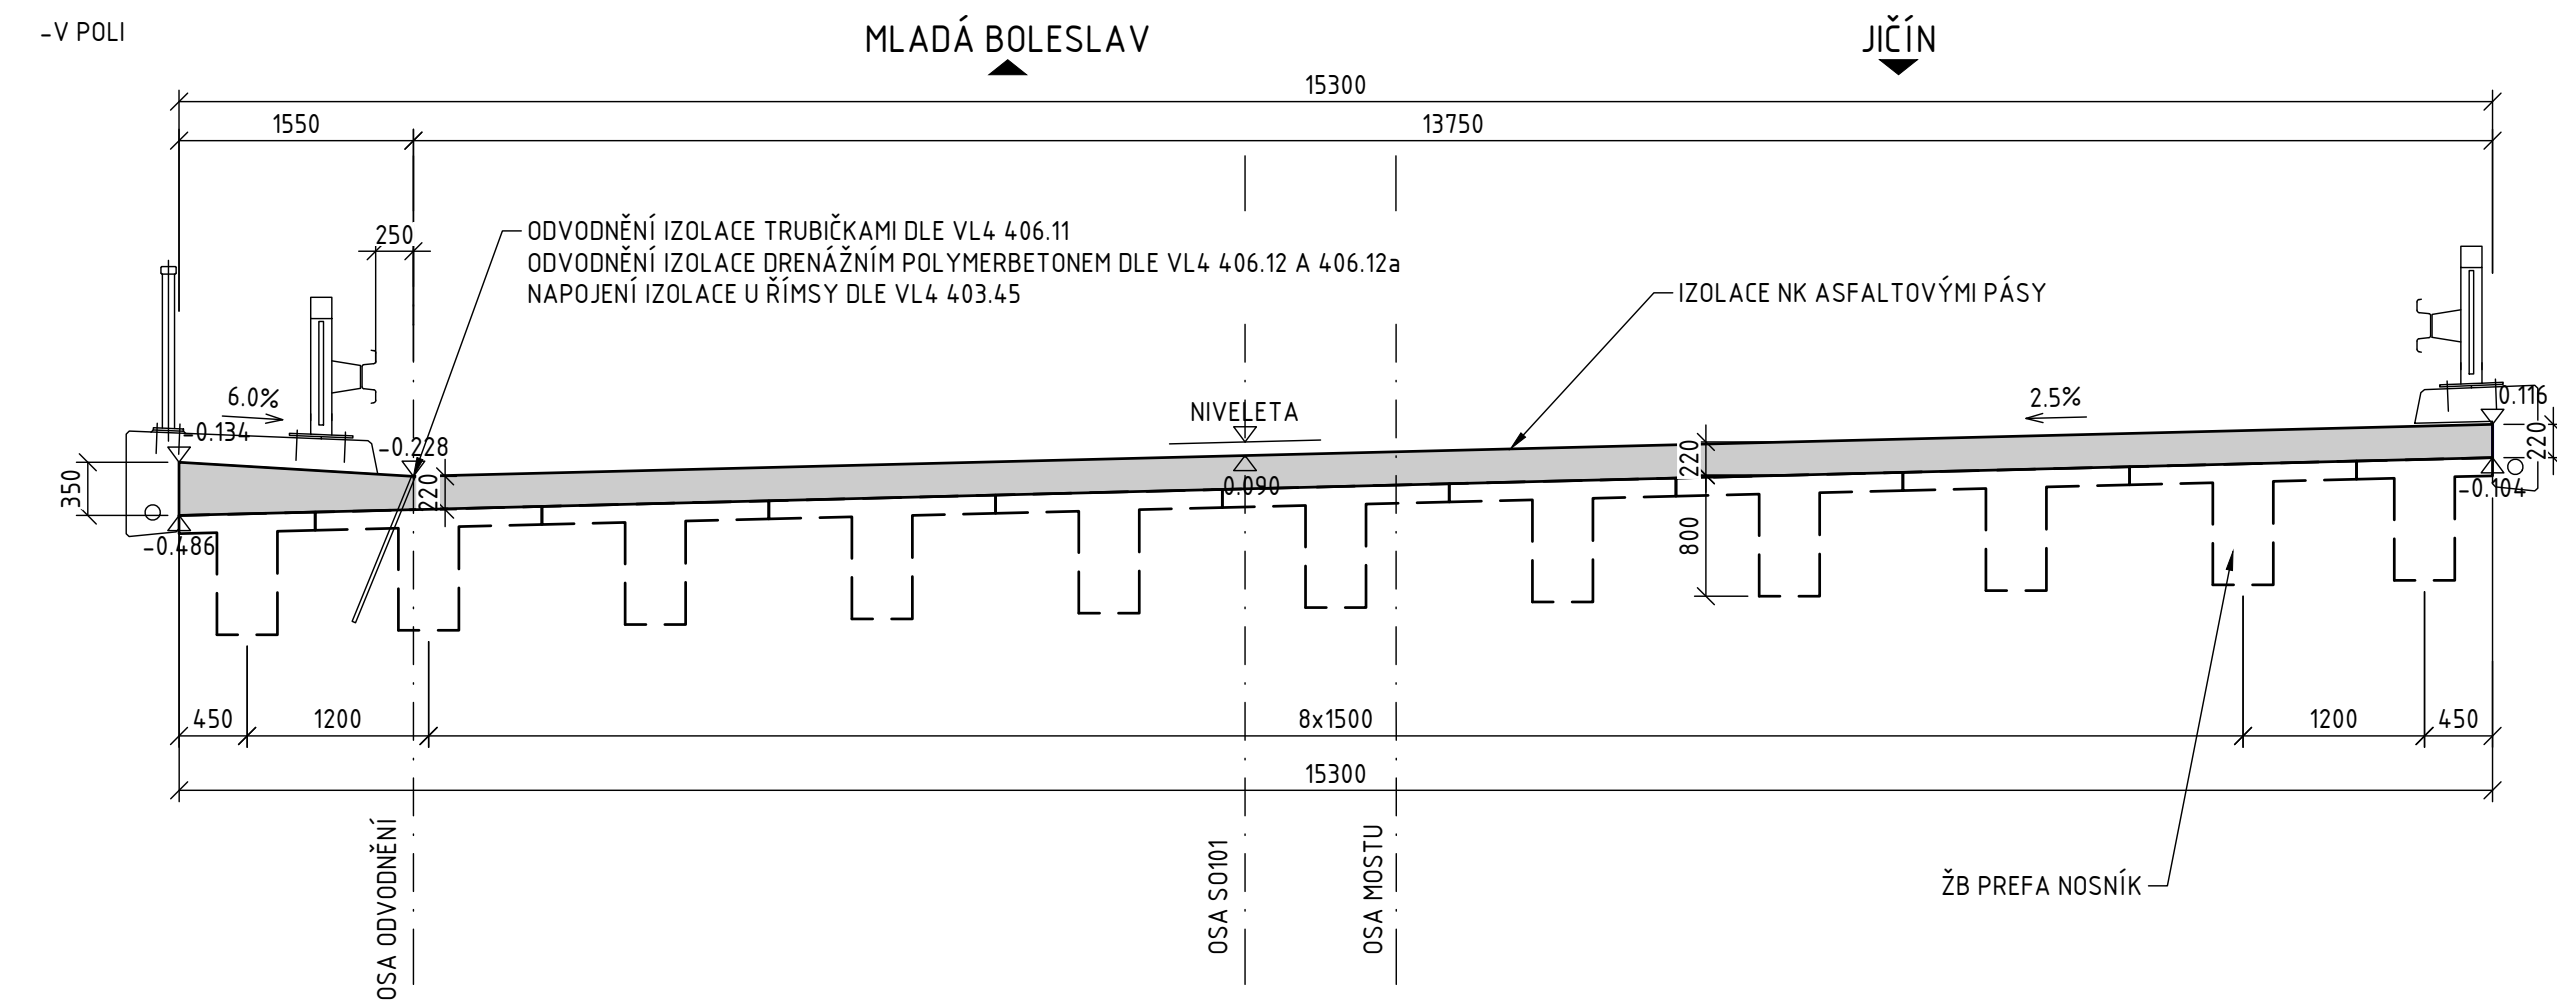

PODÉLNÝ ŘEZ PŘECHODOVOU DESKOU 1:50

VYKRESLENA PŘECHODOVÁ DESKA OPĚRY 02, PŘECHODOVÁ DESKA OPĚRY 01 ŘEŠENA OBDOBĚ

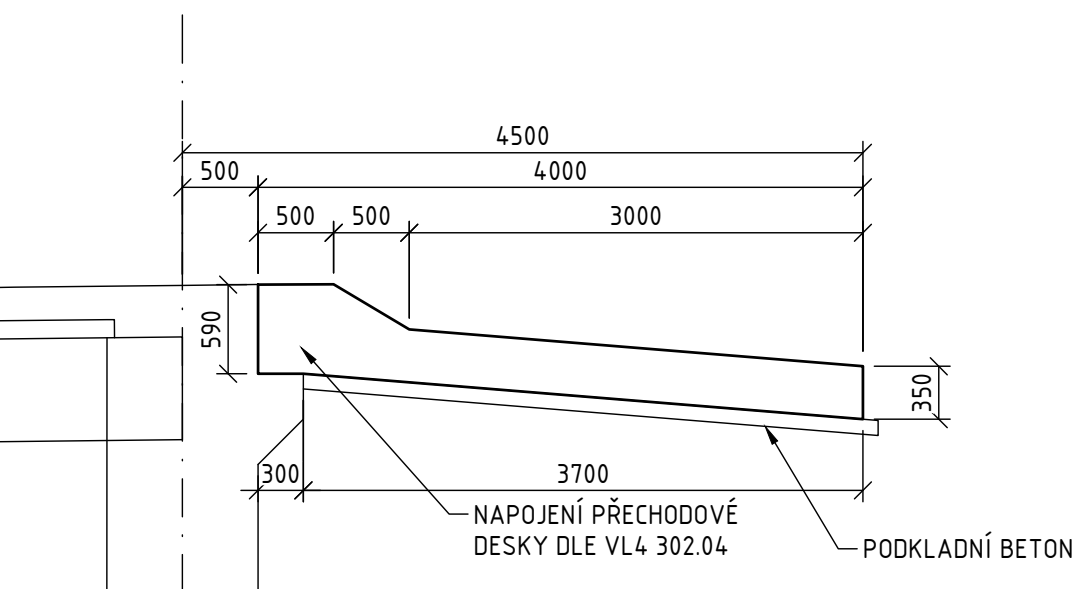

POZNÁMKY:

- NEDÍLNOU SOUČÁSTÍ VÝKRESU JSOU POZNÁMKY A SPECIFIKACE UVEDENÉ NA VÝKRESE POZNÁMEK A TECHNICKÝCH SPECIFIKACÍ

Souřadnicový systém: S-JTSK
Výškový systém: Bpv

SO 207 MOST NA I/16 PŘES PŘEPEŘSKÝ POTOK V KM 7,870



Ředitelství silnic a dálnic s. p.
Čerčanská 2023/12, Krč, 140 00 Praha 4



Valbek, spol. s r.o.
Vaňurova 505/17
460 07 Liberec 3



I/16 MLADÁ BOLESLAV - MARTINOVICE

201

