




ŘEZ B-B 1:100

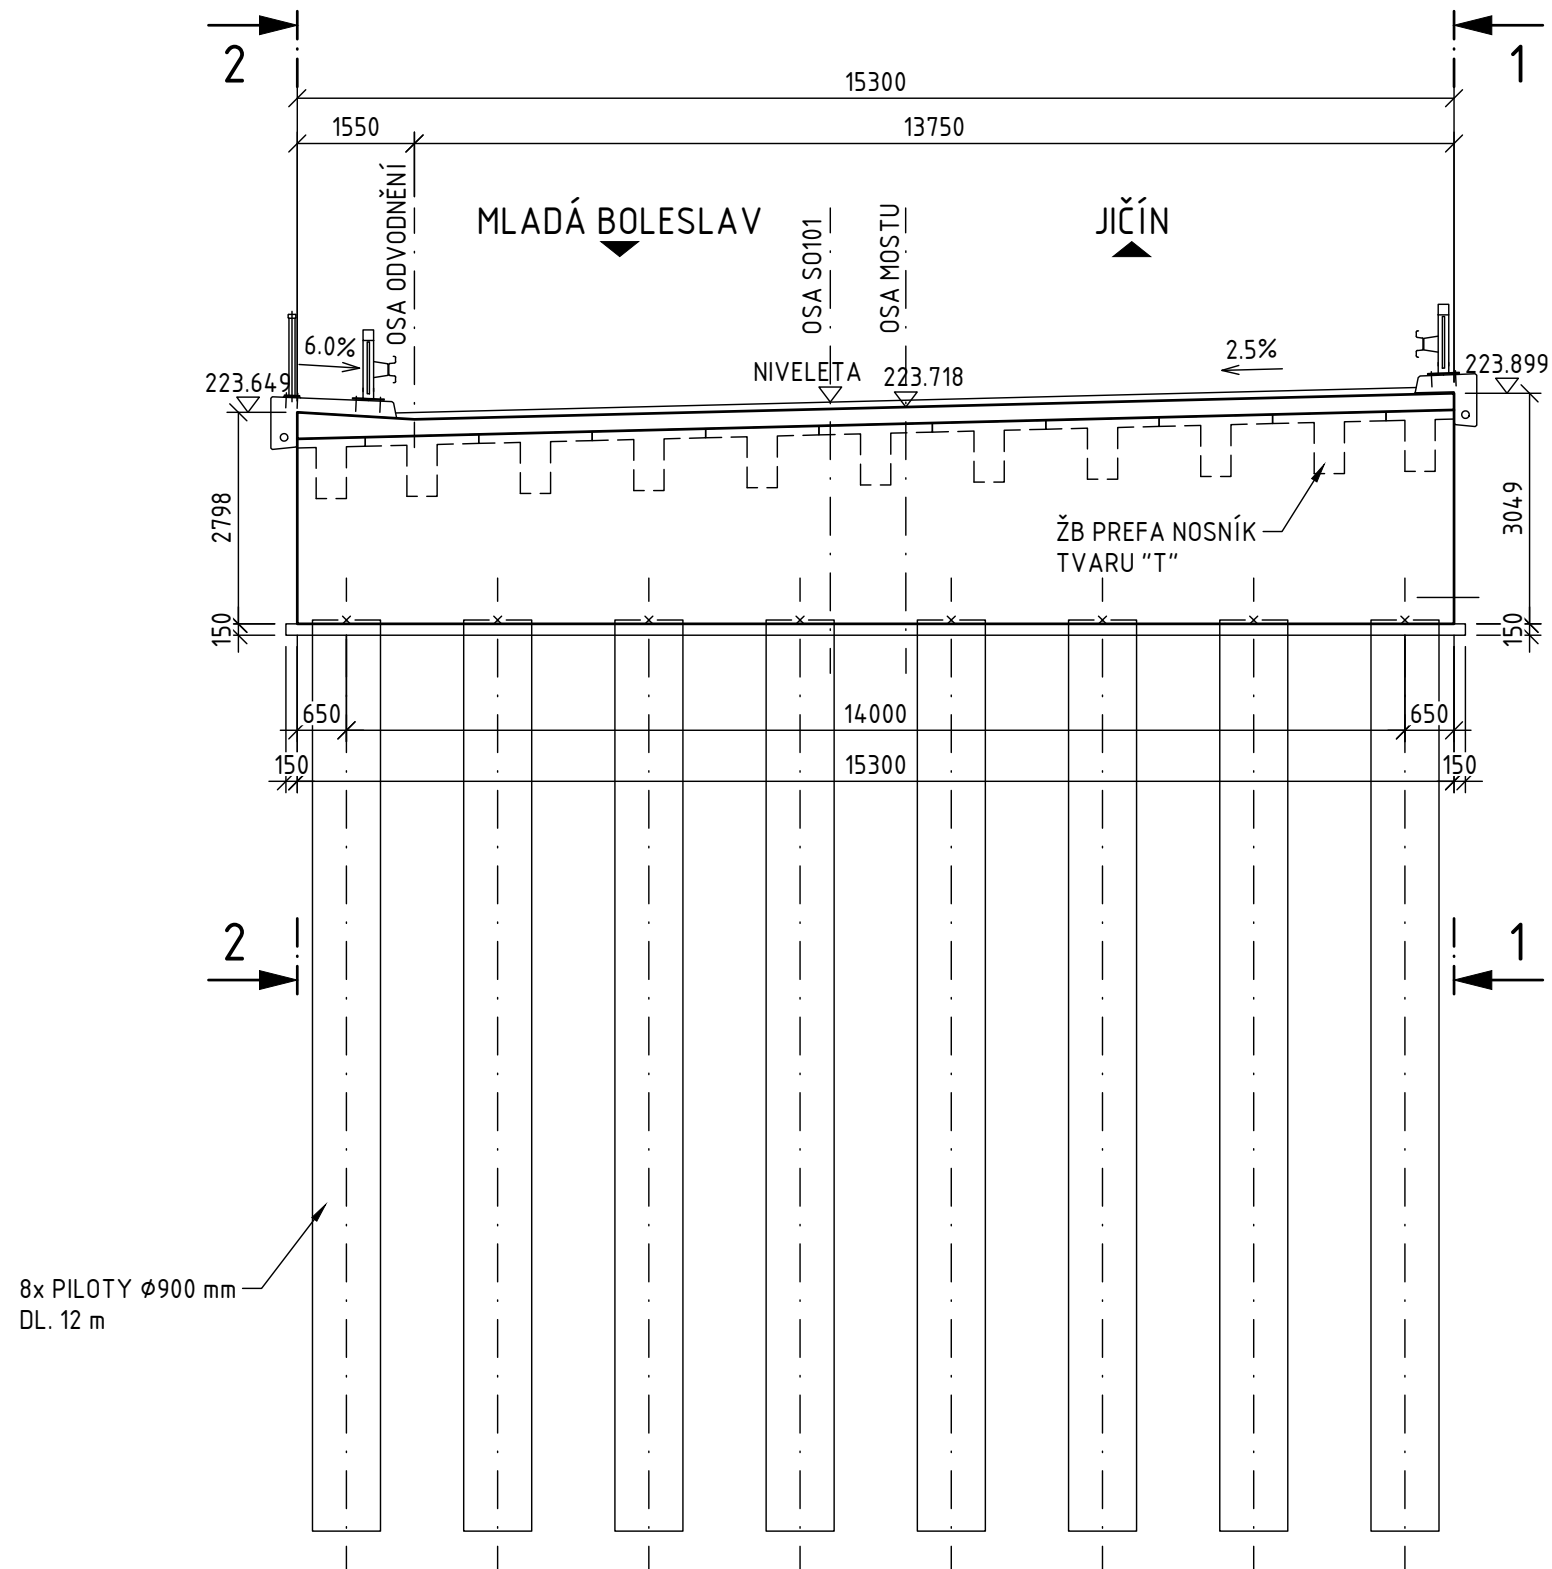


ŘEZ C-C 1:100

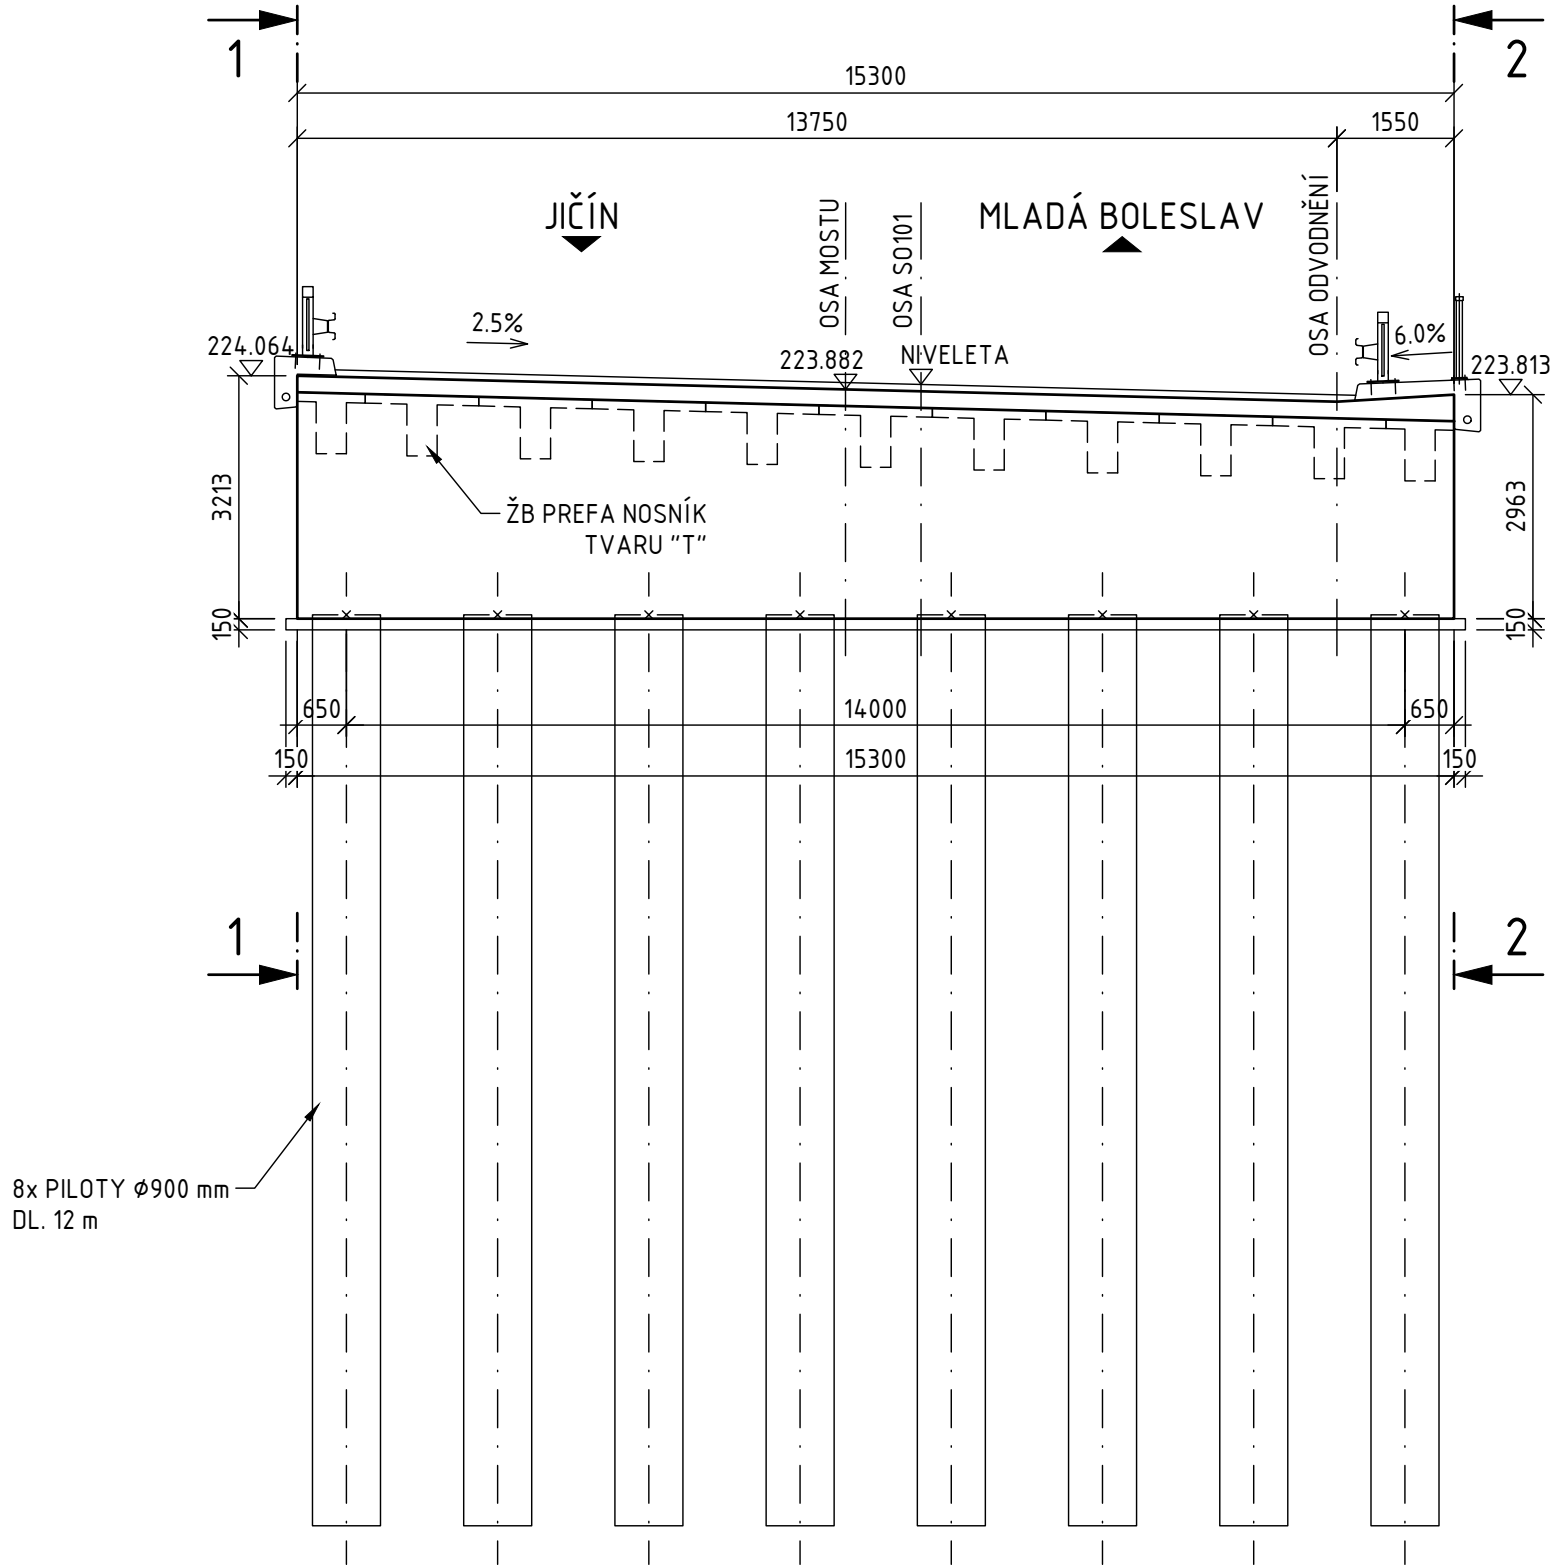


POHLED 1 1:100

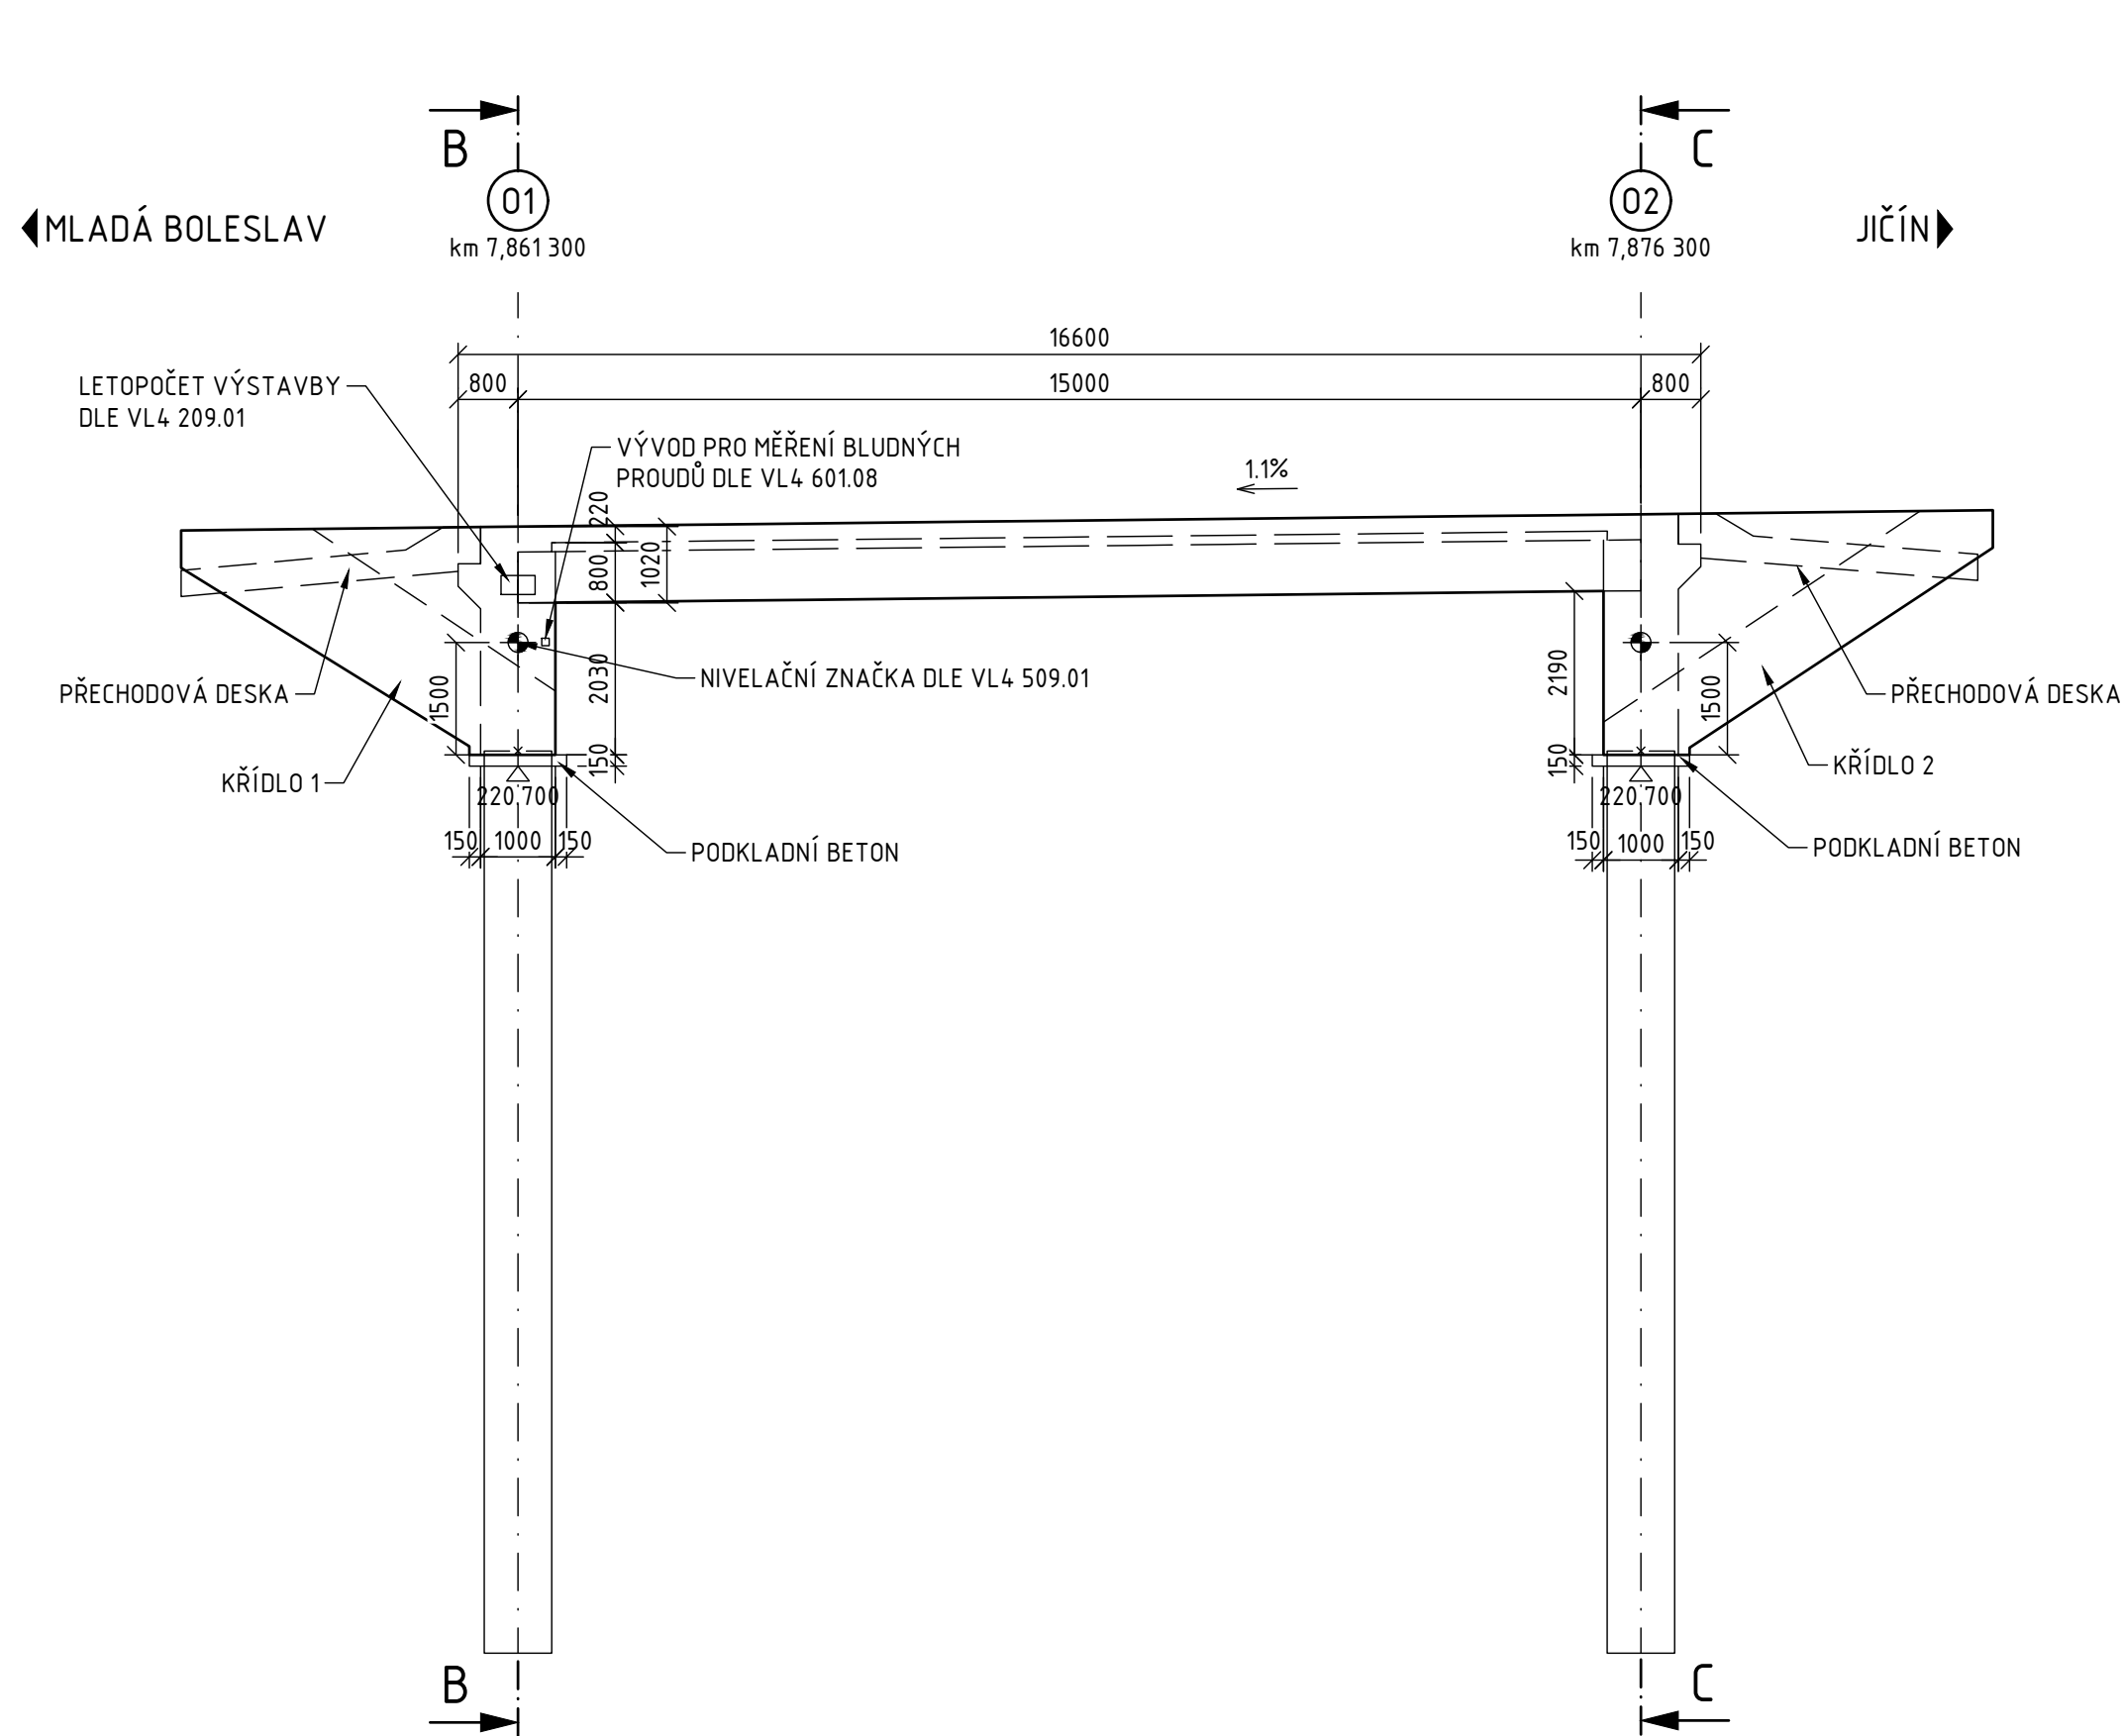


POHLED 2 1:100

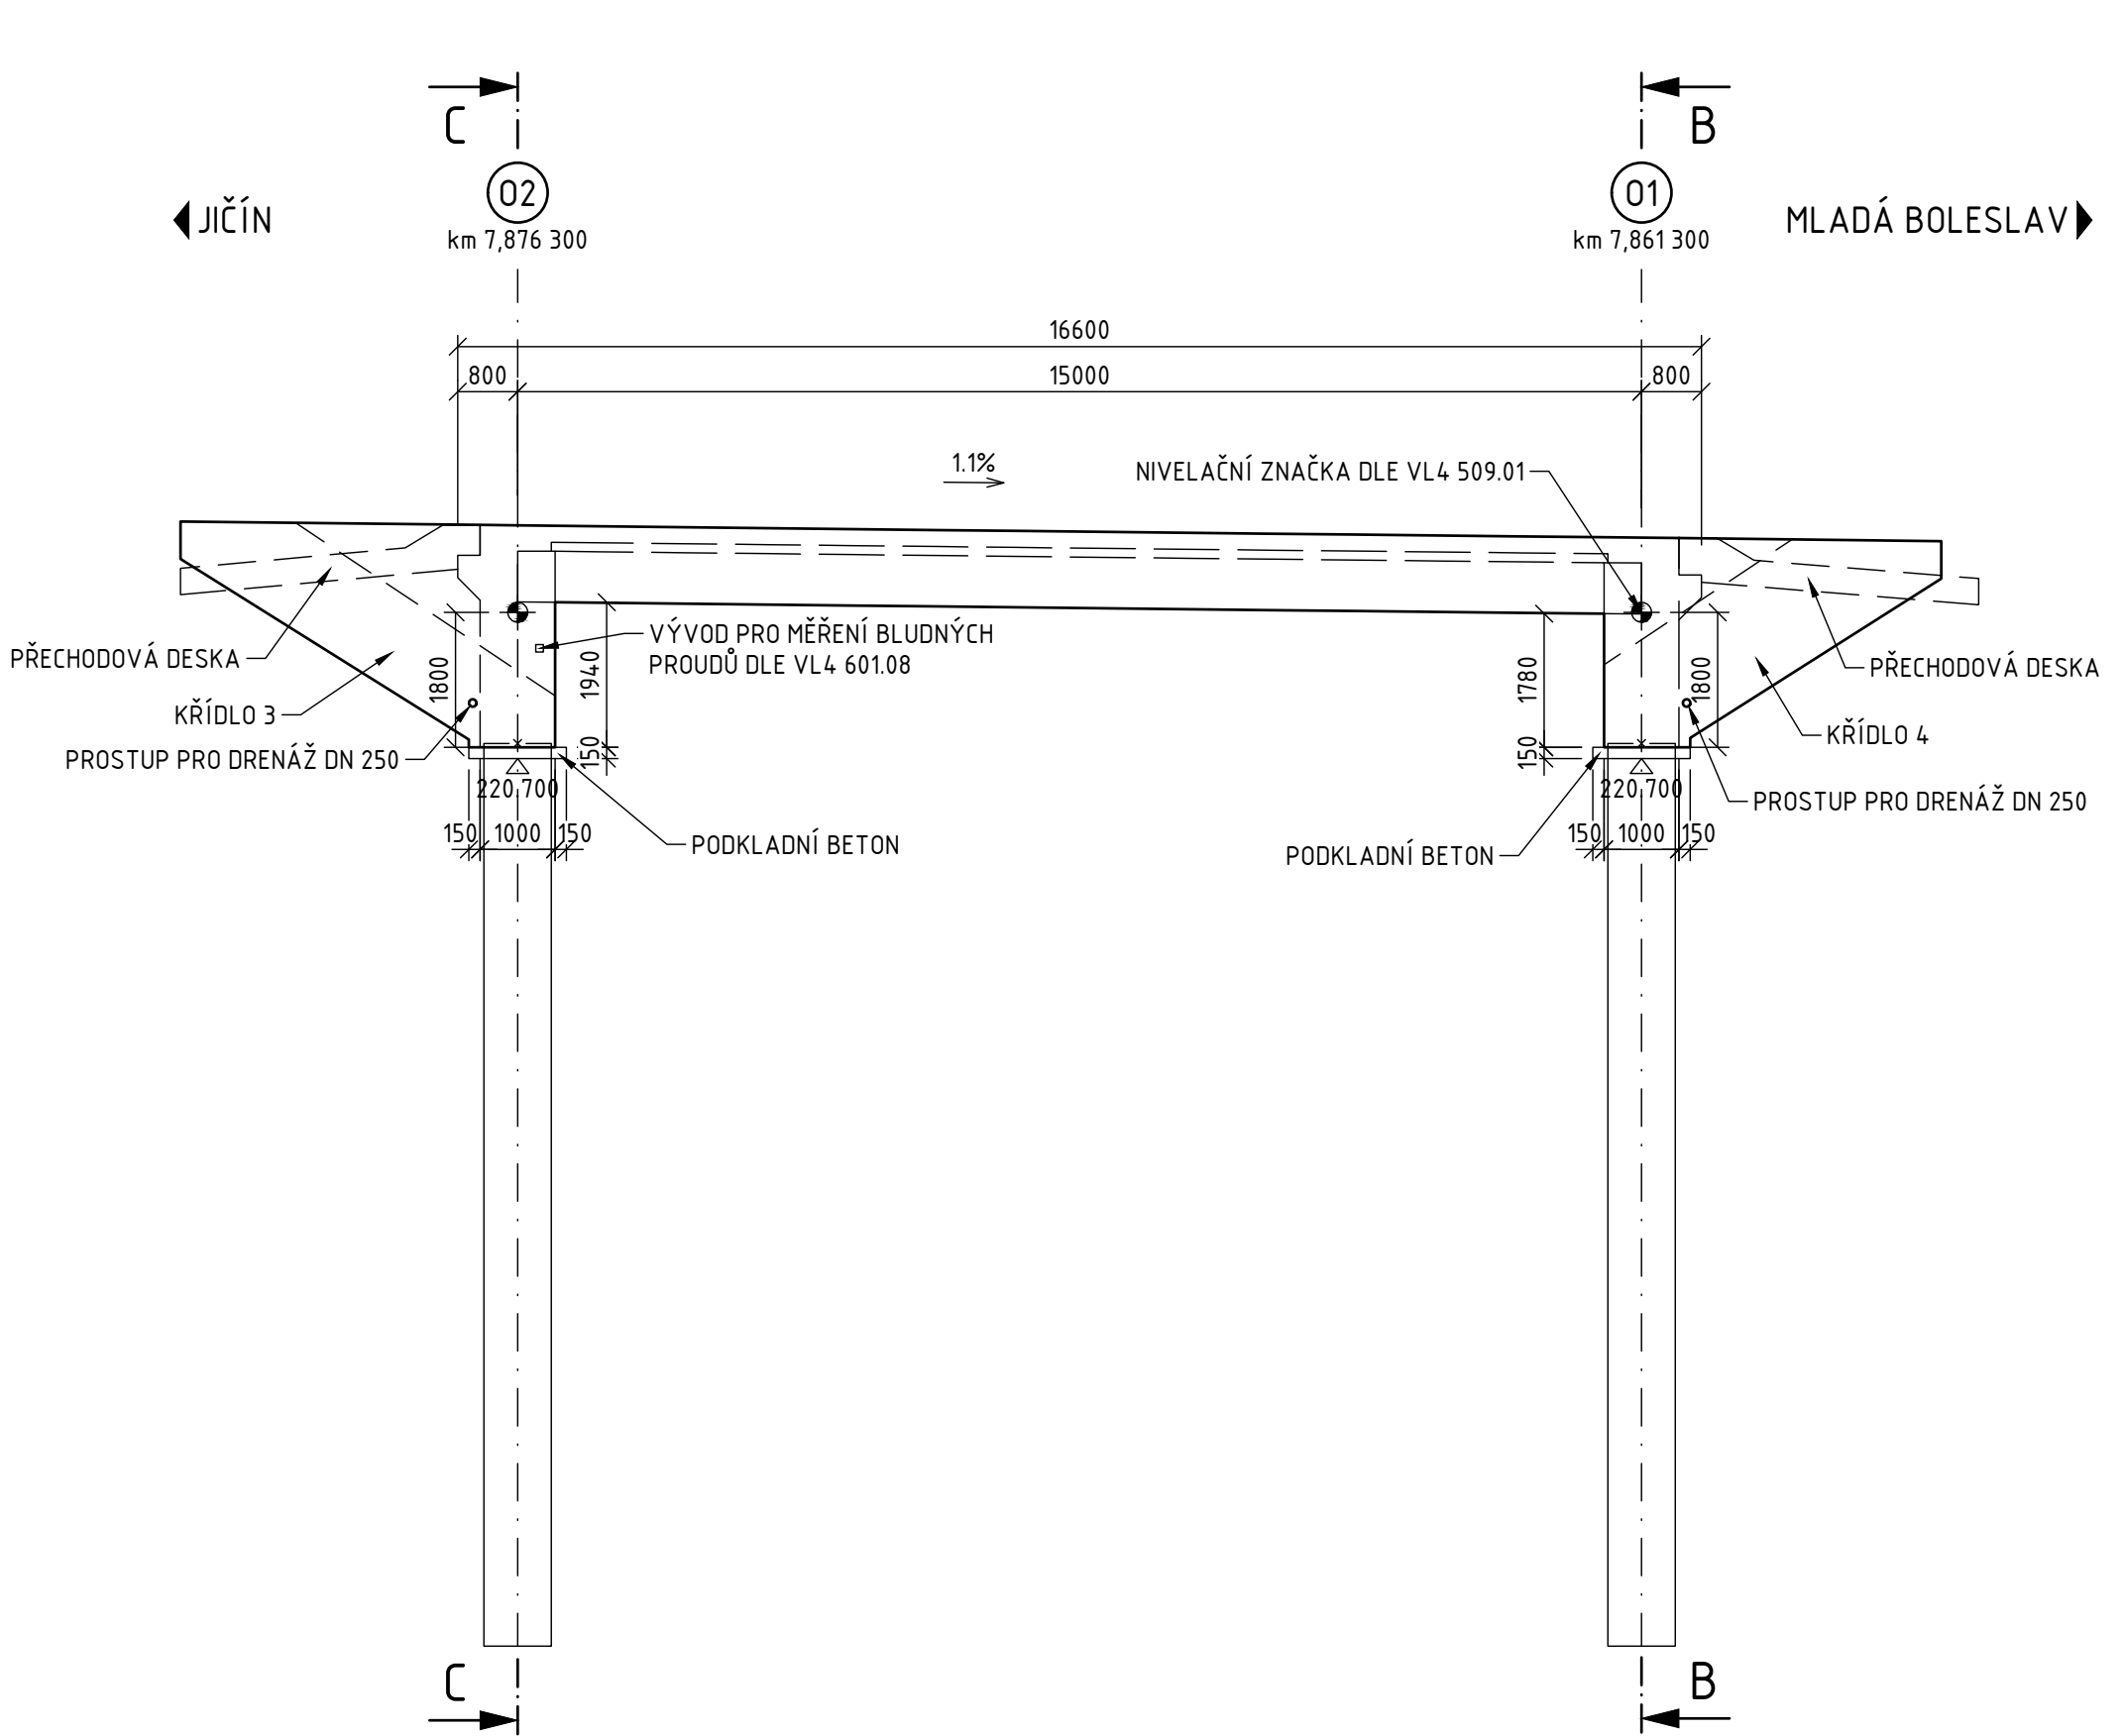

ŘEZ KŘÍDLEM 1, 2
1:50

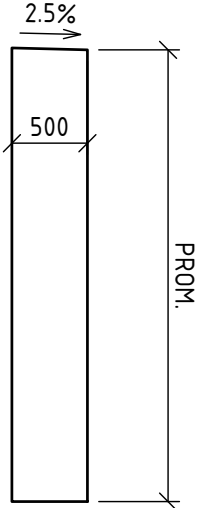

ŘEZ KŘÍDLEM 3, 4
1:50

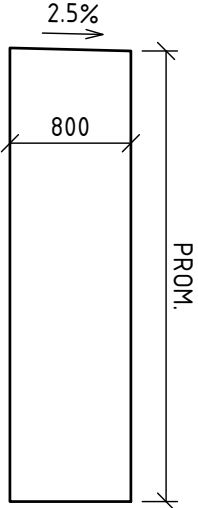

POZNÁMKY:

- NEDÍLNOU SOUČÁSTÍ VÝKRESU JSOU POZNÁMKY A SPECIFIKACE UVEDENÉ NA VÝKRESE
POZNÁMEK A TECHNICKÝCH SPECIFIKACÍ

Souřadnicový systém: S-JTSK
Výškový systém: Bpv

SO 207 MOST NA I/16 PŘES PŘEPEŘSKÝ POTOK V KM 7,870

Objednatel:



Ředitelství silnic a dálnic s. p.
Čerčanská 2023/12, Krč, 140 00 Praha 4



Valbek, spol. s r.o.
Vaňurova 505/17
460 07 Liberec 3



Vypracoval	A. MICHALIKOVÁ	Zak. číslo	21-L113-001	
Zodp. projektant	ING. O. BAKHMET	Datum	02/2025	
Tech. kontrola	ING. I. BELDA	Stupeň	PDPS	
Akce	I/16 MLADÁ BOLES LAV - MARTINOVICE		Počet formátů	8x A4
			Měřítko	1:100,50
			Č. přílohy	Paré
Příloha			202	
TVAR NOSNÉ KONSTRUKCE 2(2)				

MĚŘÍTKO 1:50 0 0.5 1 1.5 2 2.5 3 3.5 4 4.5 5m

MĚŘÍTKO 1:100 1 0 1 2 3 4 5 6 7 8 9 10m