

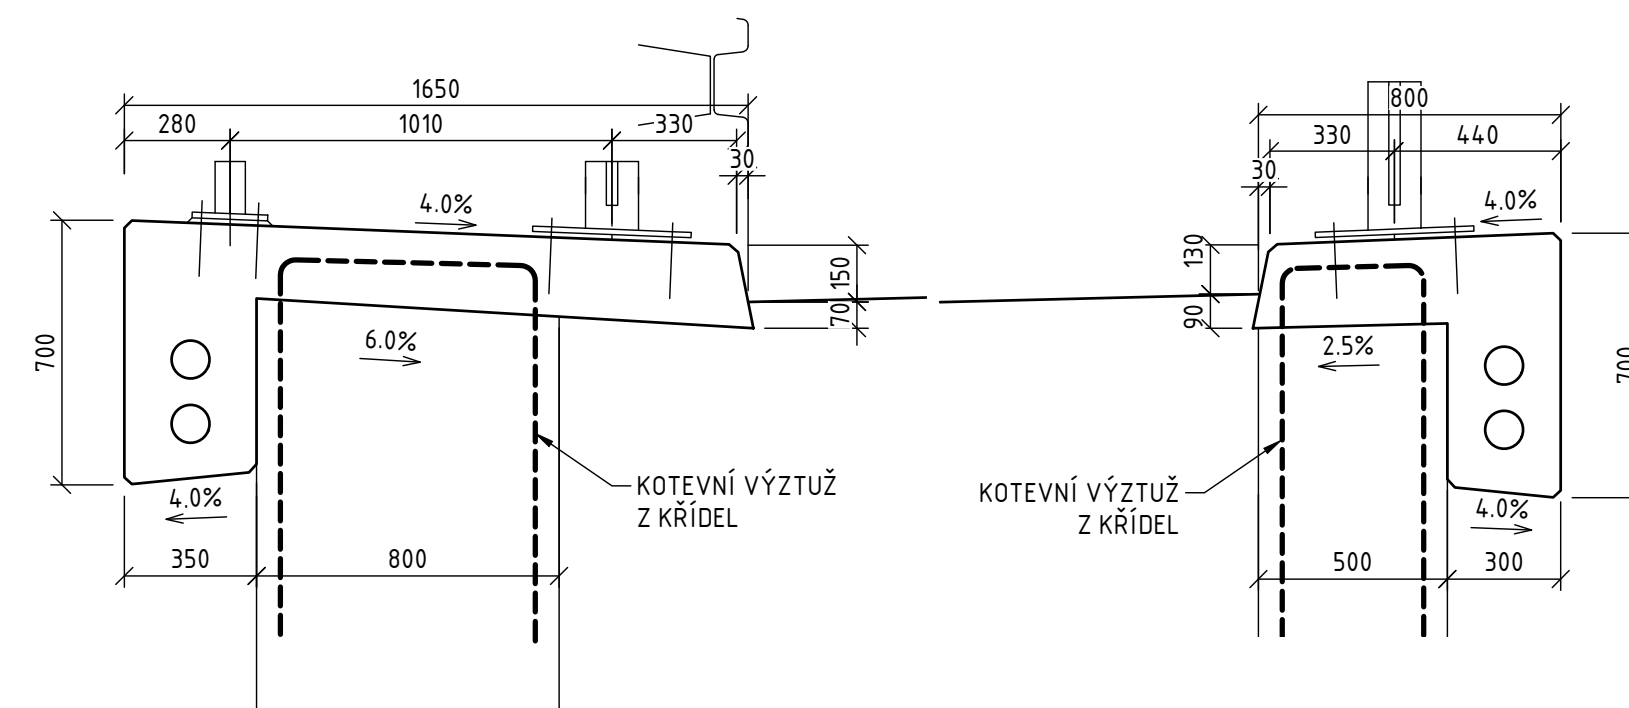




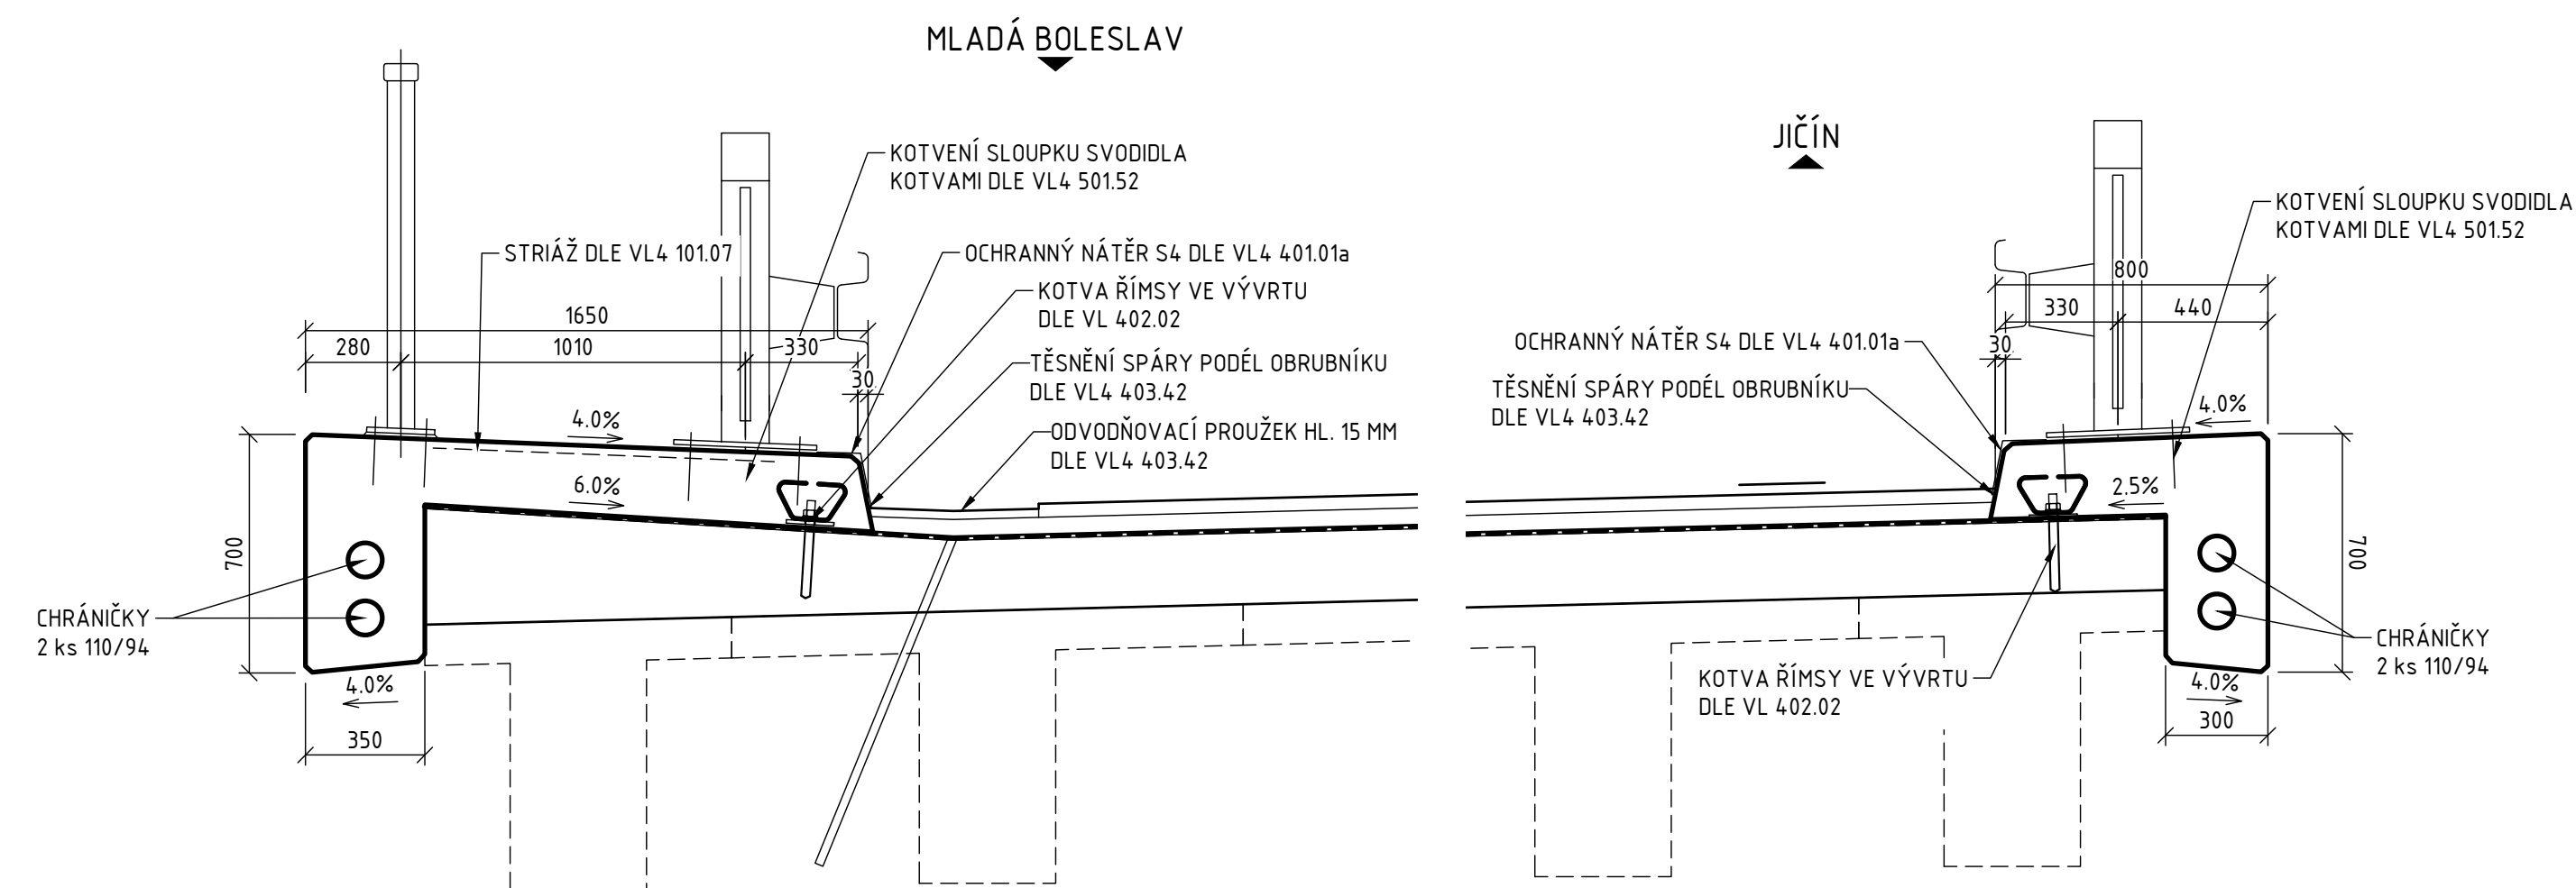


OSA SO 101

OSA MOSTU

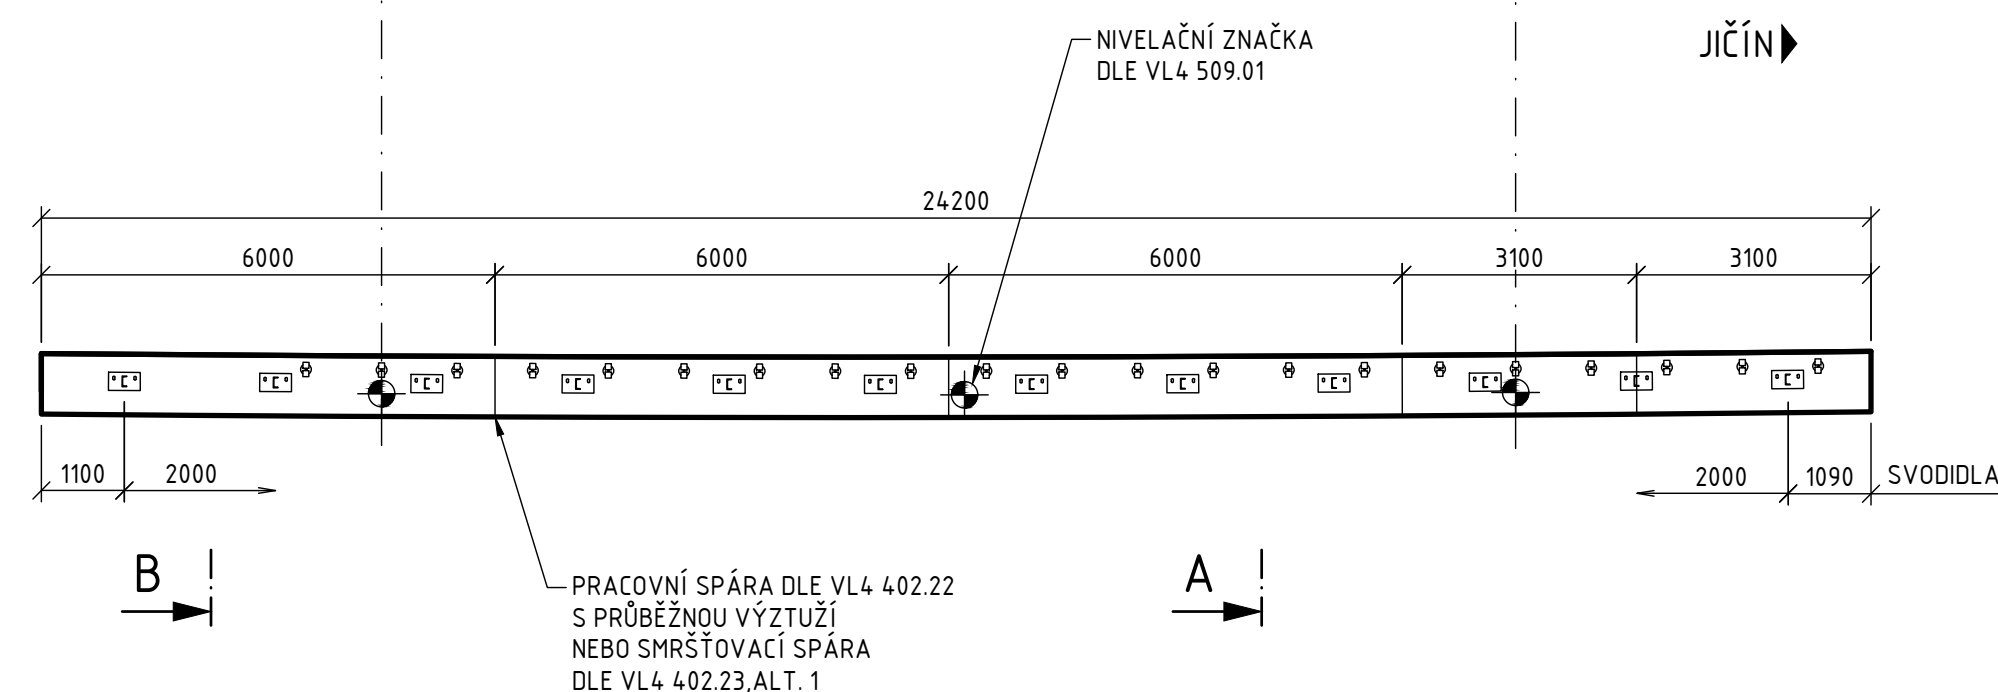

PODÉLNÝ ŘEZ OSOU SO 101

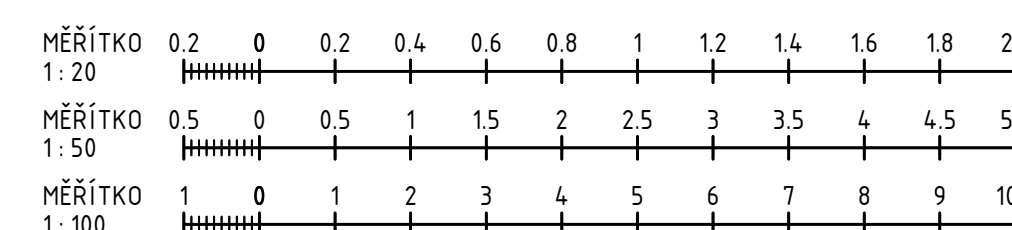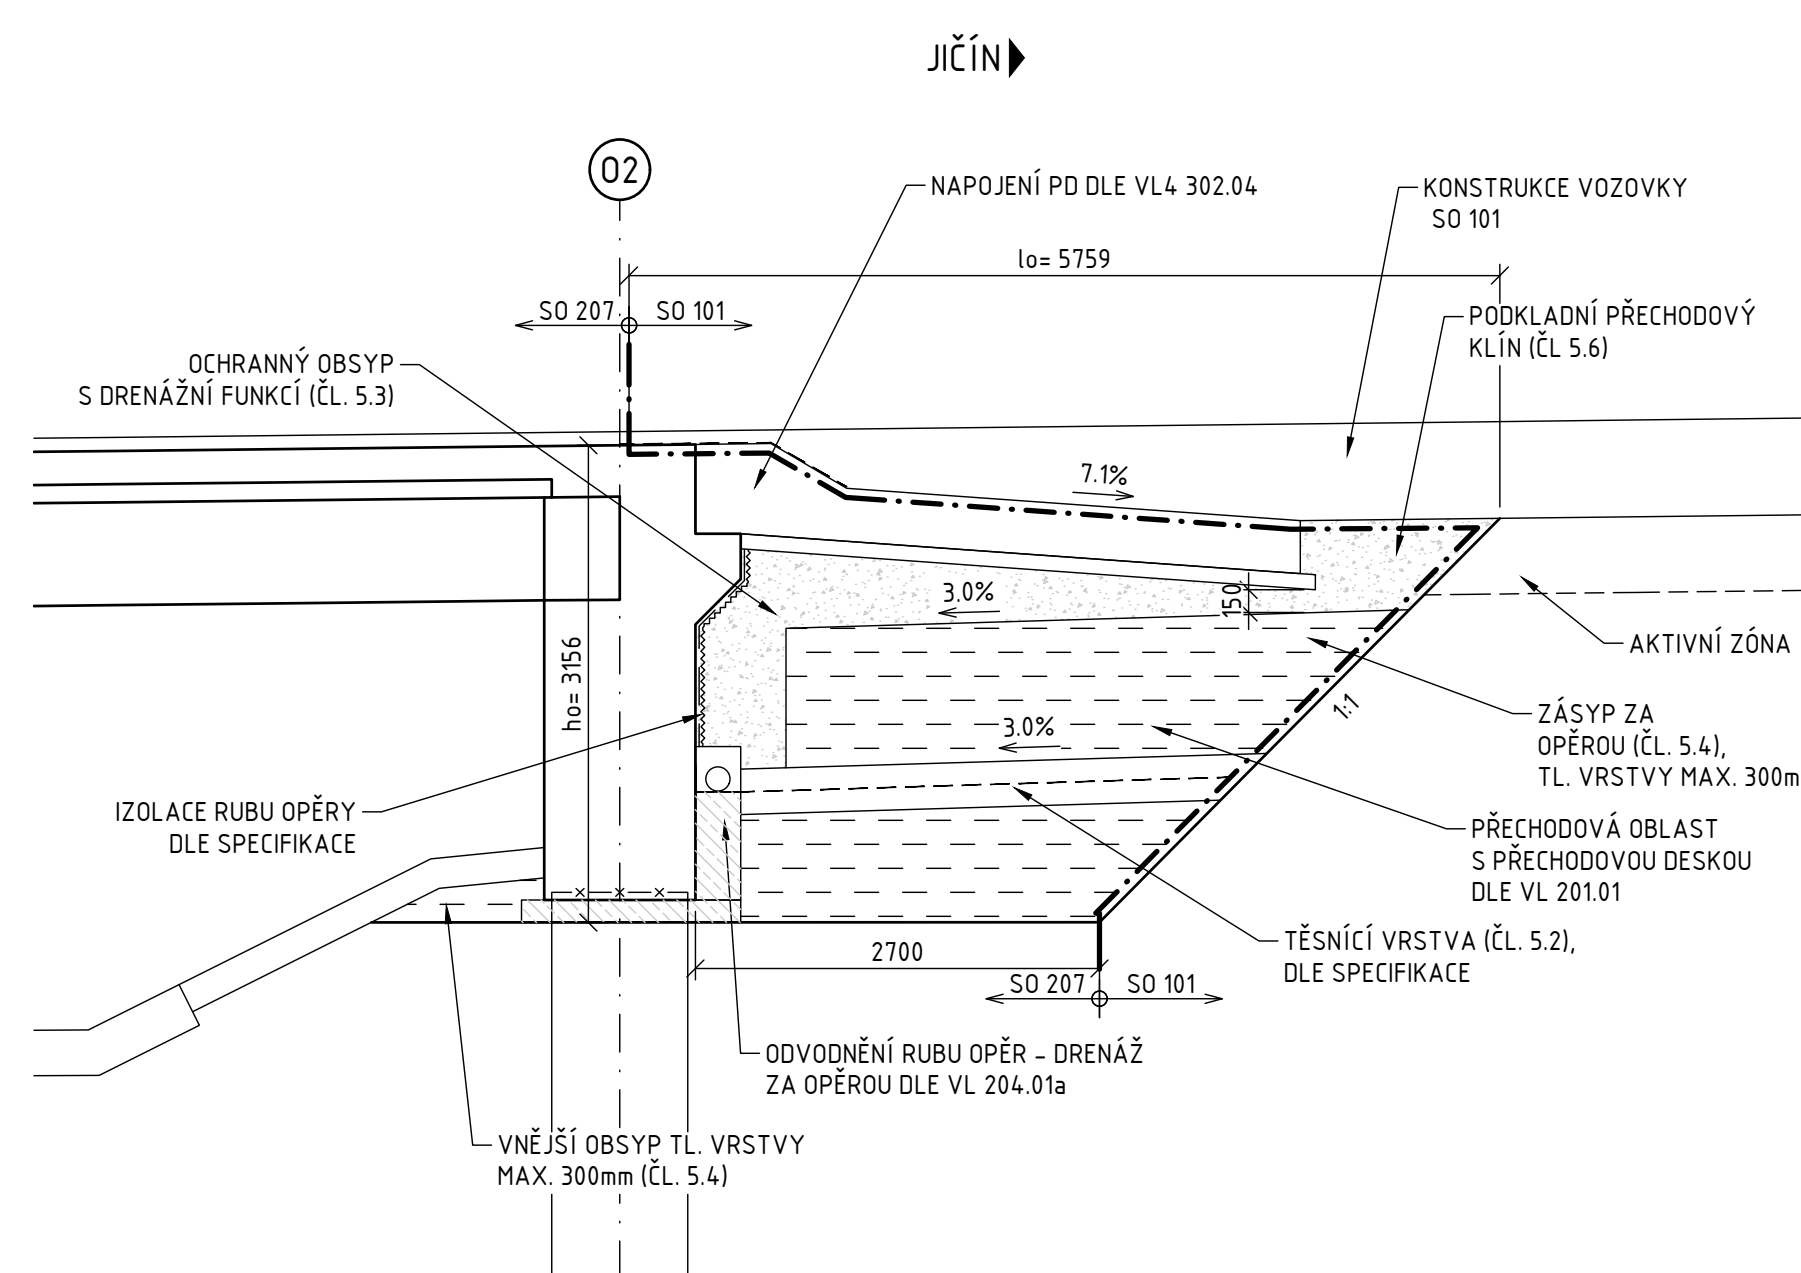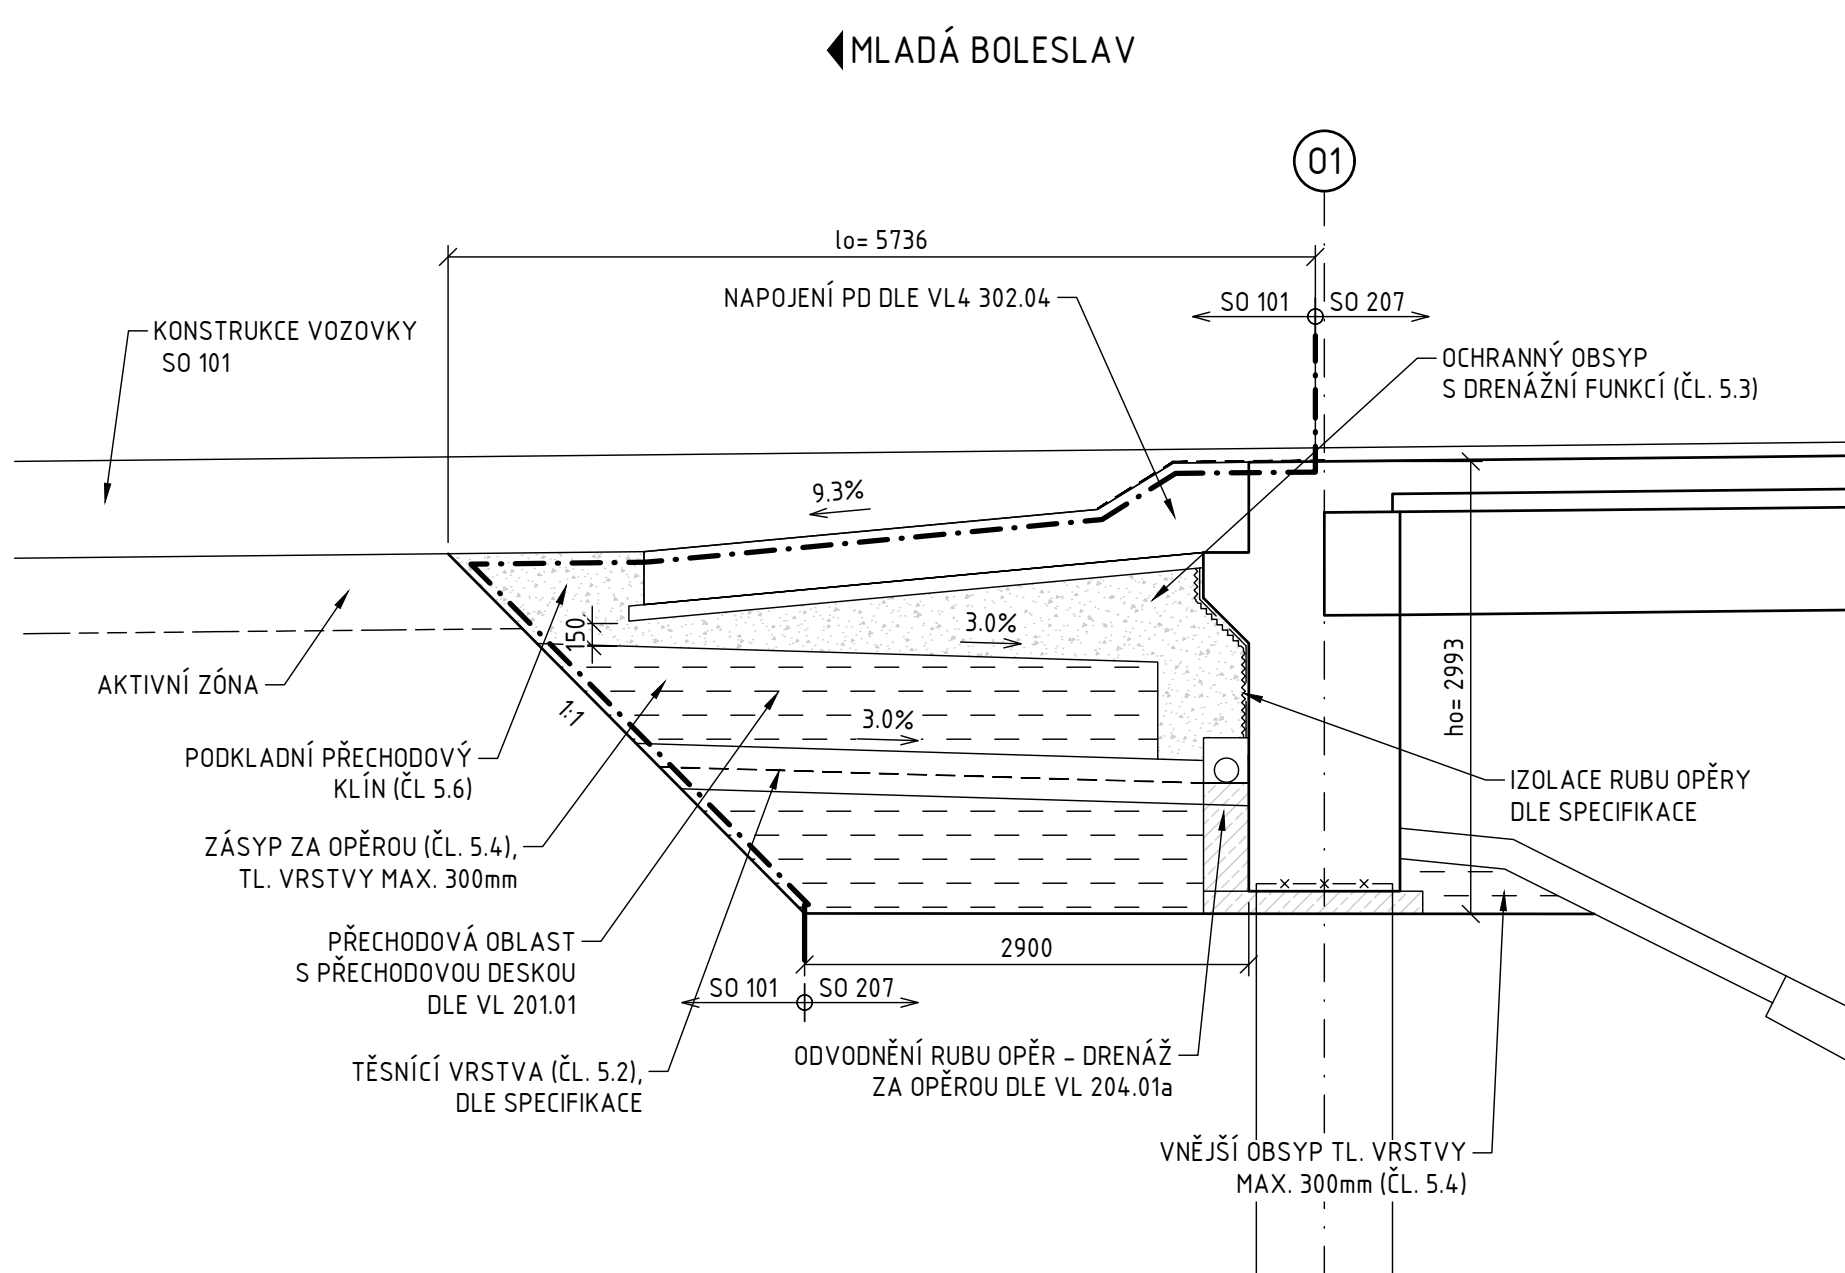

- NEDÍLNOU SOUČÁSTÍ VÝKRESU JSOU POZNÁMKY A SPECIFIKACE UVEDENÉ NA VÝKRESE
POZNÁMEK A TECHNICKÝCH SPECIFIKACÍ

Souřadnicový systém: S-JTSK
Výškový systém: Bpv

SO 207	MOST NA I/16 PŘES PŘEPEŘSKÝ POTOK V KM 7,870
---------------	--

Objednatel:



Ředitelství silnic a dálnic s. p.
Čerčanská 2023/12, Krč, 140 00 Praha 4



Valbek, spol. s r.o.
Vaňurova 505/17
460 07 Liberec 3



Zhotovitel:
Valbek, spol. s r.o.
Vaňurova 505/17
460 07 Liberec 3

Příloha	PŘECHODOVÉ OBLASTI, TVAR ŘÍMS
---------	-------------------------------

204

204