

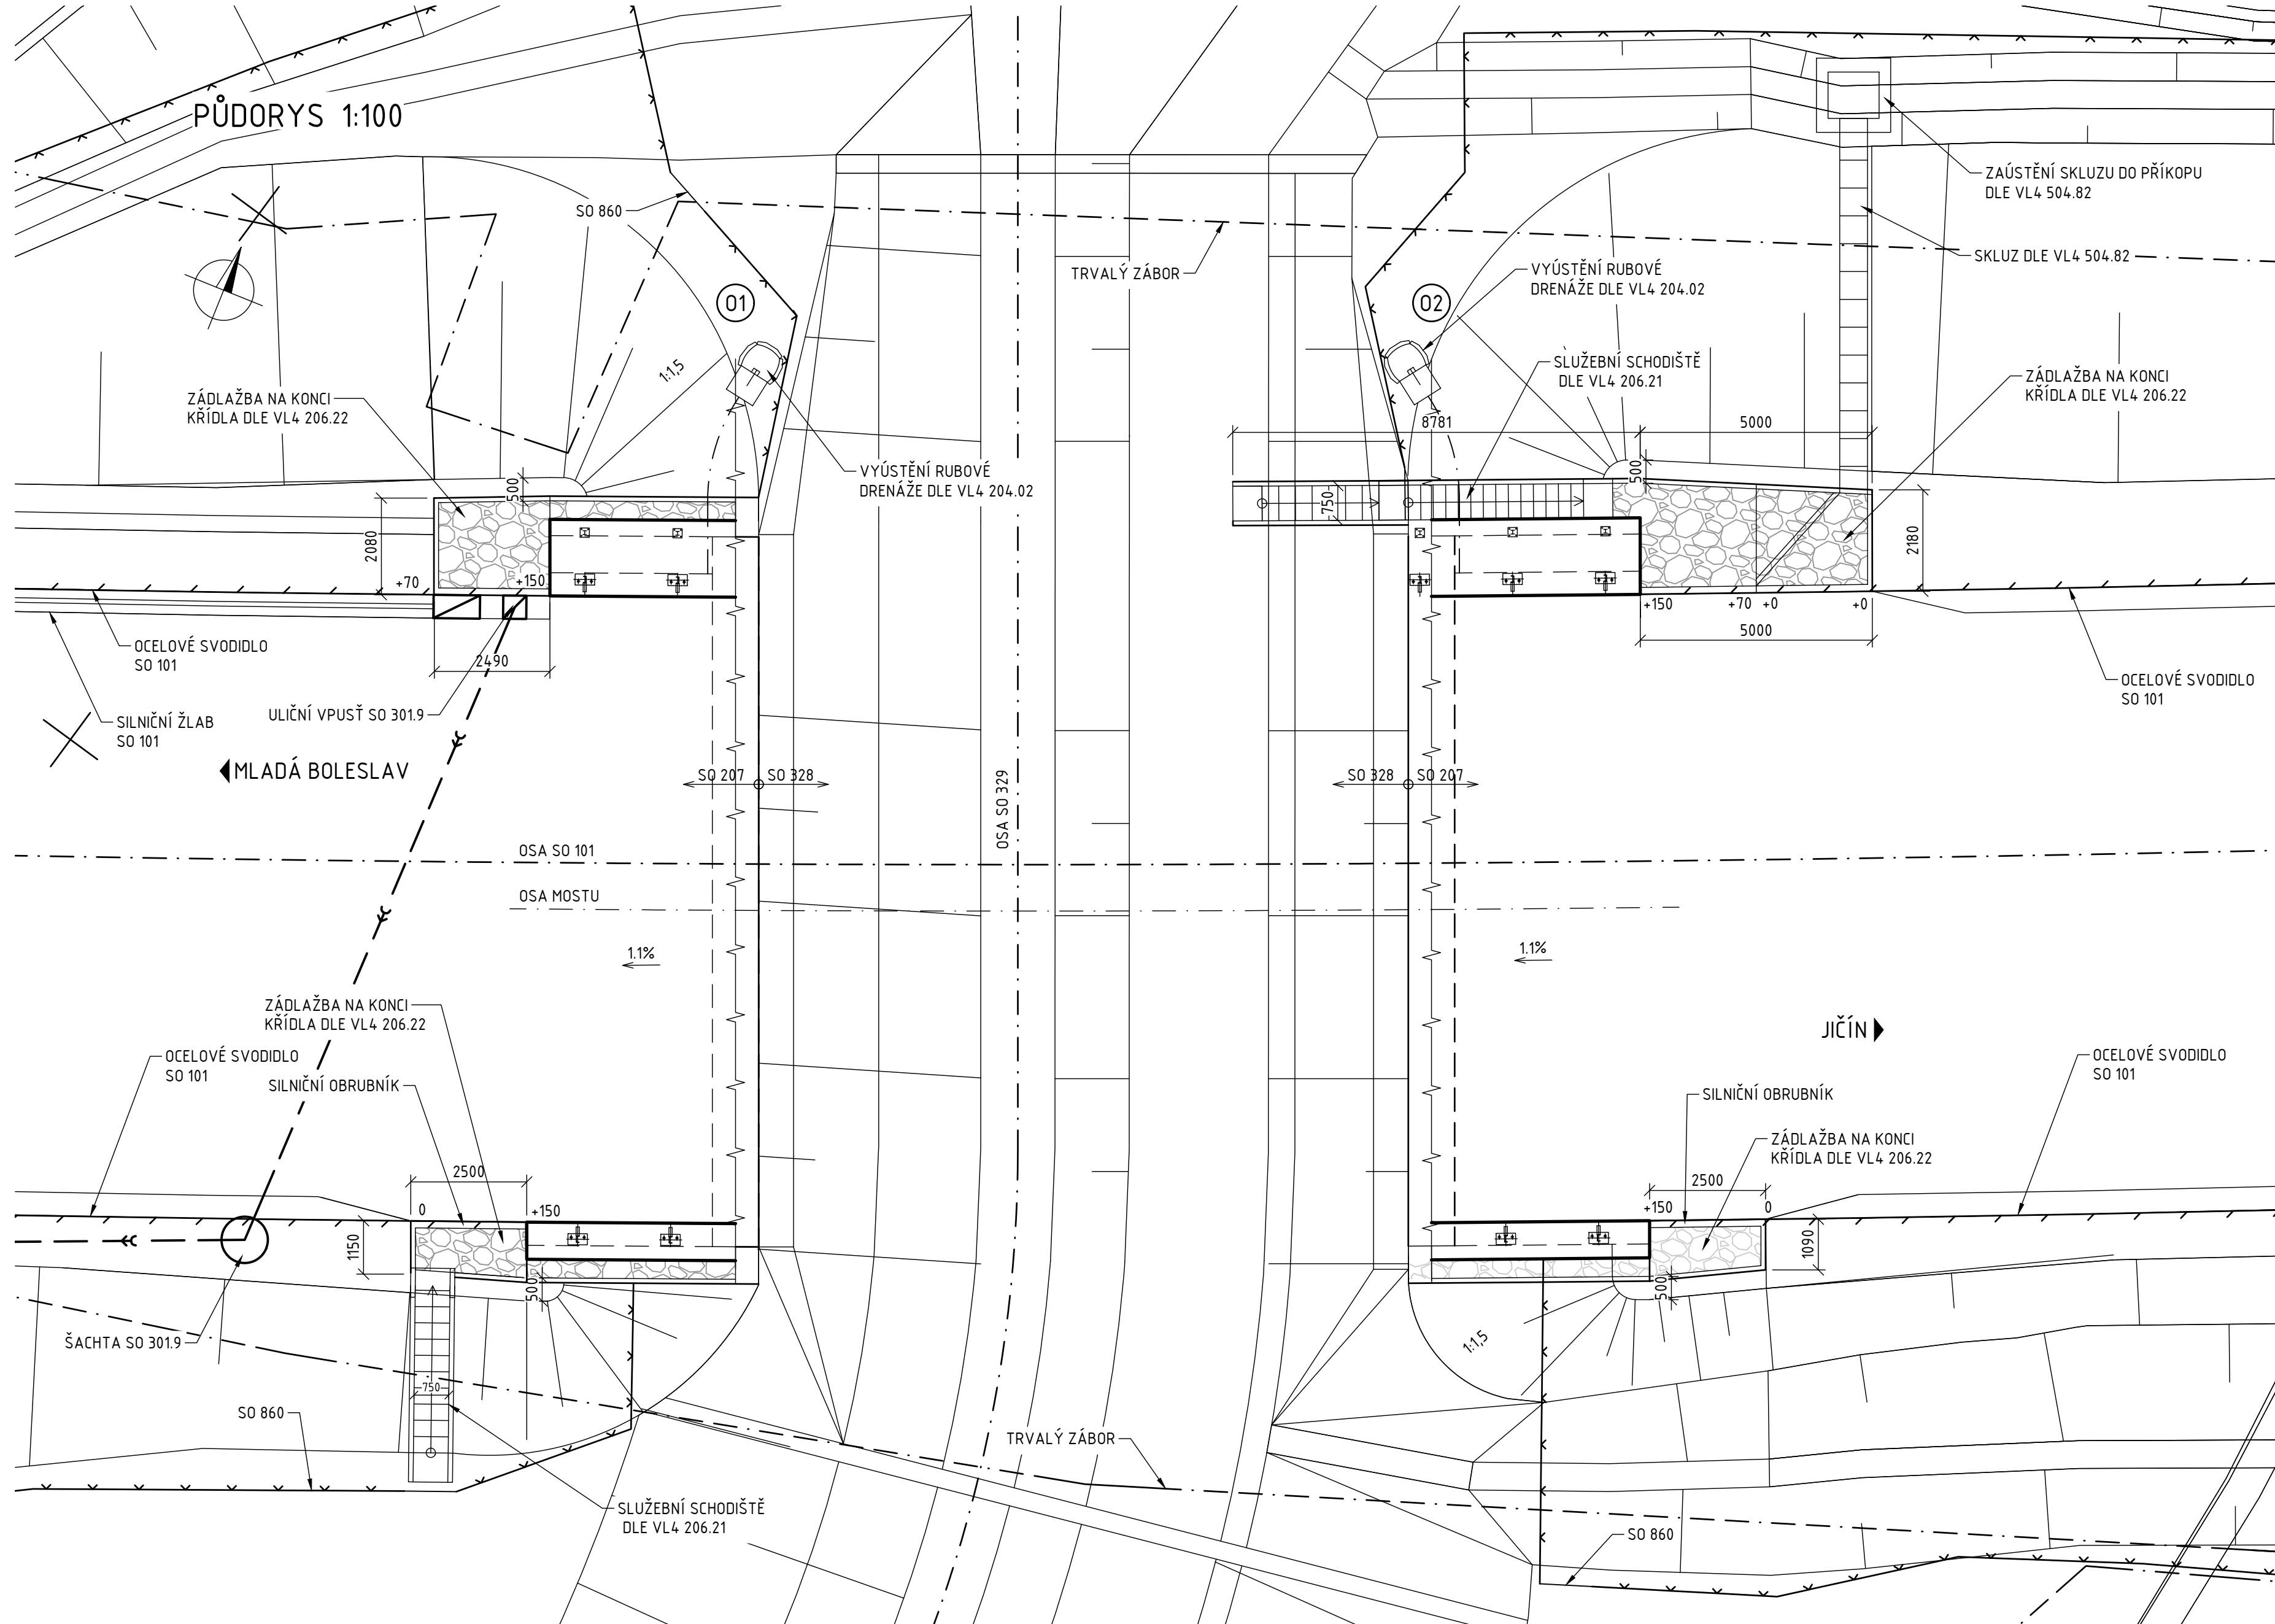



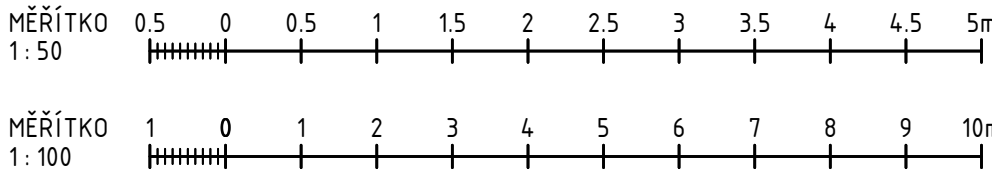


POZNÁMKY:
- NEDÍLNOU SOUČÁSTÍ VÝKRESU JSOU POZNÁMKY A SPECIFIKACE UVEDENÉ NA VÝKRESE
POZNÁMEK A TECHNICKÝCH SPECIFIKACÍ

SCHODIŠTĚ 1 - PODÉLNÝ ŘEZ 1:75

SCHODIŠTĚ 2 - PODÉLNÝ ŘEZ 1:75

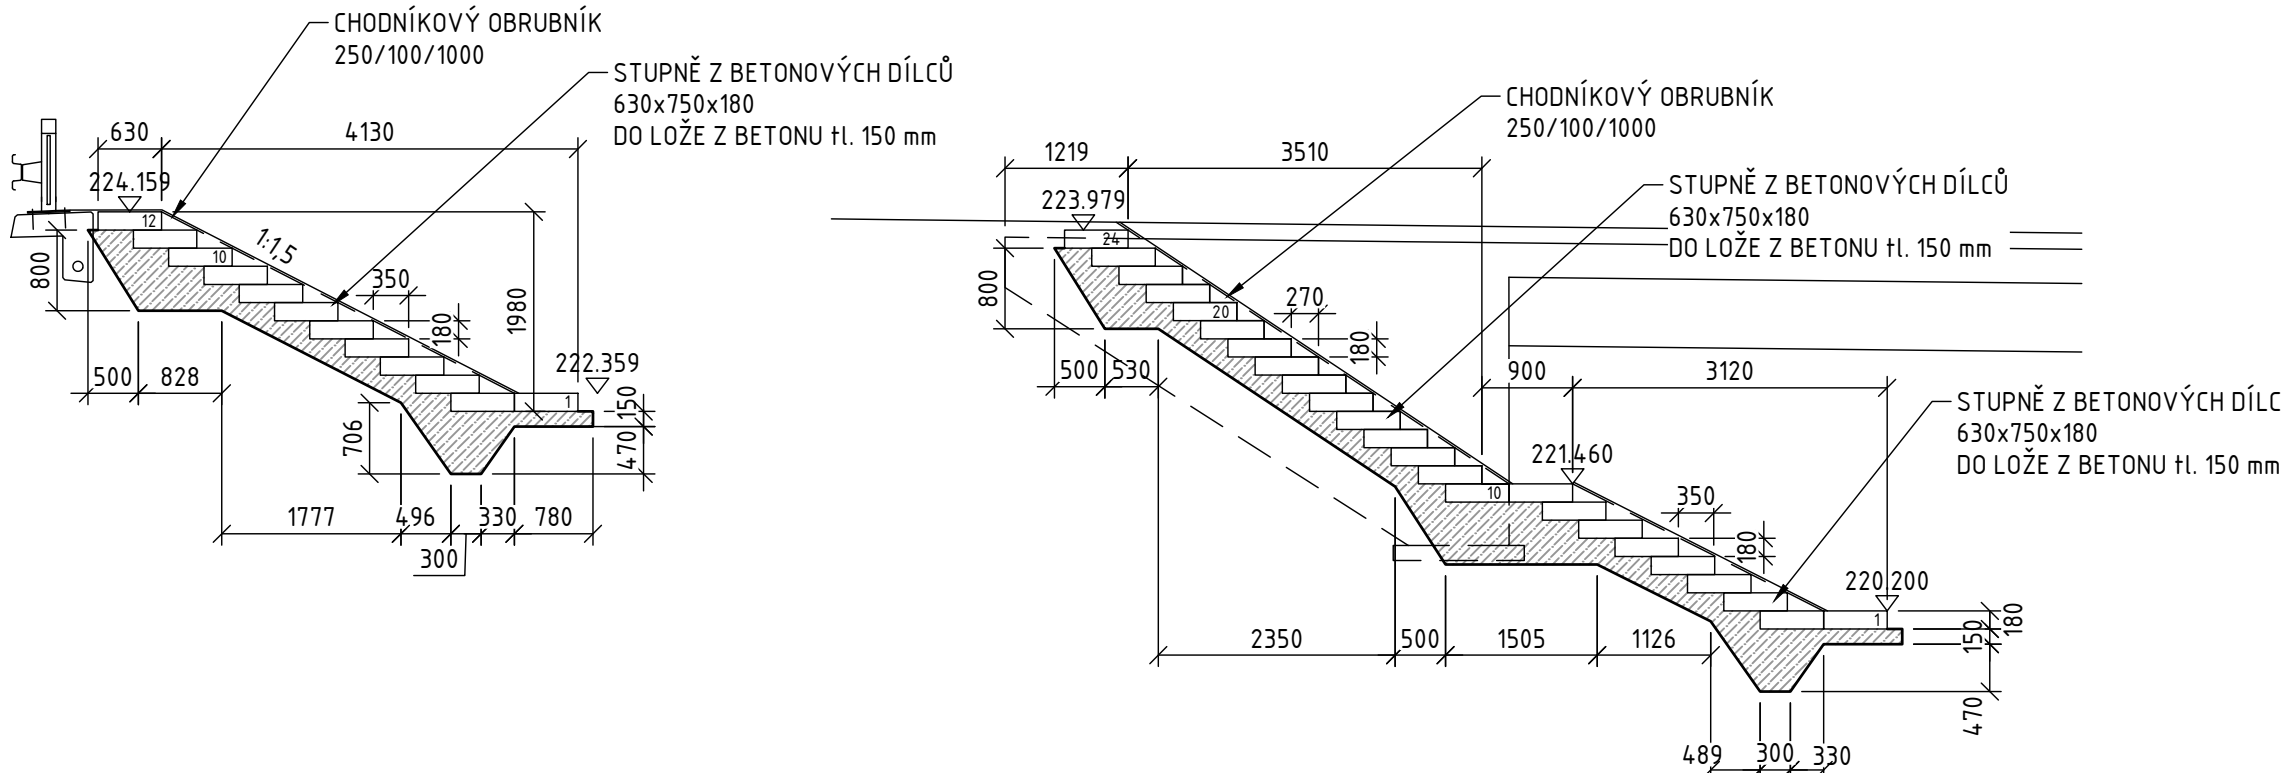

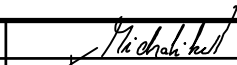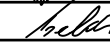Souřadnicový systém: S-JTSK Výškový systém: Bpv					
SO 207 MOST NA I/16 PŘES PŘEPEŘSKÝ POTOK V KM 7,870					
Objednatel:  ŘEDITELSTVÍ SILNIC A DÁLNIC Ředitelství silnic a dálnic s. p. Čerčanská 2023/12, Krč, 140 00 Praha 4					
 Valbek, spol. s r.o. Vaňurova 505/17 460 07 Liberec 3					
	Vypracoval	A. MICHALIKOVÁ		Zak. číslo	21-L113-001
	Zodp. projektant	ING. O. BAKHMET		Datum	02/2025
	Tech. kontrola	ING. I. BELDA		Stupeň	PDPS
	Akce I/16 MLADÁ BOLESLAV - MARTINOVICE			Počet formátů	8x A4
	Zhotovitel: Valbek, spol. s r.o. Vaňurova 505/17 460 07 Liberec 3			Měřítko	1:100,75
Příloha ÚPRAVY POD MOSTEM, SLUŽEBNÍ SCHODIŠTĚ			Č. přílohy	Paré	205