


SCHÉMA VÝZTUŽE NK 1:50
PODÉLNÝ ŘEZ

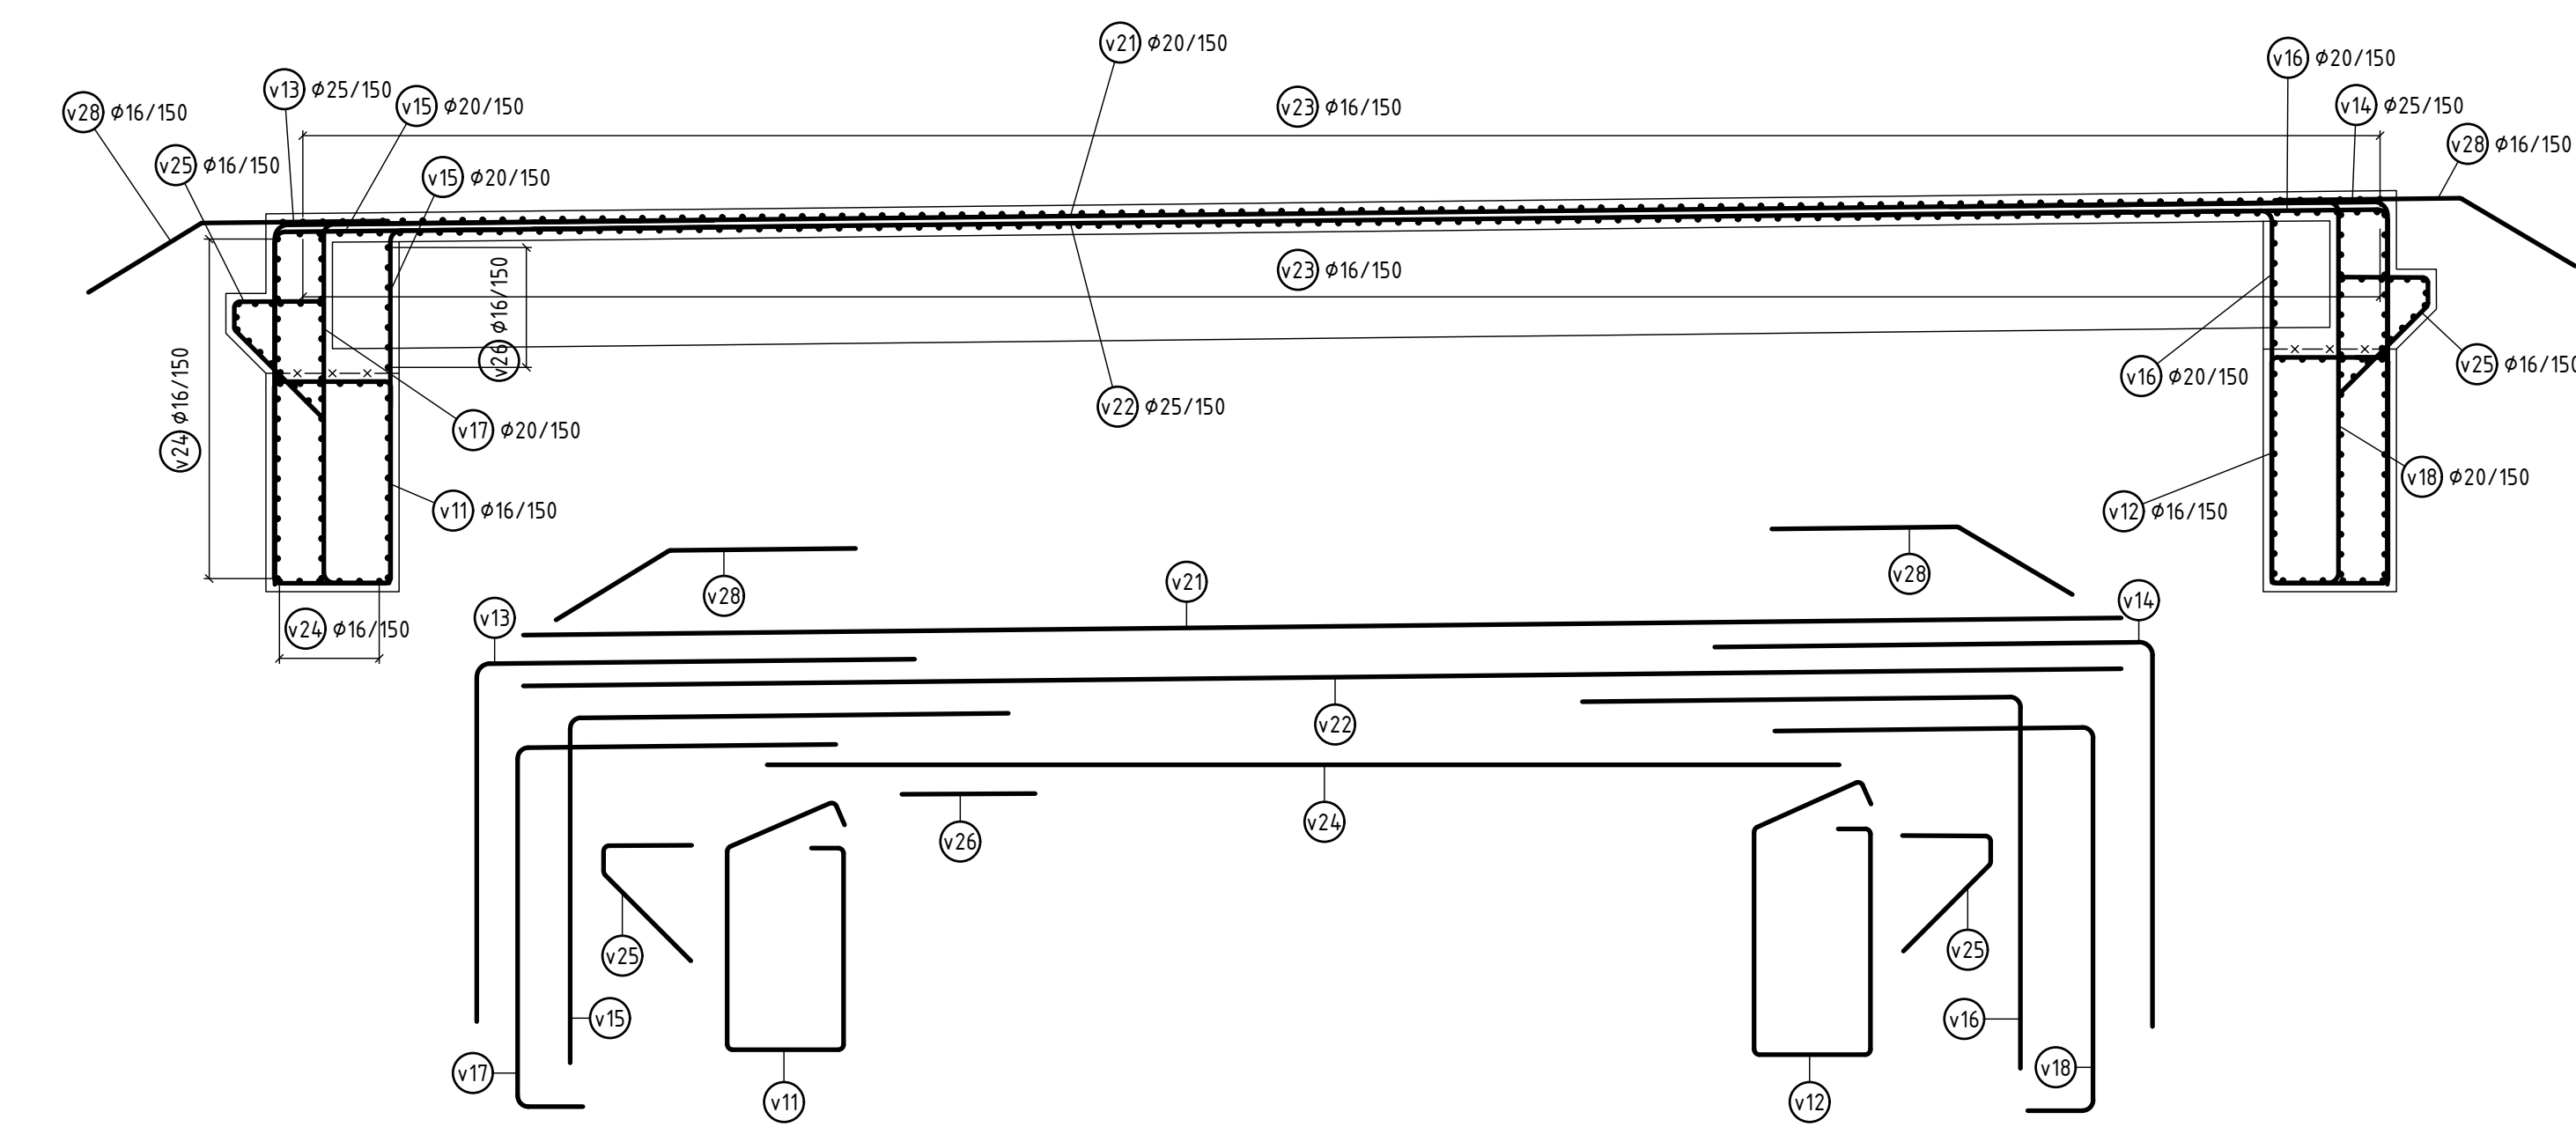


ODHAD MNOŽSTVÍ BETONÁŘSKÉ VÝZTUŽE SO 207	MNOŽSTVÍ VÝZTUŽE V %	MNOŽSTVÍ VÝZT.V KG/M3
VÝZTUŽ PILOT POD OPĚROU 1, D 900MM	1.02%	80
VÝZTUŽ PILOT POD OPĚROU 2, D 900MM	1.02%	80
VÝZTUŽ PRO DŘÍK OPĚRY, KŘÍDLA	2.17%	170
VÝZTUŽ ŘÍMS	1.72%	135
VÝZTUŽ PŘECHODOVÝCH DESEK	2.04%	160


POZNÁMKY:

- NEDÍLNOU SOUČÁSTÍ VÝKRESU JSOU POZNÁMKY A SPECIFIKACE UVEDENÉ NA VÝKRESE
POZNÁMEK A TECHNICKÝCH SPECIFIKACÍ



PŘÍČNÝ ŘEZ 1:50

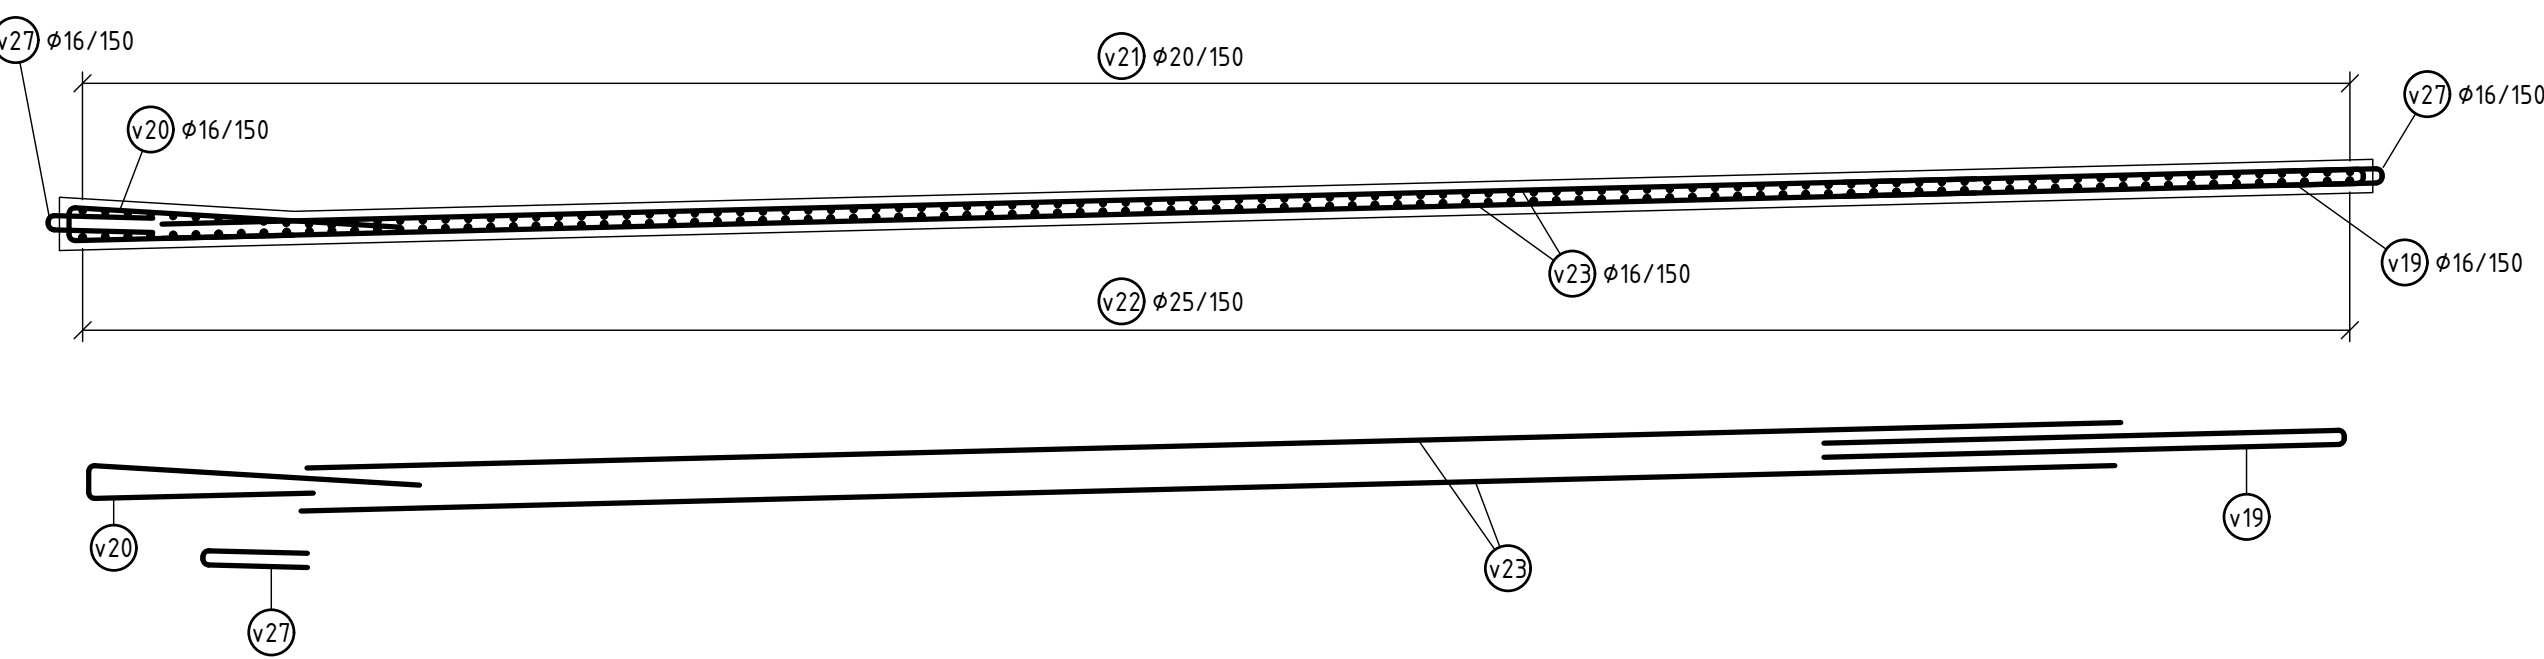

ŘEZ KŘÍDLEM 1, 2
1:50

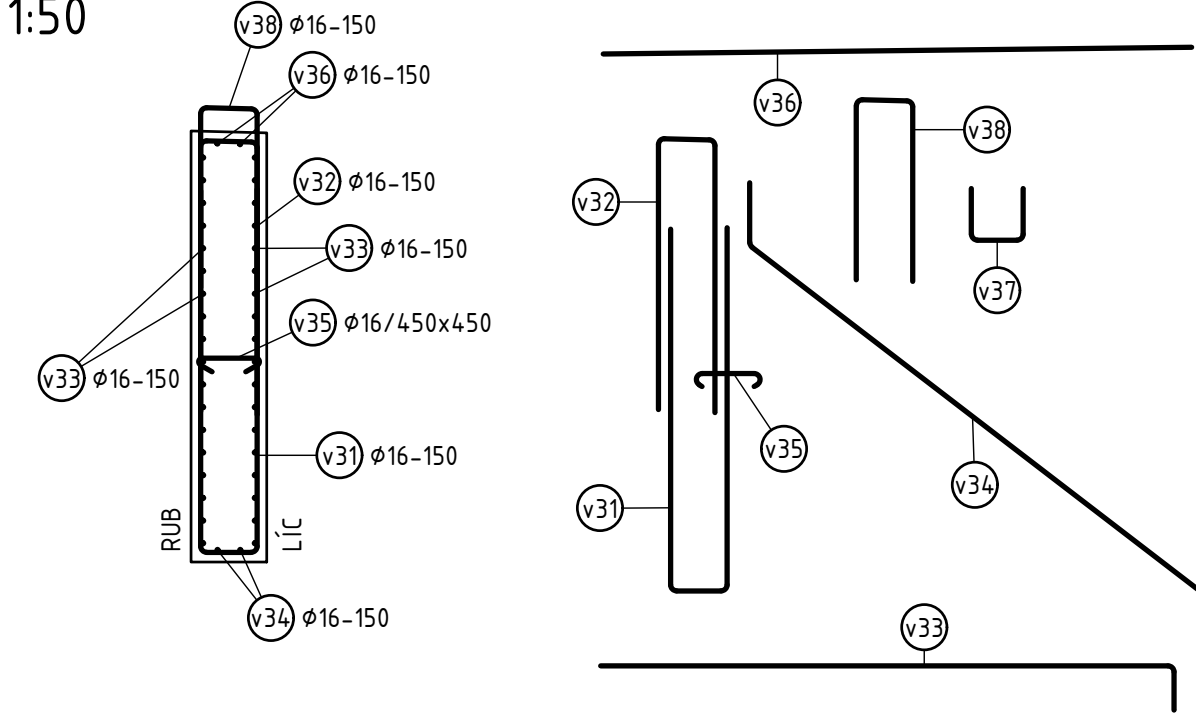

ŘEZ KŘÍDLEM 3, 4
1:50

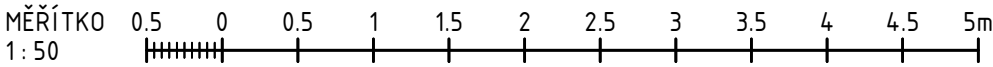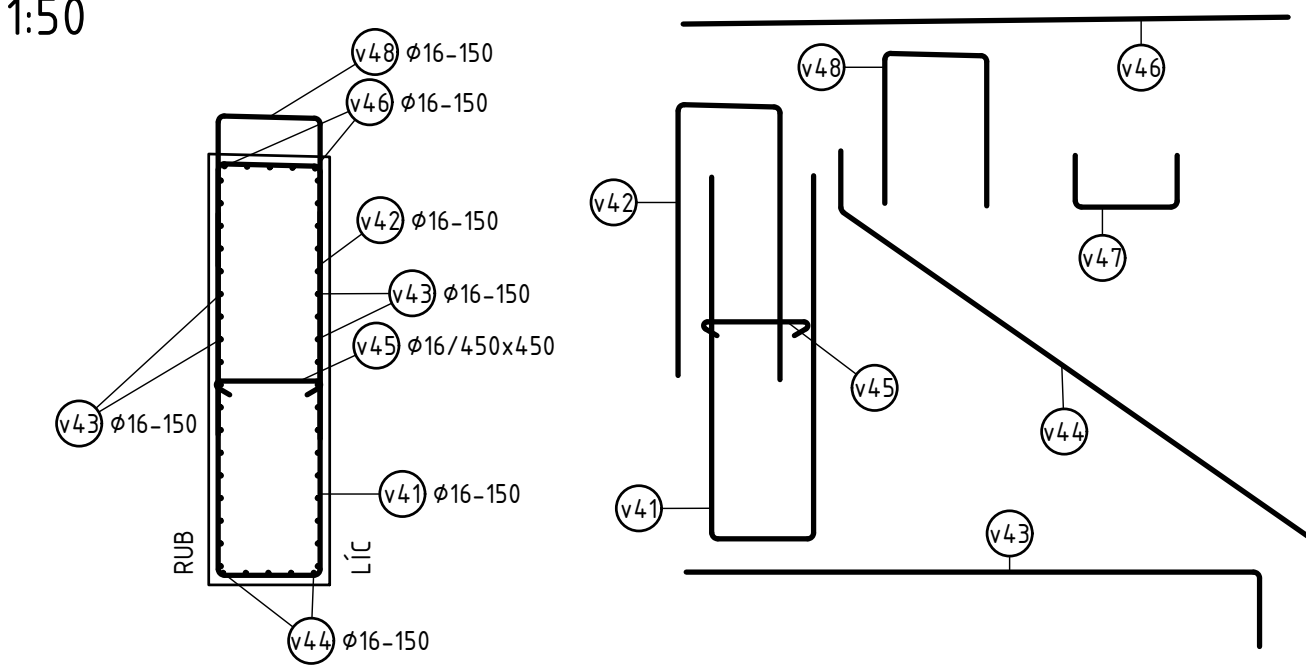

Souřadnicový systém: S-JTSK
Výškový systém: BpV

SO 207 MOST NA I/16 PŘES PŘEPEŘSKÝ POTOK V KM 7,870

Objednatel:



Ředitelství silnic a dálnic
Čerčanská 2023/12, Krč, 140 00 Praha 4



Valbek, spol. s r.o.
Vaňurova 505/17
460 07 Liberec 3

	Vypracoval	A. MICHALÍKOVÁ	Zak. číslo	21-L113-001
	Zodp. projektant	ING. O. BAKHMET	Datum	02/2025
	Tech. kontrola	ING. I. BELDA	Stupeň	PDPS
	Akce	I/16 MLADÁ BOLESLAV - MARTINOVICE		Počet formátů
Zhotovitel: Valbek, spol. s r.o. Vaňurova 505/17 460 07 Liberec 3	Příloha	SCHÉMATICKÉ VÝKRESY VÝZTUŽE	Měřítko	1:50
			Č. přílohy	Paré
			301	