



SCHÉMA POSTUPU DEMOLICE

STÁVAJÍCÍ STAV

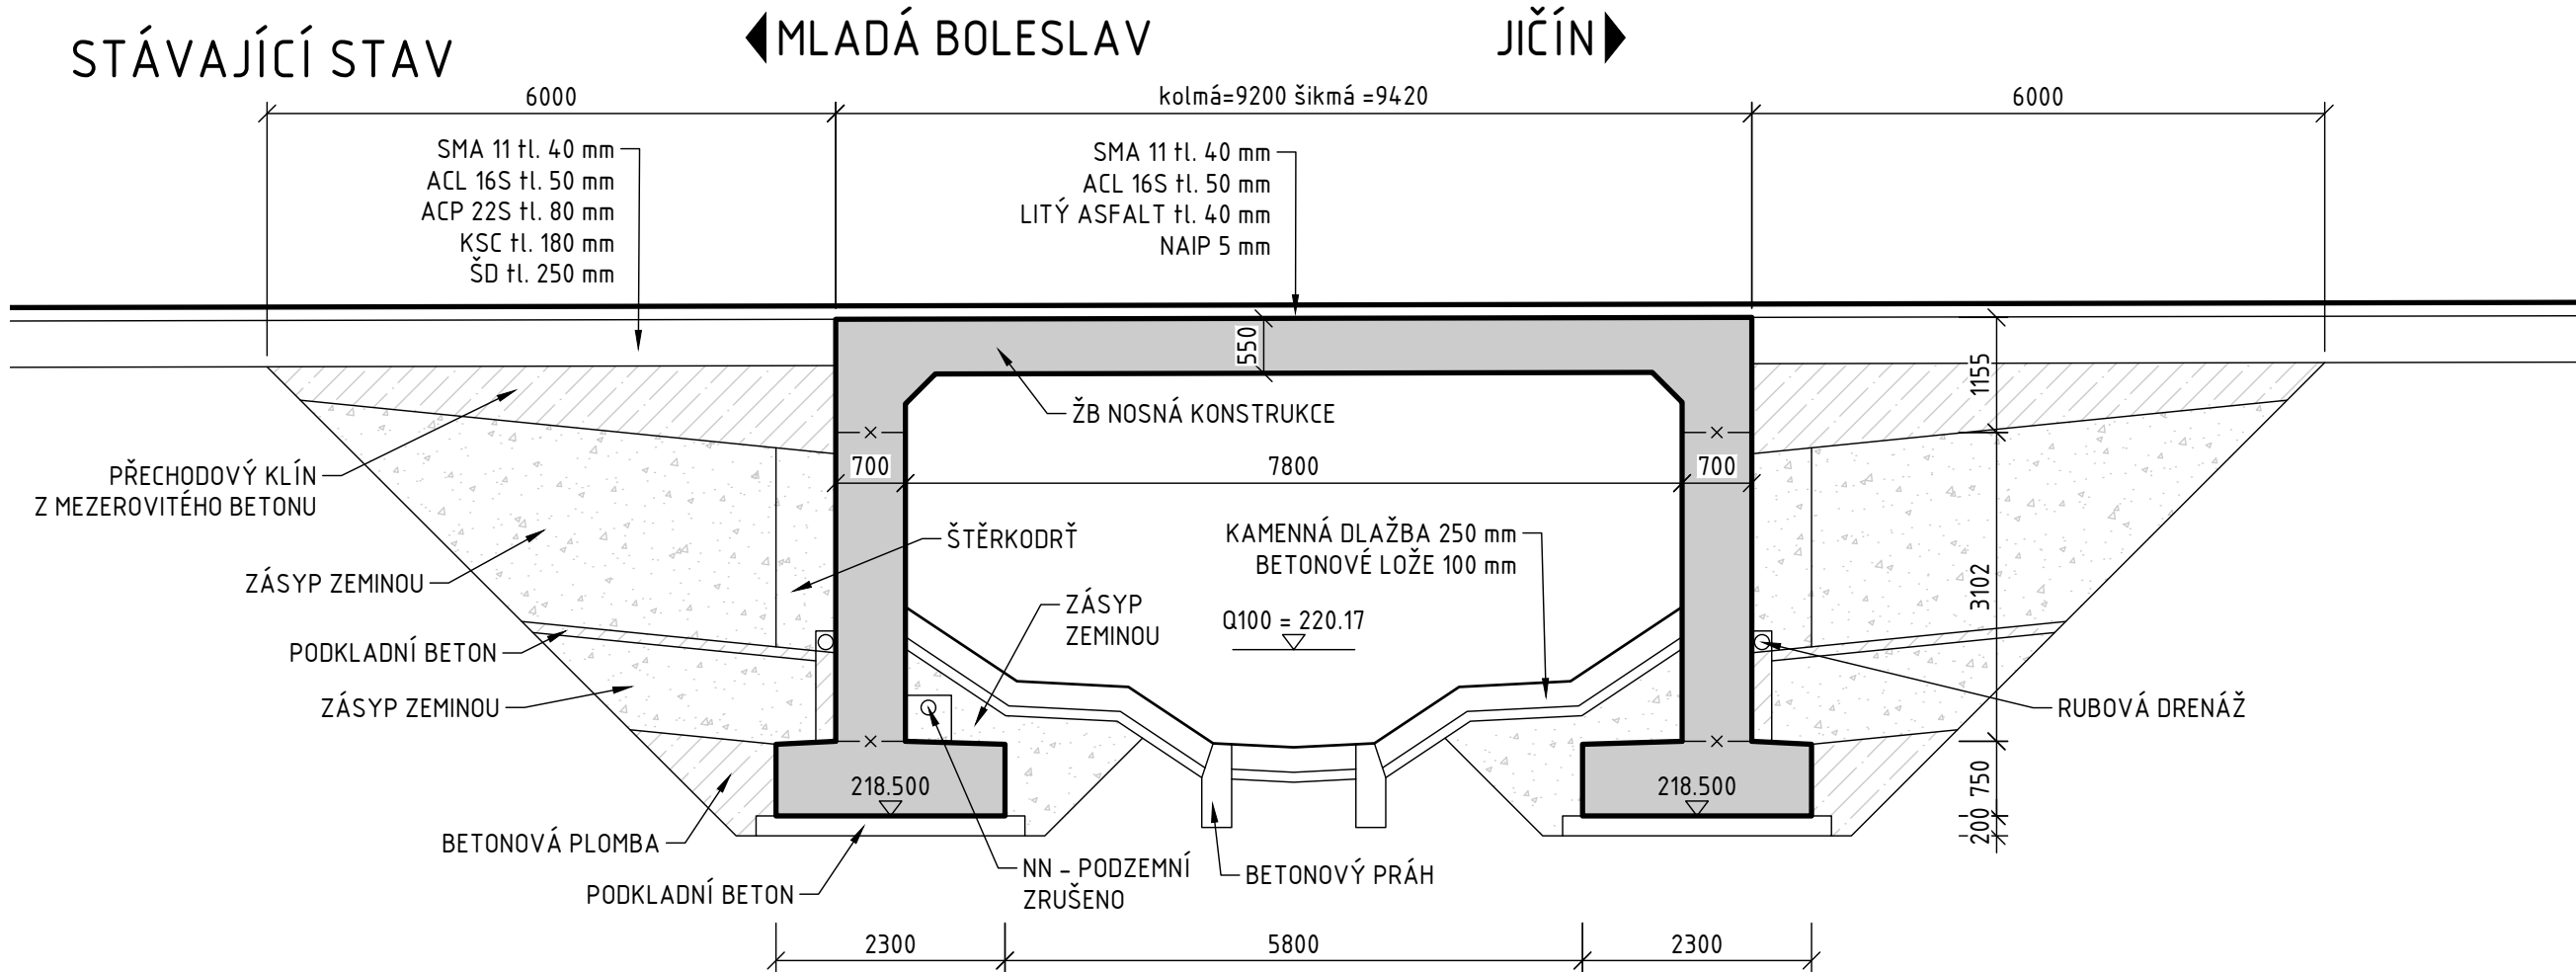

ETAPA 3

- ZPĚTNÝ ZÁSYP ZEMINOU VHDNOU DO NÁSYPU (ISO 101)
- REALIZACE VOZOVKOVÝCH VRSTEV V NOVÉ TRASE (ISO 101)
- OBNOVENÍ PROVOZU

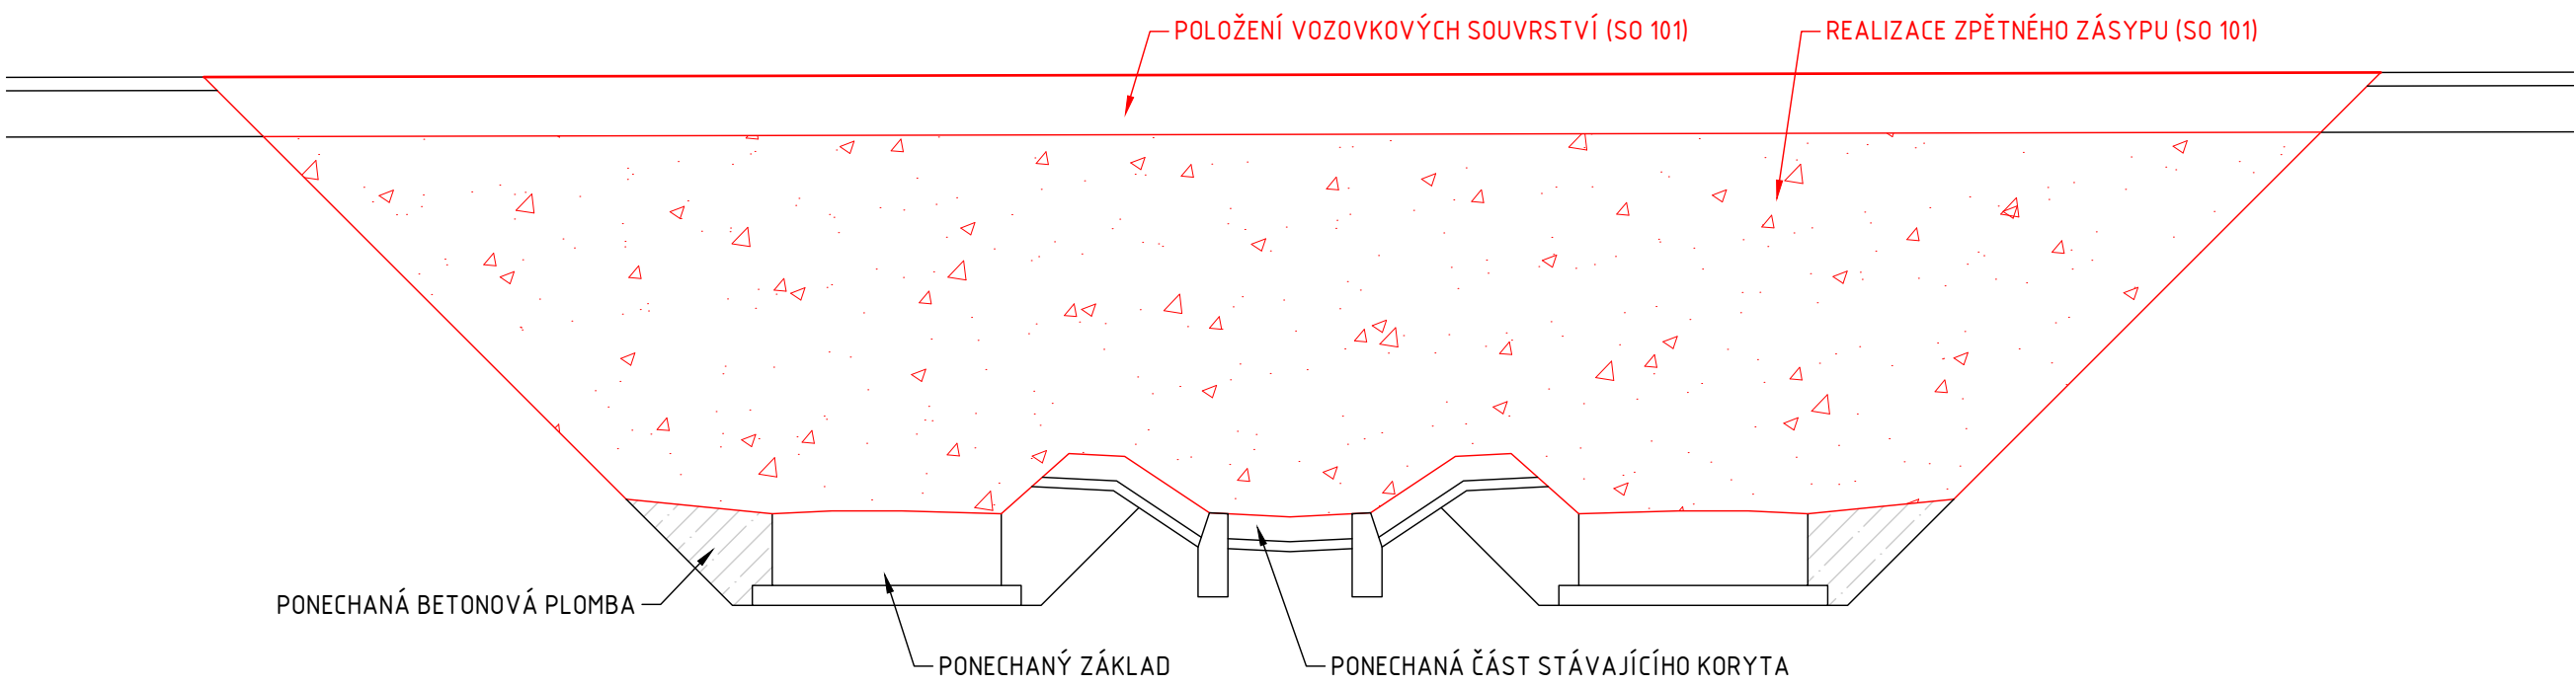


ETAPA 0

- PŘELOŽENÍ VODOTEČE POD NOVÝ MOST
- ODPOJENÍ RUŠENÉ SÍTĚ NÍZKÉHO NAPĚTÍ PODZEMNÍ VEDENÉ POD MOSTEM
- DIO


ETAPA 1

- FRÉZOVÁNÍ VOZOVKY, ODSTRANĚNÍ VOZOVKOVÉHO SOUVRSTVÍ V PŘECHODOVÉ OBLASTI
- SNESENÍ ZÁBRADELNÍHO SVODIDLA, DEMOLICE ŘÍMS
- DEMOLICE ZÁDLAŽEB NA KONCI KŘÍDLA, SLUŽEBNÍCH SCHODIŠŤ, SKLUZŮ A VÝVAŘIŠŤ
- DEMOLICE / ODTĚŽENÍ VRSTEV PŘECHODOVÉ OBLASTI PO BETONOVOU PLOMBU
- ODTĚŽENÍ OBSYPOVÝCH KUŽELŮ V NUTNÉM ROZSAHU PRO MOŽNOST DEMOLICE KŘÍDEL
- DEMOLICE ZPEVNĚNÍ KORYTA V NUTNÉM ROZSAHU PRO MOŽNOST DEMOLICE STOJKY NK
- ODSTRANĚNÍ STÁVAJÍCÍ SÍTĚ NN- PODZEMNÍ

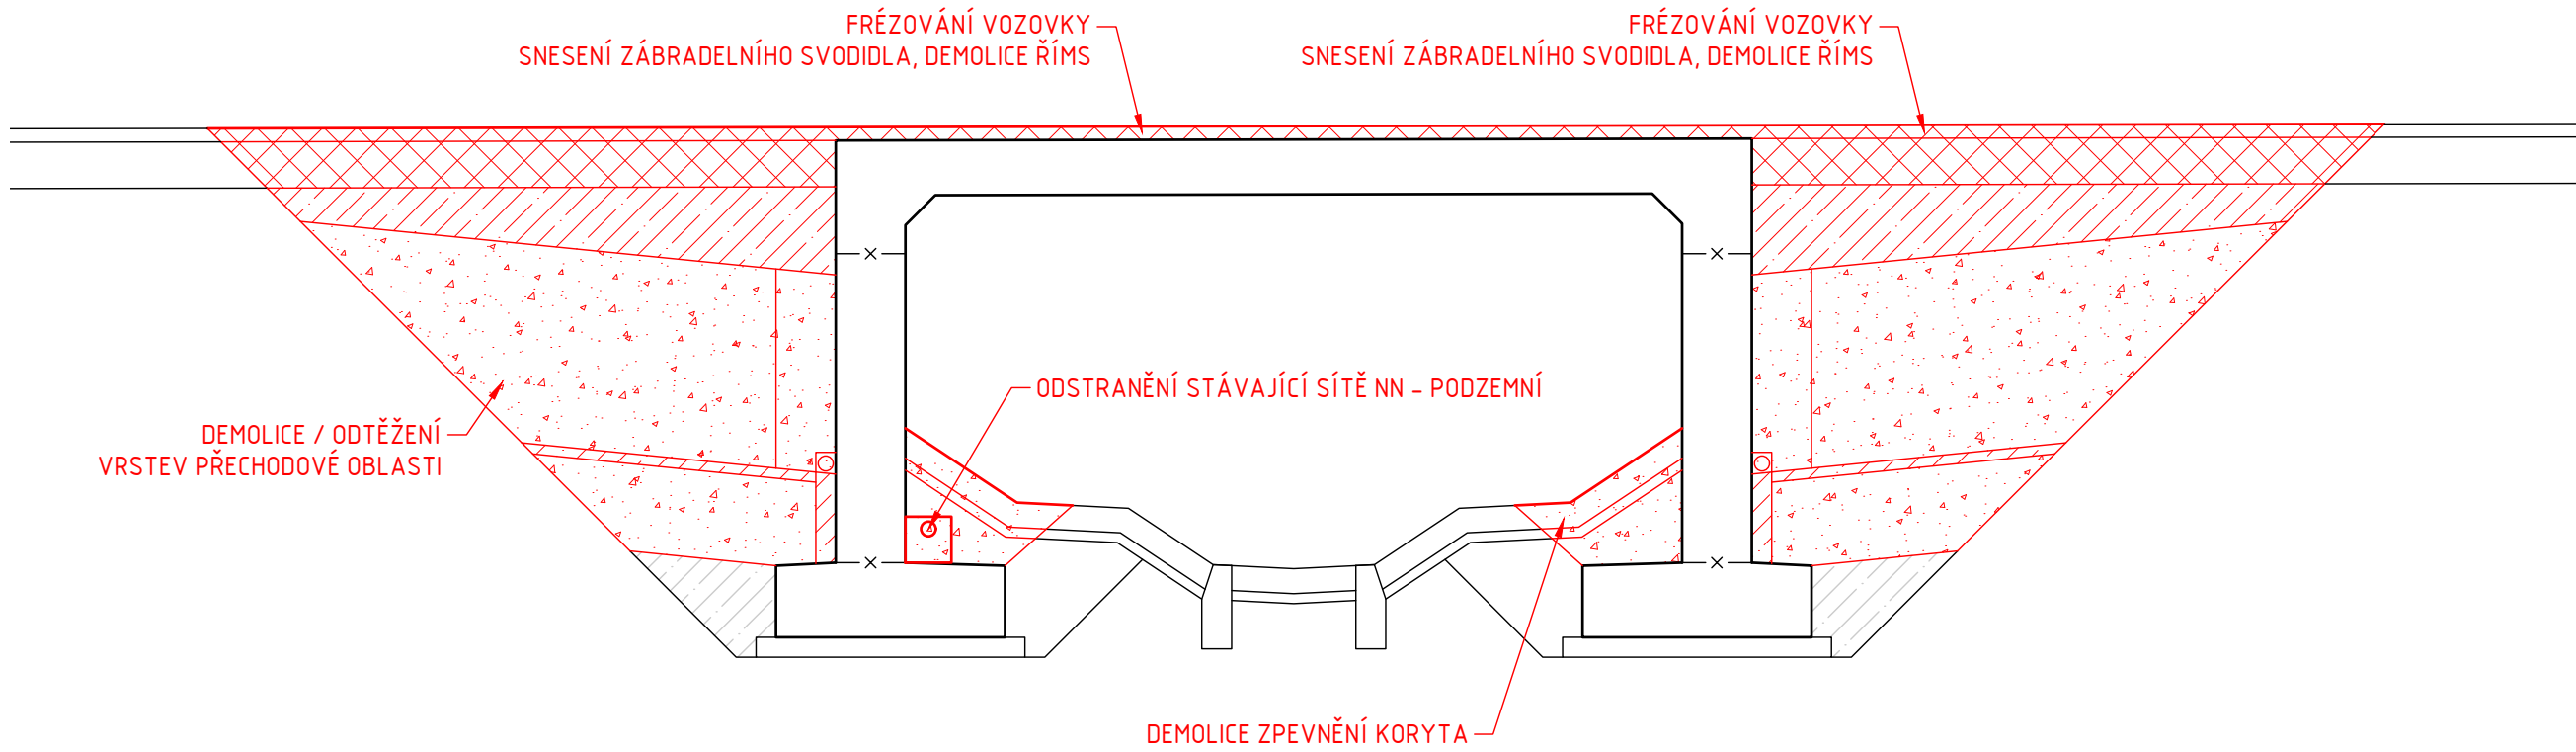

ETAPA 2

- DEMOLICE NOSNÉ DESKOVÉ KONSTRUKCE, STOJEK A KŘÍDEL PO ÚROVŇ ZÁKLADU
- DOKONČOVACÍ PRÁCE DEMOLICE

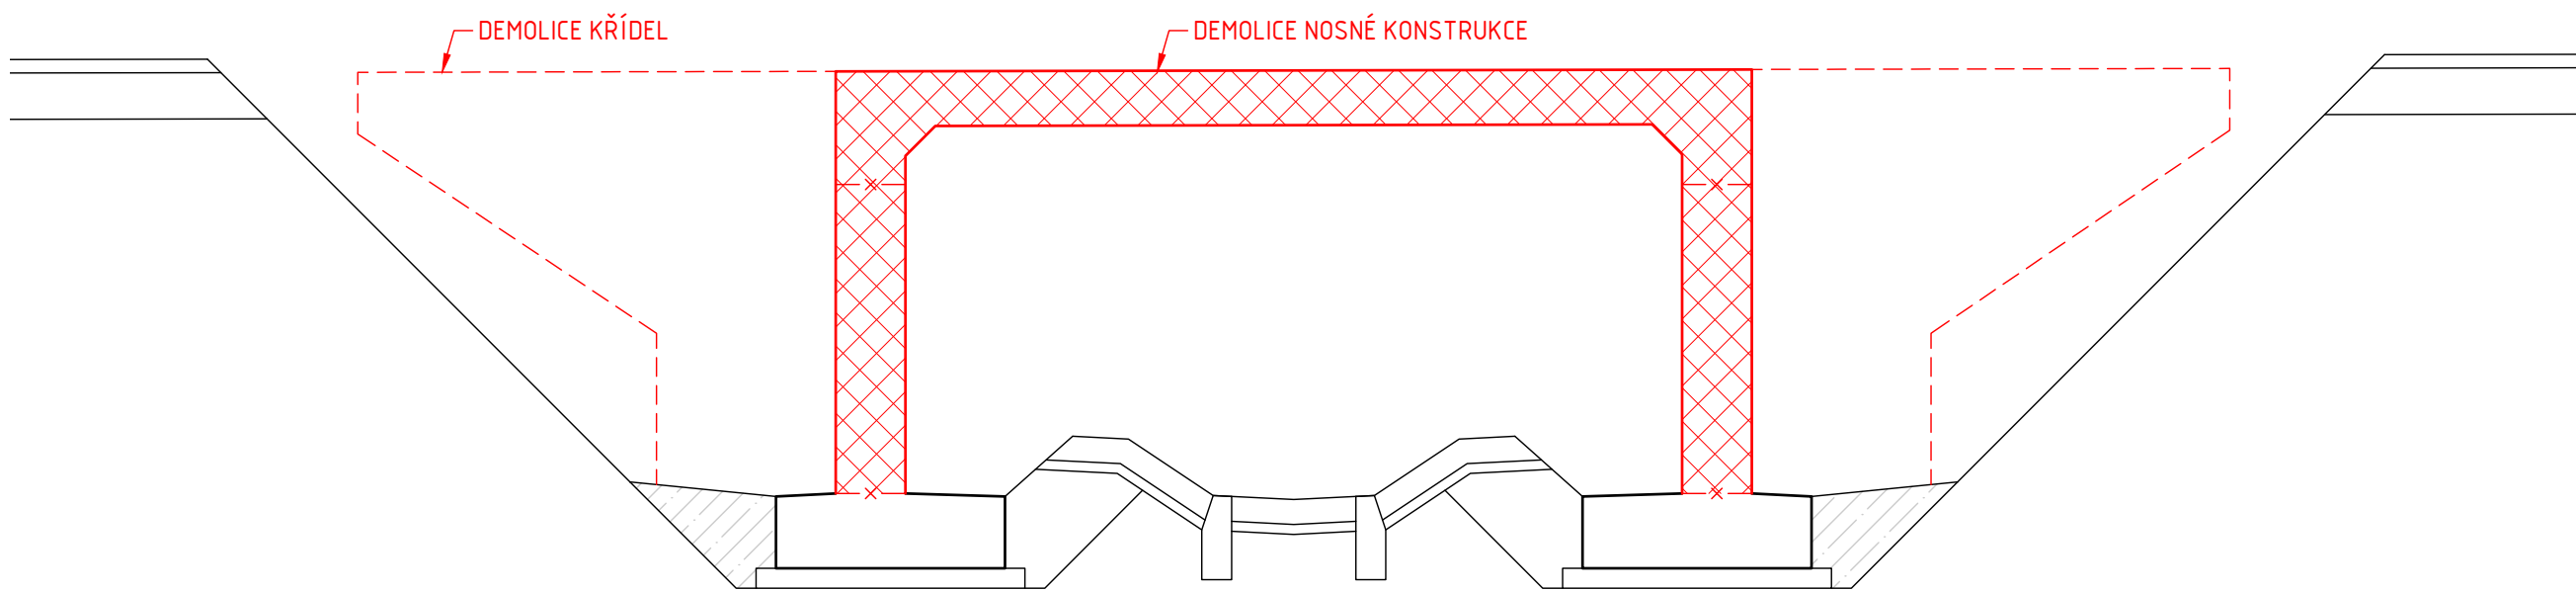

Souřadnicový systém: S-JTSK
Výškový systém: Bpv

SO 207 MOST NA I/16 PŘES PŘEPĚŘSKÝ POTOK V KM 7,870

Objednatel:



Ředitelství silnic a dálnic s. p.
Čerčanská 2023/12, Krč, 140 00 Praha 4



Valbek, spol. s r.o.
Vaňurova 505/17
460 07 Liberec 3

	Vypracoval	ING. T. JAKUBÍČEK		Zak. číslo	21-L113-001
	Zodp. projektant	ING. O. BAKHMET		Datum	02/2025
	Tech. kontrola	ING. I. BELDA		Stupeň	PDPS
	Akce	I/16 MLADÁ BOLESLAV - MARTINOVICE		Počet formátů	8x A4
Zhotovitel:		Příloha		Měřítko	1:75
Valbek, spol. s r.o. Vaňurova 505/17 460 07 Liberec 3		DEMOLICE STÁVAJÍCÍHO MOSTU ev.č. 16-033		Č. přílohy	Paré
				501	