



PŮDORYS 1:200

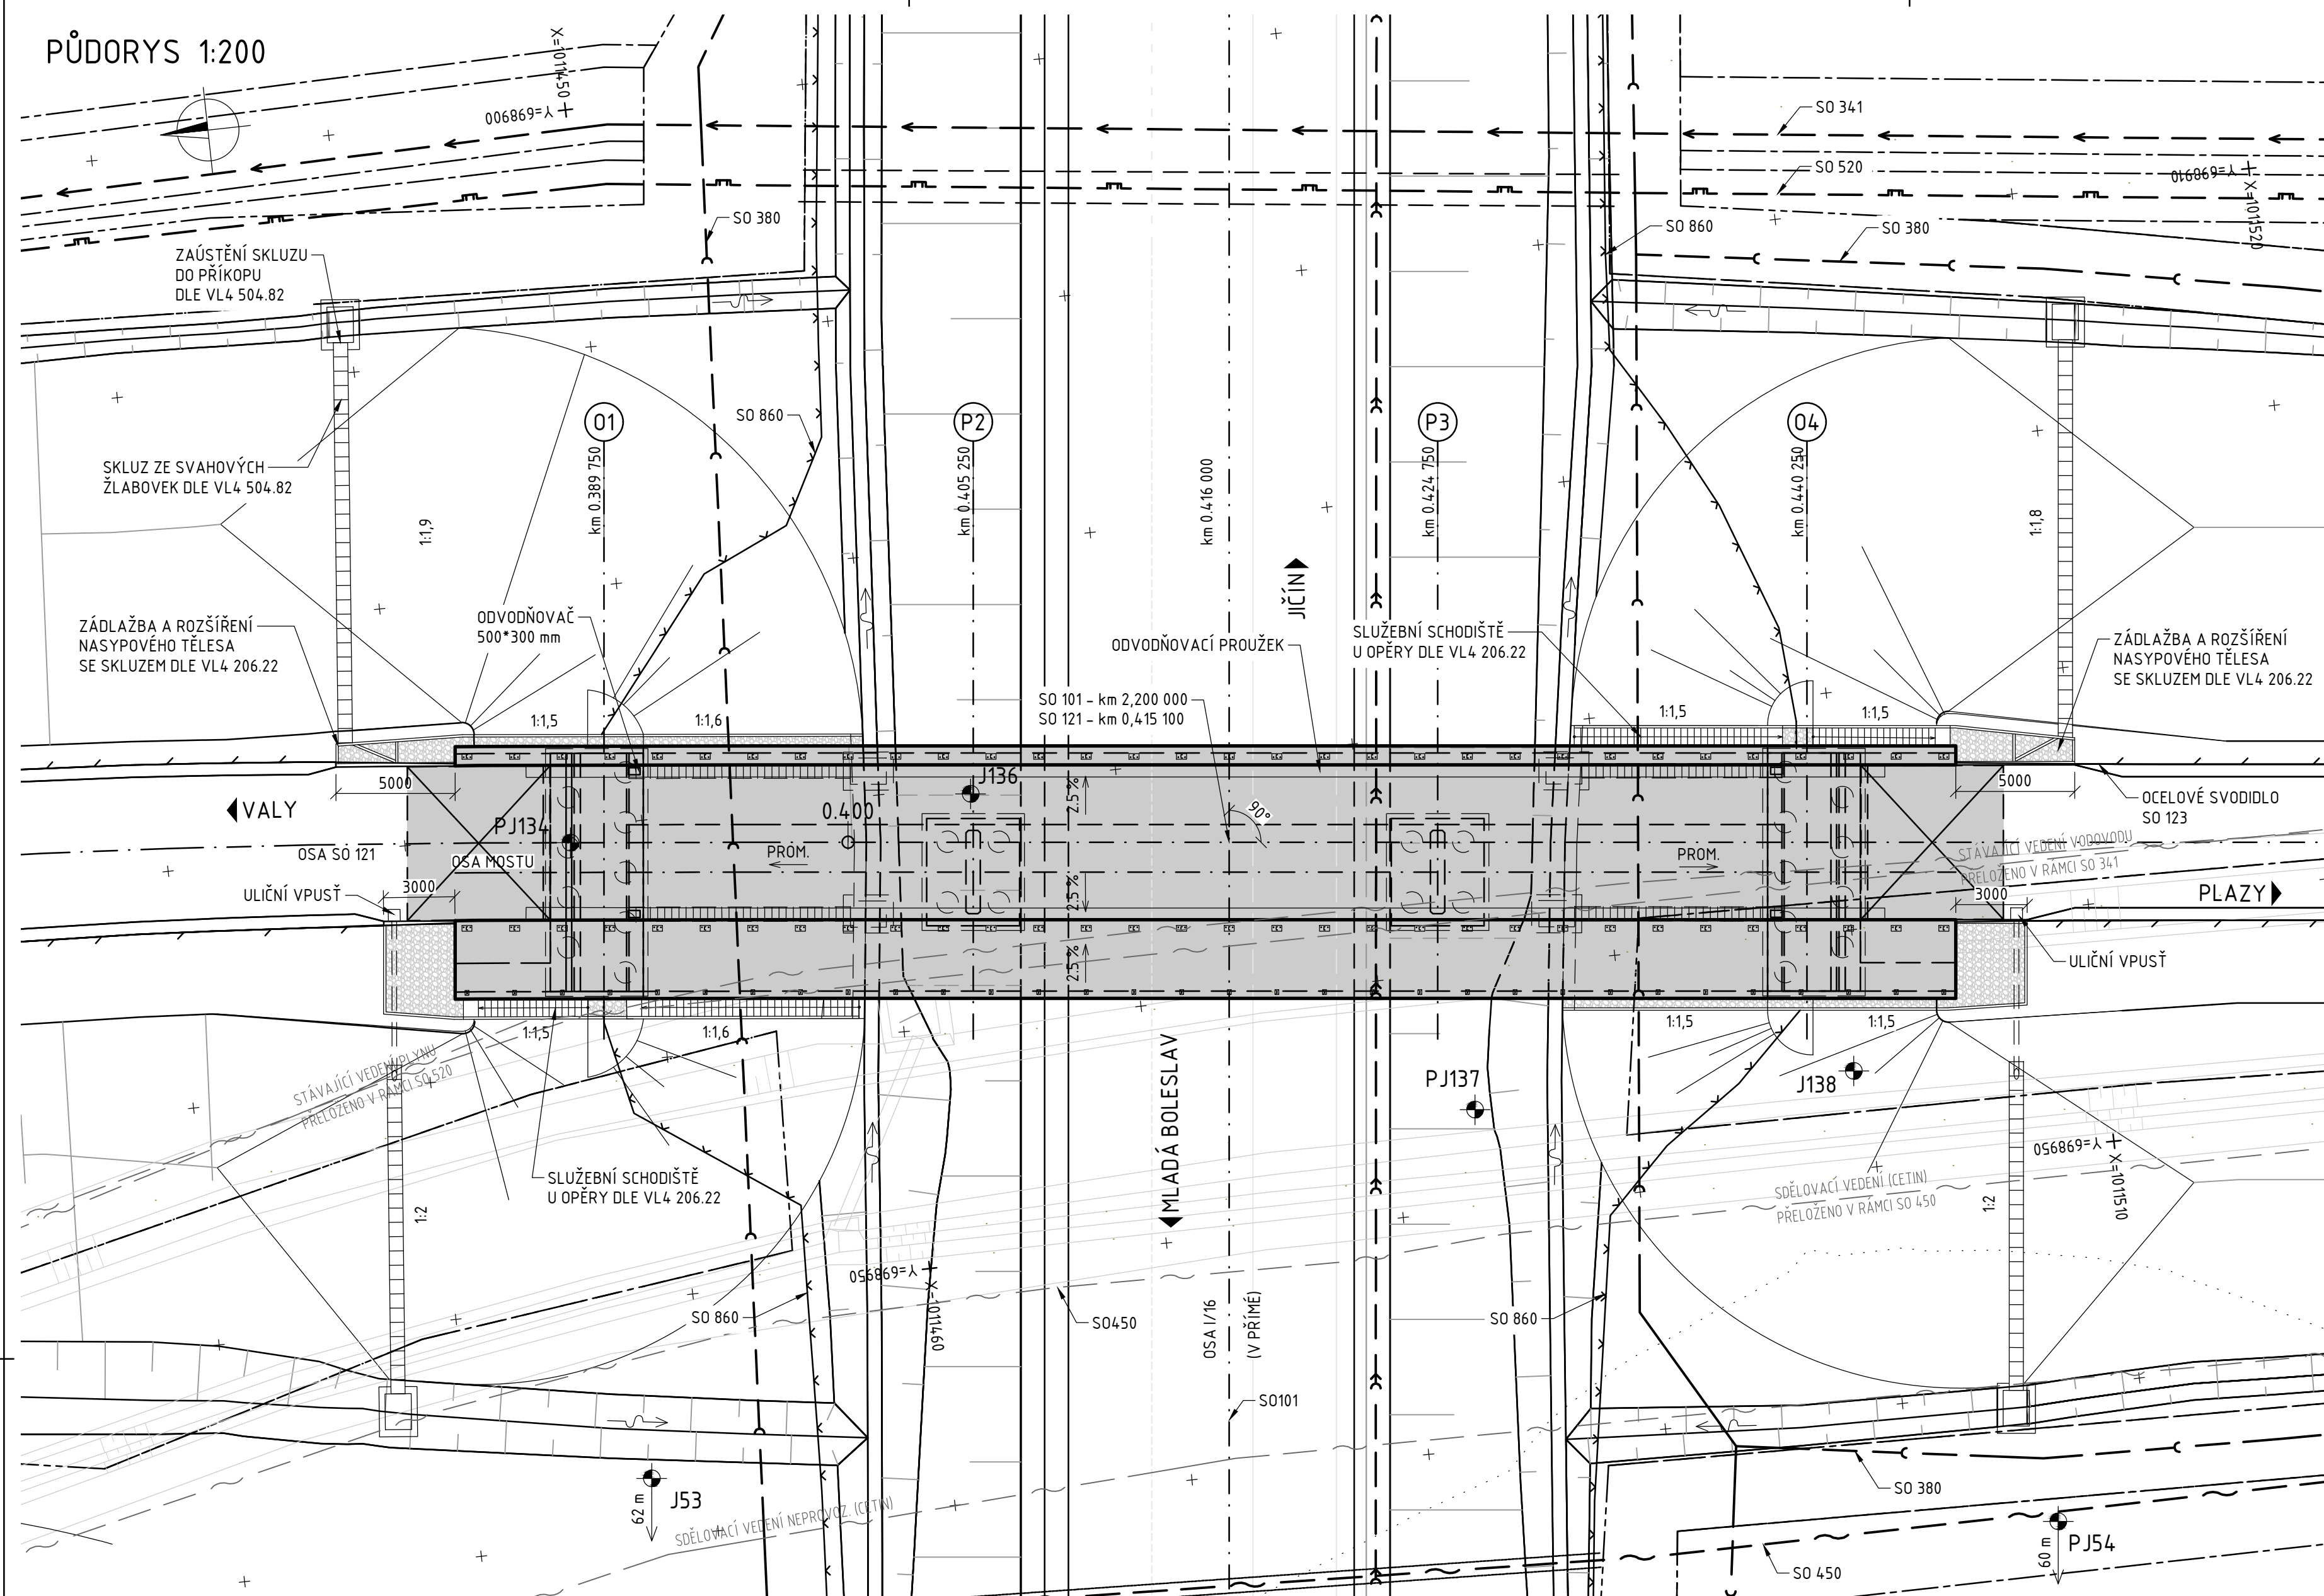


PODÉLNÝ ŘEZ 1:200

V OSE NIVELETY MOSTU

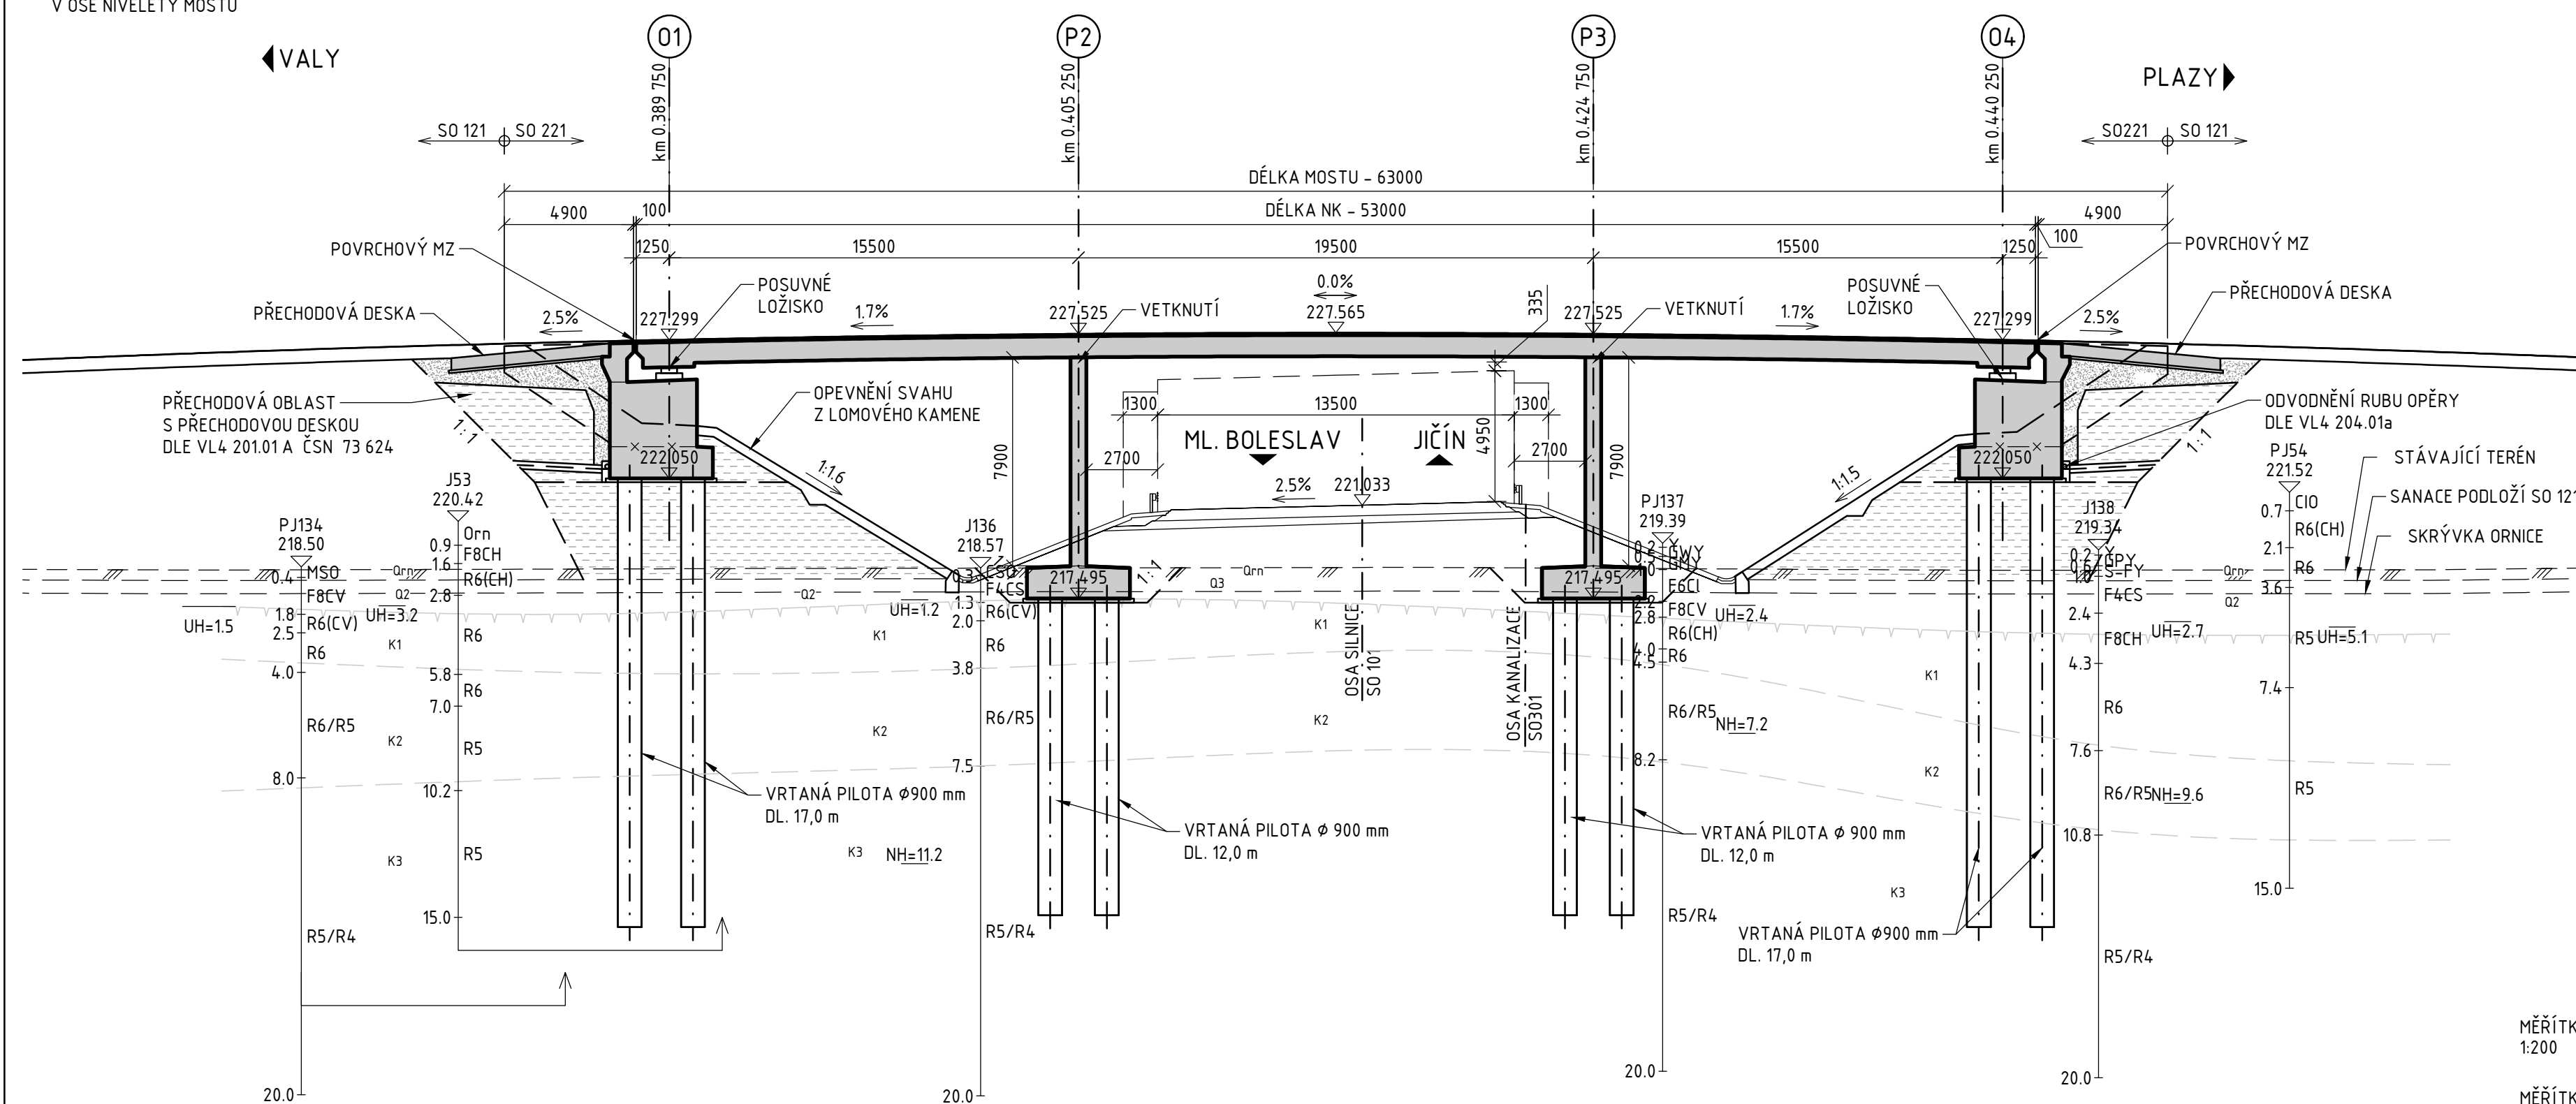


VZOROVÝ PŘÍČNÝ ŘEZ KOLMÝ 1:50


S 6,5/80

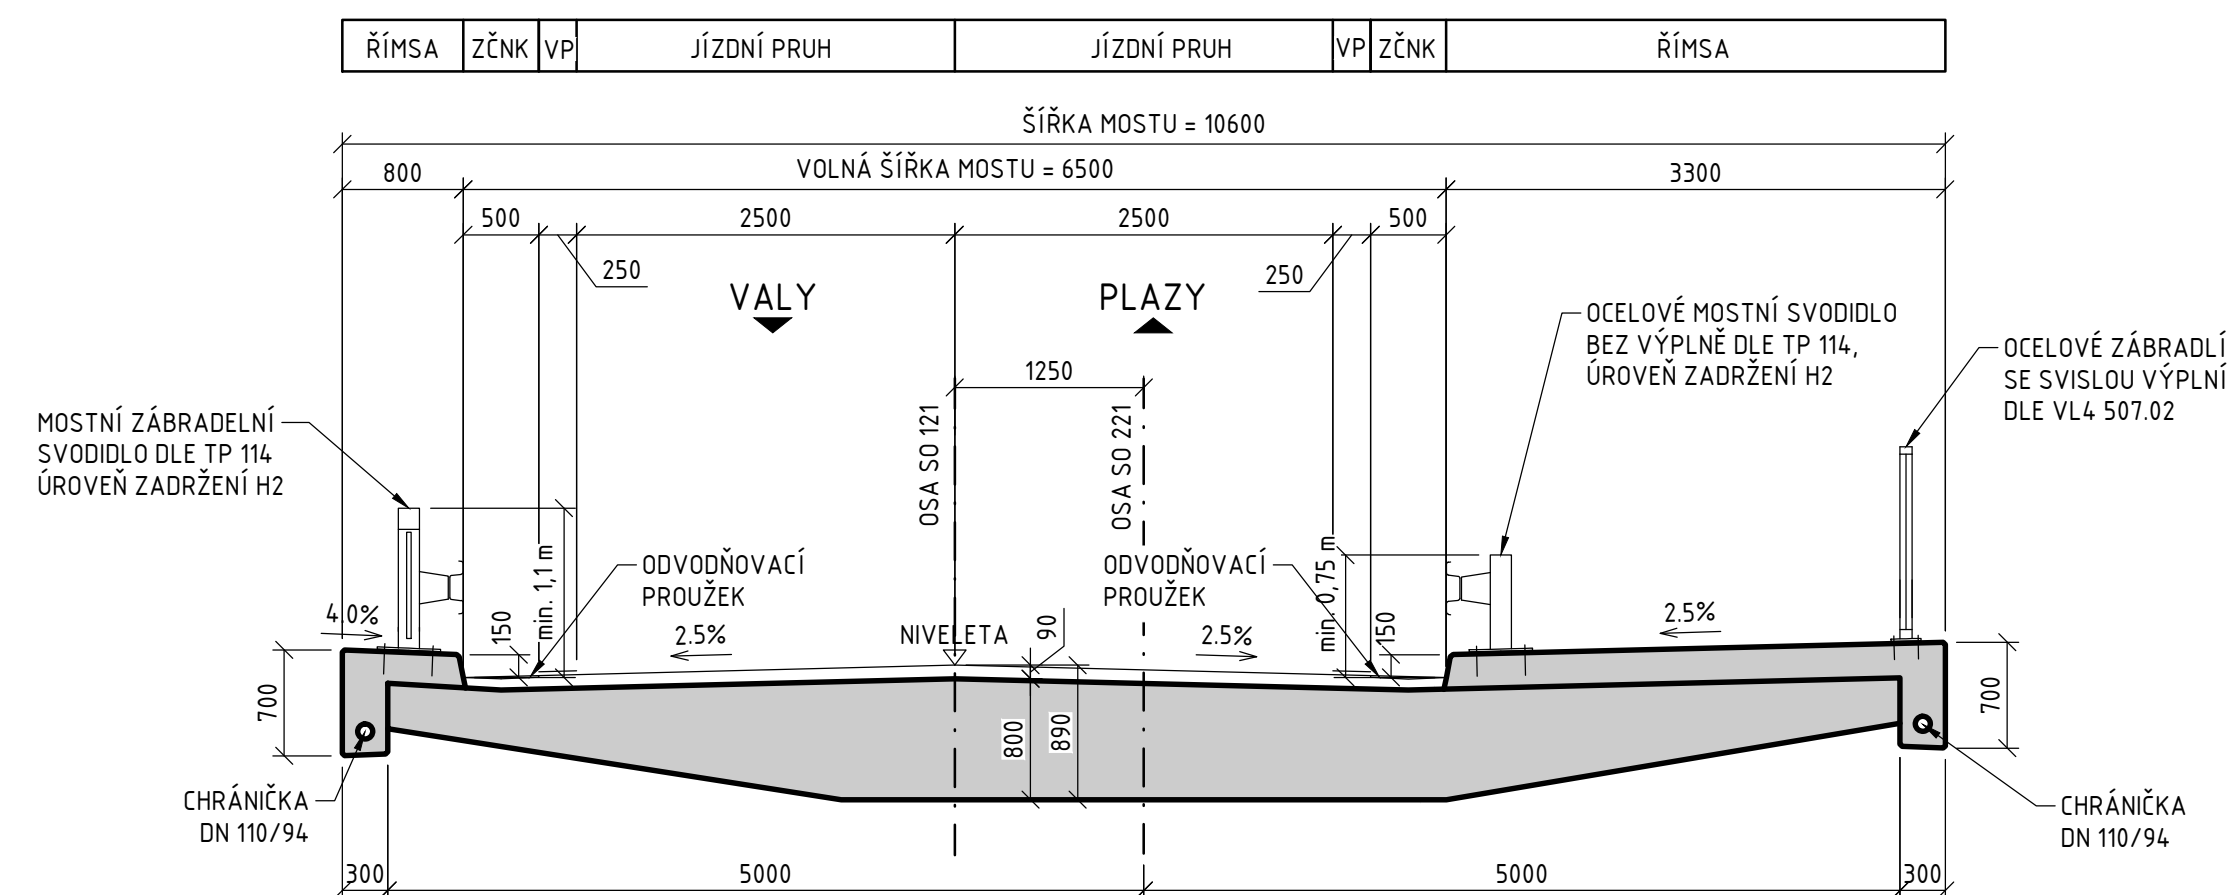

VÝŠKOVÉ VEDENÍ SO 101

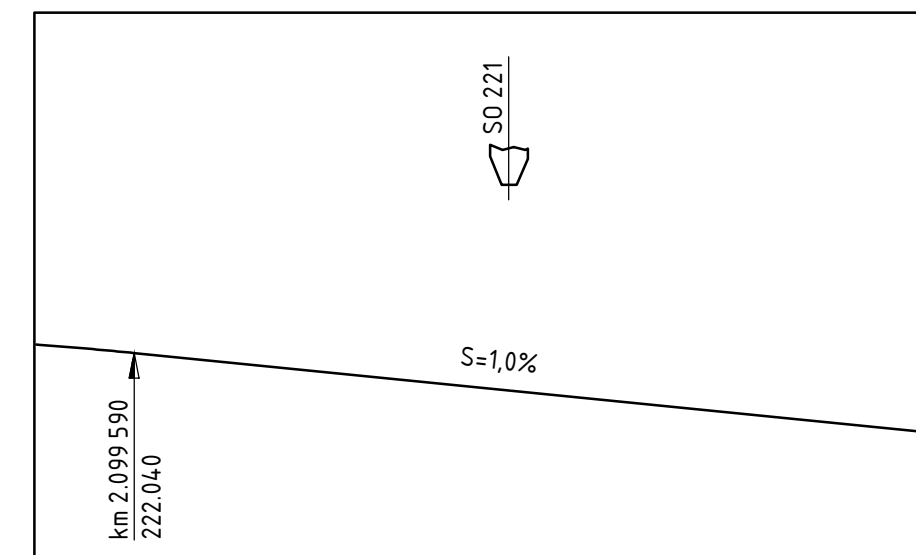

VÝŠKOVÉ VEDENÍ SO 121

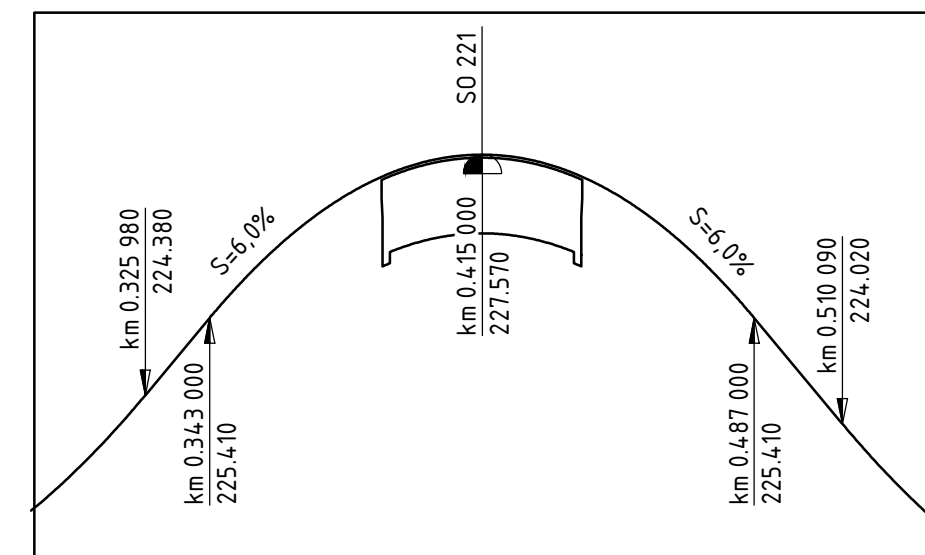

LEGENDA

TRVALÝ ZÁBOR _____

DOČASNÝ ZÁBOR nad 1 rok _____

DOČASNÝ ZÁBOR do 1 roku _____

SMĚROVÉ VEDENÍ SO 101

STANIČENÍ	X	Y	PARAMETR
km 1.699 960	699 430.725	1 011 420.970	PŘÍMÁ
km 2.457 880	698 667.149	1 011 501.983	

SMĚROVÉ VEDENÍ SO 121

STANIČENÍ	X	Y	PARAMETR
km 0.338 780	698 928.571	1 011 397.461	R = 190 m
km 0.346 000	698 928.257	1 011 404.672	A = 97,47
km 0.396 000	698 931.414	1 011 454.533	
km 0.483 280	698 940.744	1 011 541.315	PŘÍMÁ

SOUVISEJÍCÍ OBJEKTY:

- | | |
|----------|--|
| SO 020 | PŘÍPRAVA ÚZEMÍ |
| SO 101 | SILNICE I/16 MLADÁ BOLESLAV-MARTINOVICE |
| SO 121 | PŘELOŽKA SILNICE III/2768 V KM 2,200 |
| SO 151 | PŘÍSTUPY NA POZEMKY V K.Ú. PLÁZY |
| SO 190 | DOPRAVNÍ ZNAČENÍ |
| SO 301.x | ODVODNĚNÍ I/16 |
| SO 341 | PŘELOŽKA VODOVODU PE 110 V KM 2.195 |
| SO 380 | ÚPRAVY MELIORACÍ ZÚ – KÚ |
| SO 450 | PŘELOŽKA VEDENÍ SEK – DOK CETIN KM 2,188 |
| SO 520 | PŘELOŽKA STL PLYNU V KM 2,225 |
| SO 801 | VEGETAČNÍ ÚPRAVY |
| SO 810 | KÁCENÍ ZELENĚ |
| SO 830 | REKULTIVACE PLOCH DOČASNÉHO ZÁBORU |
| SO 860 | OPLOČENÍ |

Souřadnicový systém: S-JTSK
Výškový systém: Bpv

SO 221 NADJEZD PŘELOŽKY III/2768 V KM 2,200	
Objednatel:  ŘEDITELSTVÍ SILNIC A DÁLNIC	Ředitelství silnic a dálnic s. p. Čerčanská 2023/12, Krč, 140 00 Praha 4

	Valbek, spol. s r.o. Vaňurova 505/17 460 07 Liberec 3
---	---

	Vypracoval	ING. S. RUŽIČKA	<i>[Signature]</i>	Zak. číslo	21-L13-101
	Zodp. projektant	ING. S. RUŽIČKA	<i>[Signature]</i>	Datum	02/2025
	Tech. kontrola	ING. I. BELDA	<i>[Signature]</i>	Stupeň	PDPS
	Akce			Počet formátů	8x A4
	I/16 MLADÁ BOLESLAV - MARTINOVICE			Měřitko	1:200,50
Zhotovitel: Valbek, spol. s r.o. Valburska 565/17 460 07 Liberec 3	Příloha	PŮDORYS, PODÉLNÝ ŘEZ VZOROVÝ PŘÍČNÝ ŘEZ		Č. přílohy	Paré
				102	

