




POHLED 2 1 : 100, 01

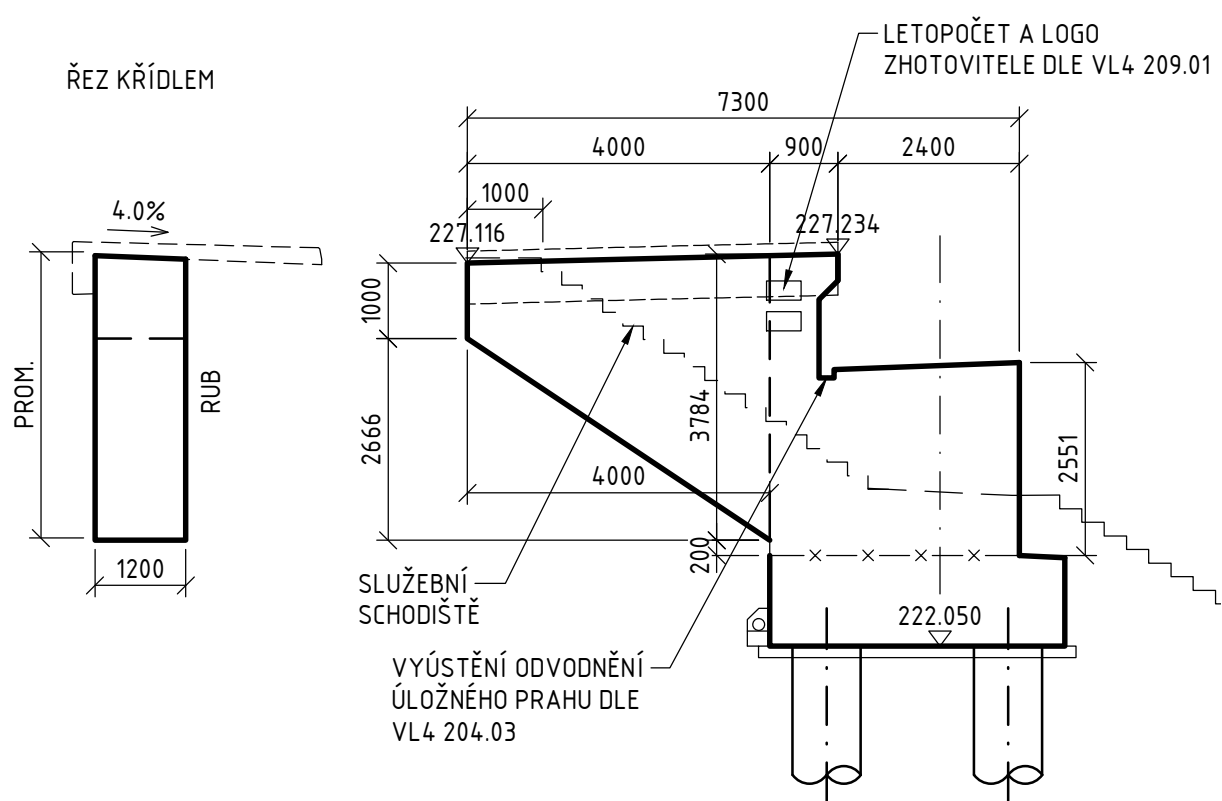


OPĚRA 01
ŘEZ A-A 1:100

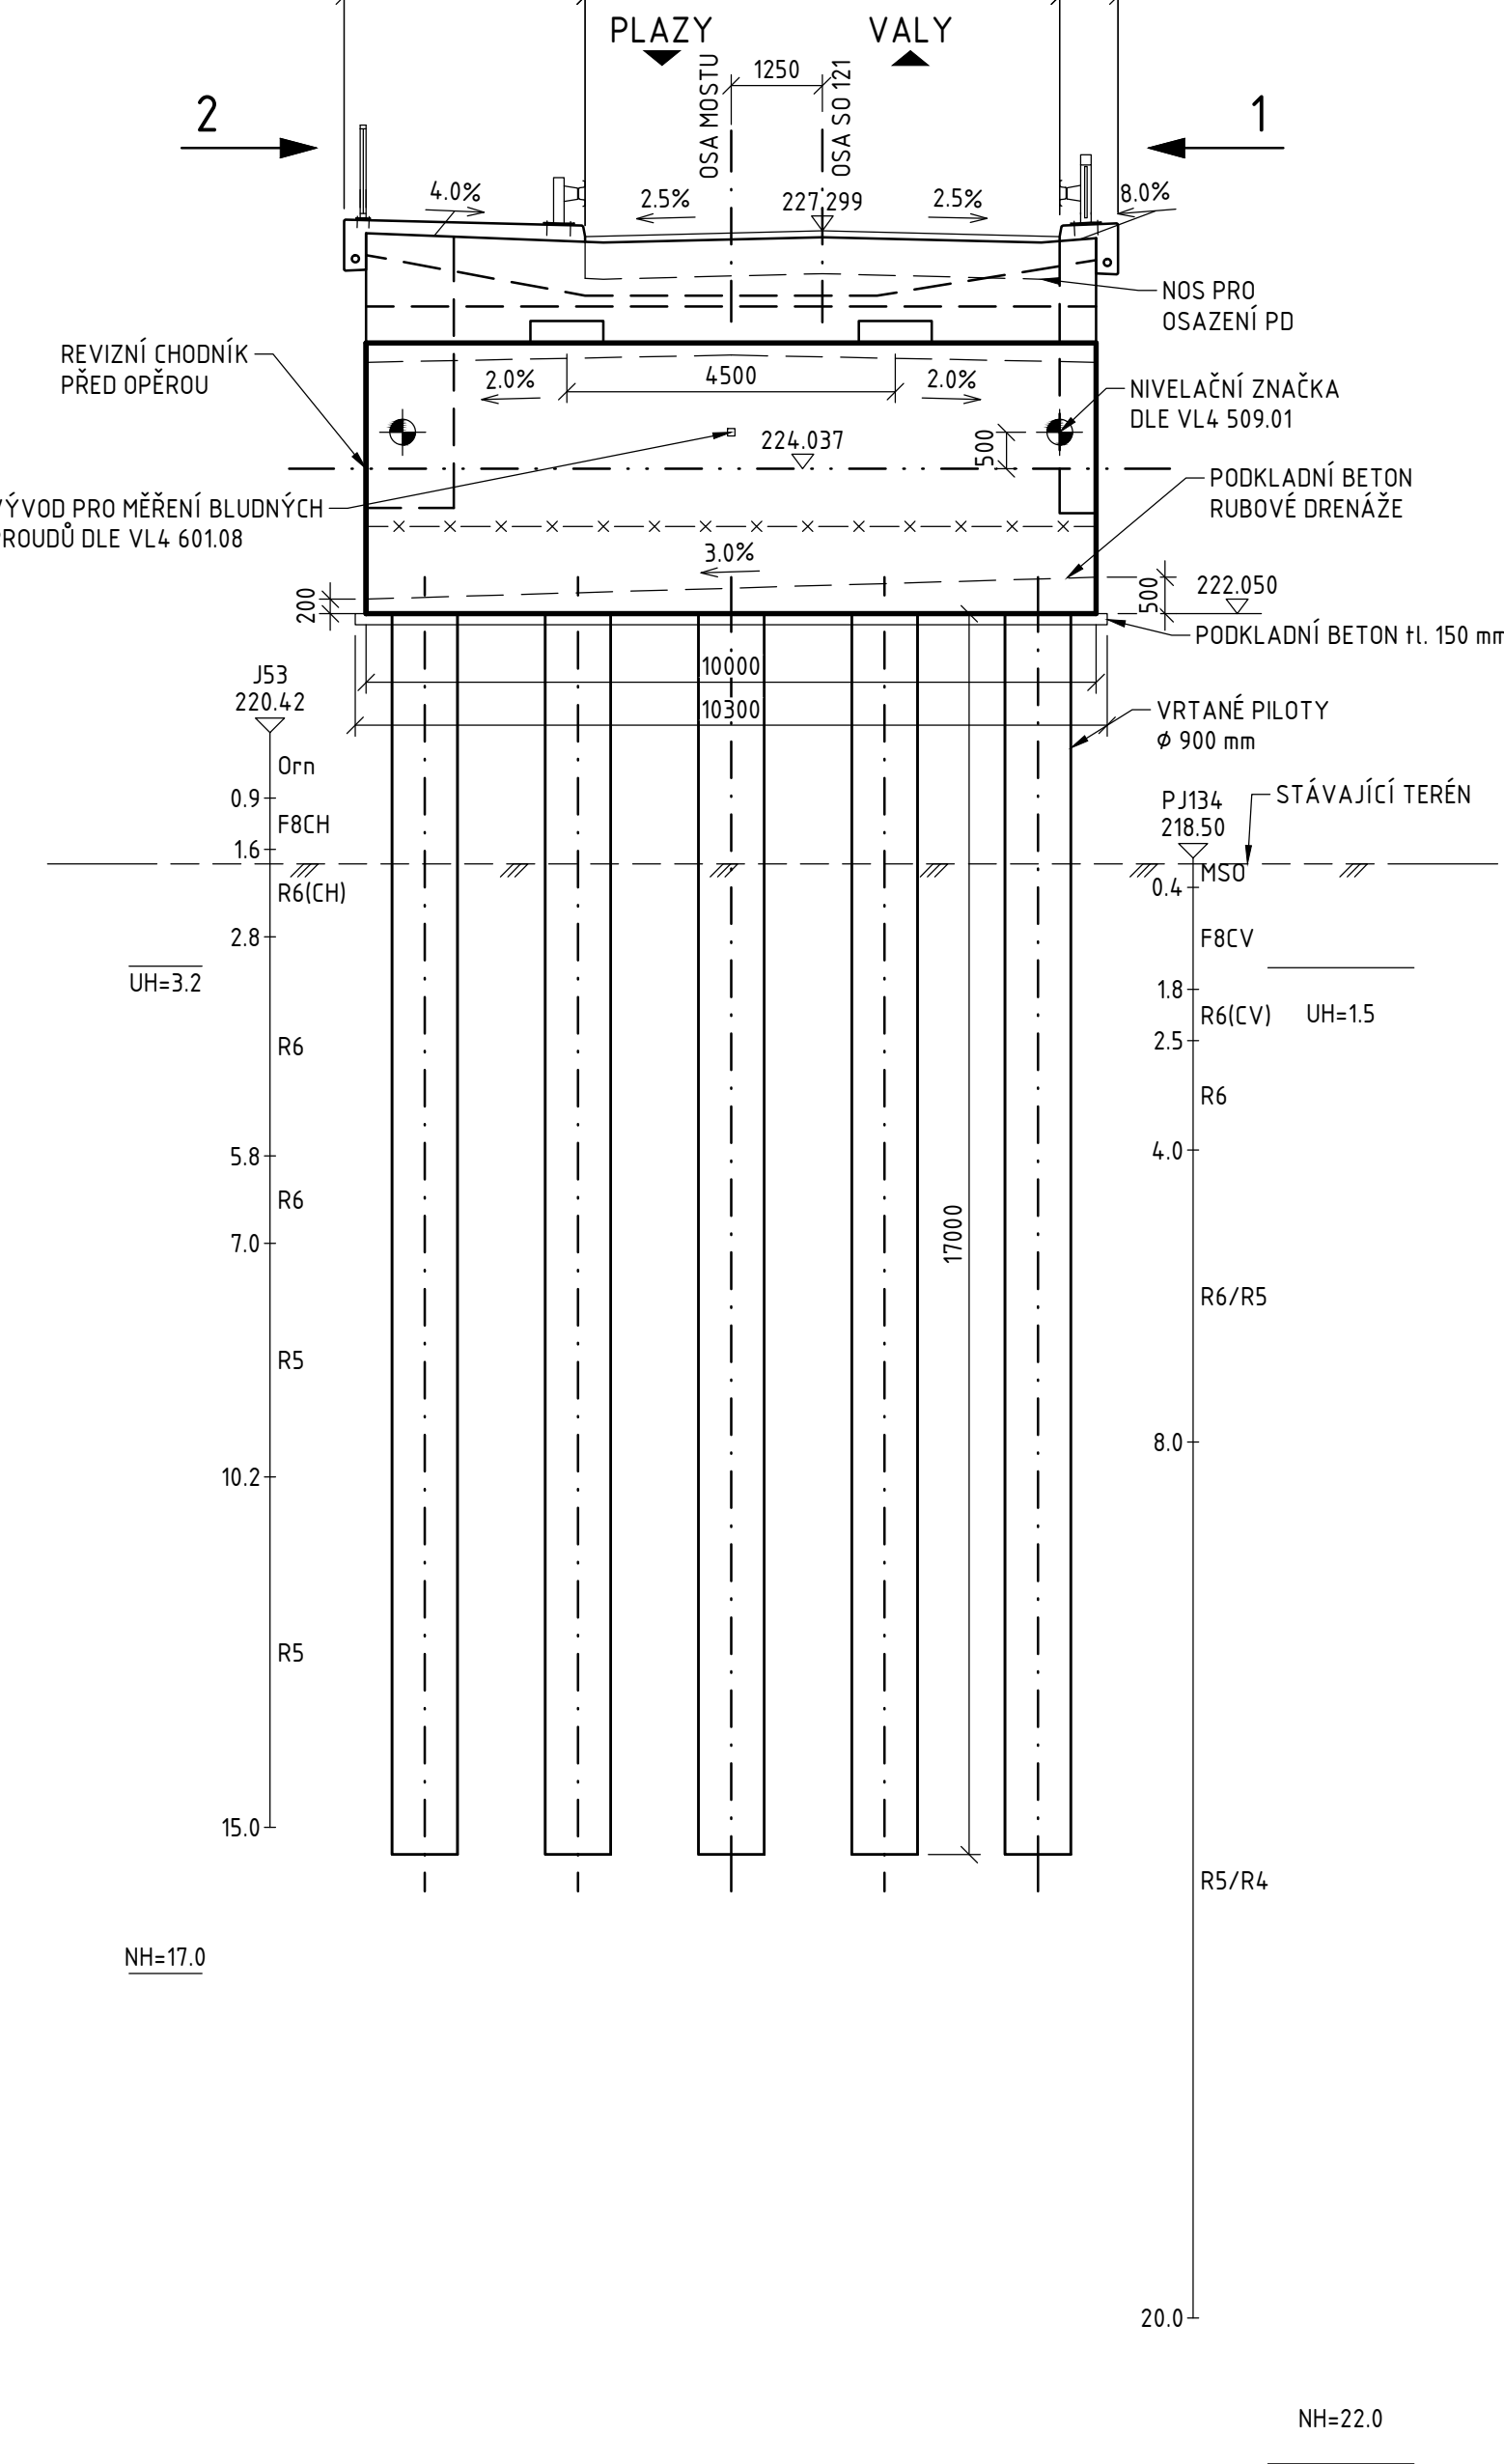

ŘEZ B-B 1:100, 01

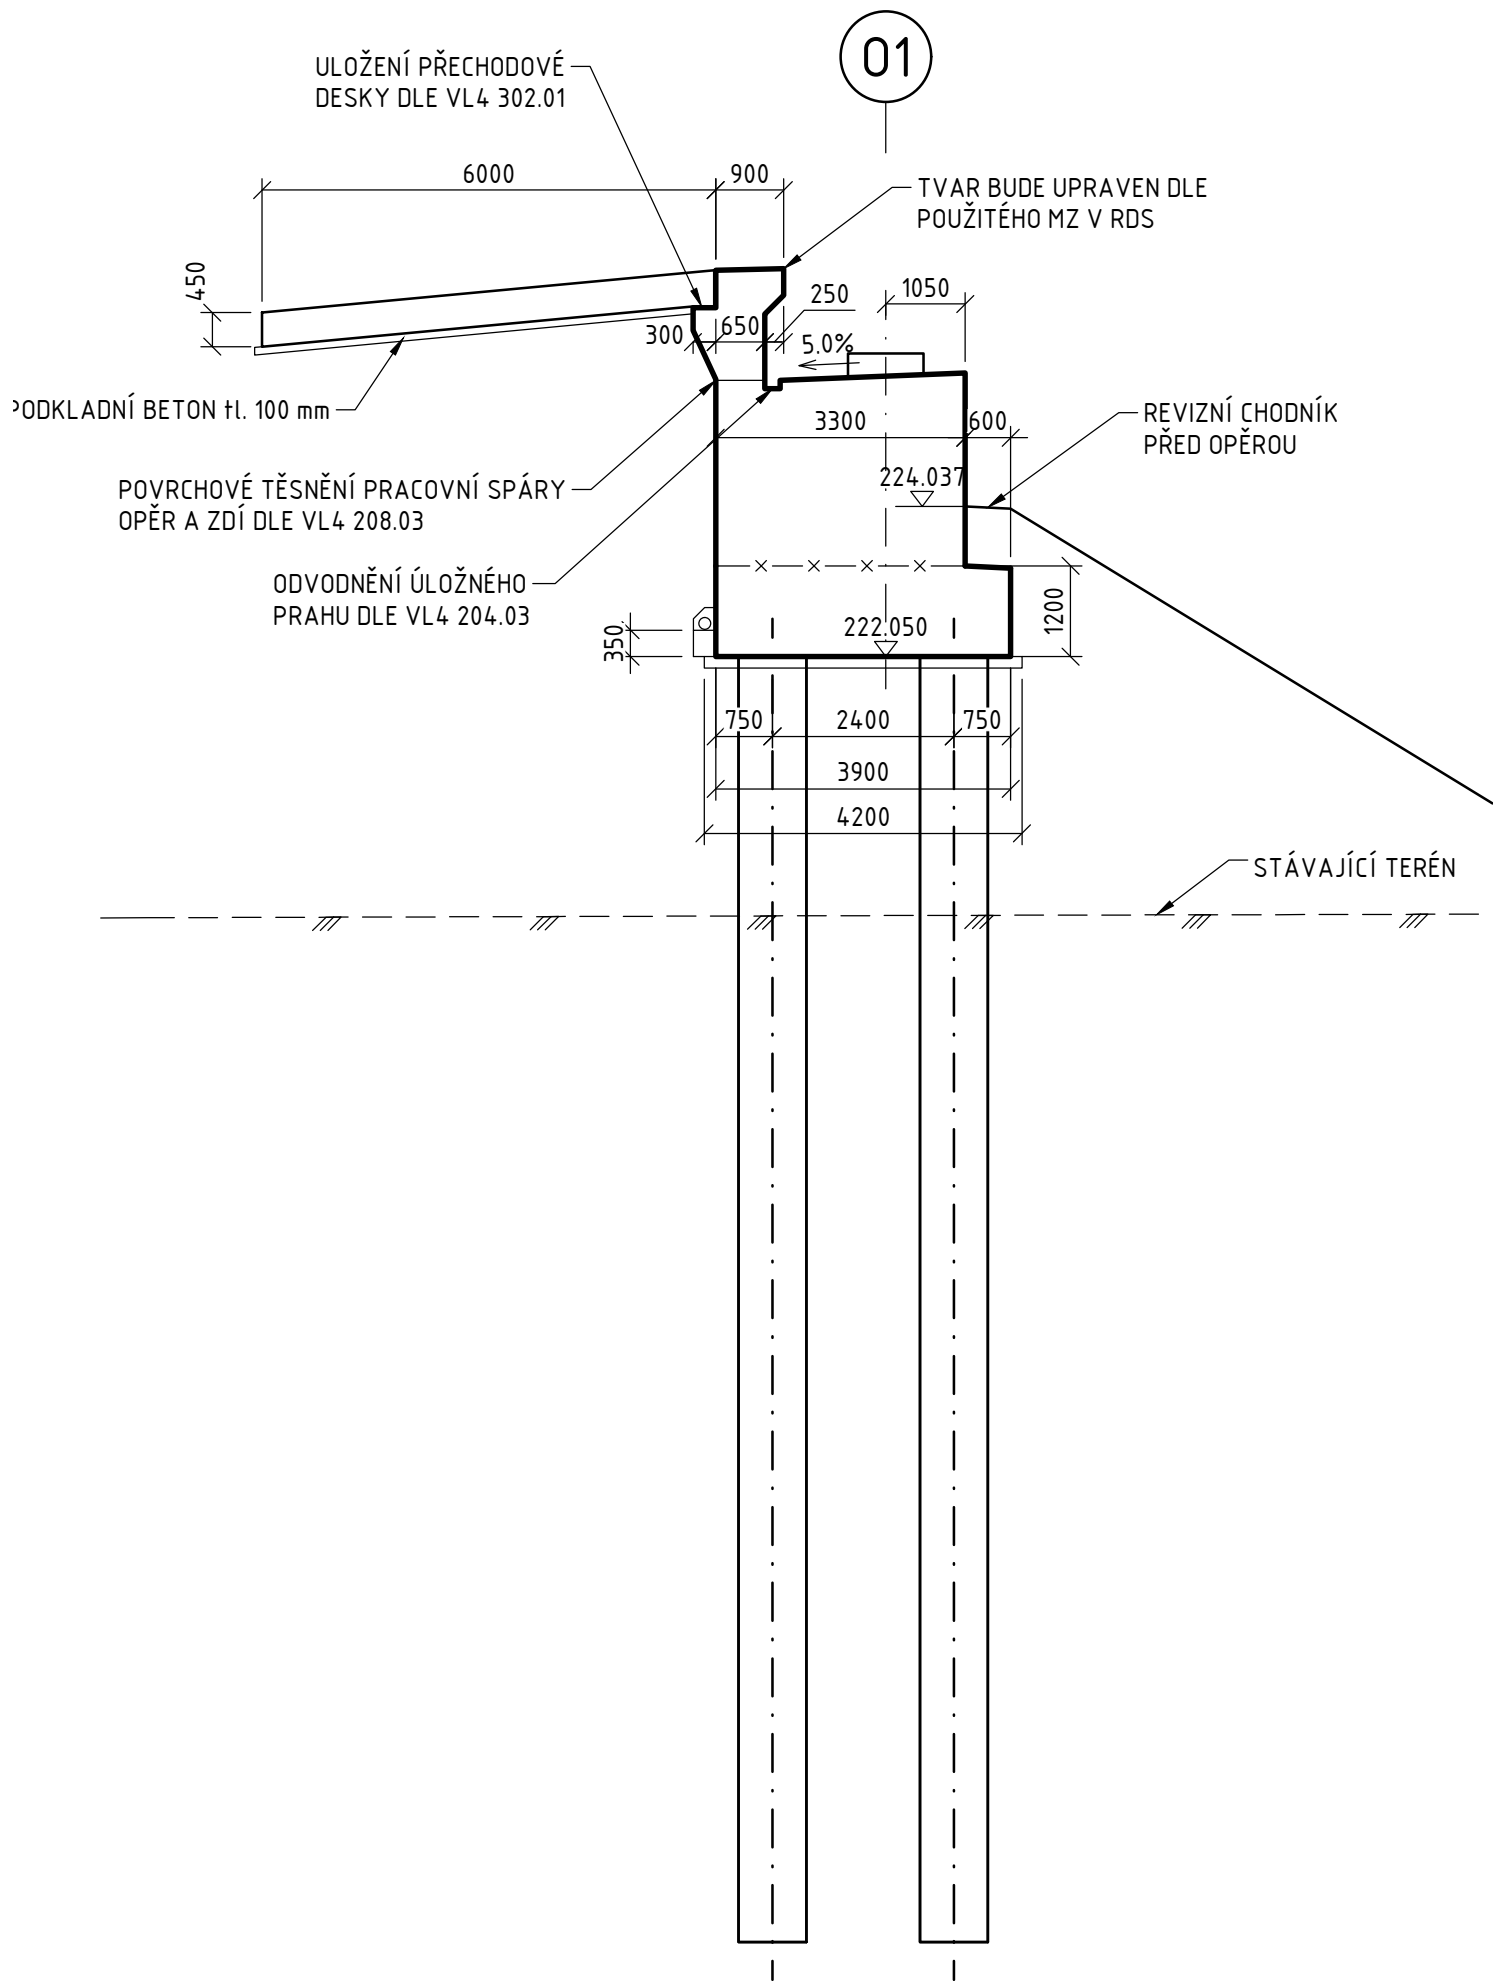


POHLED 1 1 : 100, 01

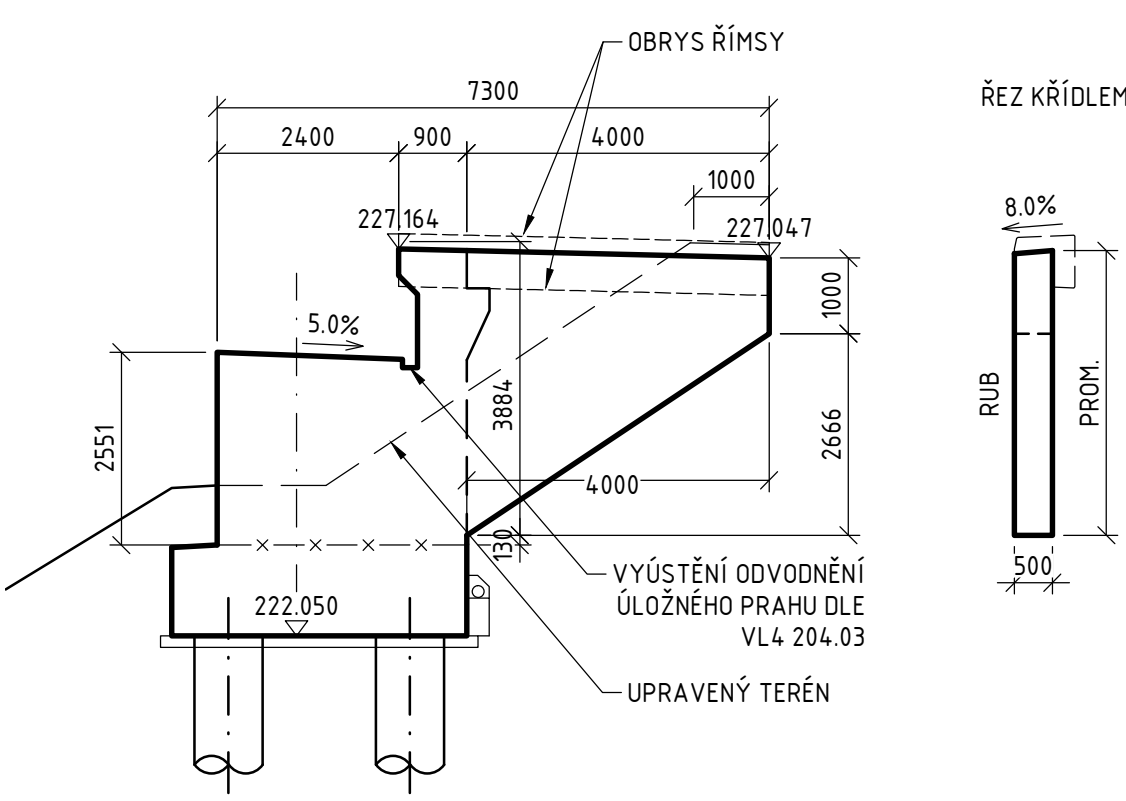

POZNÁMKY:
- NEDÍLNOU SOUČÁSTÍ VÝKRESU JSOU POZNÁMKY A SPECIFIKACE UVEDENÉ NA VÝKRESE POZNÁMEK A TECHNICKÝCH SPECIFIKACÍ

PŮDORYS ZÁKLADU 1 : 100

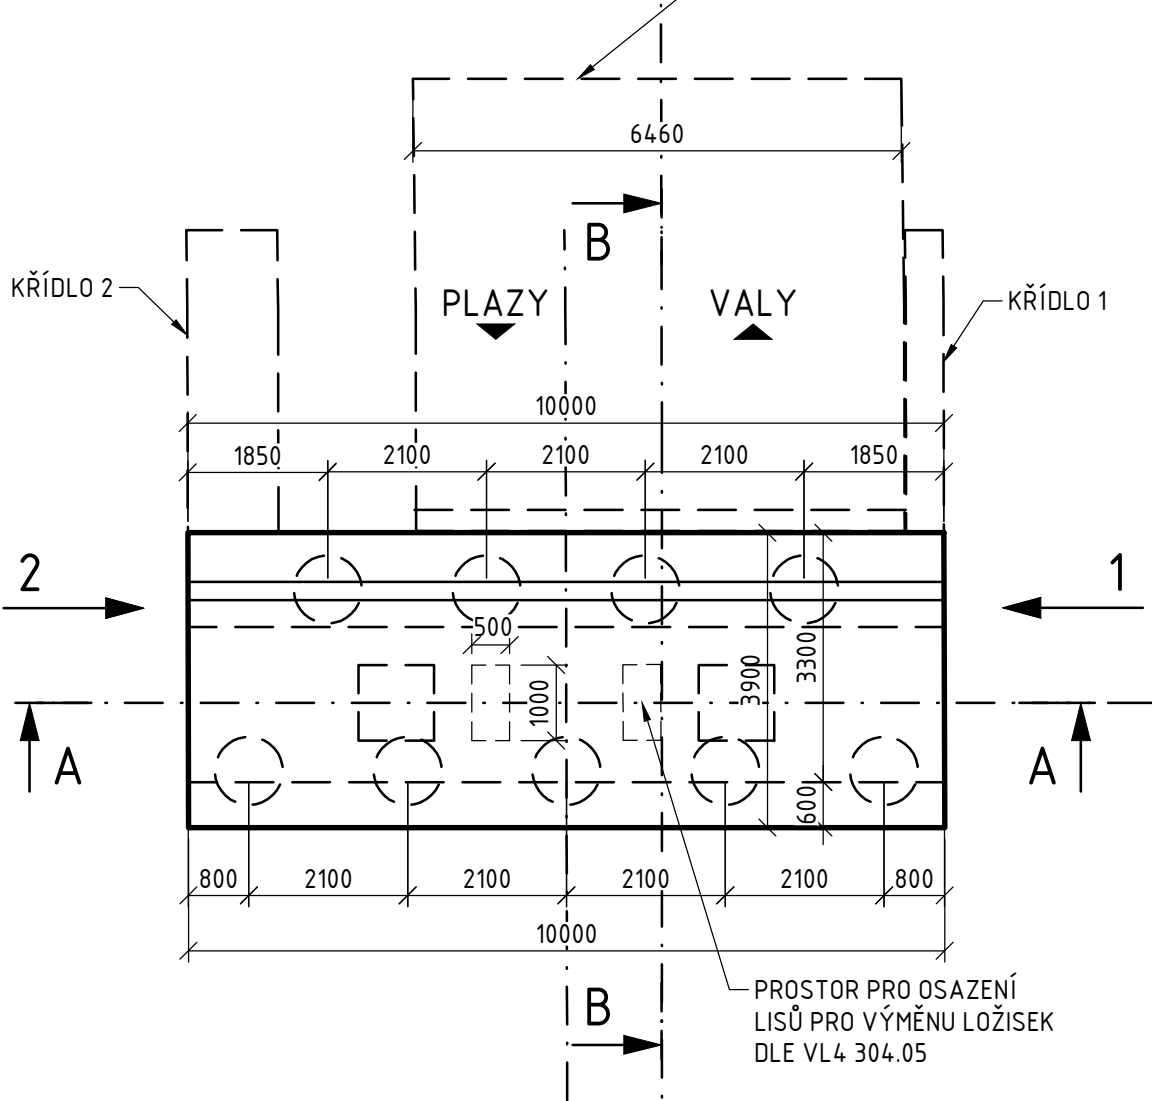

Souřadnicový systém: S-JTSK Výškový systém: Bpv					
SO 221 NADJEZD PŘELOŽKY III/2768 V KM 2,200					
Objednatel: Ředitelství silnic a dálnic s. p. Čerčanská 2023/12, Krč, 140 00 Praha 4					
Valbek, spol. s r.o. Vaňurova 505/17 460 07 Liberec 3					
	Vypracoval	M. KNESPLOVÁ		Zak. číslo	21-L113-001
	Zodp. projektant	ING. S. RŮŽIČKA		Datum	02/2025
	Tech. kontrola	ING. I. BELDA		Stupeň	PDPS
	Akce	I/16 MLADÁ BOLESLAV - MARTINOVICE		Počet formátů	8x A4
	Zhotovitel: Valbek, spol. s r.o. Vaňurova 505/17 460 07 Liberec 3	Příloha	HLUBINNÉ ZALOŽENÍ, TVAR OPĚRY 01	Měřítko	1:100
				Č. přílohy	Paré
			202		

