




POHLED 2 1:100, 04

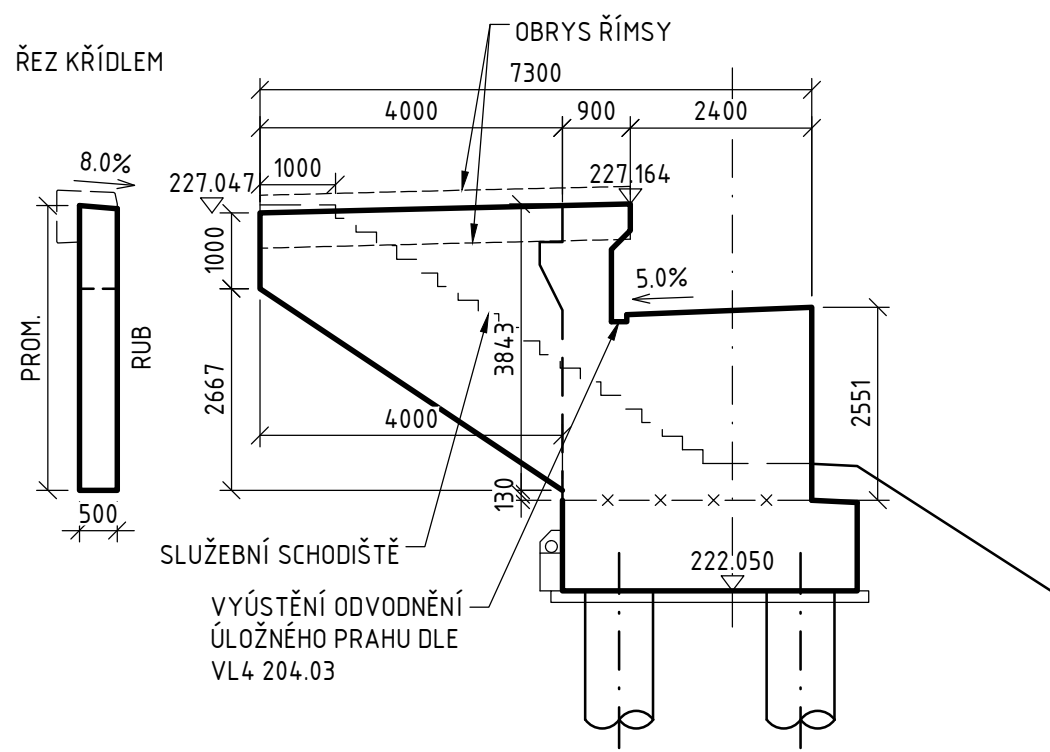


OPĚRA 04
ŘEZ A-A 1:100
OSOÚ ULOŽENÍ 04

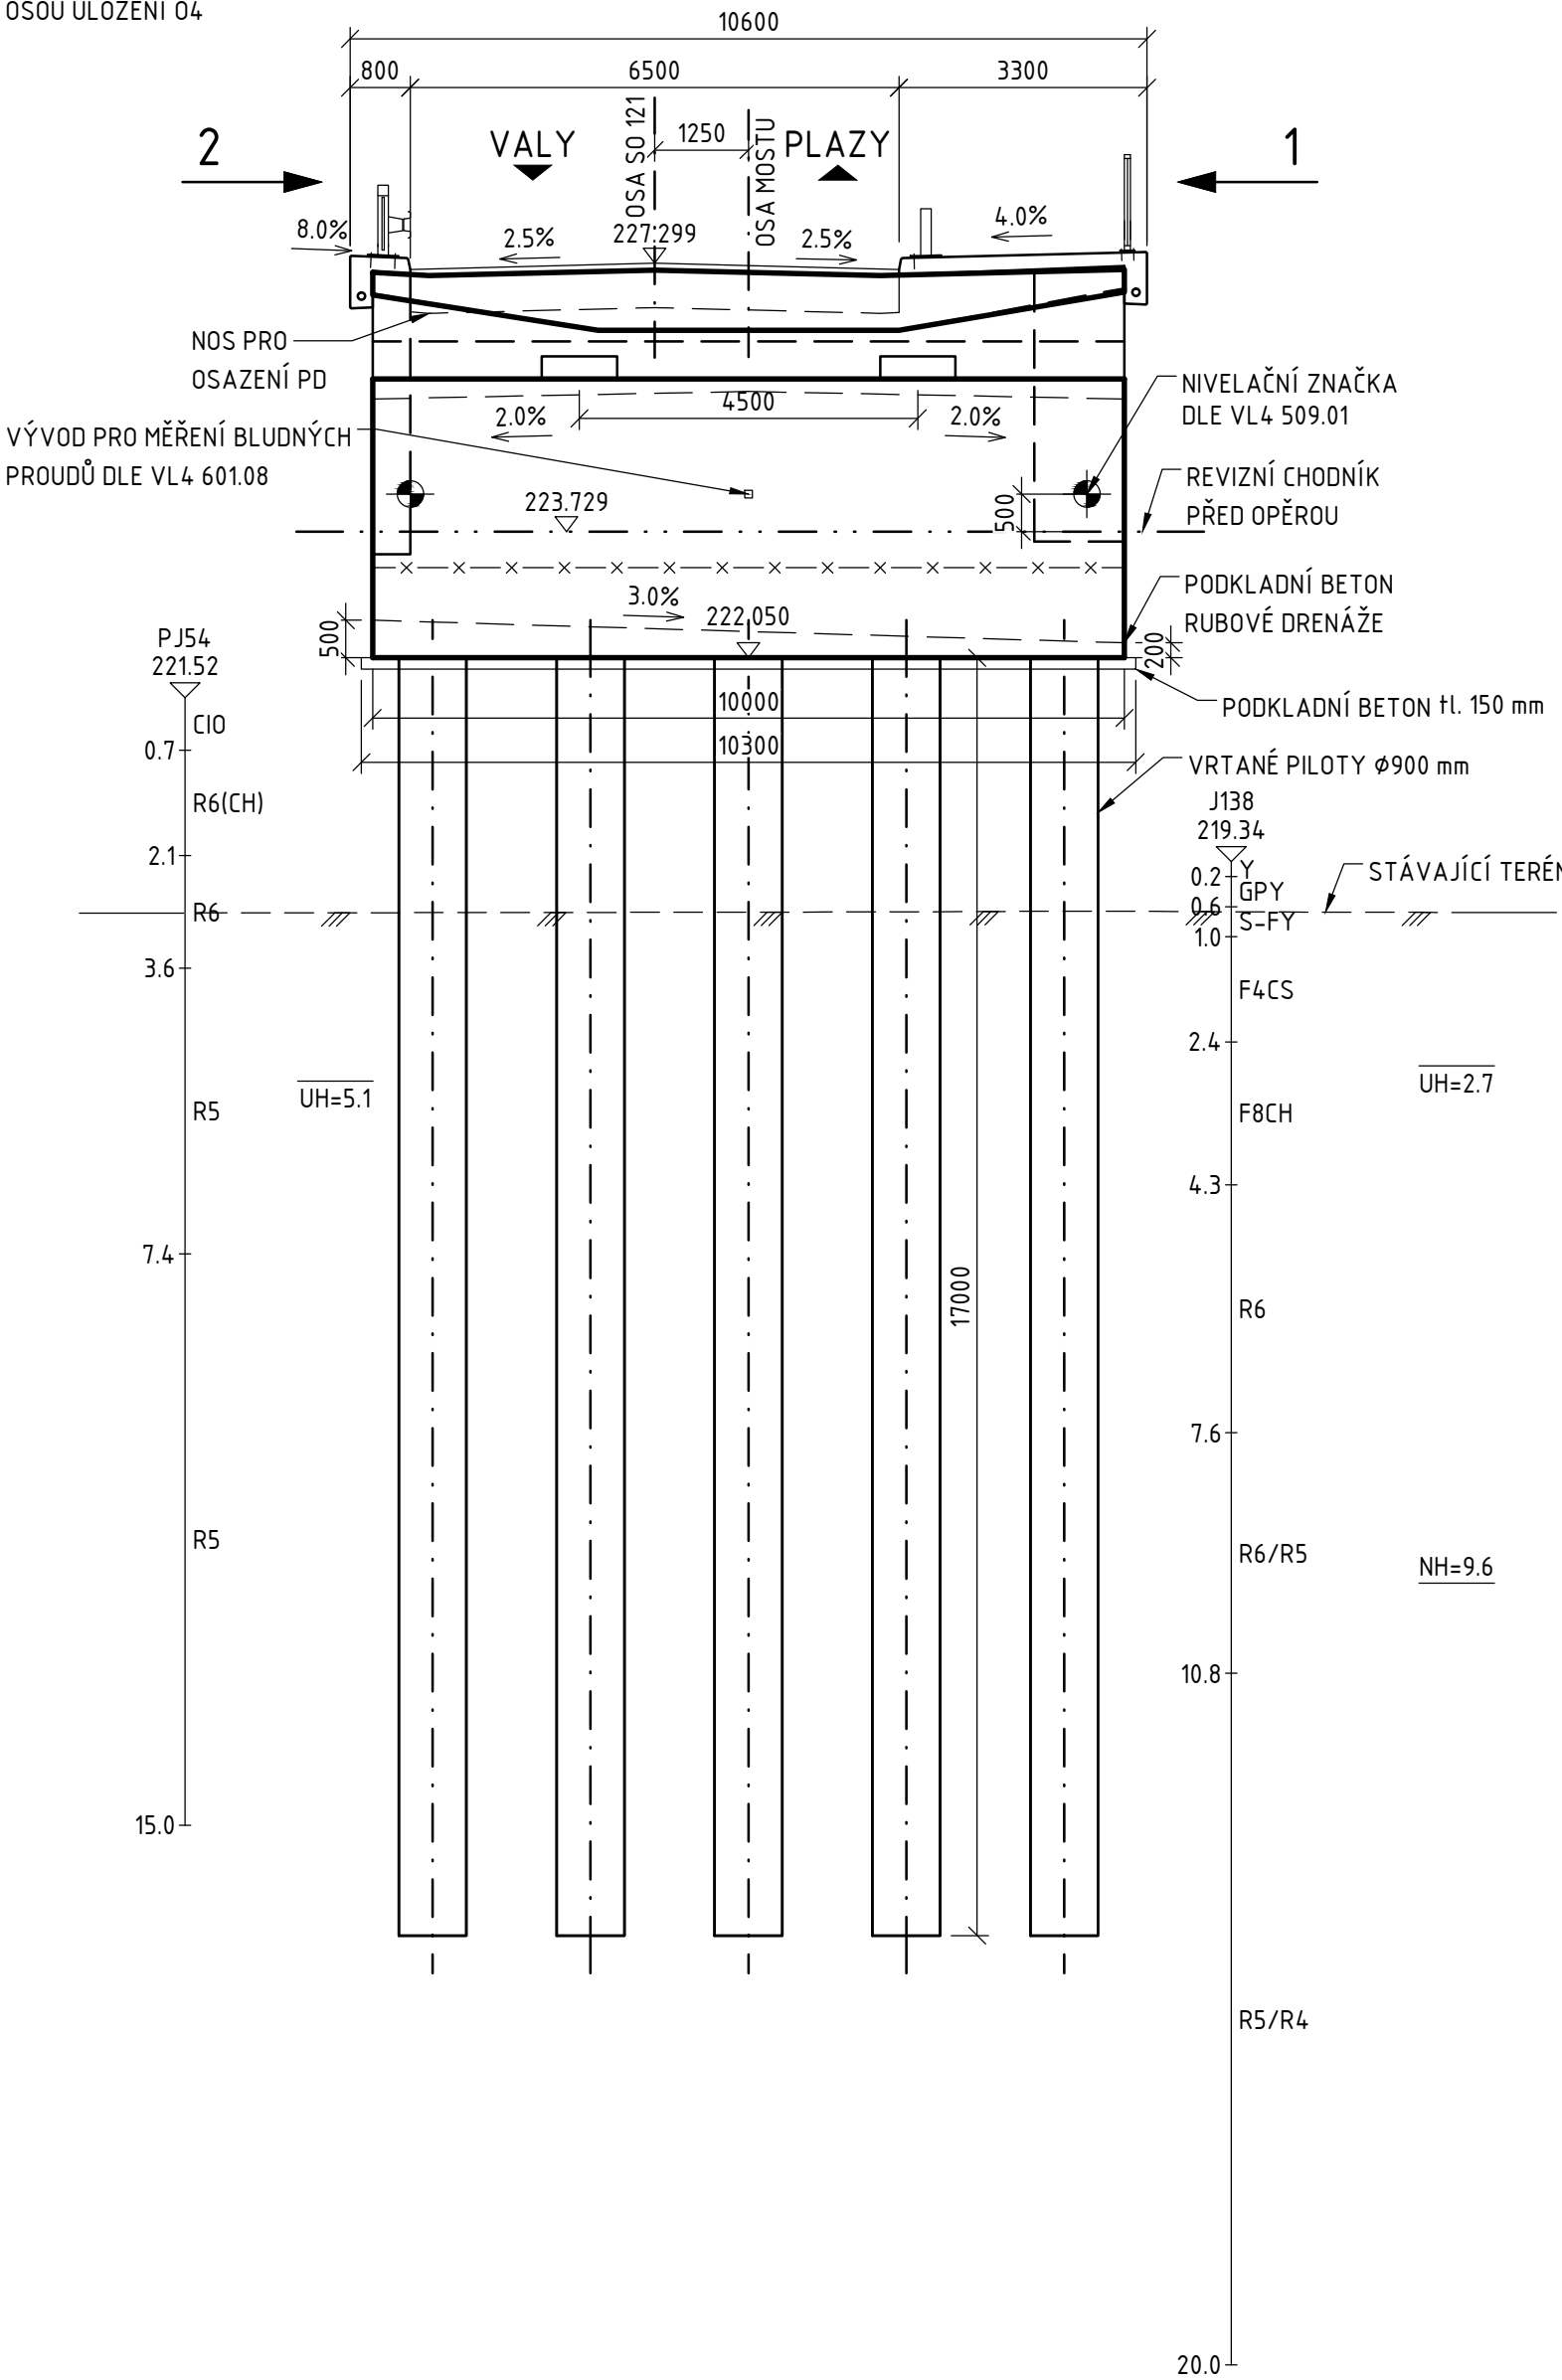

ŘEZ B-B 1:100, 04


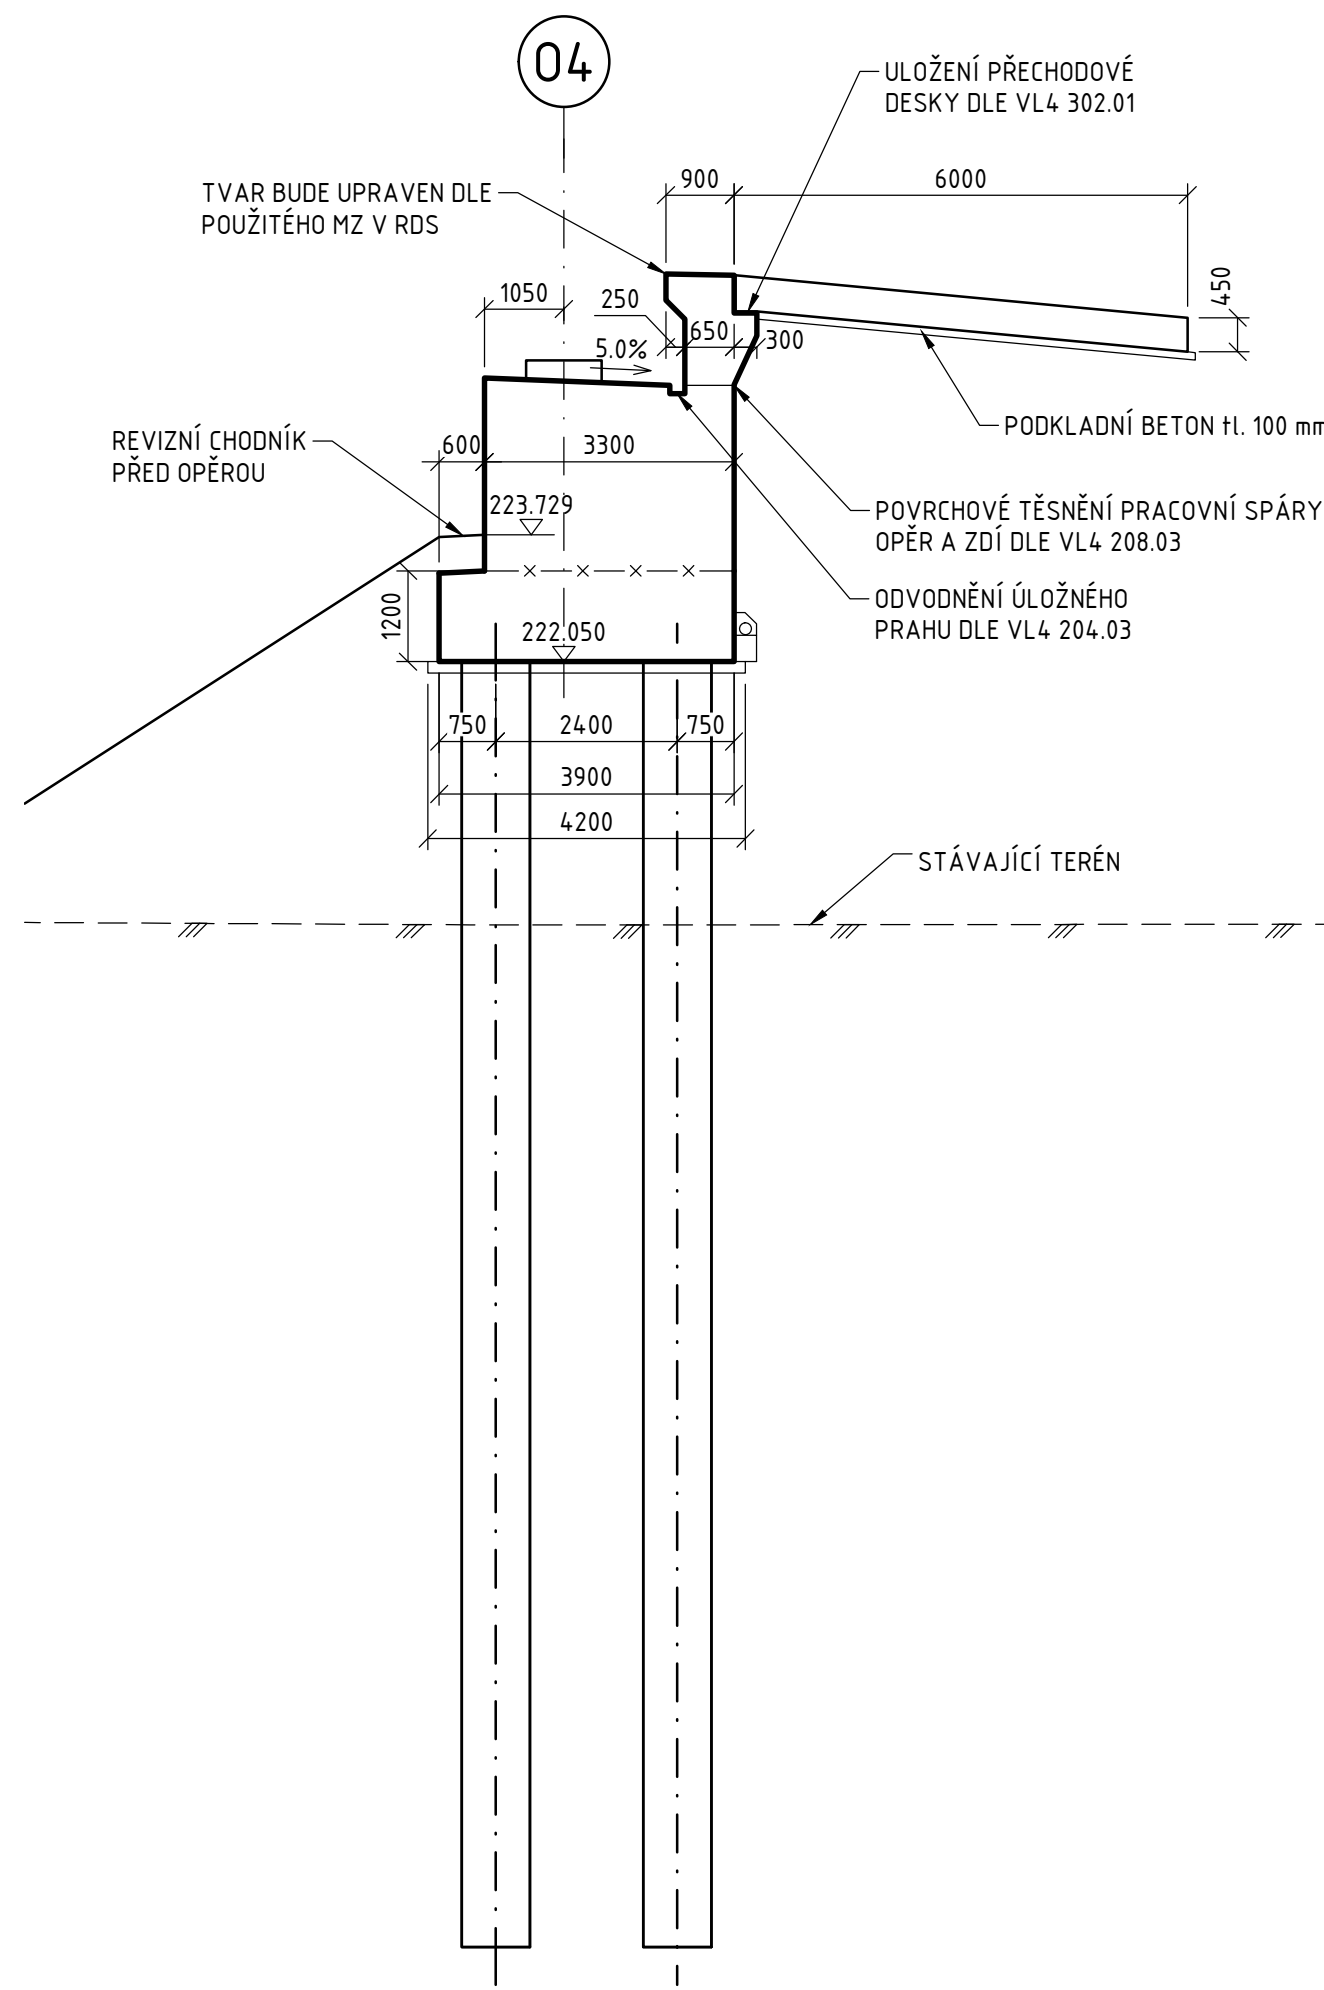


POHLED 1 1:100, 04

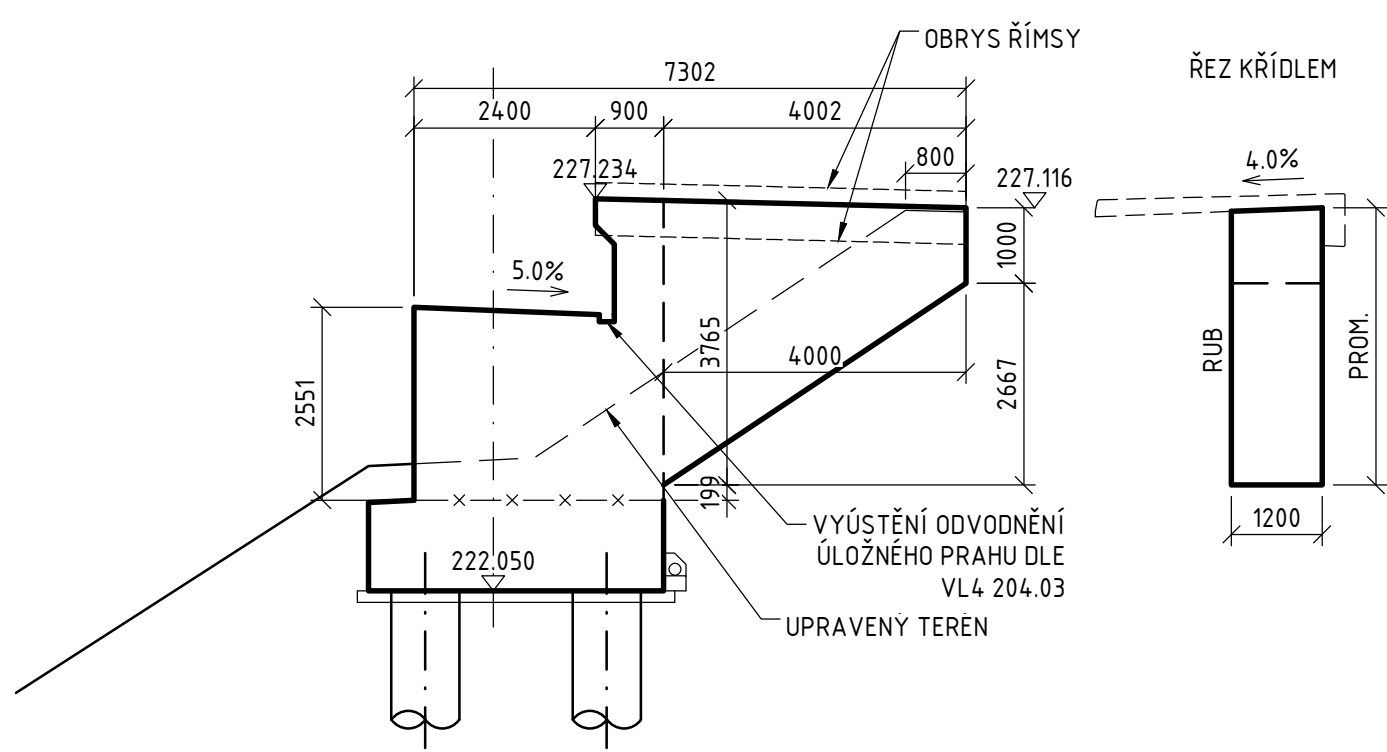

POZNÁMKY:
- NEDÍLNOU SOUČÁSTÍ VÝKRESU JSOU POZNÁMKY A SPECIFIKACE UVEDENÉ NA VÝKRESE POZNÁMEK A TECHNICKÝCH SPECIFIKACÍ

PŮDORYS ZÁKLADU 1: 100

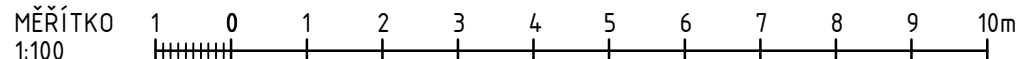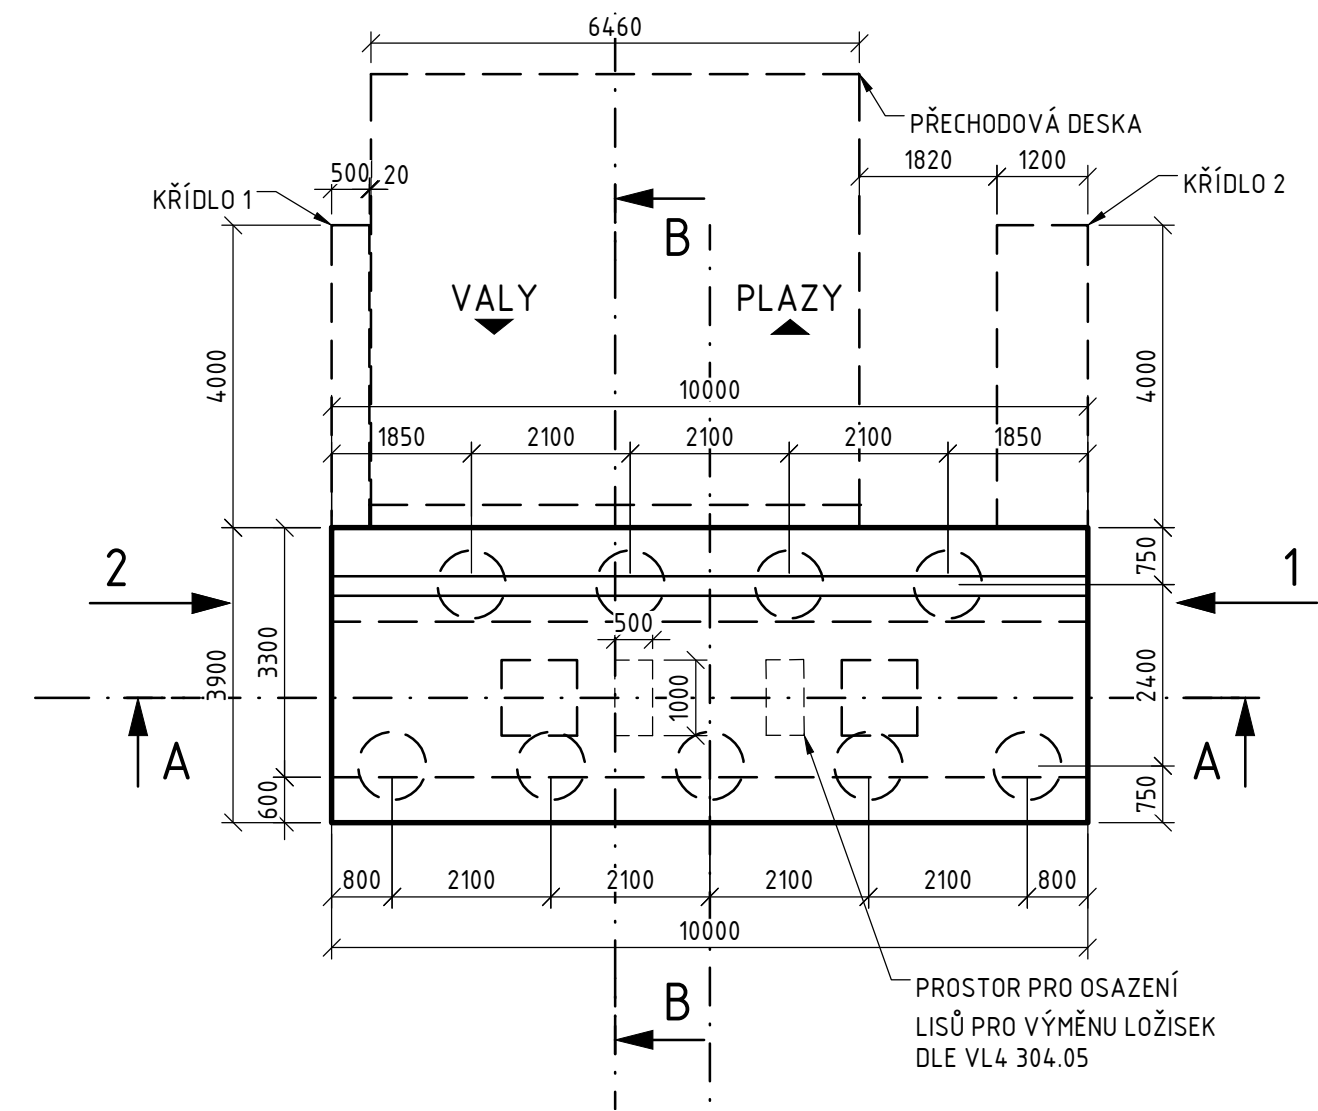

Souřadnicový systém: S-JTSK
Výškový systém: Bpv

SO 221 NADJEZD PŘELOŽKY III/2768 V KM 2,200

Objednatel: **Ředitelství silnic a dálnic**
Čerčanská 2023/12, Krč, 140 00 Praha 4

Valbek, spol. s r.o.
Vaňurova 505/17
460 07 Liberec 3

Valbek	Vypracoval	M. KNESPLOVÁ	Zak. číslo	21-L113-001
	Zodp. projektant	ING. S. RŮŽIČKA	Datum	02/2025
	Tech. kontrola	ING. I. BELDA	Stupeň	PDPS
	Akce	I/16 MLADÁ BOLESLAV - MARTINOVICE		Počet formátů
Zhotovitel:	Příloha		Měřítko	1:100
Valbek, spol. s r.o. Vaňurova 505/17 460 07 Liberec 3	HLUBINNÉ ZALOŽENÍ, TVAR OPĚRY 04		Č. přílohy	Paré

203