



PŮDORYS 1:200

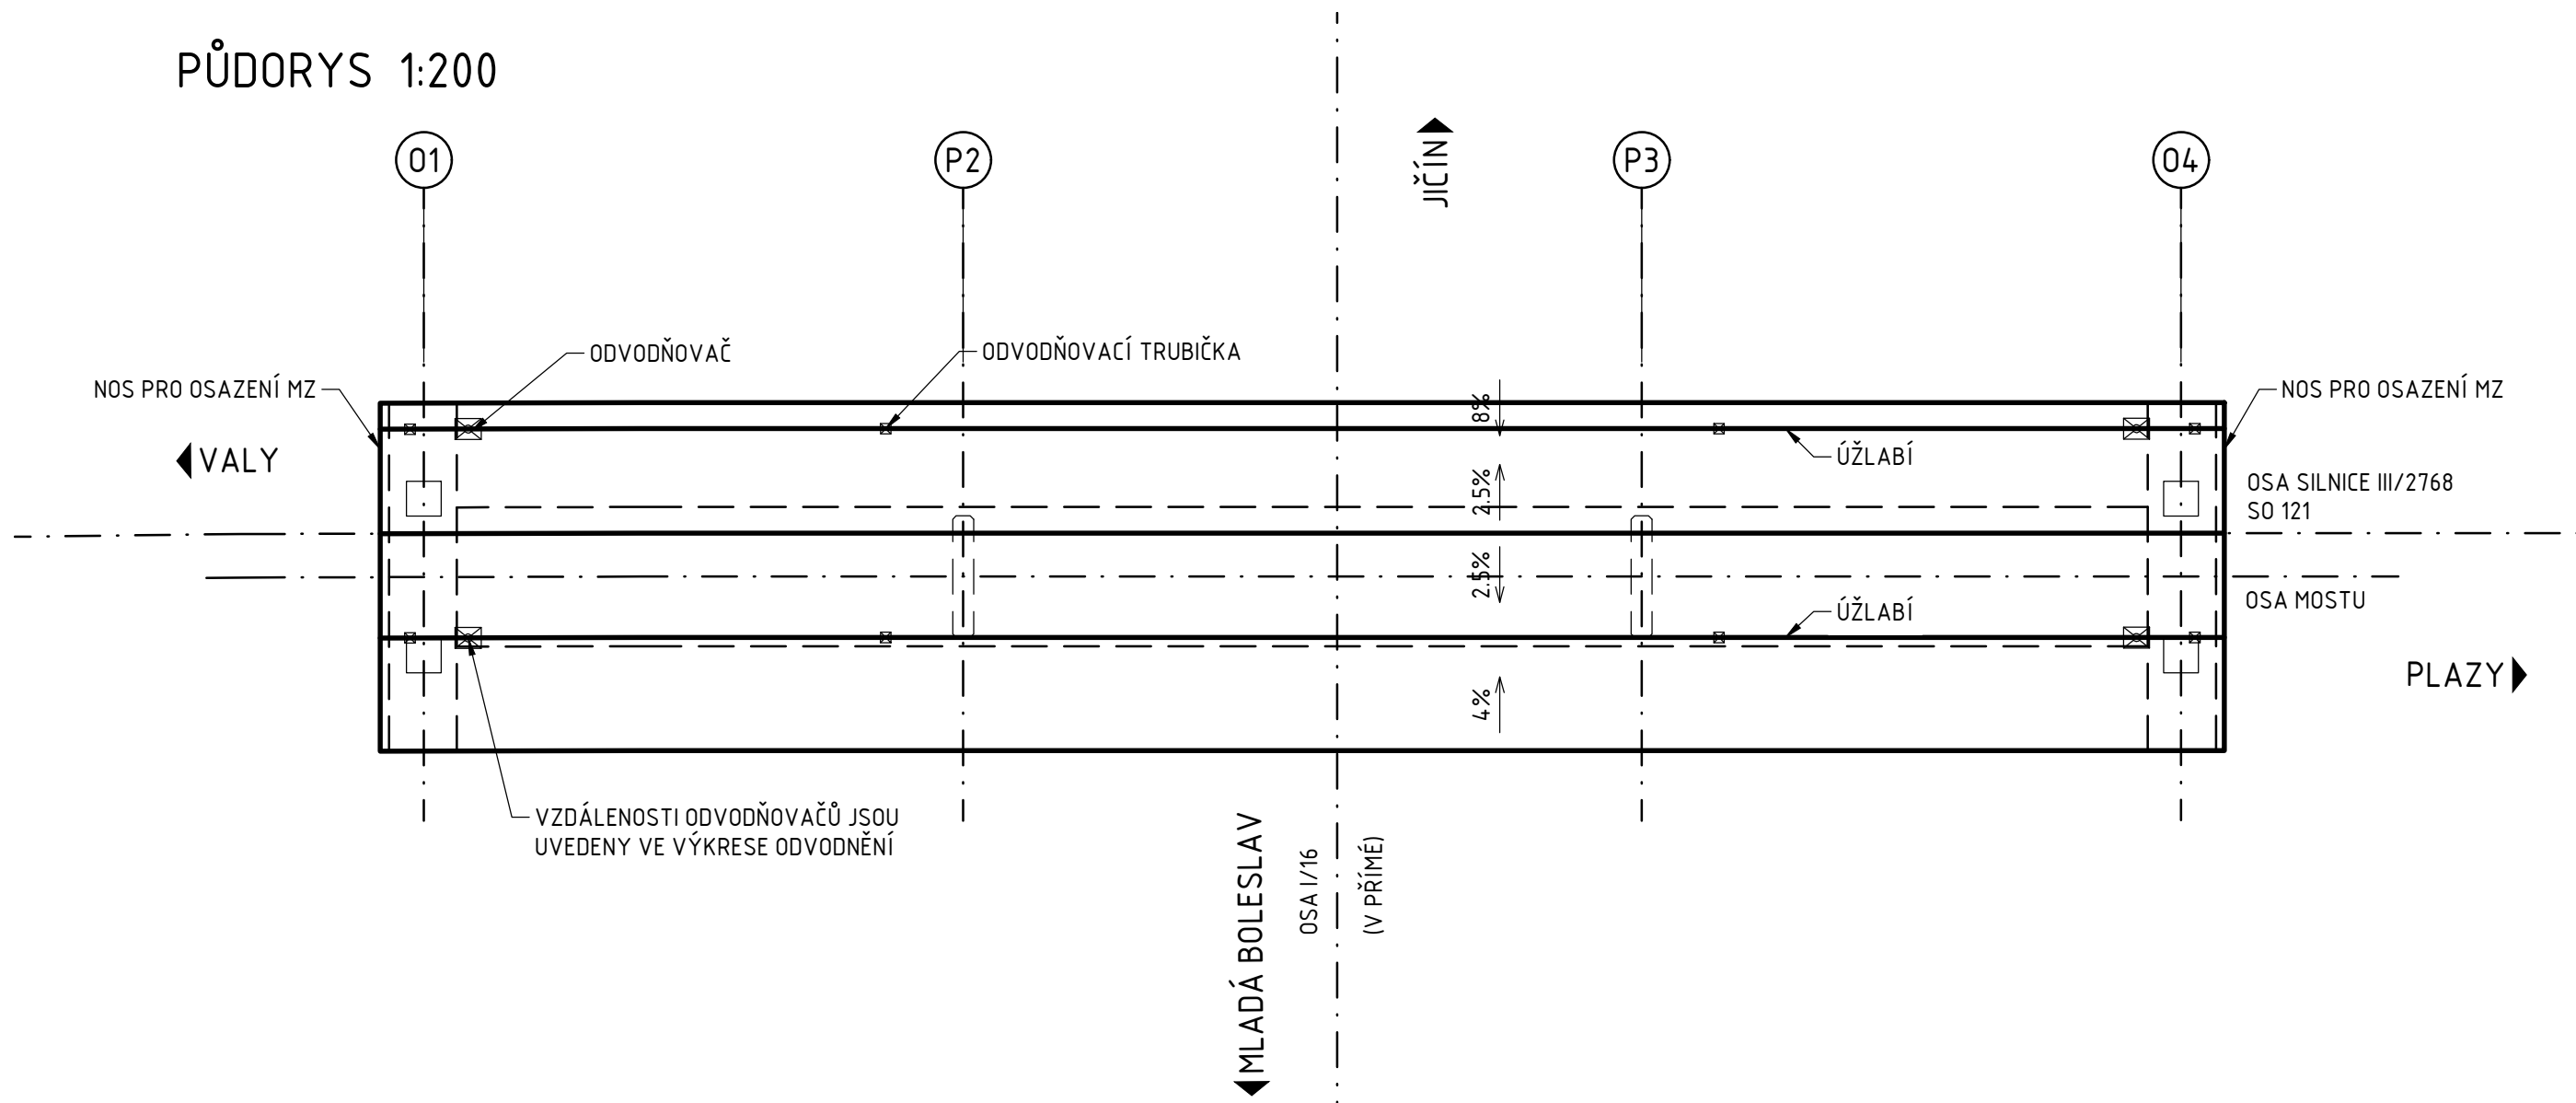


PODÉLNÝ ŘEZ 1:200

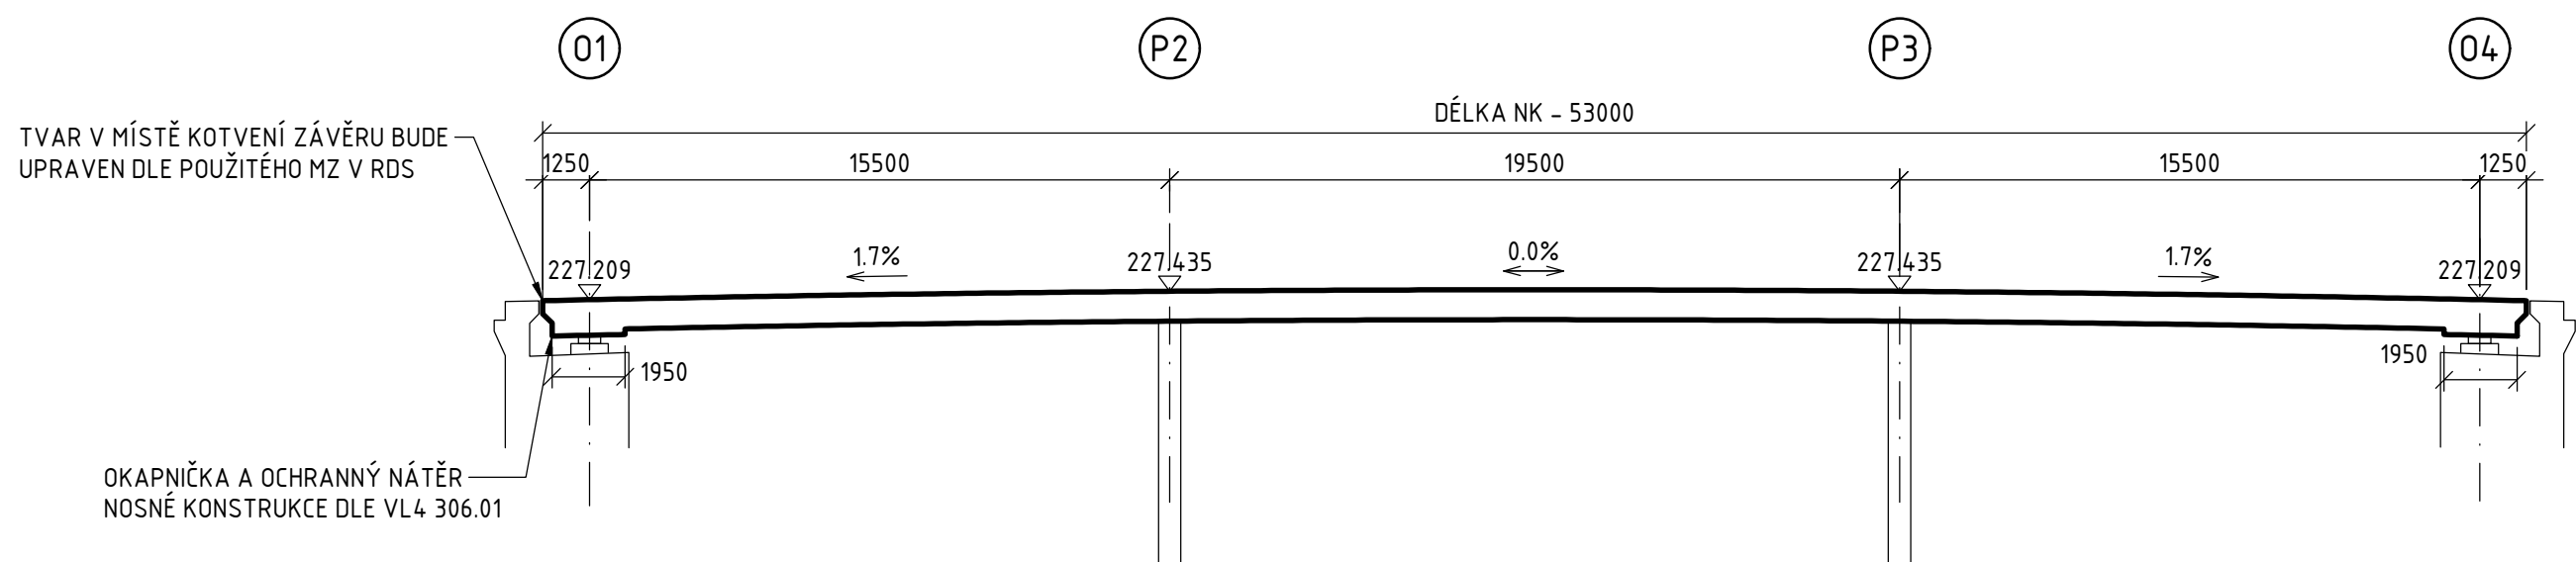


PŘÍČNÝ ŘEZ NK 1:75

POHLED VE SMĚRU STANIČENÍ

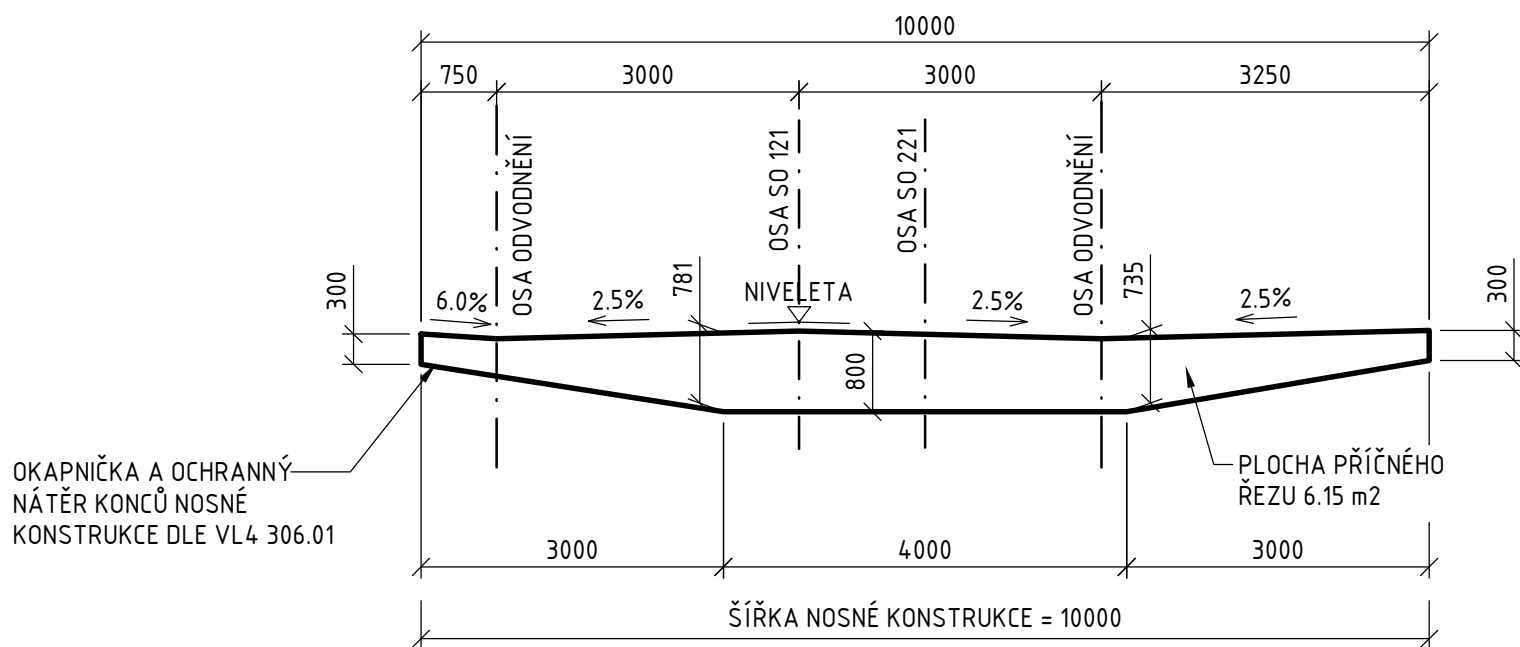


TVAR PŘÍČNÍKU V MÍSTĚ 01 1:75

ŘEZ V MÍSTĚ ULOŽENÍ PROTI SMĚRU STANIČENÍ

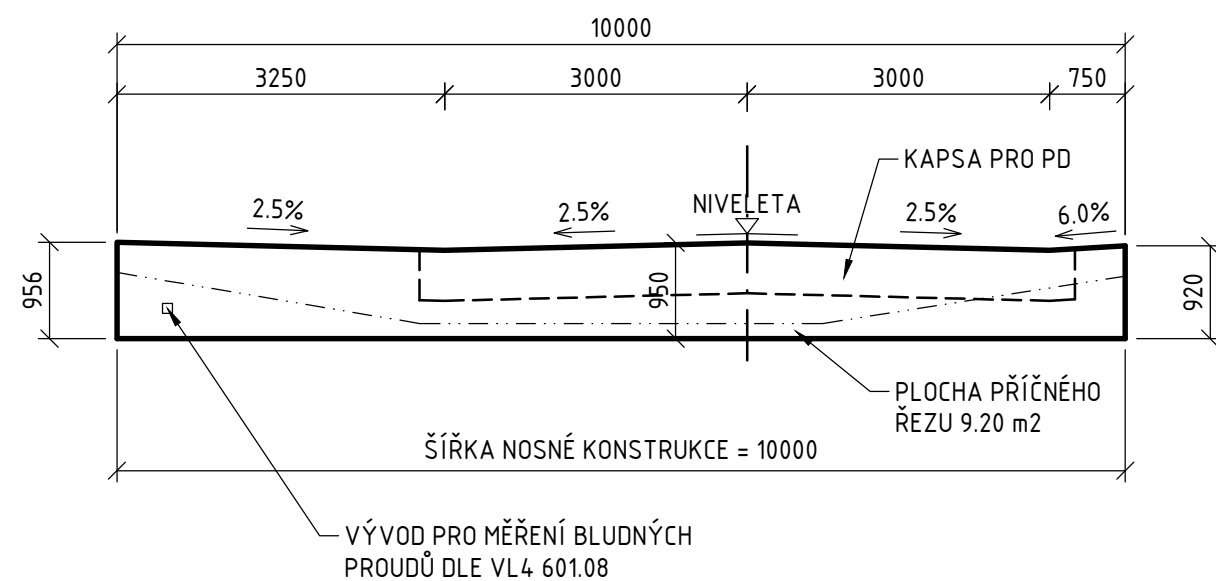

TVAR PŘÍČNÍKU V MÍSTĚ 04 1:75

ŘEZ V MÍSTĚ ULOŽENÍ VE SMĚRU STANIČENÍ

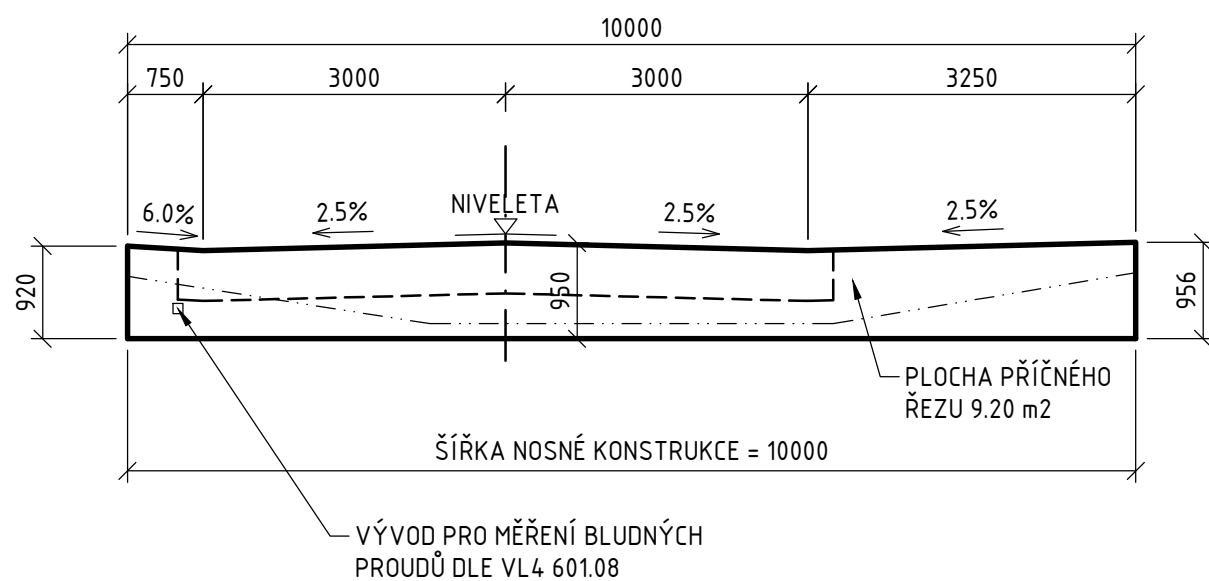

POZNÁMKY:

- NEDÍLNOU SOUČÁSTÍ VÝKRESU JSOU POZNÁMKY A SPECIFIKACE UVEDENÉ NA VÝKRESE POZNÁMEK A TECHNICKÝCH SPECIFIKACÍ

Souřadnicový systém: S-JTSK
Výškový systém: Bpv

SO 221 NADJEZD PŘELOŽKY III/2768 V KM 2,200

Objednatel:



Ředitelství silnic a dálnic s. p.
Čerčanská 2023/12, Krč, 140 00 Praha 4



Valbek, spol. s r.o.
Vaňurova 505/17
460 07 Liberec 3



Vypracoval: M. KNESPLOVÁ	Zak. číslo: 21-L113-001
Zodp. projektant: ING. S. RŮŽIČKA	Datum: 02/2025
Tech. kontrola: ING. I. BELDA	Stupeň: PDPS
Akce: I/16 MLADÁ BOLESLAV - MARTINOVICE	Počet formátů: 8x A4
Měřítko: 1:200,75	C. přílohy: Paré
Zhotovitel: Valbek, spol. s r.o.	205
Vaňurova 505/17	460 07 Liberec 3

TVAR NOSNÉ KONSTRUKCE

