



SCHÉMA PŘEDPÍNAČÍ VÝZTUŽE

PODÉLNÝ ŘEZ 1:100

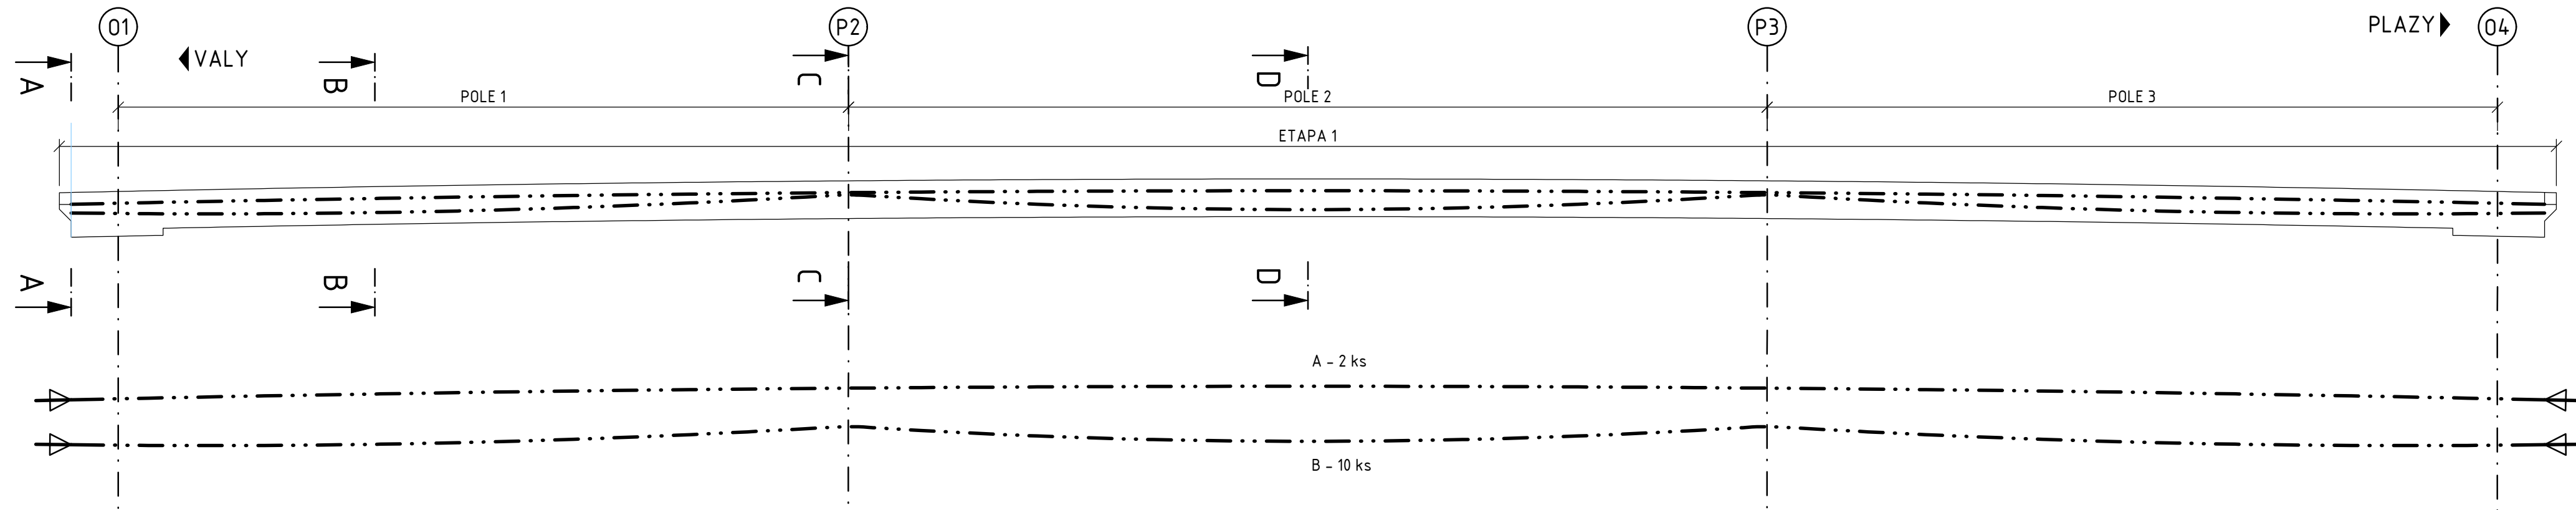

POHLED NA PŘÍČNÍK 01 A 04 A-A 1:50

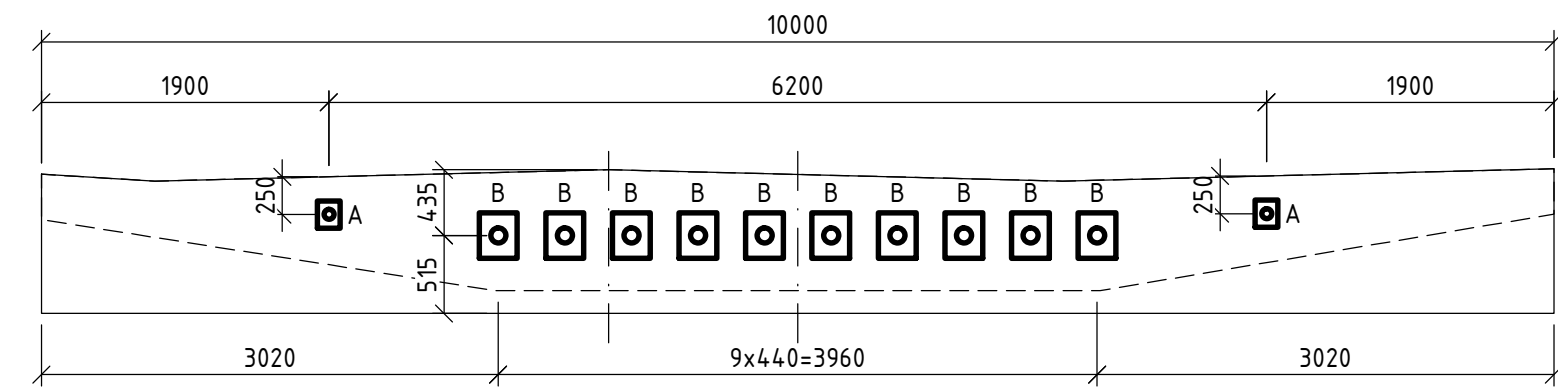


VÝKAZ PŘEDPÍNAČÍCH KABELŮ


KABEL	POČET KABELŮ [ks]	DÉLKA KABELŮ [m]	POČET LAN V 1 KABELU	HMOTNOST [kg]
A	2	52,51	7	867,5
B	10	52,53	19	11 777,2
CELKOVÁ HMOTNOST [t]				12 644,7

- PŘEDPÍNAČÍ VÝZTUŽ - Y1860S7-15.7-A
DLE prEN 10138-1 a 3 (150 mm²)
- KOTEVNÍ NAPĚTÍ - 1350 MPa
- PODRŽENÍ NAPĚTÍ - 5 min


PŘÍČNÝ ŘEZ B-B 1:50

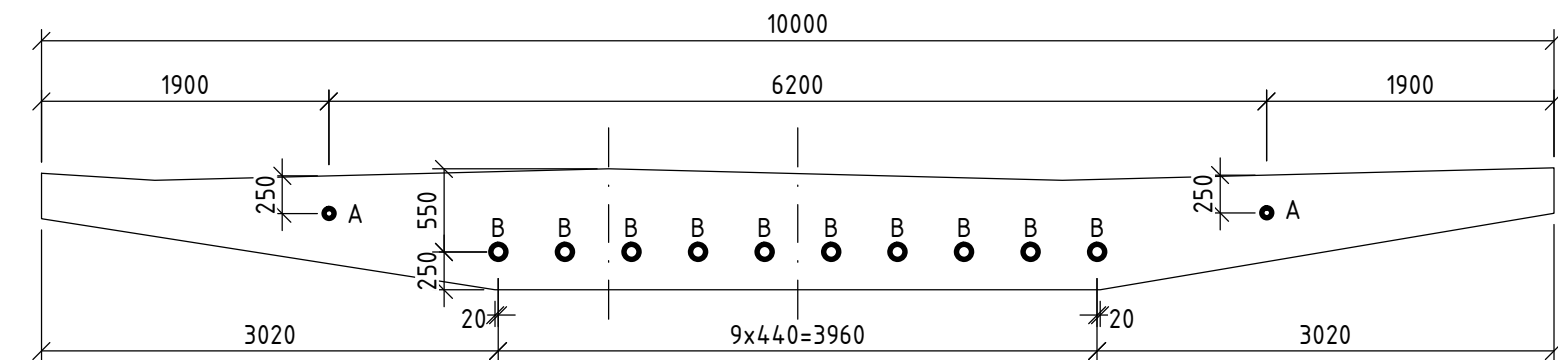

PŘÍČNÝ ŘEZ C-C 1:50

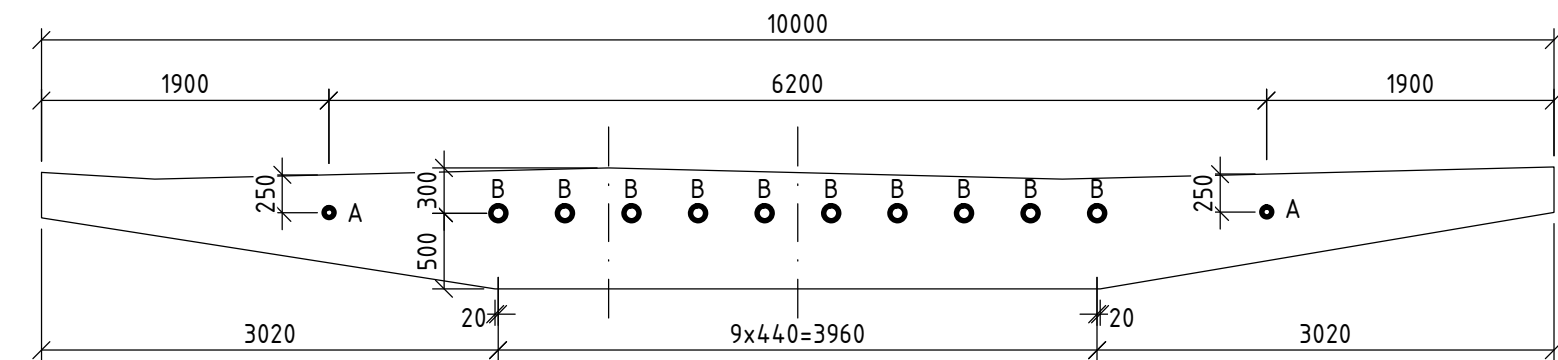

PŘÍČNÝ ŘEZ D-D 1:50

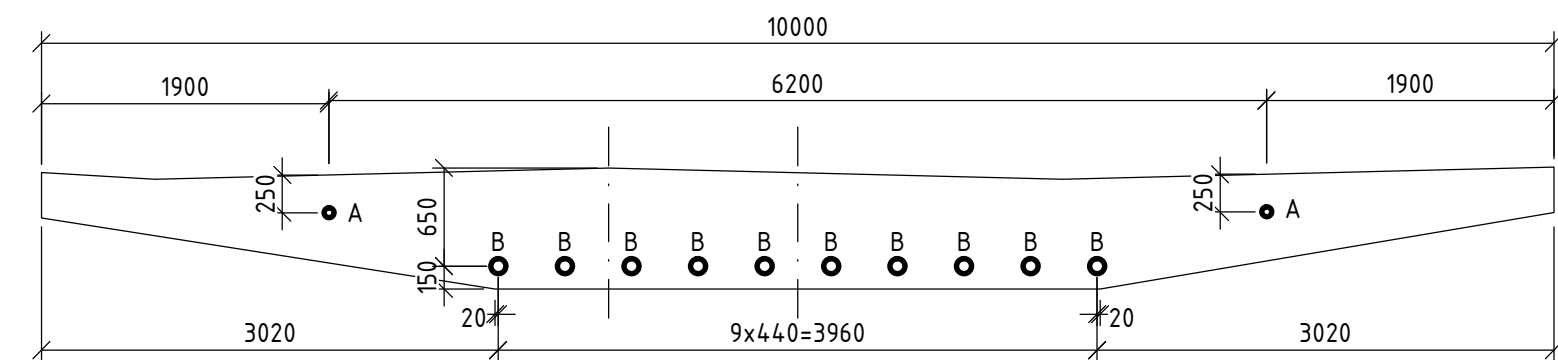

- △ PEVNÁ KOTVA
- ◀ KOTVA NA NAPÍNANÉM KONCI
- ◊ SPOJKA
- ◀ SPOJKA NA NAPÍNANÉM KONCI
- PASIVNÍ KOTVA

POZNÁMKY:

- NEDÍLNOU SOUČÁSTÍ VÝKRESU JSOU POZNÁMKY A SPECIFIKACE UVEDENÉ NA VÝKRESE POZNÁMEK A TECHNICKÝCH SPECIFIKACÍ

Souřadnicový systém: S-JTSK
Výškový systém: Bpv

SO 221 NADJEZD PŘELOŽKY III/2768 V KM 2,200

Objednatel:



Ředitelství silnic a dálnic s. p.
Čerčanská 2023/12, Krč, 140 00 Praha 4



Valbek, spol. s r.o.
Vaňurova 505/17
460 07 Liberec 3



Vypracoval	ING. S. RŮŽIČKA	<i>S. Růžička</i>	Zak. číslo	21-L113-001
Zodp. projektant	ING. S. RŮŽIČKA	<i>S. Růžička</i>	Datum	02/2025
Tech. kontrola	ING. I. BELDA	<i>I. Belda</i>	Stupeň	PDPS
Akce	I/16 MLADÁ BOLESLAV - MARTINOVICE			Počet formátů 8x A4
				Měřítko 1:100,50
				Č. přílohy Paré
Zhotovitel:	Příloha			206
Valbek, spol. s r.o. Vaňurova 505/17 460 07 Liberec 3	SCHÉMA PŘEDPÍNAČÍ VÝZTUŽE			

