


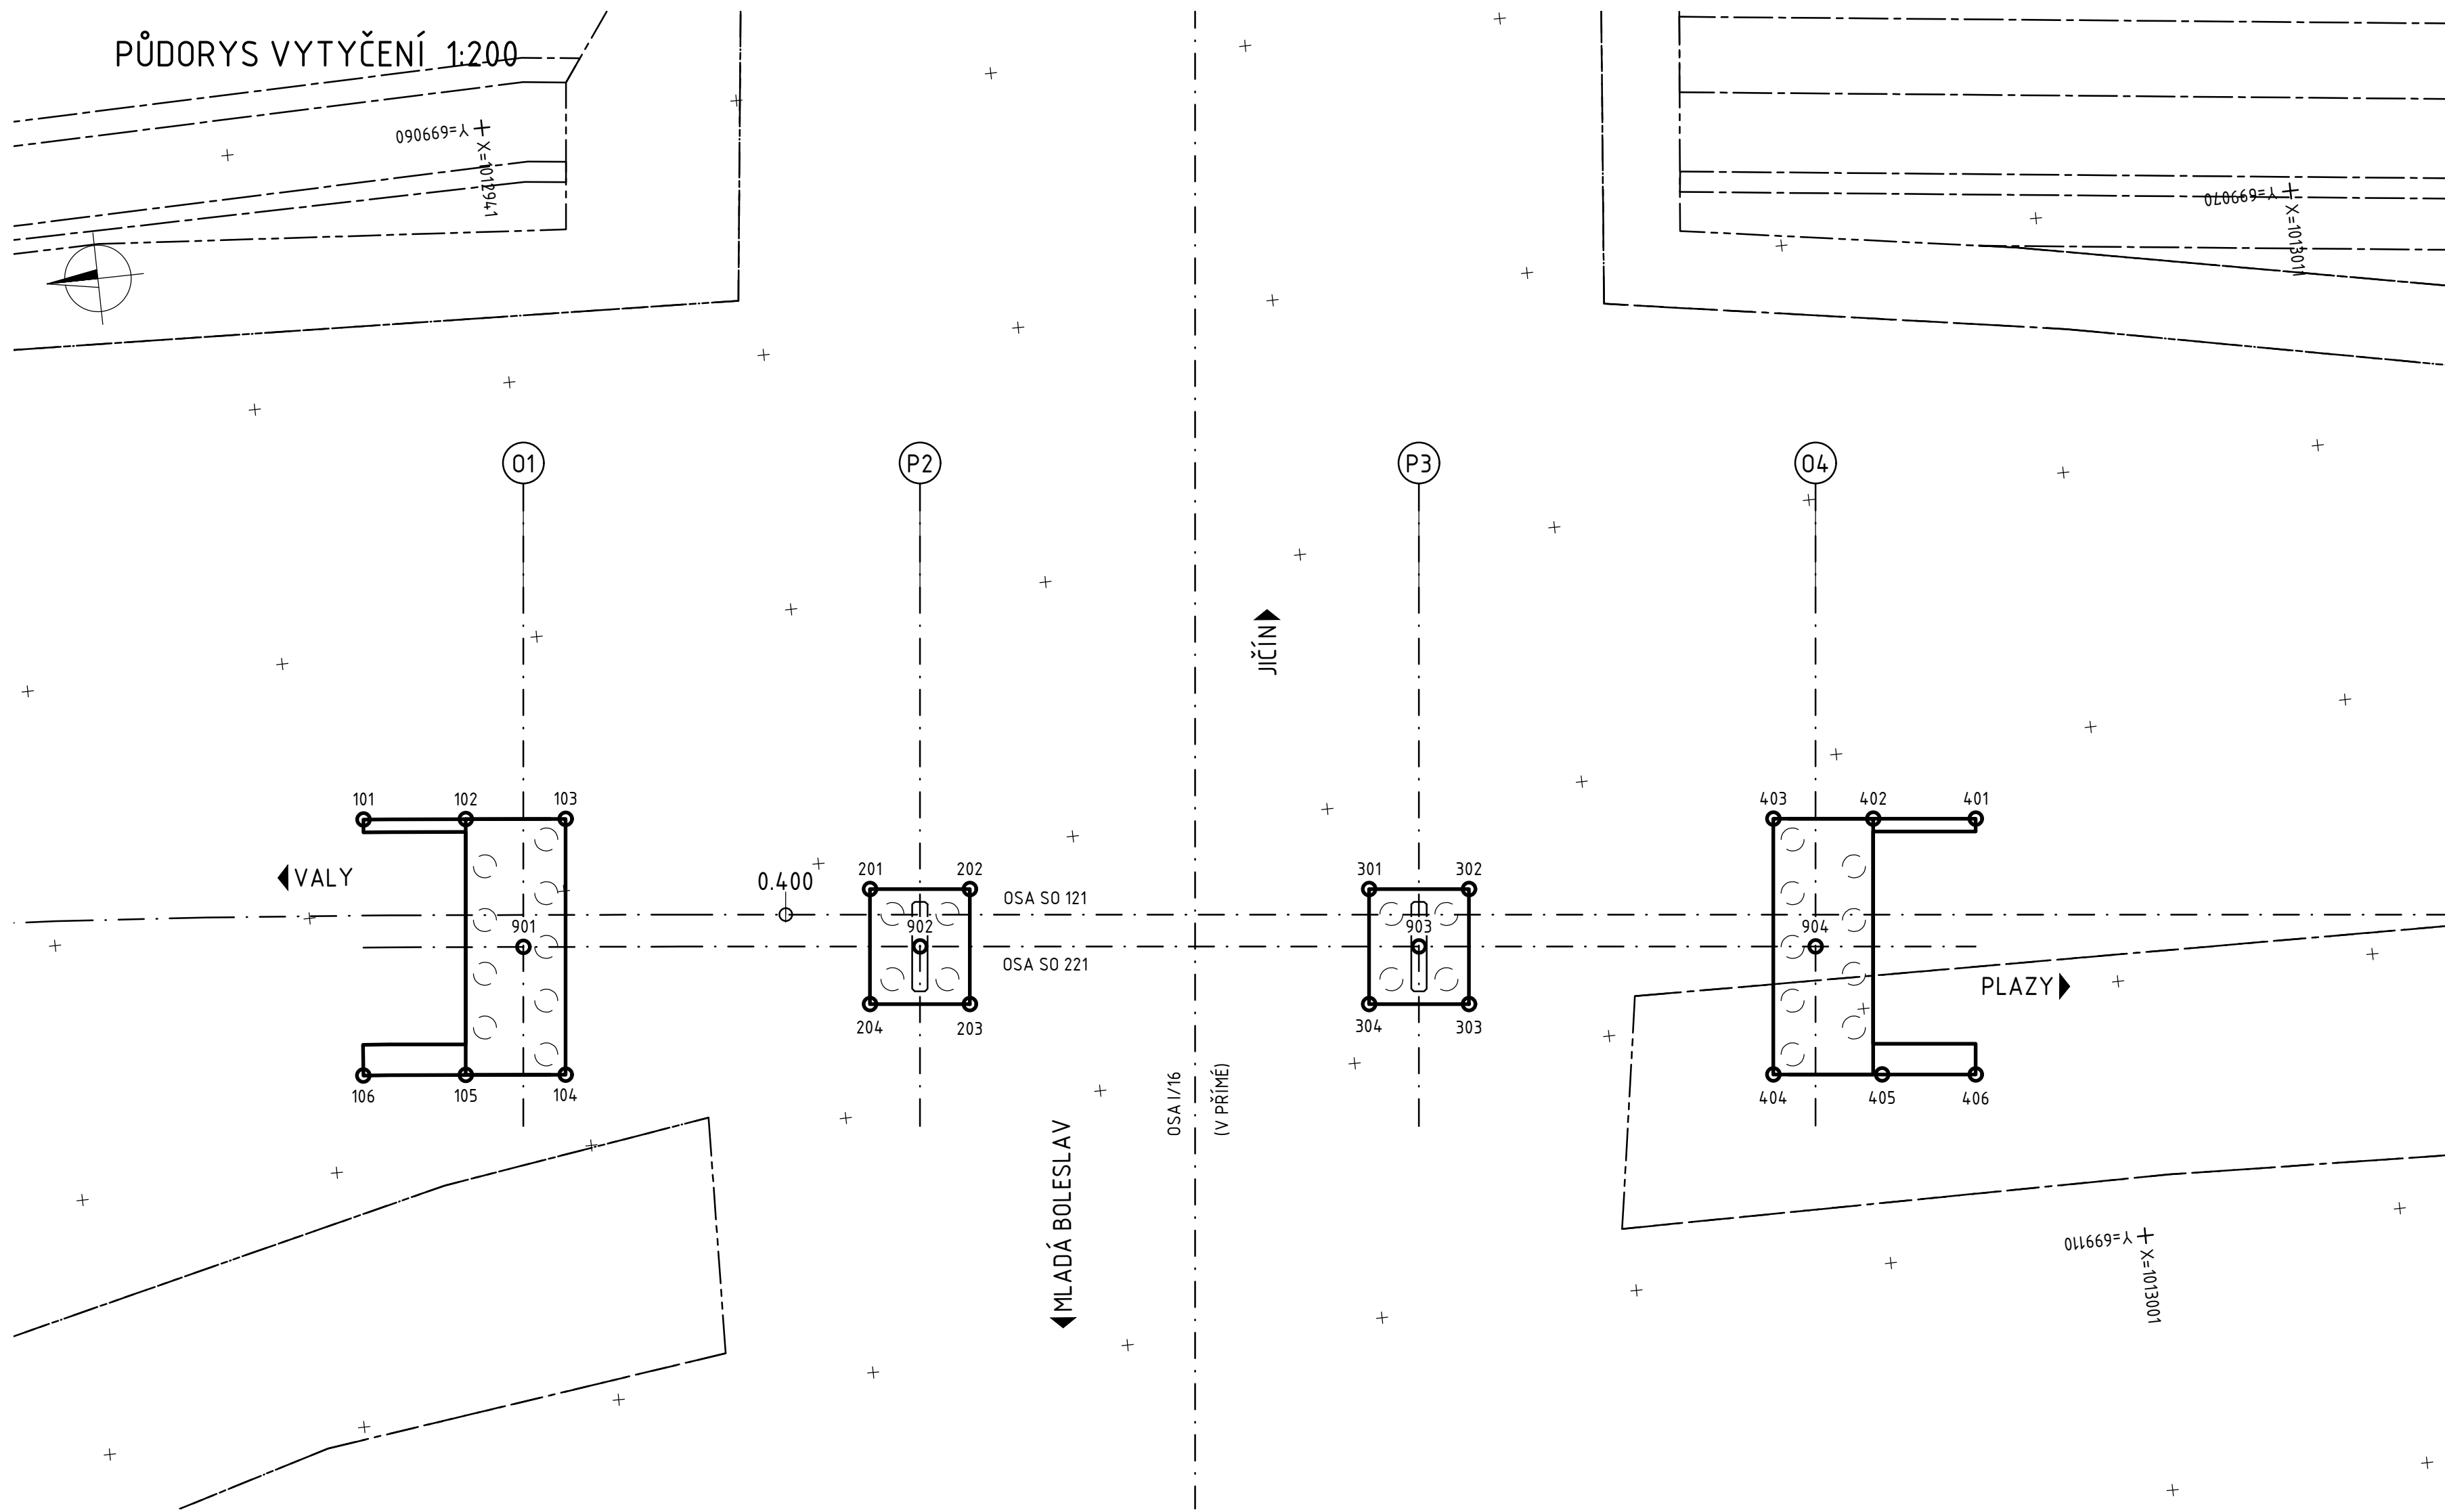

SOUŘADNICE VB

BOD	Y [m]	X [m]	Z [m]
901	698932.004	101144.8183	-
902	698933.646	101146.596	-
903	698935.730	101148.984	-
904	698937.387	101149.396	-
101	698926.388	101144.2501	227.047
102	698926.797	101144.6480	222.050
103	698927.205	101145.0359	222.050
104	698937.148	101144.9289	222.050
105	698936.740	101144.5411	222.050
106	698936.332	101144.1432	227.116
201	698931.200	101146.1898	217.495
202	698931.617	101146.5775	217.495
203	698936.092	101146.5294	217.495
204	698935.675	101146.1417	217.495
301	698933.285	101148.1286	217.495
302	698933.702	101148.5164	217.495
303	698938.176	101148.4683	217.495
304	698937.759	101148.0805	217.495
401	698933.084	101150.5144	227.047
402	698932.656	101150.1167	222.050
403	698932.239	101149.7290	222.050
404	698942.182	101149.6221	222.050
405	698942.636	101150.446	222.050
406	698943.026	101150.4075	227.116

LEGENDA



TRVALÝ ZÁBOR	---
DOČASNÝ ZÁBOR nad 1 rok	---
DOČASNÝ ZÁBOR do 1 roku	---

POZNÁMKY:

- VYTYČOVACÍ ODCHYLKY: VIZ PŘÍLOHA E.4.5.1 - GVS - SEZNAM SOUŘADNIC
- NEDÍLNOU SOUČÁSTÍ VÝKRESU JSOU POZNÁMKY A SPECIFIKACE UVEDENÉ NA VÝKRESE POZNÁMEK A TECHNICKÝCH SPECIFIKACÍ

PŘECHODOVÉ OBLASTI, PODÉLNÝ ŘEZ 1:100

PŘECHODOVÉ OBLASTI S PŘECHODOVOU DESKOU DLE VL4 201.01 A ČSN 73 6244

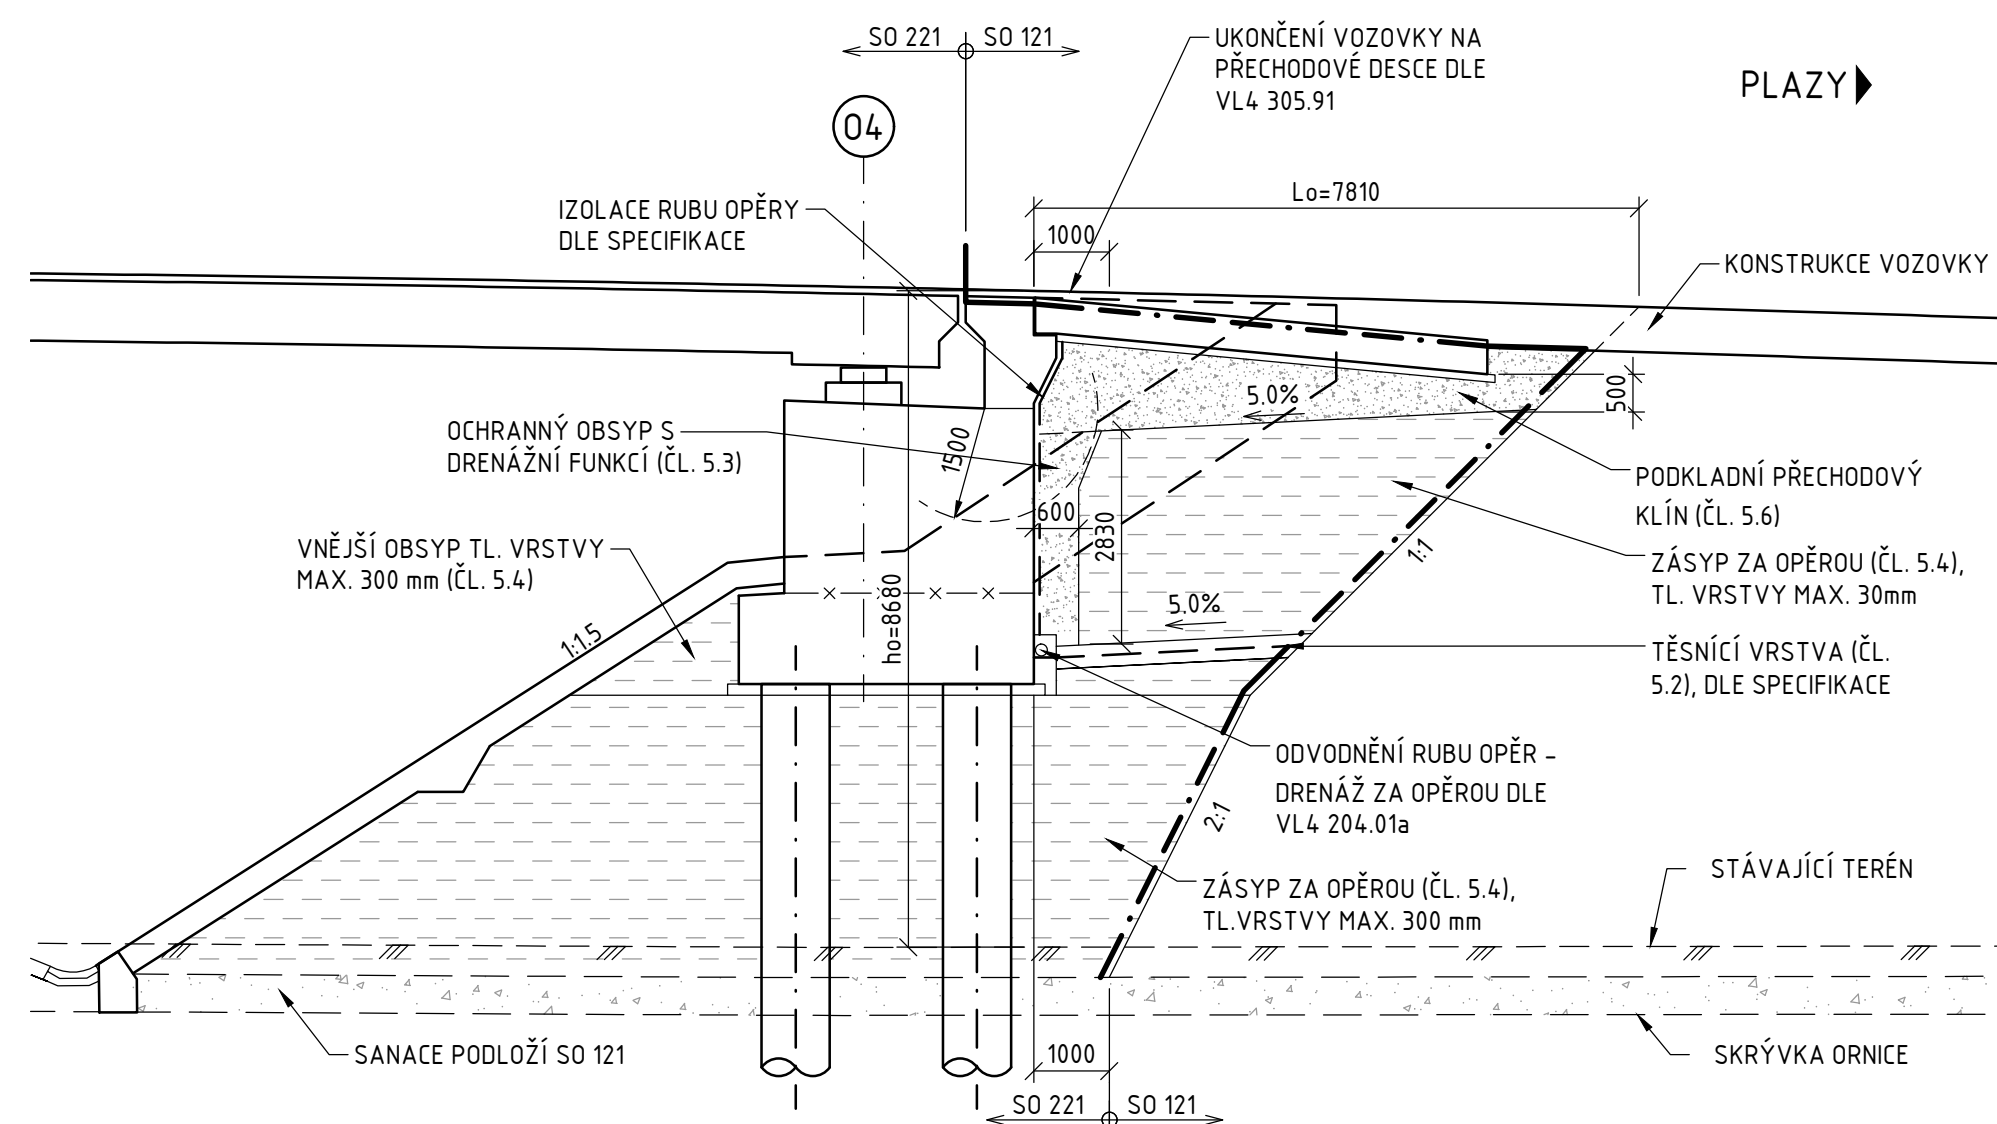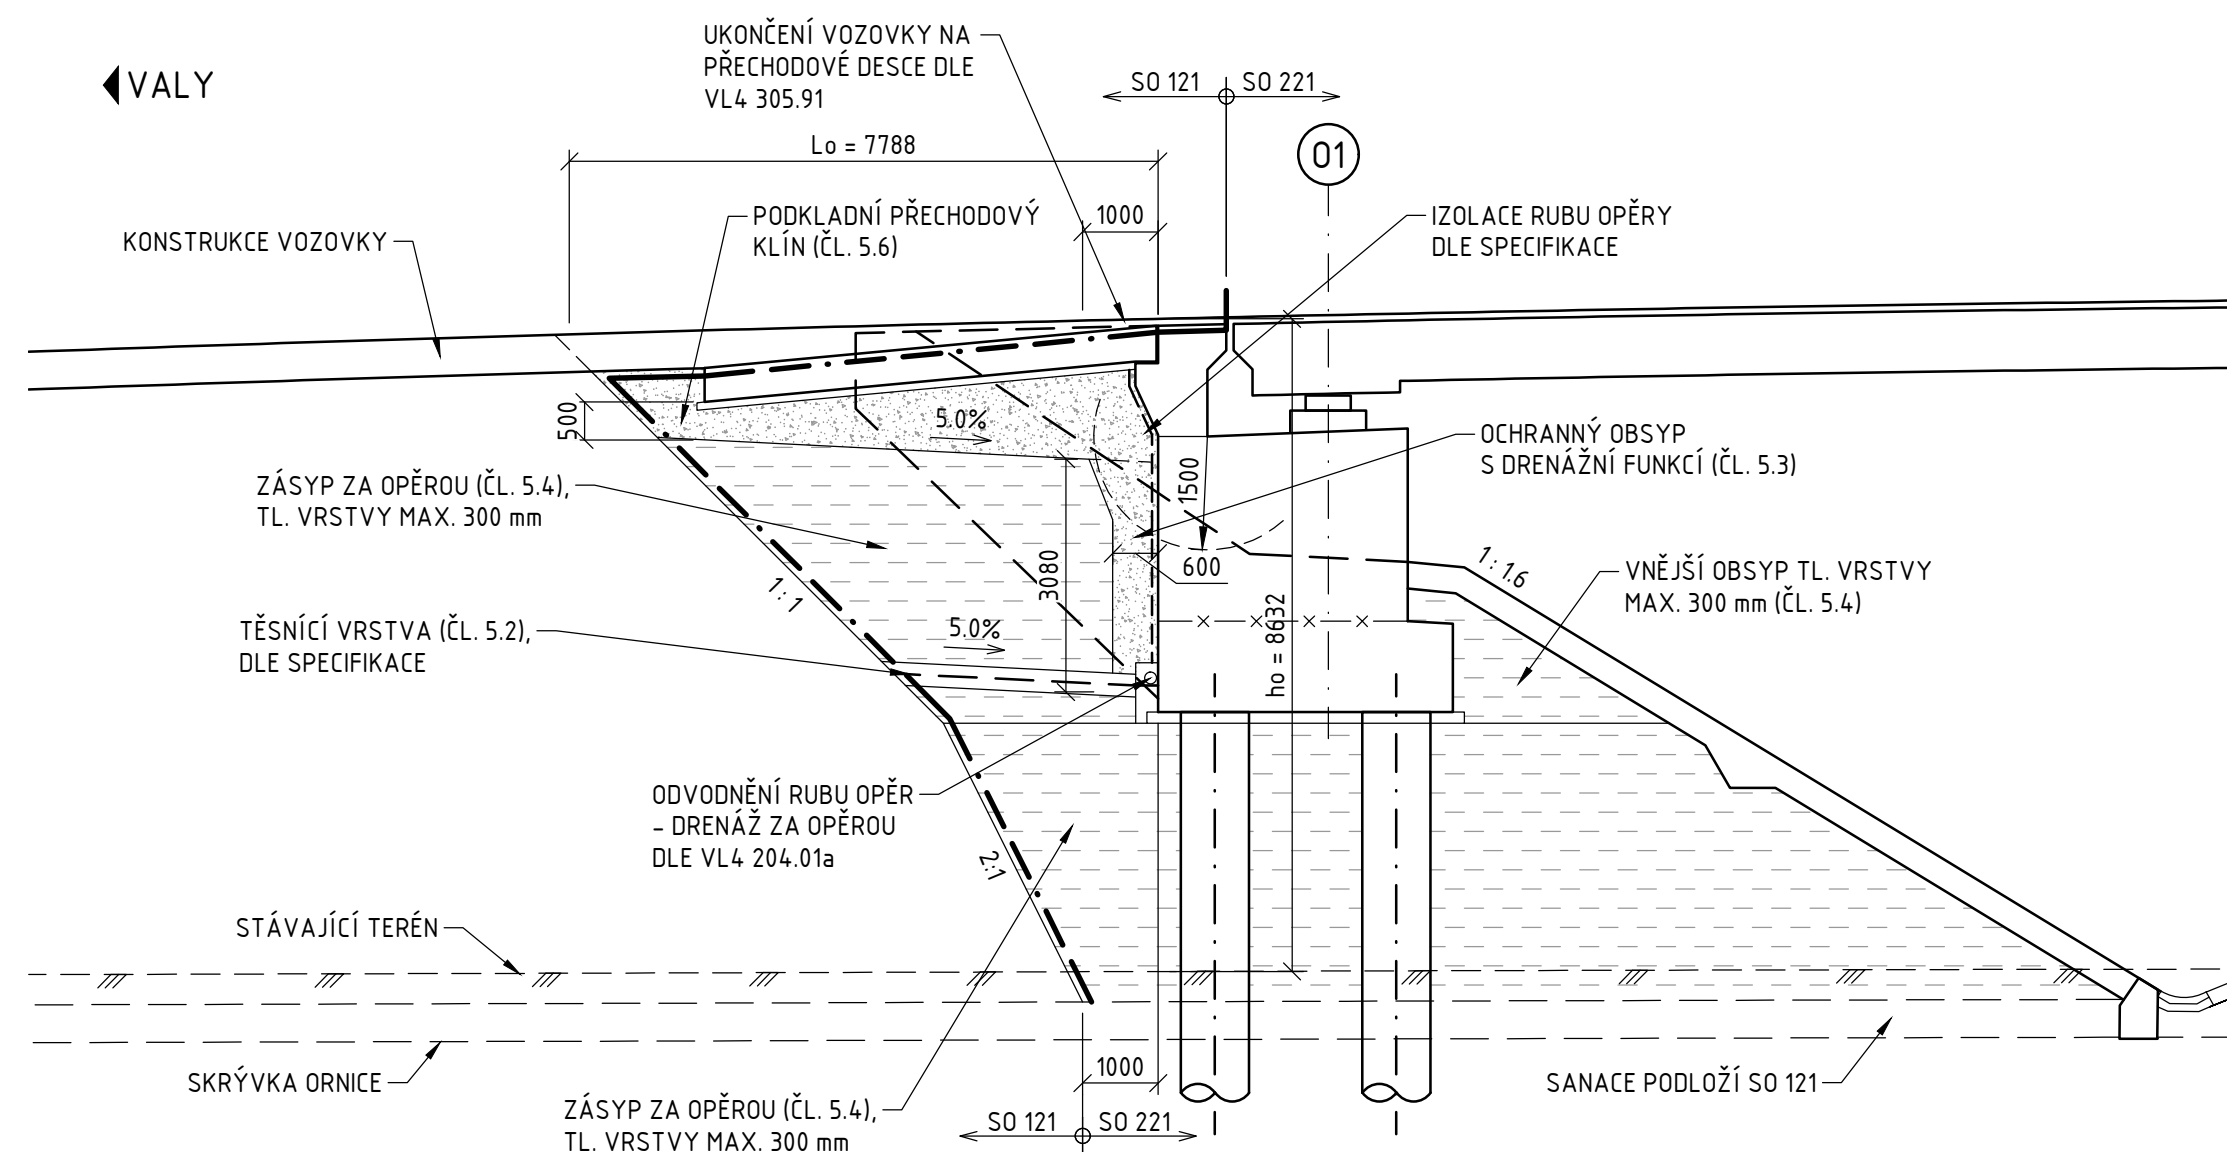

Souřadnicový systém: S-JTSK
Výškový systém: Bpv

SO 221 NADJEZD PŘELOŽKY III/2768 V KM 2,200

Objednatel:



Ředitelství silnic a dálnic s. p.
Čerčanská 2023/12, Krč, 140 00 Praha 4



Valbek, spol. s r.o.
Vaňurova 505/17
460 07 Liberec 3



Vypracoval	M. KNESPOVÁ	Zak. číslo	21-L113-001	
Zodp. projektant	ING. S. RŮŽIČKA	Datum	02/2025	
Tech. kontrola	ING. I. BELDA	Stupeň	PDPS	
Akce	I/16 MLADÁ BOLESLAV - MARTINOVICE		Počet formátů	8x A4
			Mřížko	1:200,100
			Č. přílohy	Paré
Příloha	VYTYČENÍ, PŘECHODOVÉ OBLASTI		207	

