


SCHÉMA ODVODNĚNÍ
PODÉLNÝ ŘEZ 1:100


◀ VALY

ČÍSLO ODVODŇOVAČE

ČÍSLO TRUBÍČKY IZOLACE

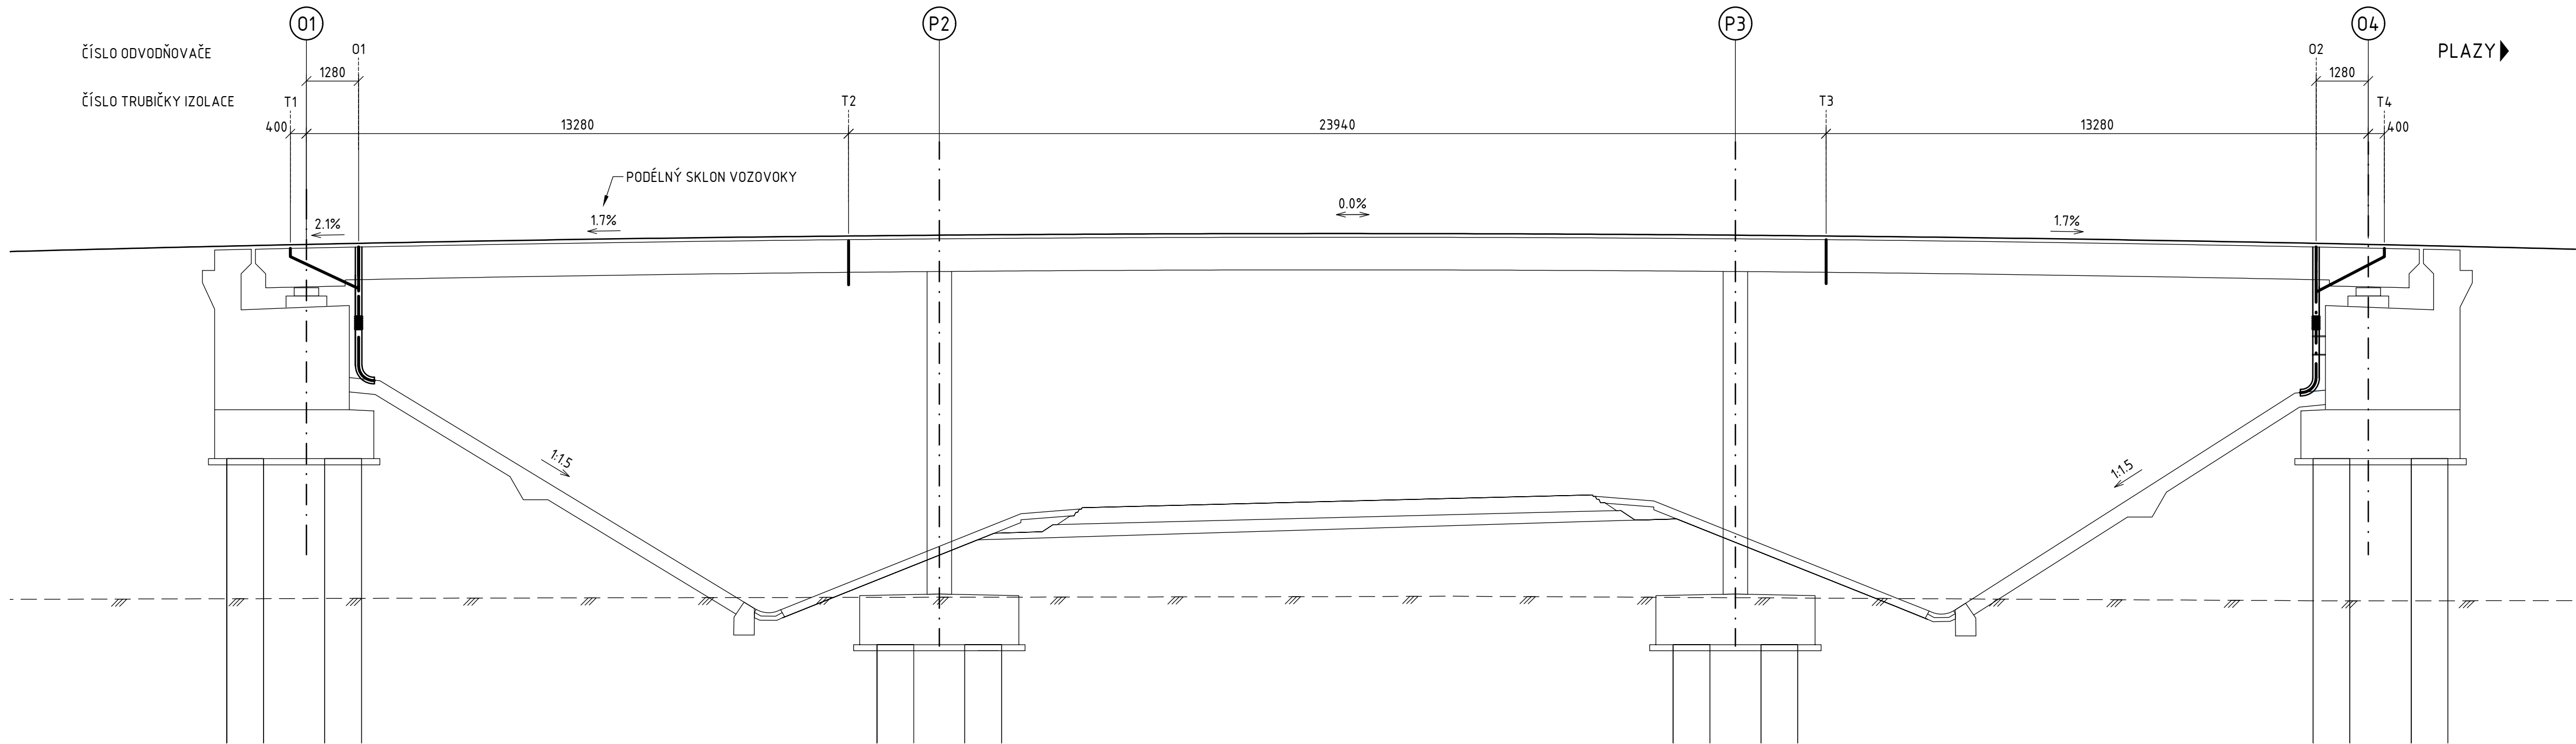

PŘÍČNÝ ŘEZ 1:50

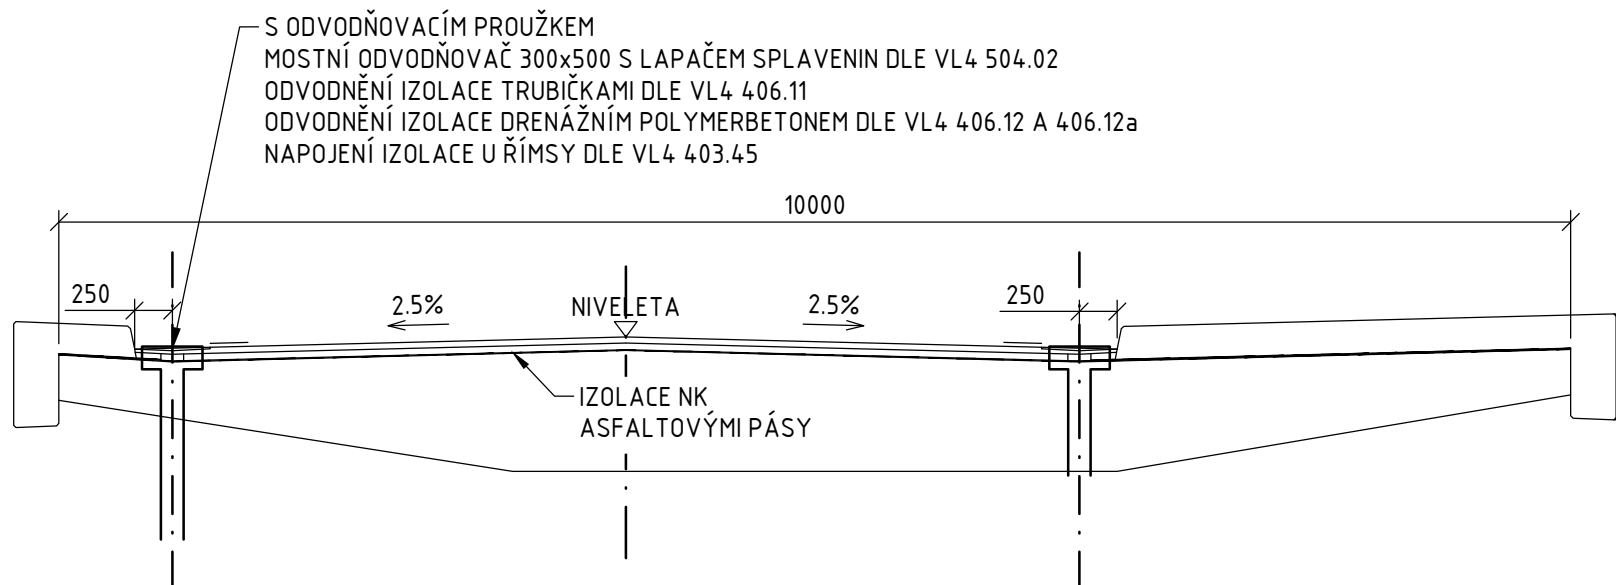

ROZMÍSTĚNÍ LOŽISEK - PŮDORYS

PODPĚRA	01	P2	P3	04	×	VETKNUTÍ
ČÍSLO LOŽISKA	1	×	×	3	↔	LOŽISKO JEDNOSMĚRNĚ POSUVNÉ
ČÍSLO LOŽISKA	2	×	×	4	↔	LOŽISKO VŠESMĚRNĚ POSUVNÉ

TABULKA LOŽISEK

PODPĚRA		OPĚRA 1		OPĚRA 4	
ČÍSLO LOŽISKA		1	2	3	4
DRUH LOŽISKA		HRNCOVÉ	HRNCOVÉ	HRNCOVÉ	HRNCOVÉ
POPIS		PODÉLNĚ POSUVNÉ	VŠESMĚRNĚ POSUVNÉ	PODÉLNĚ POSUVNÉ	VŠESMĚRNĚ POSUVNÉ
MAX. SVISLÉ PROVOZNÍ ZATÍŽENÍ (MSP)	[kN]	2300	1650	2300	1650
MAX. SVISLÉ NÁVRHOVÉ ZATÍŽENÍ (MSÚ)	[kN]	3000	2150	3000	2150
MIN. SVISLÉ NÁVRHOVÉ ZATÍŽENÍ (MSÚ)	[kN]	600	700	600	700
MAX. VODOROVNÉ NÁVRHOVÉ ZATÍŽENÍ PODÉLNĚ (MSÚ)	[kN]	200	0	200	0
MAX. VODOROVNÉ NÁVRHOVÉ ZATÍŽENÍ PŘÍČNĚ (MSÚ)	[kN]	290	0	290	0
POSUN PODÉLNÝ CELKOVÝ (MSÚ) (z mostu + do mostu)	[mm]	70	70	70	70
POSUN PODÉLNÝ CELKOVÝ (MSP) (z mostu + do mostu)	[mm]	48	48	48	48
POSUN PŘÍČNÝ CELKOVÝ (MSÚ)	[mm]	0	5	0	5


POZNÁMKY:

- NEDÍLNOU SOUČÁSTÍ VÝKRESU JSOU POZNÁMKY A SPECIFIKACE UVEDENÉ NA VÝKRESE POZNÁMEK A TECHNICKÝCH SPECIFIKACÍ


MOSTNÍ ZÁVĚRY

PŘÍČNÝ ŘEZ NK V MÍSTĚ MZ 1: 50

MOSTNÍ ZÁVĚR JE KOLMÝ, PLATÍ PRO MOSTNÍ ZÁVĚRY OBOU OPĚR

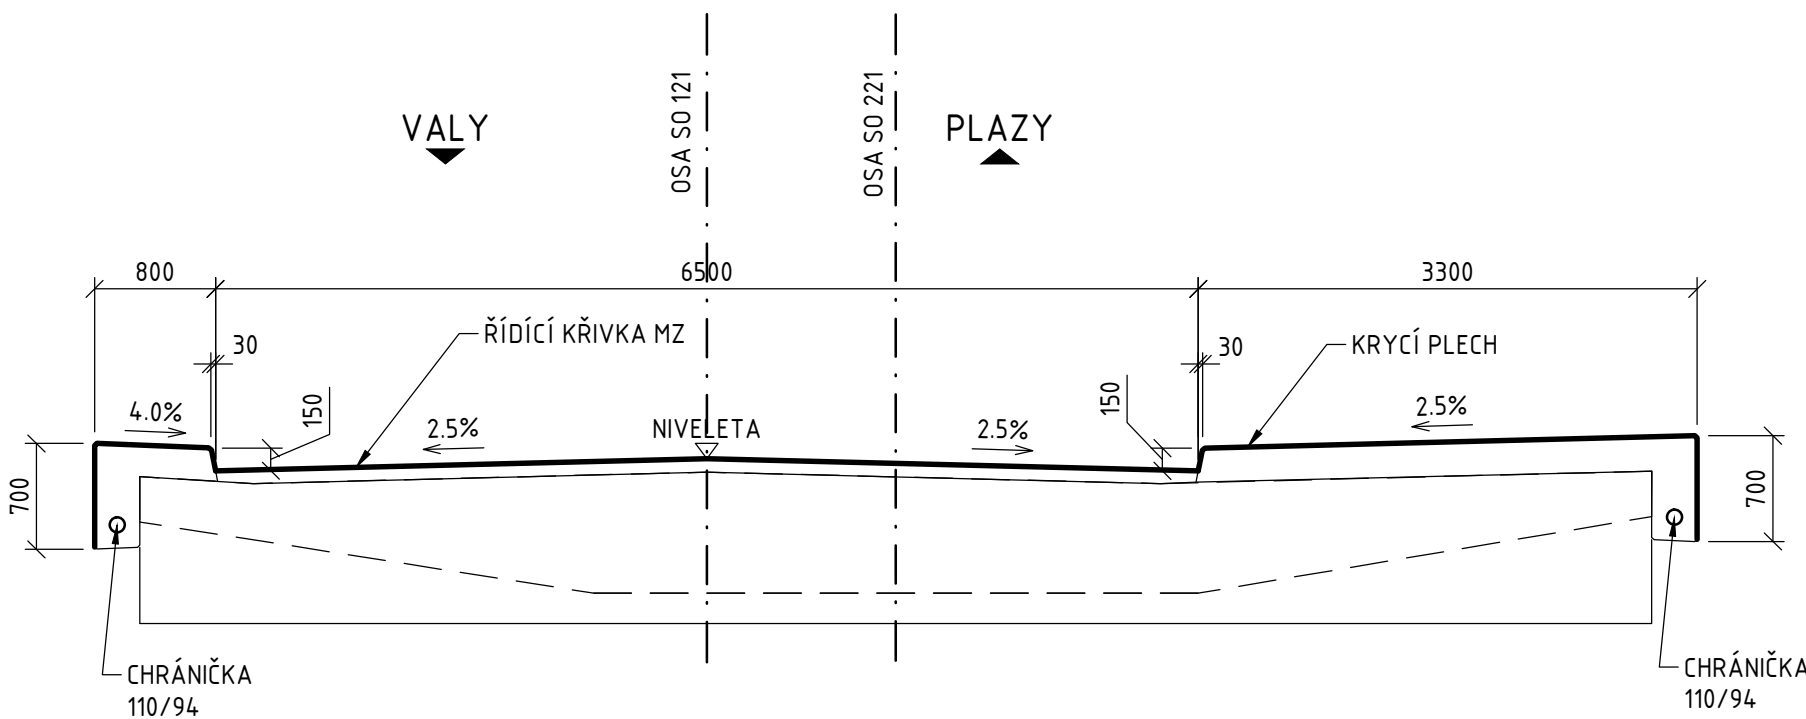

PŘÍČNÝ ŘEZ MOSTNÍM ZÁVĚREM VE VOZOVCE 1:50

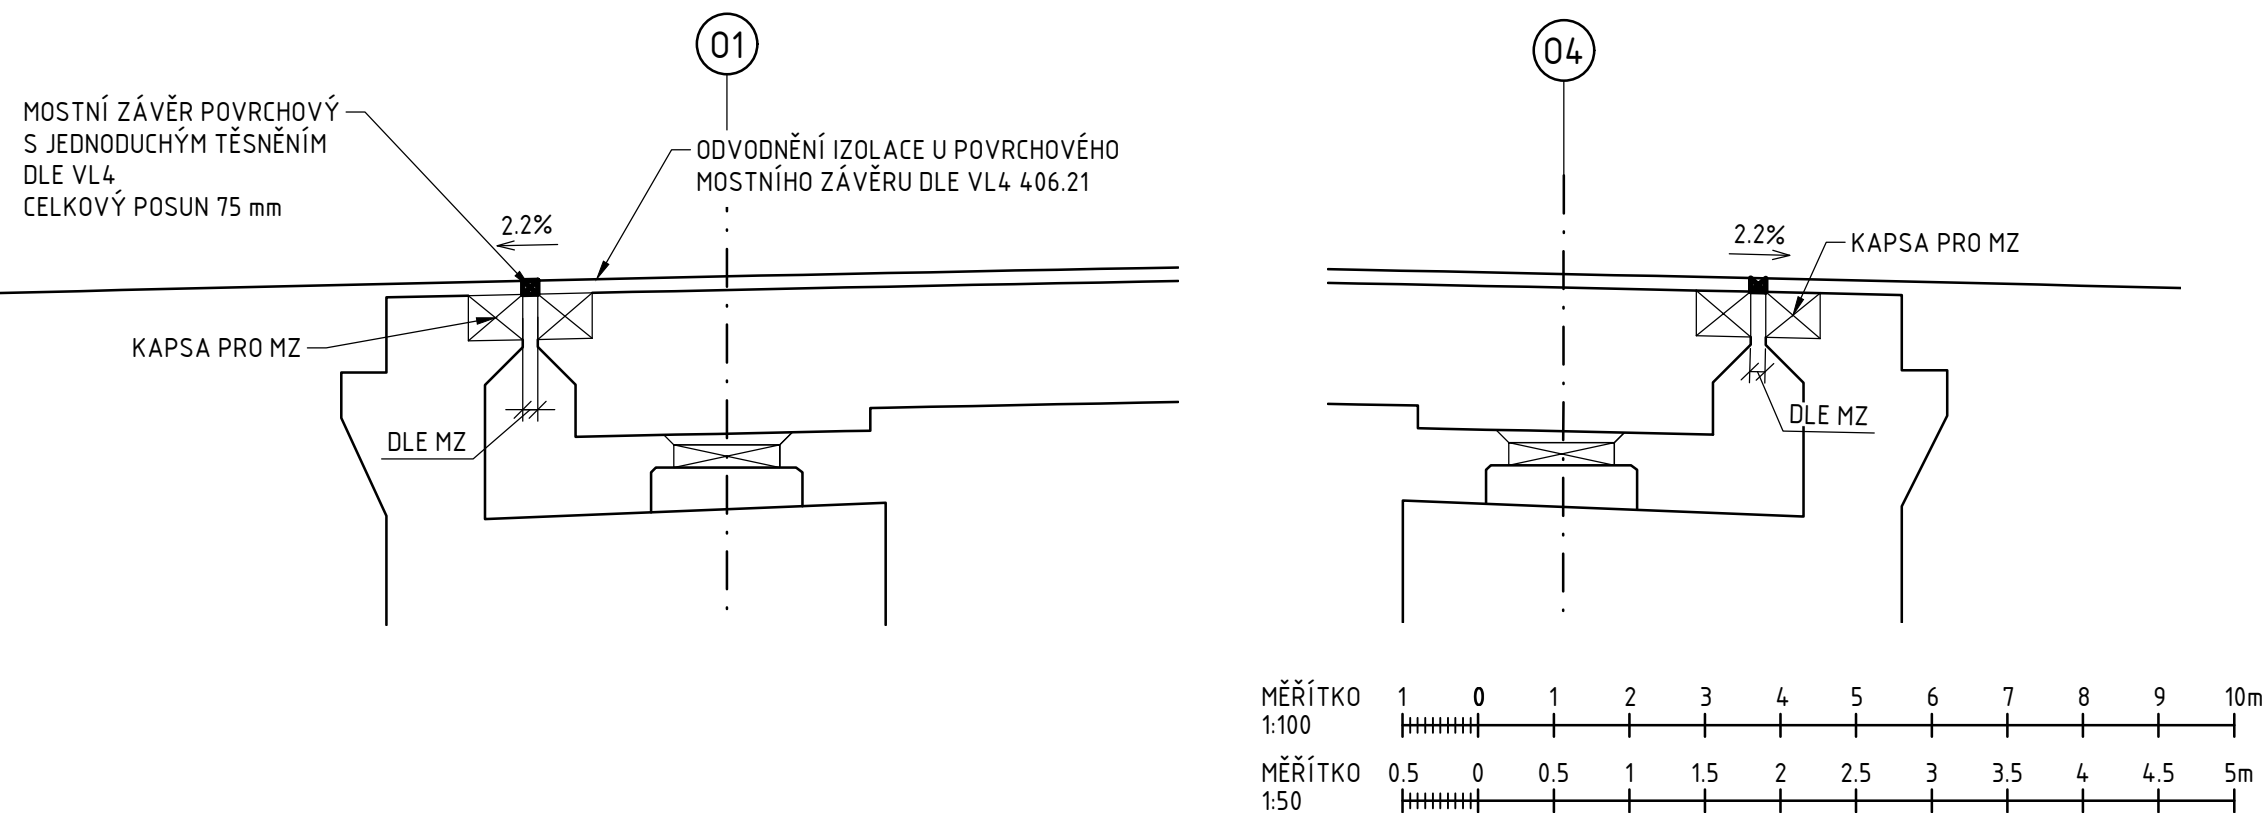

Souřadnicový systém: S-JTSK
Výškový systém: Bpv

SO 221 NADJEZD PŘELOŽKY III/2768 V KM 2,200

Objednatel:



Ředitelství silnic a dálnic s. p.
Čerčanská 2023/12, Krč, 140 00 Praha 4



Valbek, spol. s r.o.
Vaňurova 505/17
460 07 Liberec 3



Vypracoval	M. KNESPOVÁ	Zak. číslo	21-L113-001
Zodp. projektant	ING. S. RŮŽIČKA	Datum	02/2025
Tech. kontrola	ING. I. BELDA	Stupeň	PDPS
Akce	I/16 MLADÁ BOLESLAV - MARTINOVICE	Počet formátů	8x A4
		Měřítko	1:100,50
		Č. přílohy	Paré
Zhotovitel:	Příloha SCHÉMA ODVODNĚNÍ, MOSTNÍ ZÁVĚRY SCHÉMA LOŽISEK		
Valbek, spol. s r.o. Vaňurova 505/17 460 07 Liberec 3	208		