



PŮDORYS 1:100

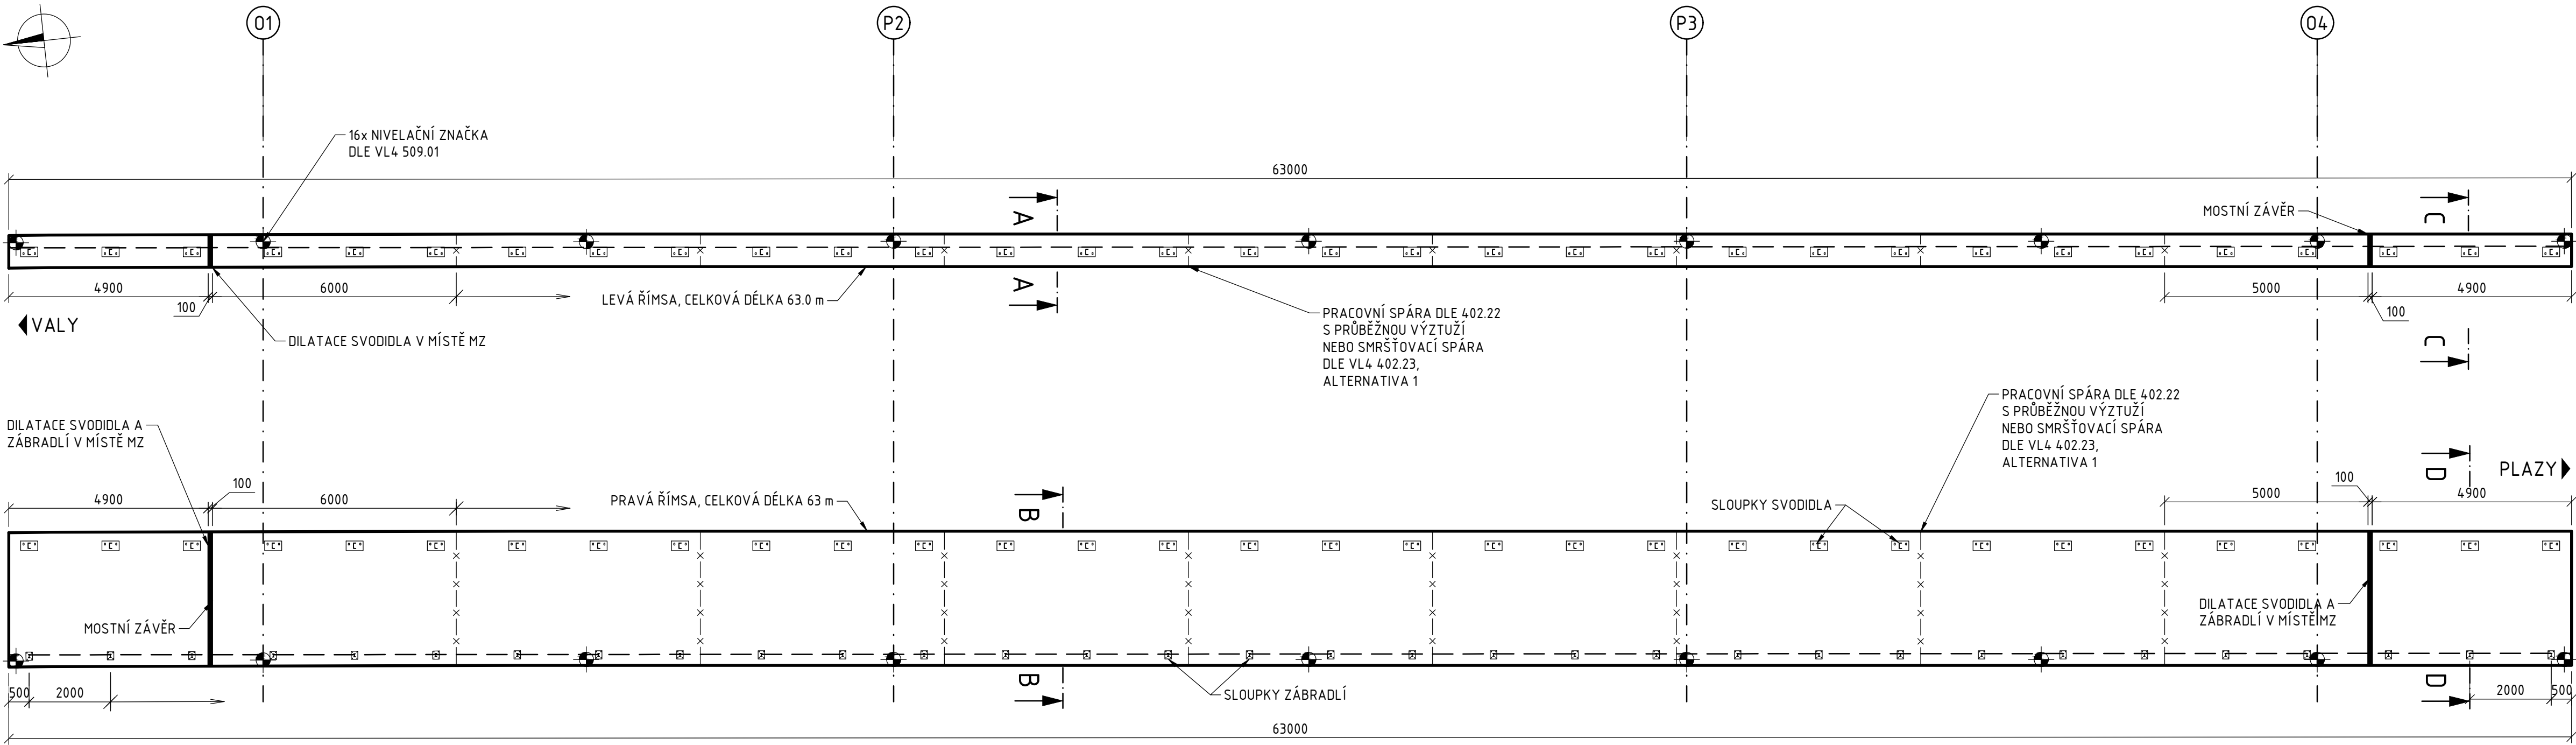


ŘEZ A-A 1:20

KRAJNÍ ŘÍMSA SE ZÁBRADELNÍM SVODIDLEM
DLE VL4 101.05

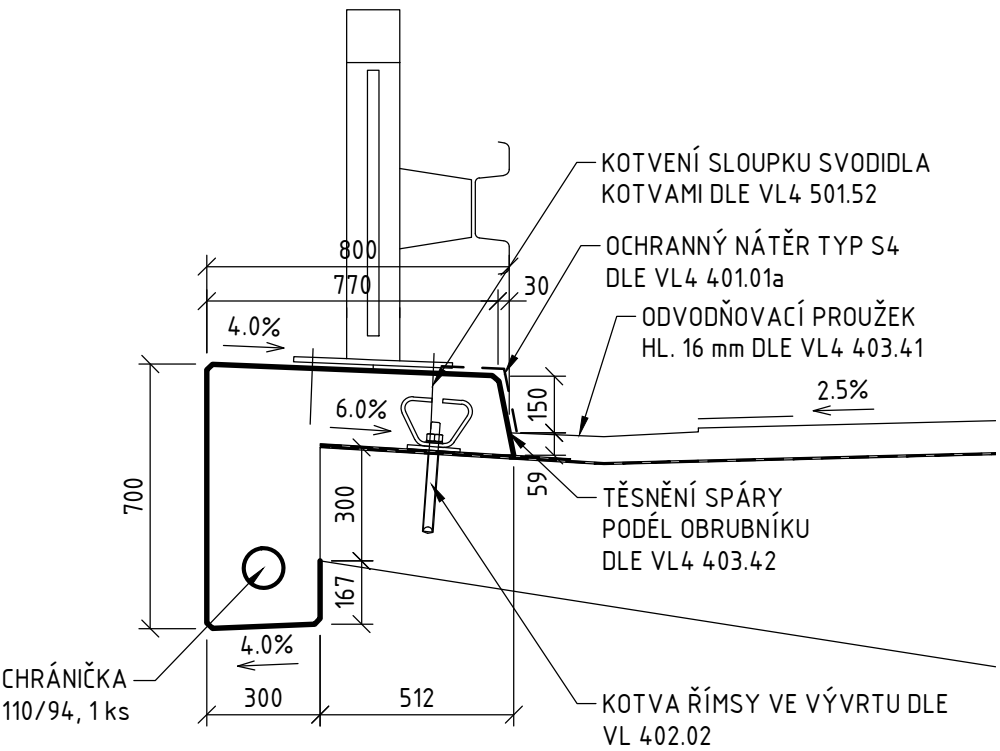


ŘEZ B-B 1:20



KRAJNÍ ŘÍMSA SE ZÁBRADELNÍM SVODIDLEM
DLE VL4 101.07

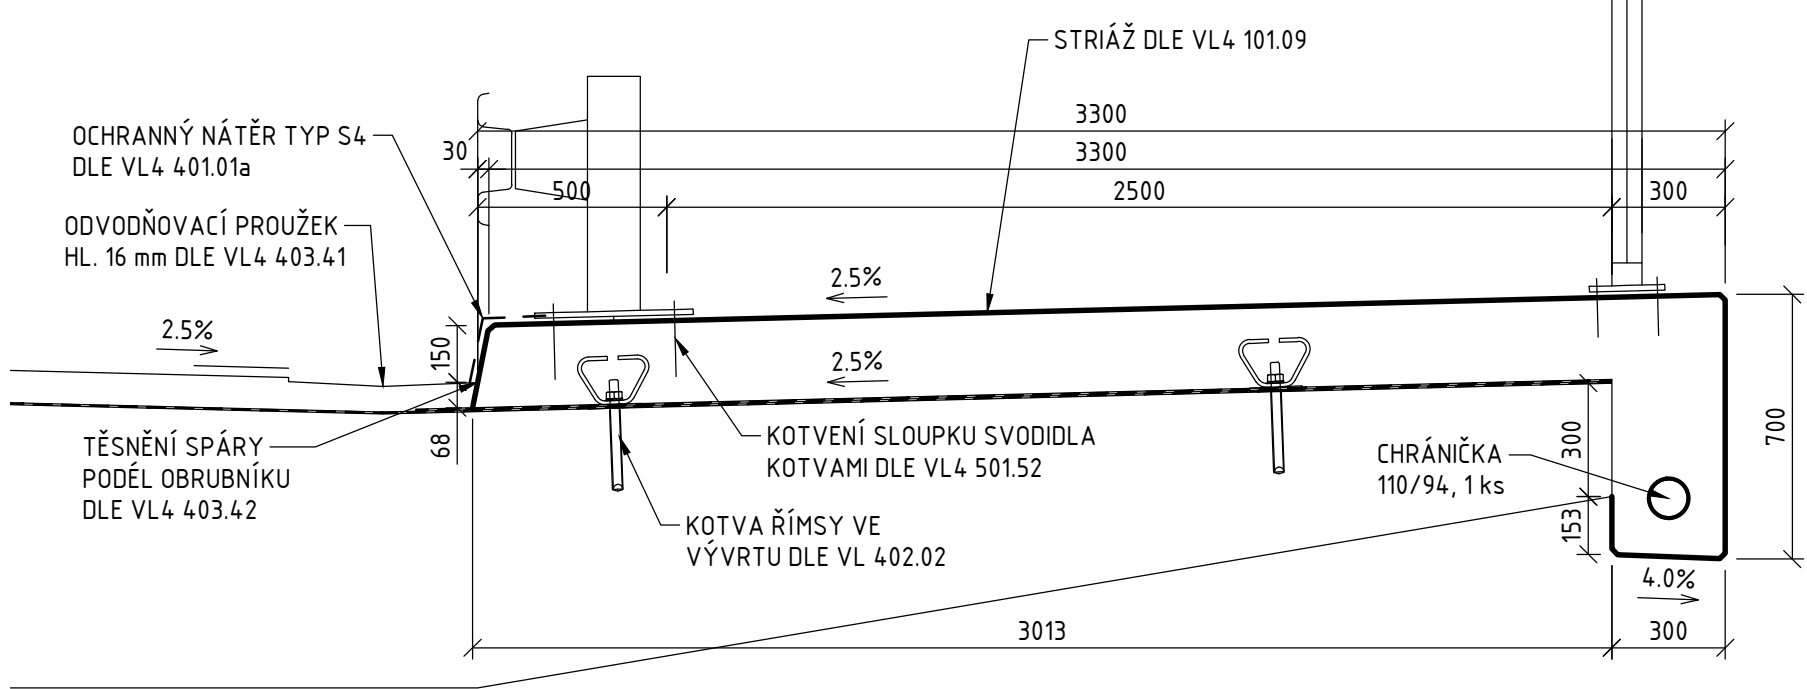

ŘEZ C-C 1:20

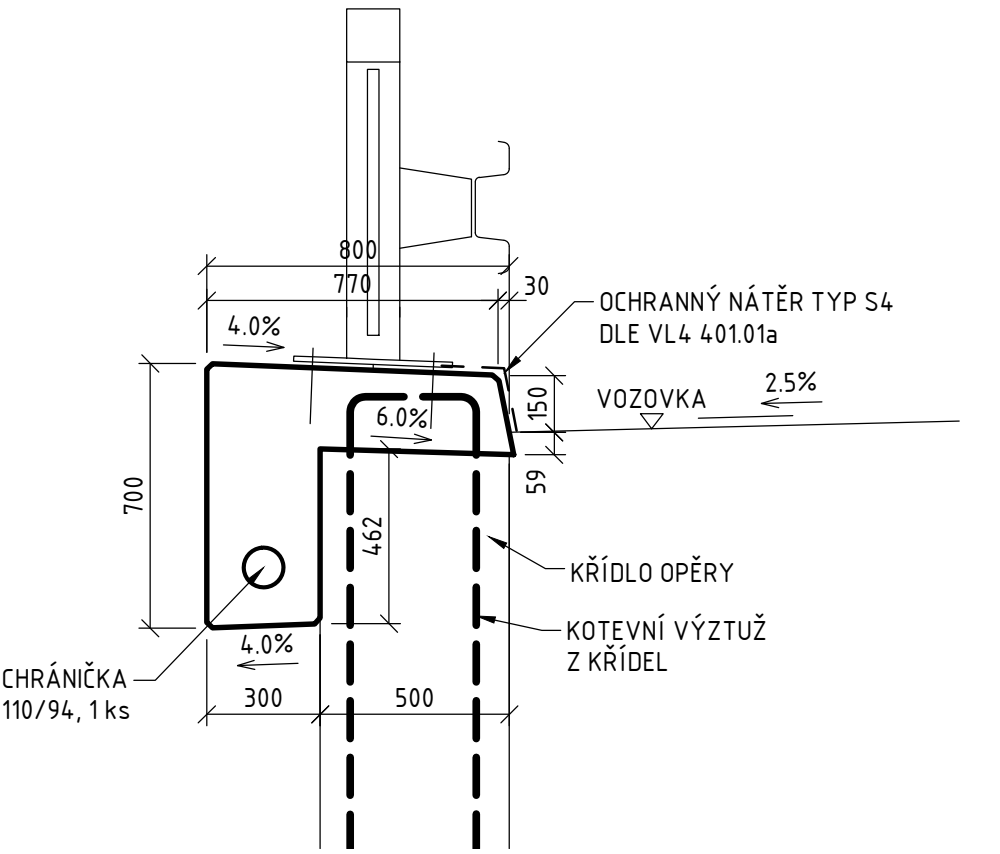

ŘEZ D-D 1:20

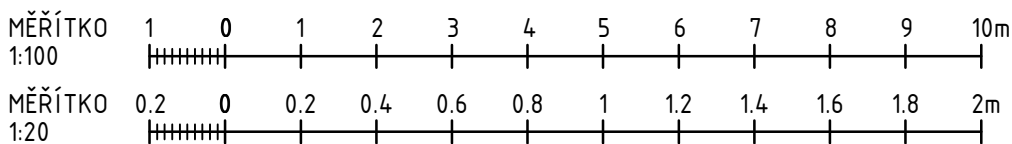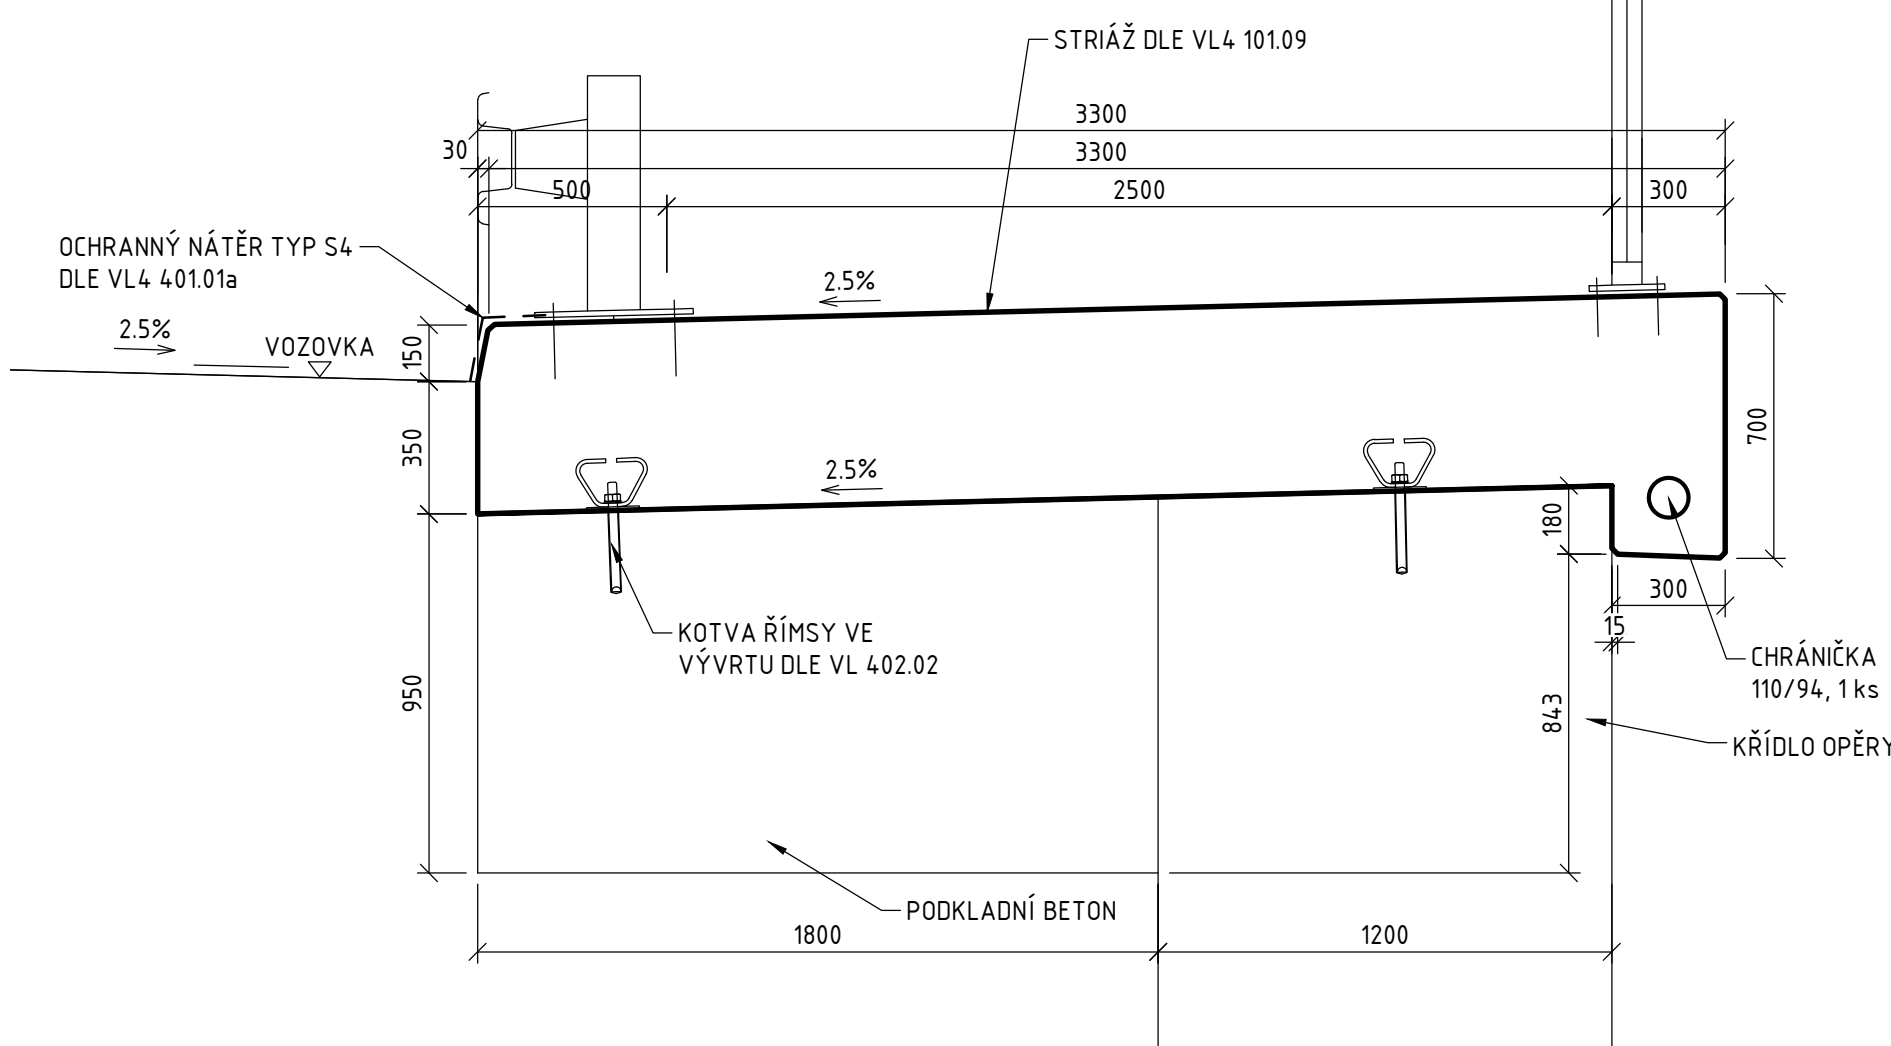

POZNÁMKY:

- NEDÍLNOU SOUČÁSTÍ VÝKRESU JSOU POZNÁMKY A SPECIFIKACE UVEDENÉ NA VÝKRESE POZNÁMEK A TECHNICKÝCH SPECIFIKACÍ

Souřadnicový systém: S-JTSK
Výškový systém: Bpv

SO 221 NADJEZD PŘELOŽKY III/2768 V KM 2,200

Objednatel:



Ředitelství silnic a dálnic s. p.
Čerčanská 2023/12, Krč, 140 00 Praha 4



Valbek, spol. s r.o.
Vaňurova 505/17
460 07 Liberec 3



Vypracoval	M. KNESPLOVÁ		Zak. číslo	21-L113-001	
Zodp. projektant	ING. S. RŮŽIČKA	<i>Bazila</i>	Datum	02/2025	
Tech. kontrola	ING. I. BELDA	<i>Bazila</i>	Stupeň	PDPS	
Akce	I/16 MLADÁ BOLESLAV - MARTINOVICE			Počet formátů	8x A4
				Měřitko	1:100,20
				Č. přílohy	Paré
Příloha				209	
TVAR ŘÍMS					