

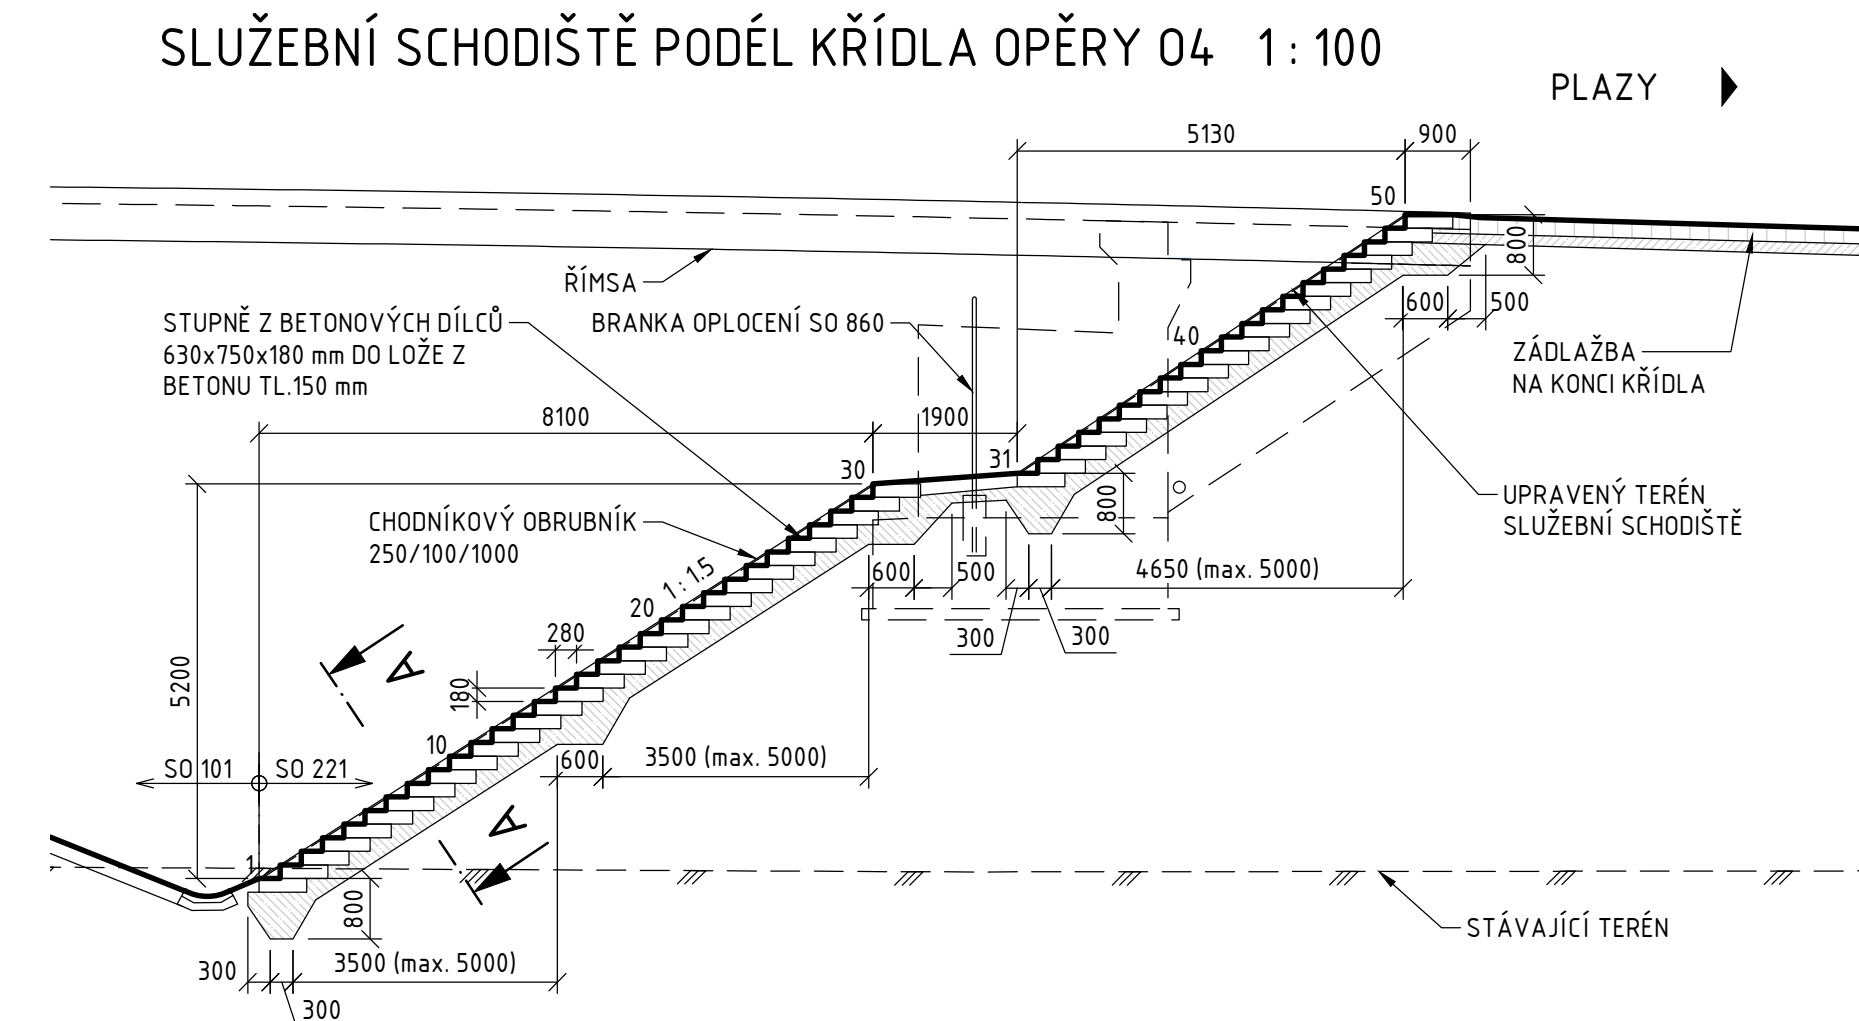


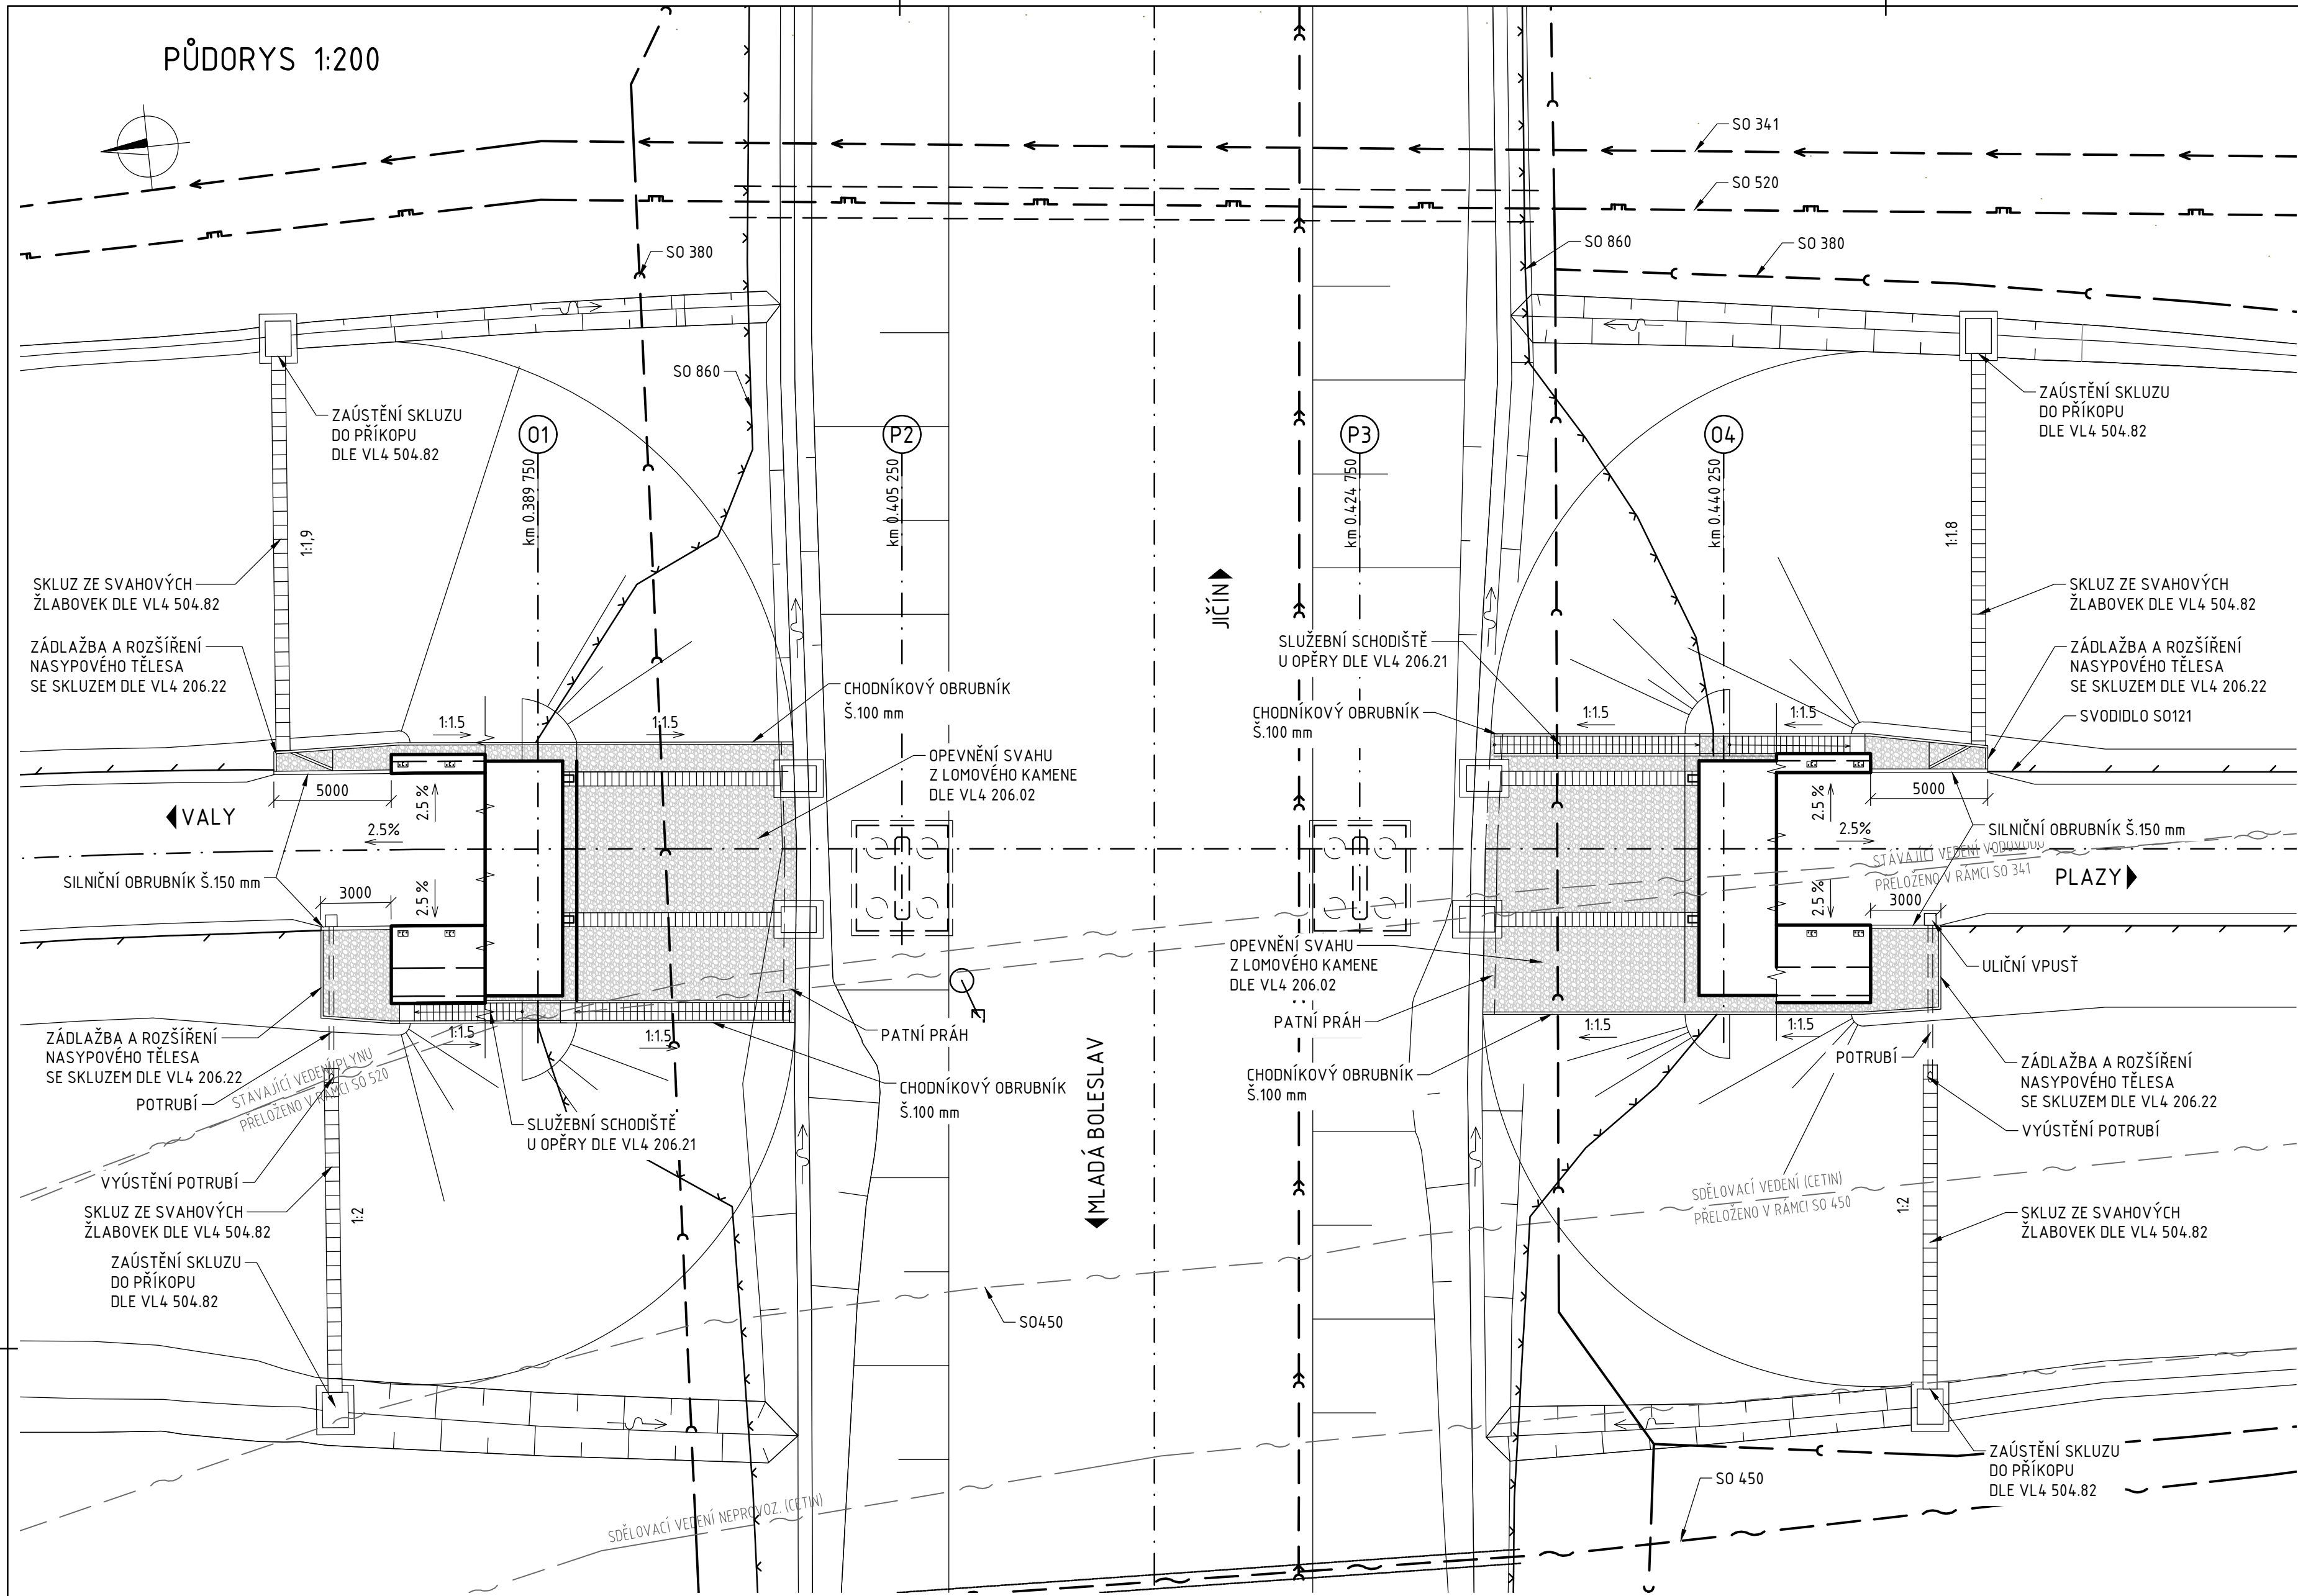


PODÉLNÝ ŘEZ ODLÁŽDĚNÍM POD MOSTEM 1:100

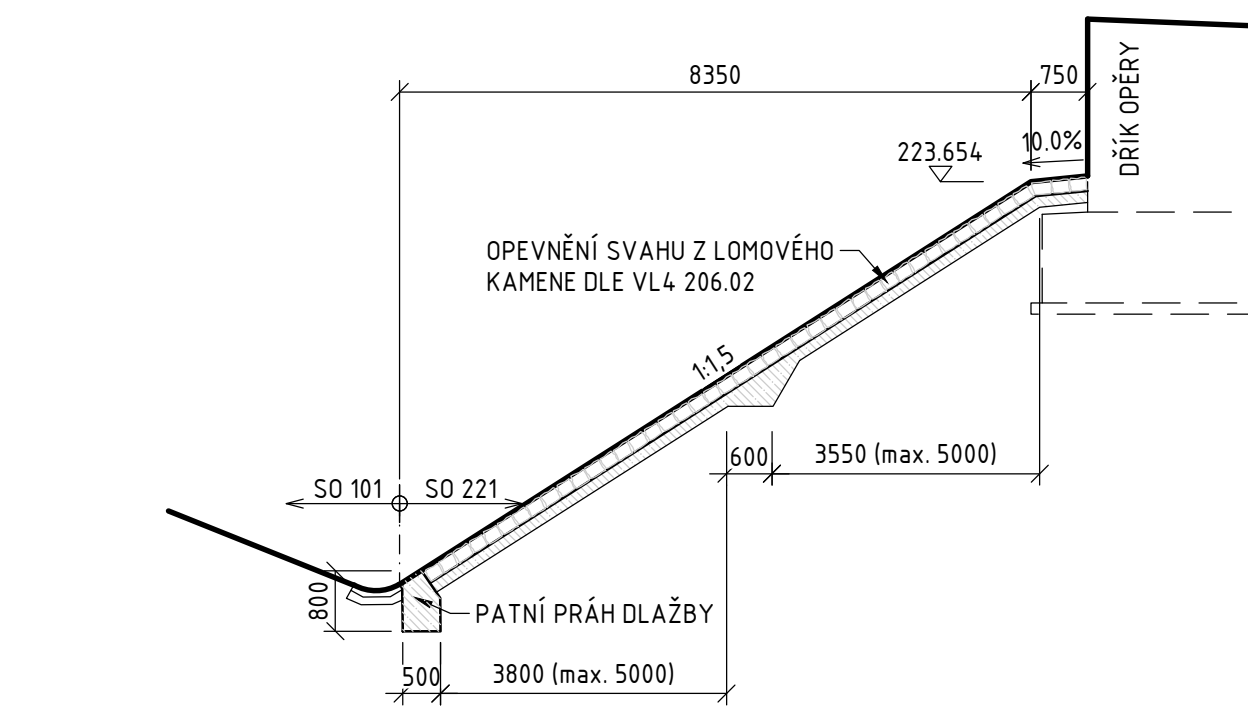


POZNÁMKY:

- NEDÍLNOU SOUČÁSTÍ VÝKRESU JSOU POZNÁMKY A SPECIFIKACE UVEDENÉ NA VÝKRESE POZNÁMEK A TECHNICKÝCH SPECIFIKACÍ


PODÉLNÝ ŘEZ SKLUZEM POD MOSTEM 1:100

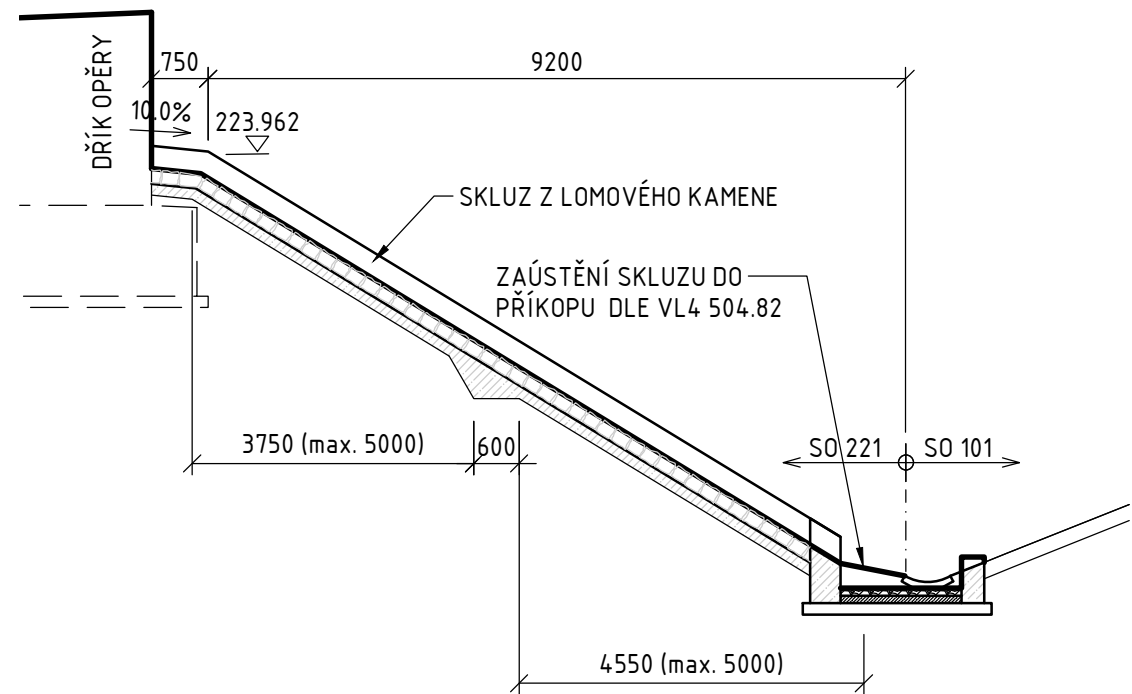


PODÉLNÝ ŘEZ ODLÁŽDĚNÍM POD MOSTEM 1:100

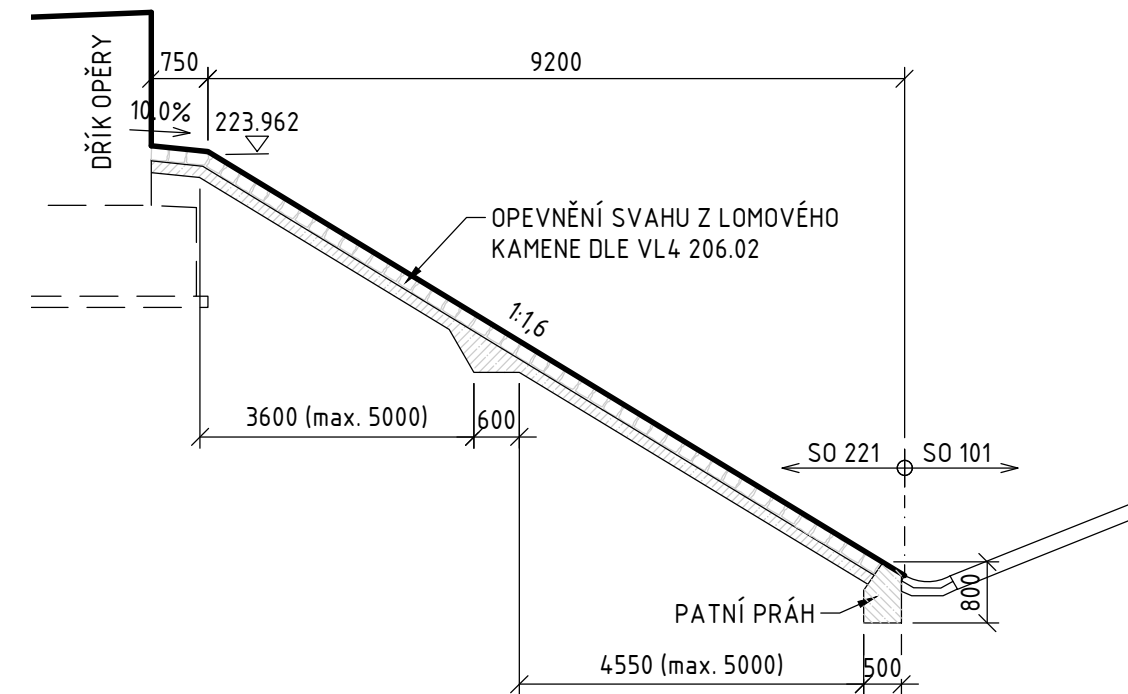



SLUŽEBNÍ SCHODIŠTĚ PODÉL KŘÍDLA OPĚRY 01 1:100

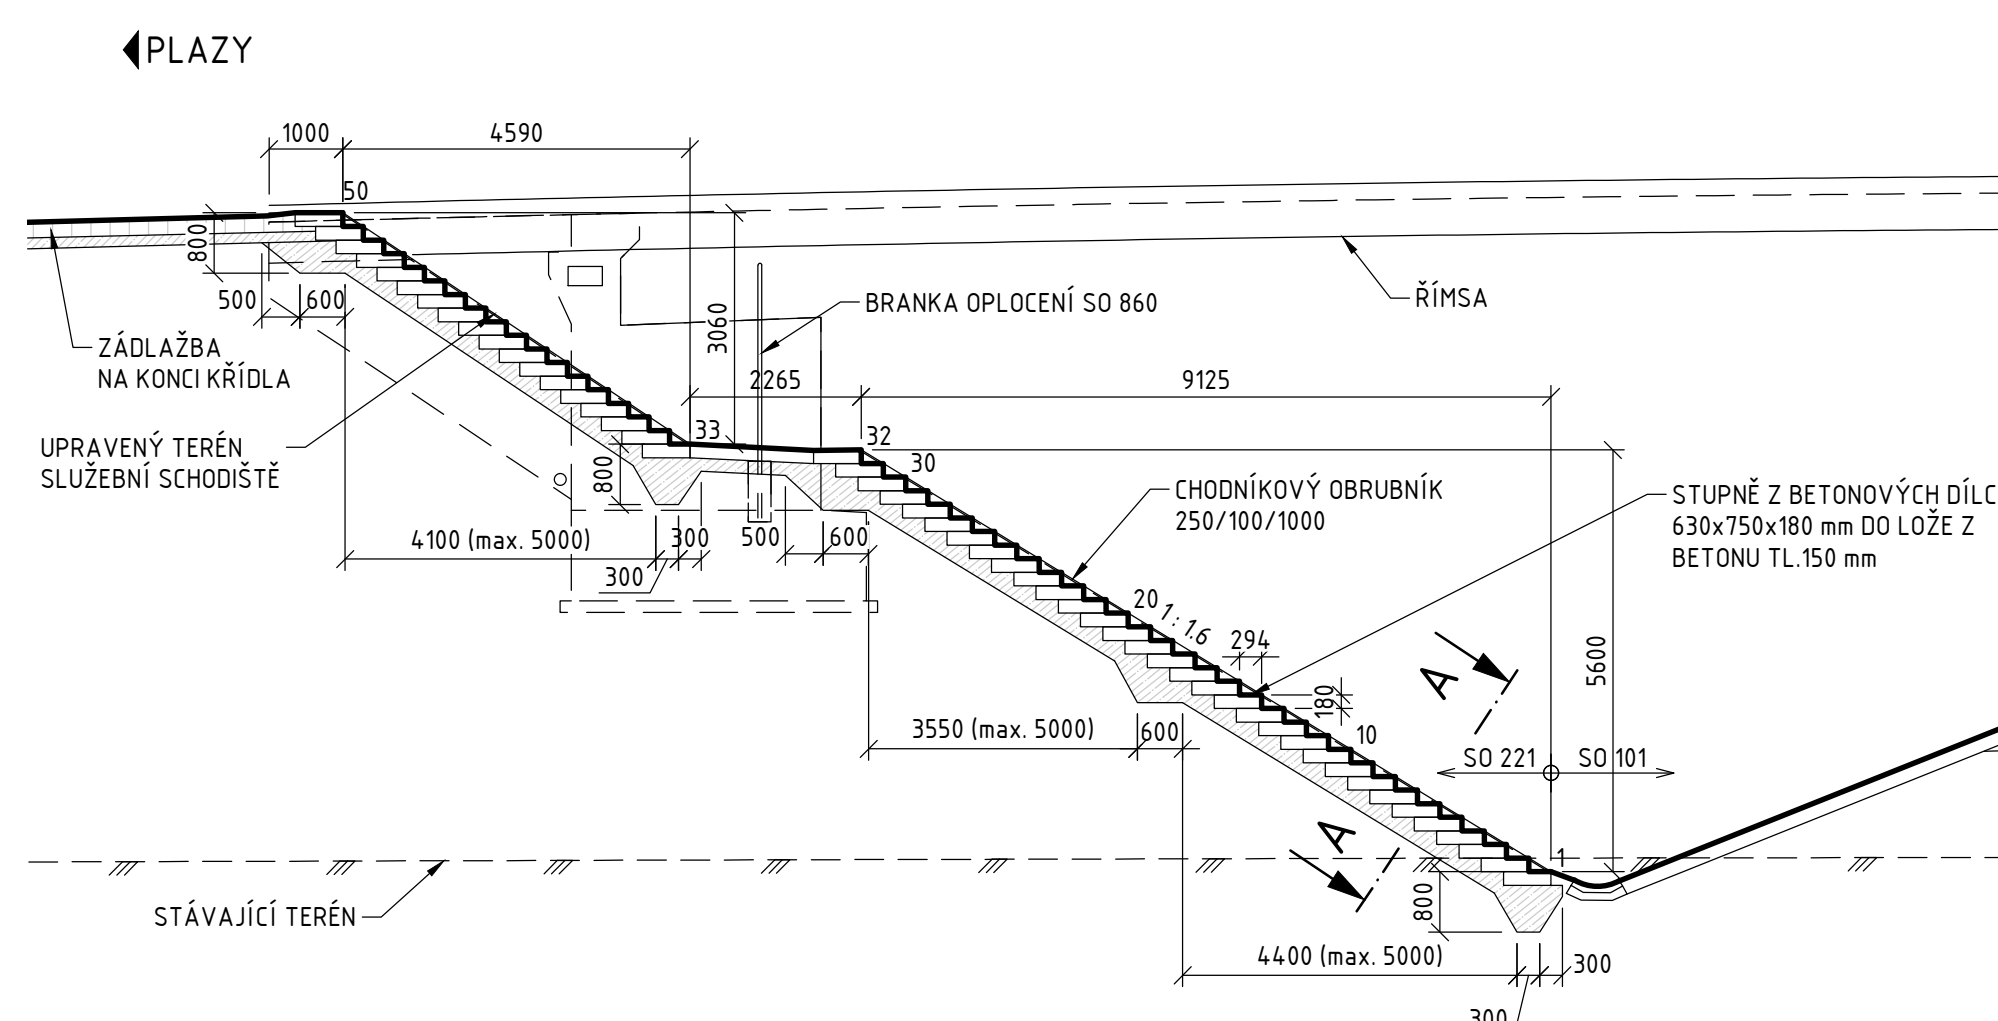

PŘÍČNÝ ŘEZ SKLUZEM Z LOMOVÉHO KAMENE 1:25

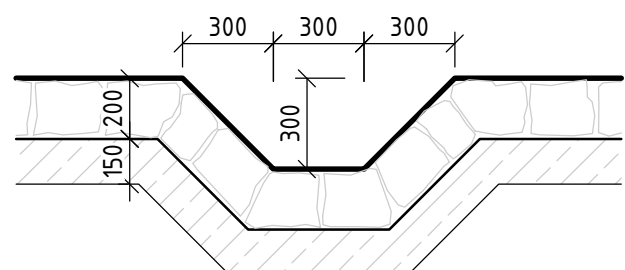

ŘEZ A-A 1:25

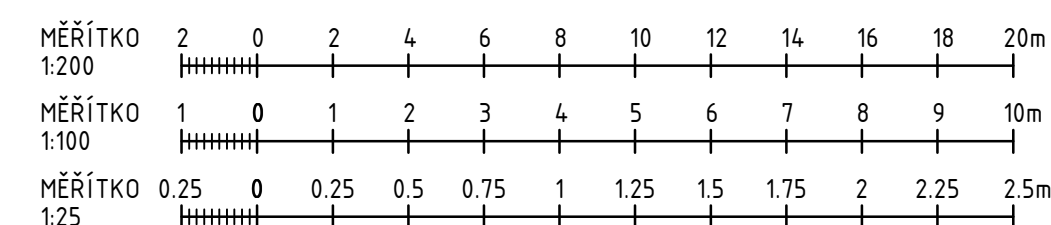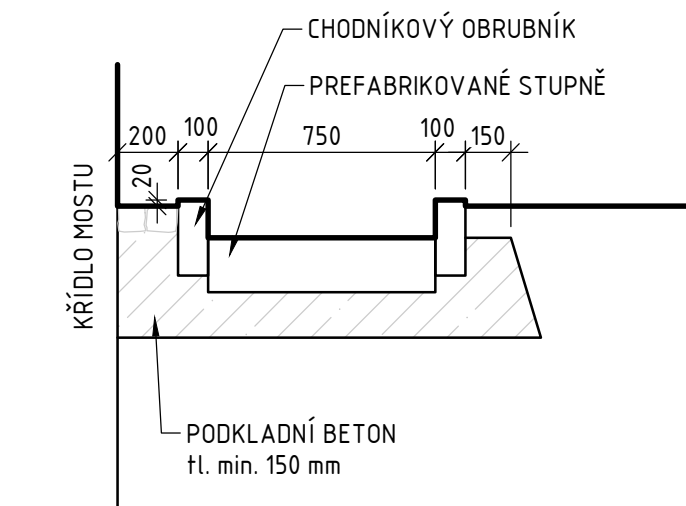

Souřadnicový systém: S-JTSK
Výškový systém: Bpv

SO 221 NADJEZD PŘELOŽKY III/2768 V KM 2,200	
	Ředitelství silnic a dálnic s. p. Čerčanská 2023/12, Krč, 140 00 Praha 4

	Valbek, spol. s r.o. Vaňurova 505/17 460 07 Liberec 3

	Vypracoval M. KNESPLOVÁ Zodp. projektant ING. S. RŮŽIČKA Tech. kontrola ING. I. BELDA Akce I/16 MLADÁ BOLESLAV - MARTINOVICE	Zak. číslo 21-L113-001 Datum 02/2025 Stupeň PDPS Počet formátů 8x A4 Měřítko 1:200, 100, 25 Č. přílohy Paré

Zhotovitel: Valbek, spol. s r.o. Vaňurova 505/17 460 07 Liberec 3	Příloha ÚPRAVY POD MOSTEM, SLUŽEBNÍ SCHODIŠTĚ	210
---	---	-----