



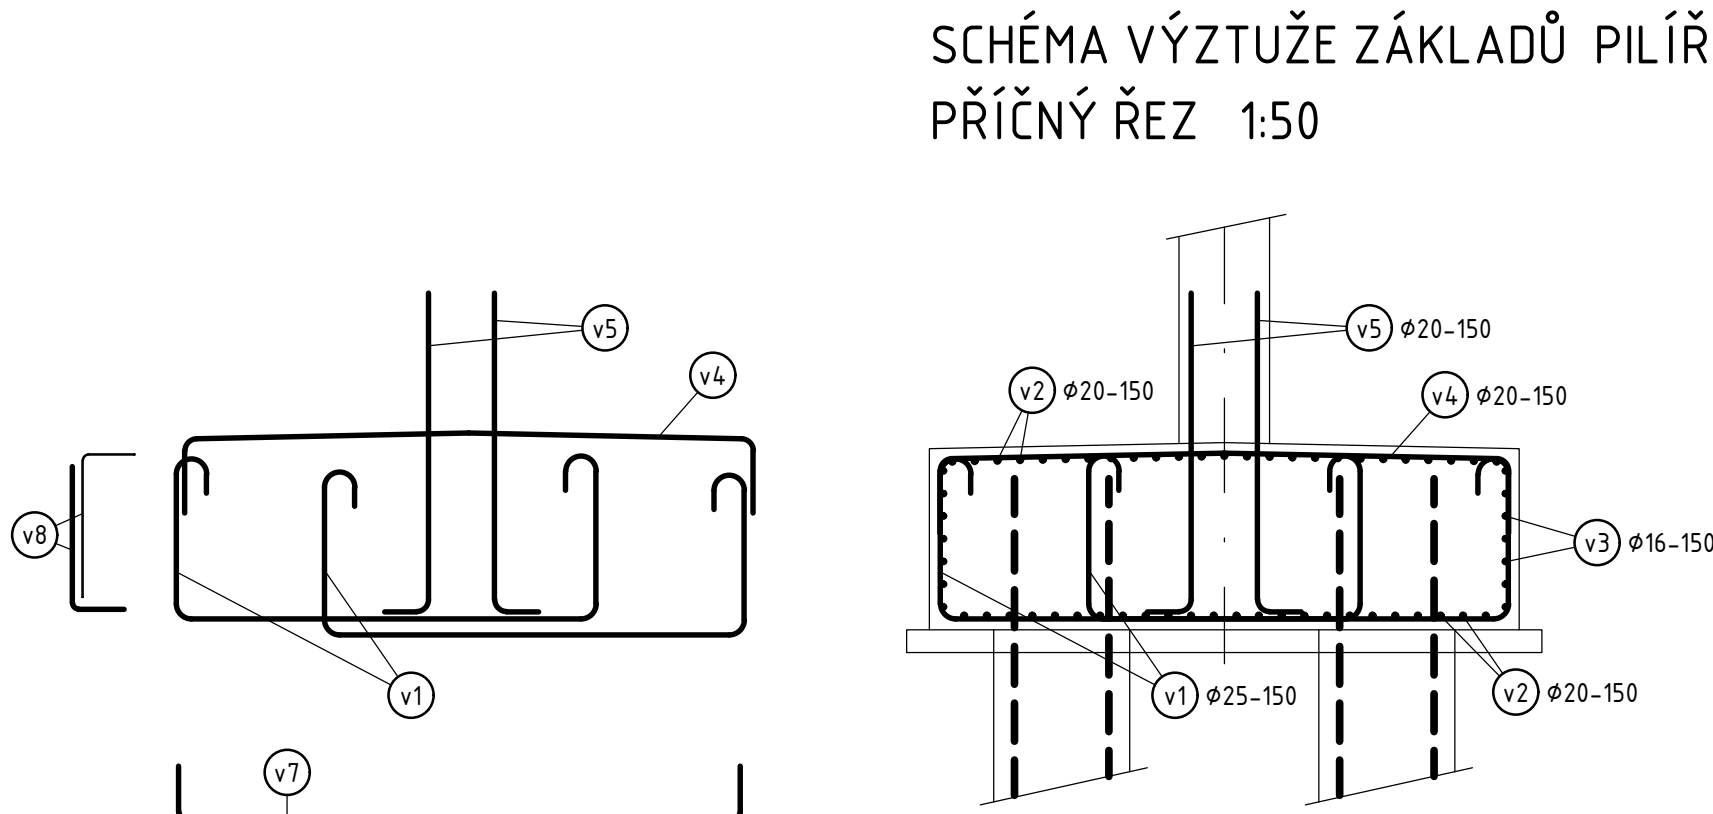



SCHÉMA VÝZTUŽE OPĚRY 01
PŘÍČNÝ ŘEZ 1:50

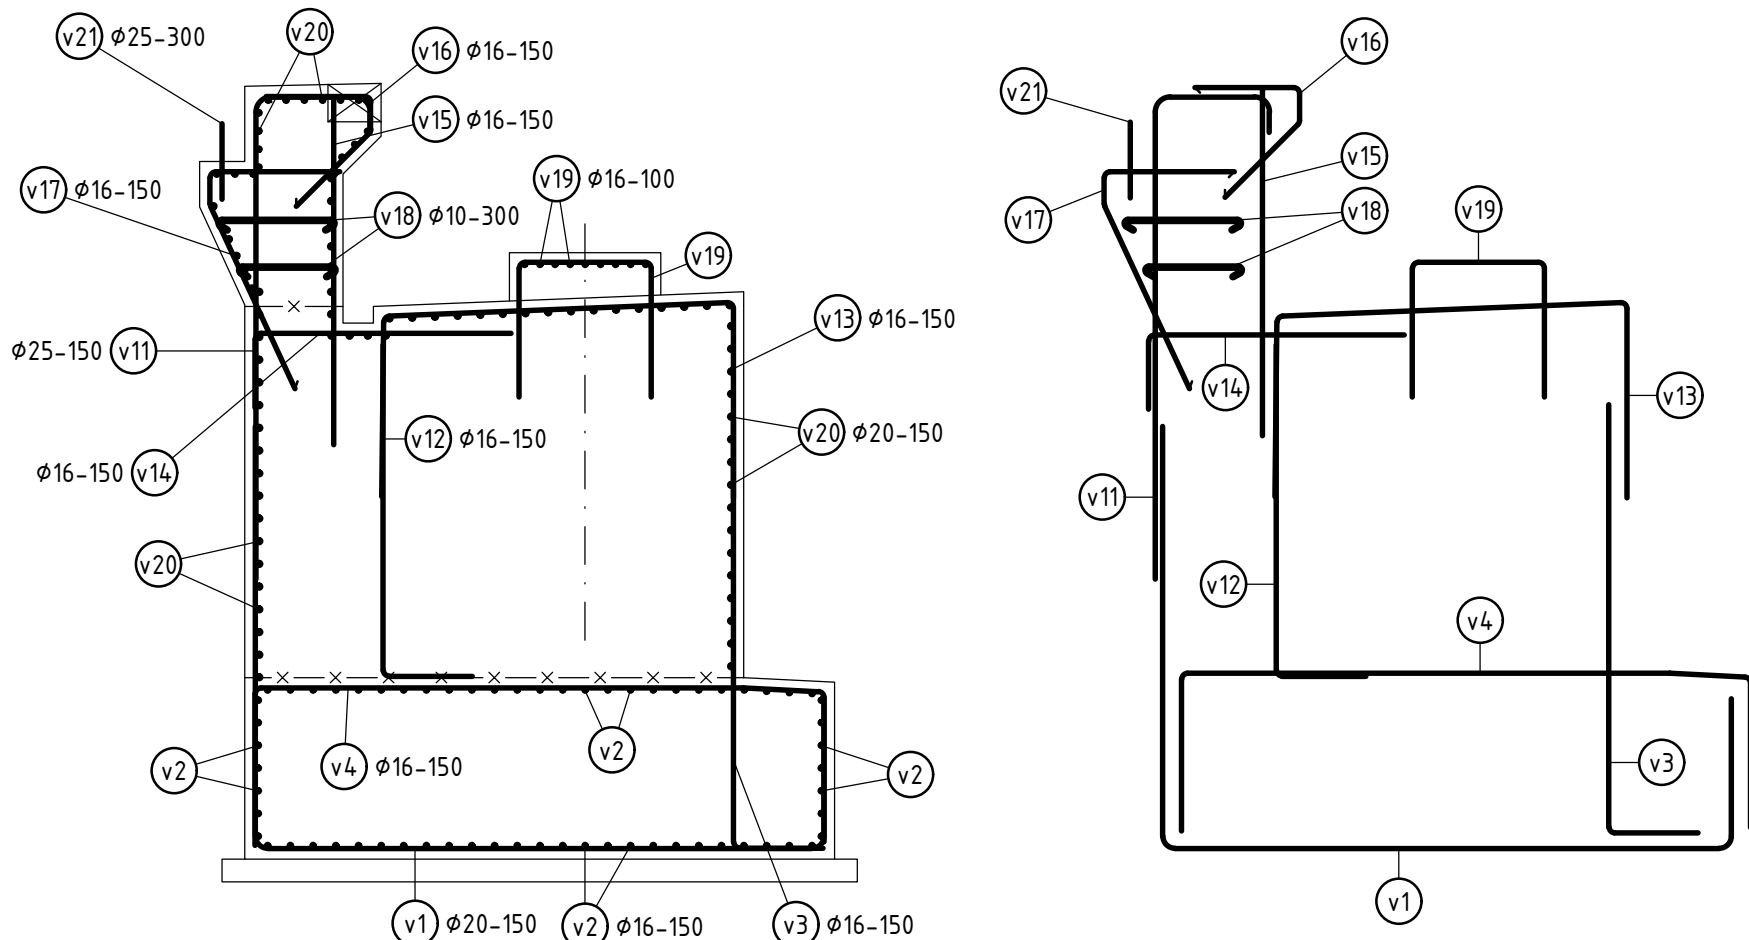


ŘEZ KŘÍDLEM 1:50

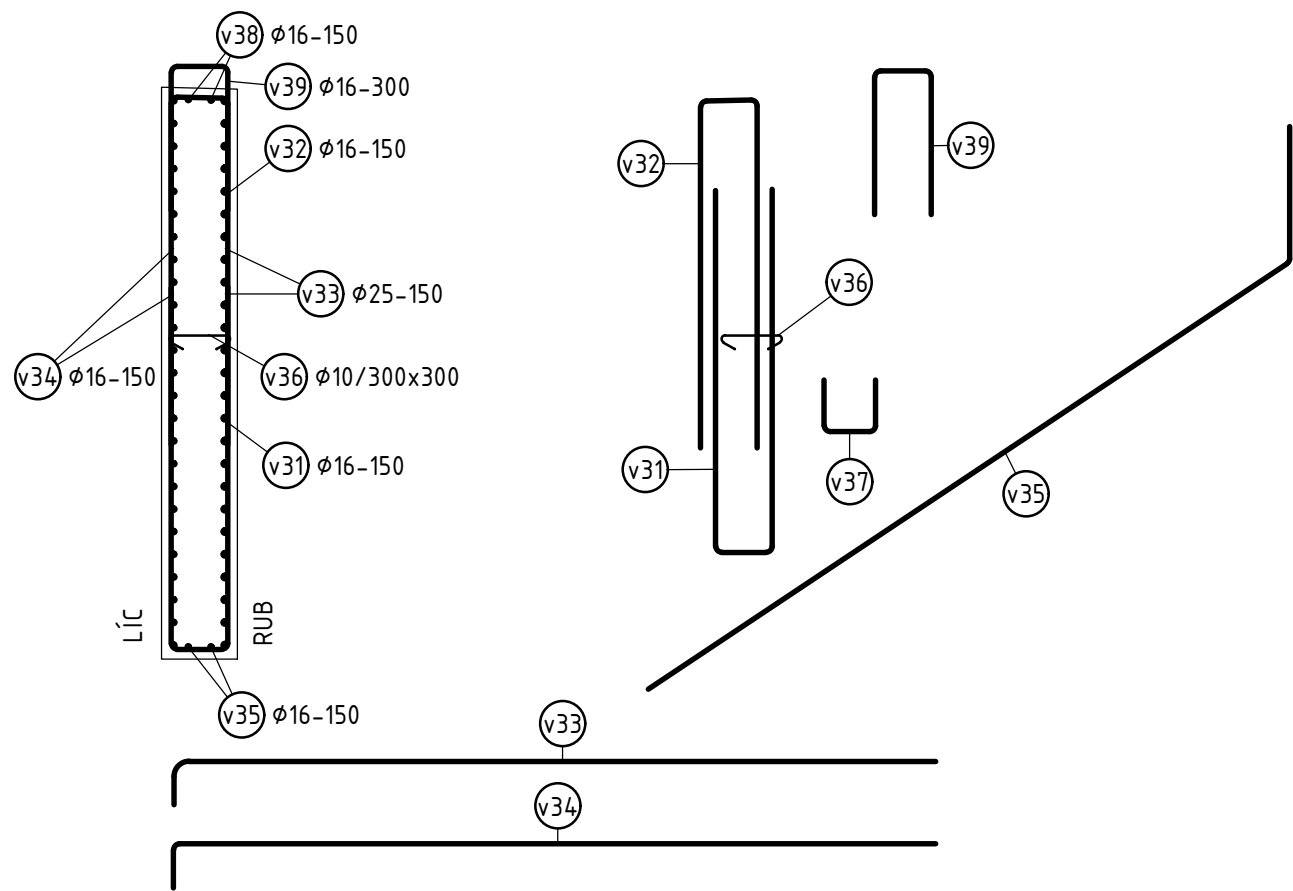


ŘEZ DŘÍKEM PILÍŘE 1:50

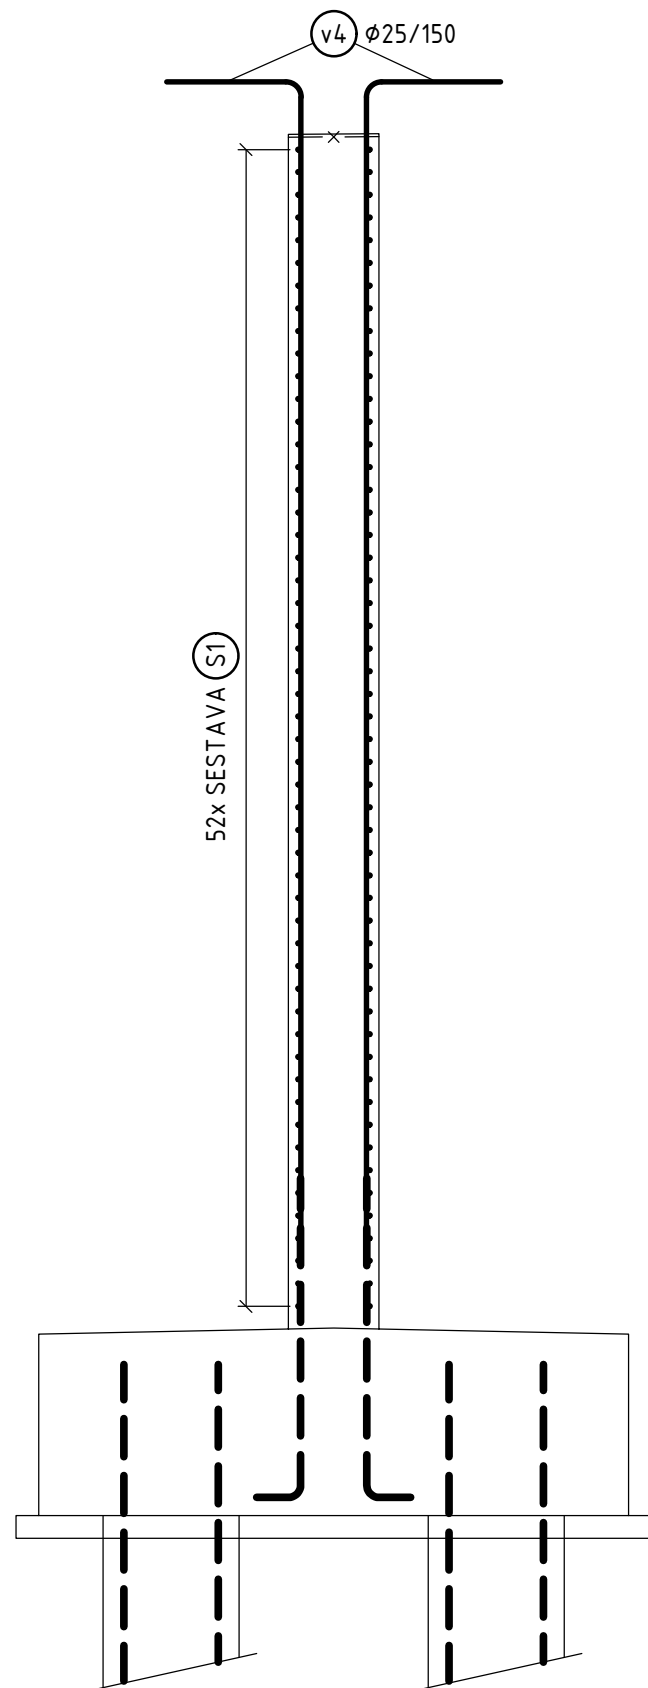

PŮDORYS DŘÍKU PILÍŘE 1:35

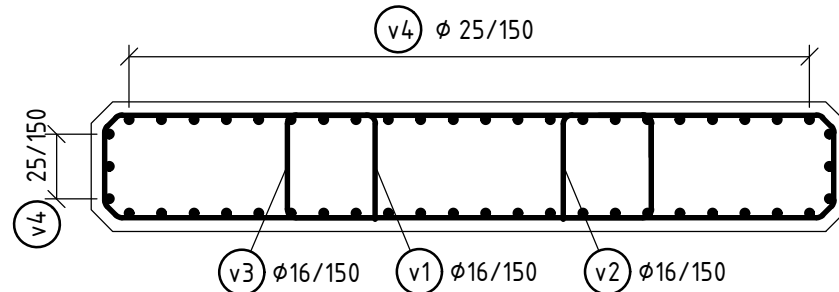

SESTAVA S1

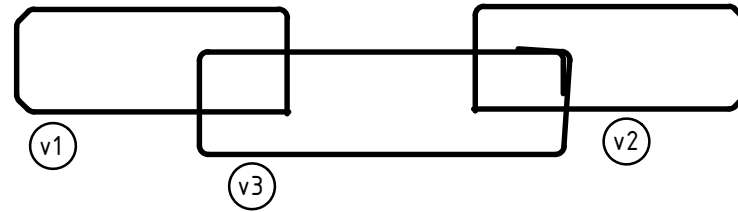

ODHAD MNOŽSTVÍ BETONÁŘSKÉ VÝZTUŽE SO 221	MNOŽSTVÍ VÝZTUŽE V %	MNOŽSTVÍ VÝZT. V KG/M3
VÝZTUŽ PILOT POD OPĚROU 1, D 900MM	0.81%	63.3
VÝZTUŽ PILOT POD OPĚROU 4, D 900MM	0.81%	63.3
VÝZTUŽ PILOT POD PILÍŘI, D 900MM	0.83%	64.9
VÝZTUŽ ZÁKLADŮ OPĚRY 01	0.97%	76.3
VÝZTUŽ ZÁKLADŮ OPĚRY 04	0.97%	76.3
VÝZTUŽ ZÁKLADŮ PILÍŘŮ	1.65%	129.3
VÝZTUŽ PILÍŘŮ	2.10%	163.3
VÝZTUŽ DŘÍKU A KŘÍDEL OPĚRY 01	0.92%	71.9
VÝZTUŽ DŘÍKU A KŘÍDEL OPĚRY 04	0.92%	71.9
VÝZTUŽ NOSNÉ KONSTRUKCE	1.67%	131.1
VÝZTUŽ ŘÍMS	1.83%	143.8
VÝZTUŽ PŘECHODOVÝCH DESEK	1.76%	137.1

Souřadnicový systém: S-JTSK
Výškový systém: Bpv

SO 221 NADJEZD PŘELOŽKY III/2768 v km 2,200

Objednatel:
**ŘEDITELSTVÍ
SILNIC
A DÁLNIC**
Ředitelství silnic a dálnic s. p.
Čerčanská 2023/12, Krč, 140 00 Praha 4

Valbek, spol. s r.o.
Vaňurova 505/17
460 07 Liberec 3

	Vypracoval	M. KNESPOVÁ	Zak. číslo	21-L113-001	
	Zodp. projektant	ING. S. RŮŽIČKA	Datum	02/2025	
	Tech. kontrola	ING. I. BELDA	Stupeň	PDPS	
	Akce	I/16 MLADÁ BOLESLAV - MARTINOVICE			
Zhotovitel: Valbek, spol. s r.o. Vaňurova 505/17 460 07 Liberec 3	Příloha	SCHÉMATICKÉ VÝKRESY VÝZTUŽE 1(2)		Počet formátů	8x A4
				Měřítko	-
				Č. přílohy	Paré
				301	