

SCHÉMA VÝZTUŽE NOSNÉ KONSTRUKCE
PODÉLNÝ ŘEZ 1:50



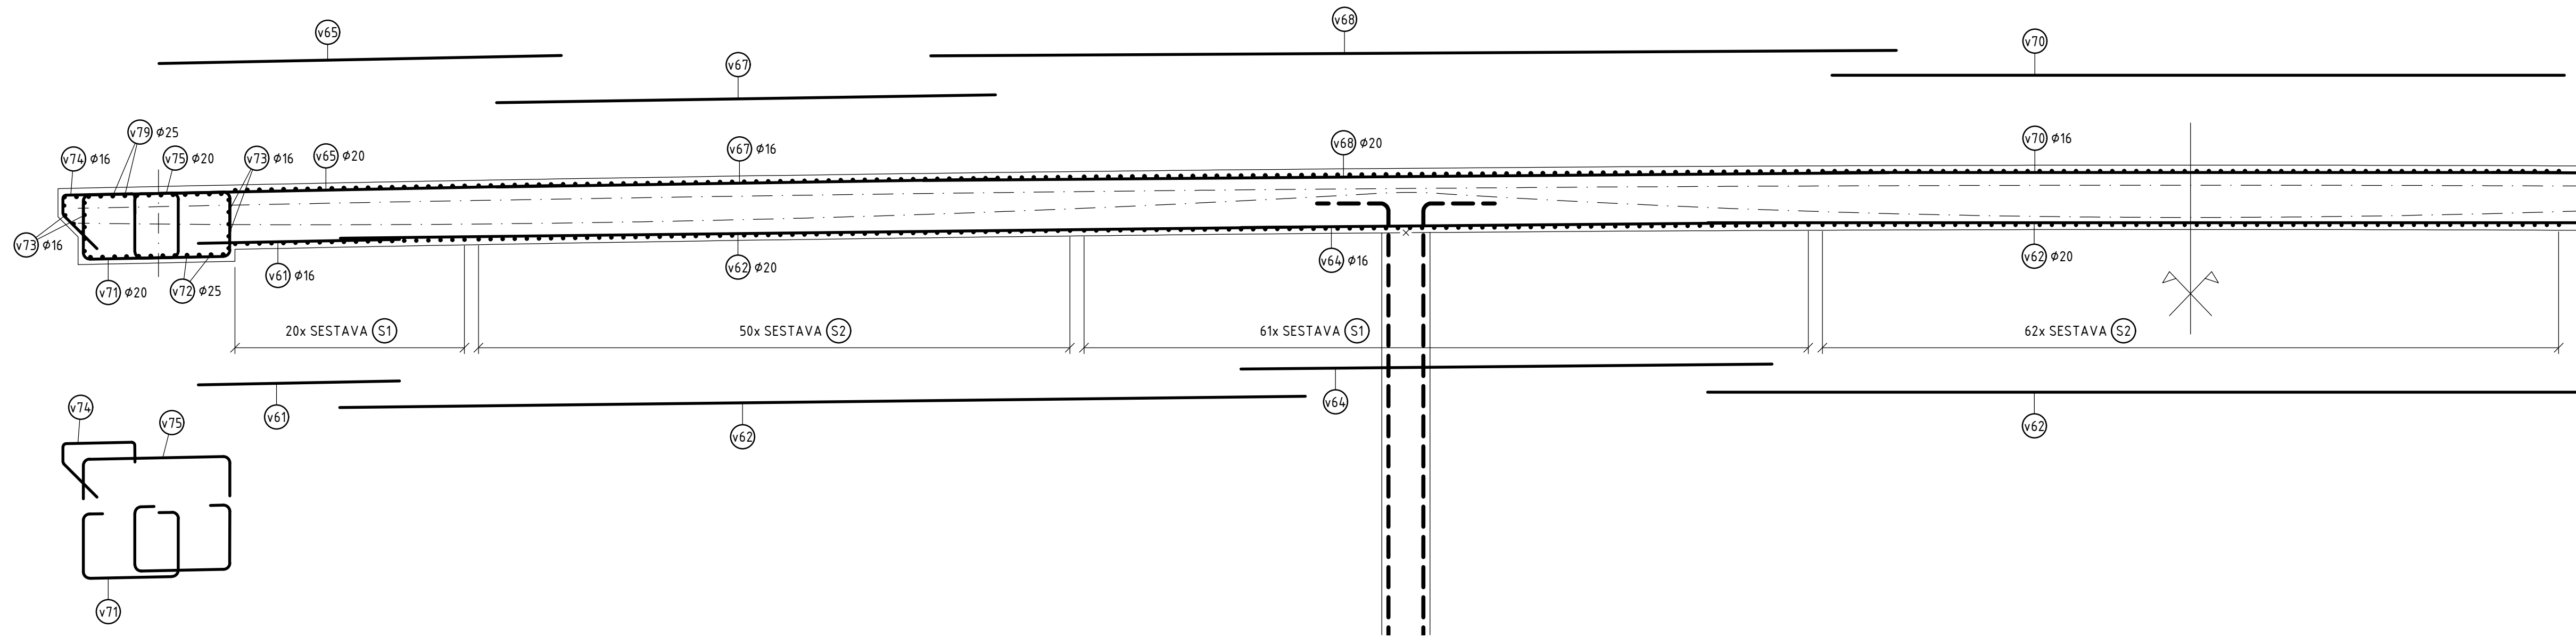



SCHÉMA VÝZTUŽE NOSNÉ KONSTRUKCE
PŘÍČNÝ ŘEZ PŘED OPĚROU 1:50

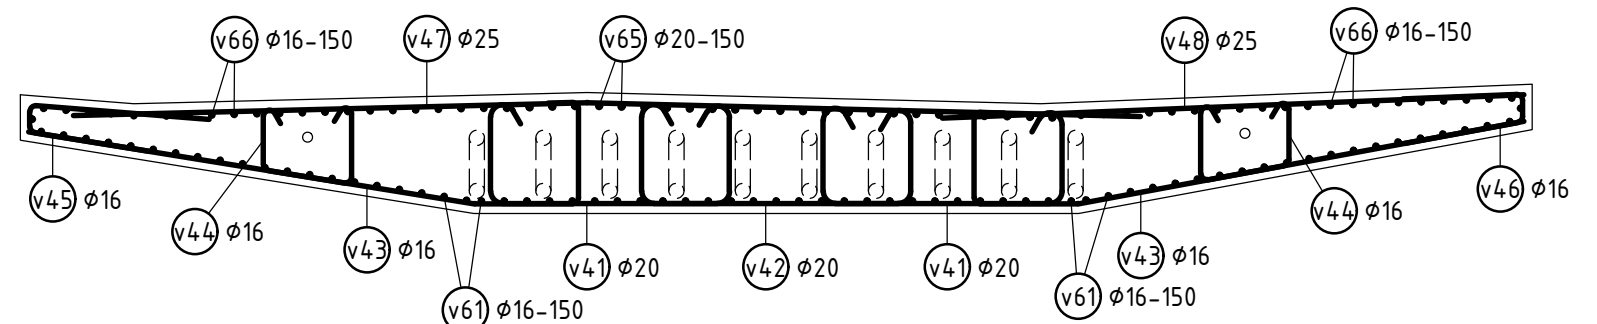


SESTAVA (S1)

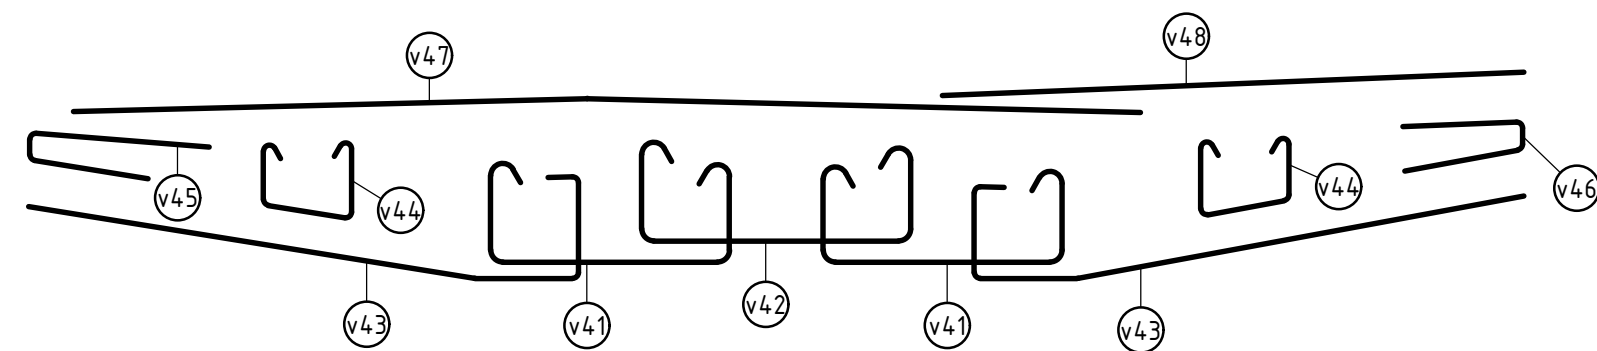


PŘÍČNÝ ŘEZ V POLI 1:50

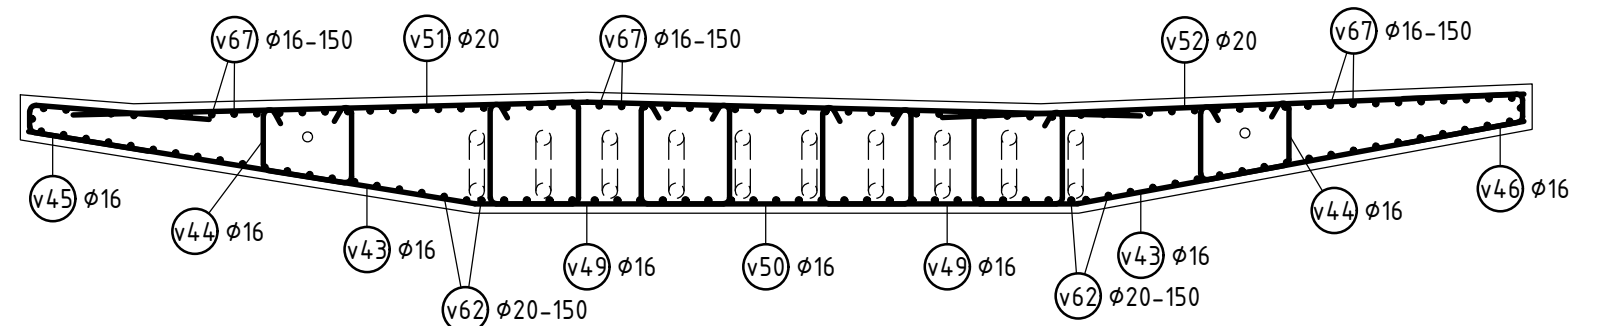

SESTAVA (S2)

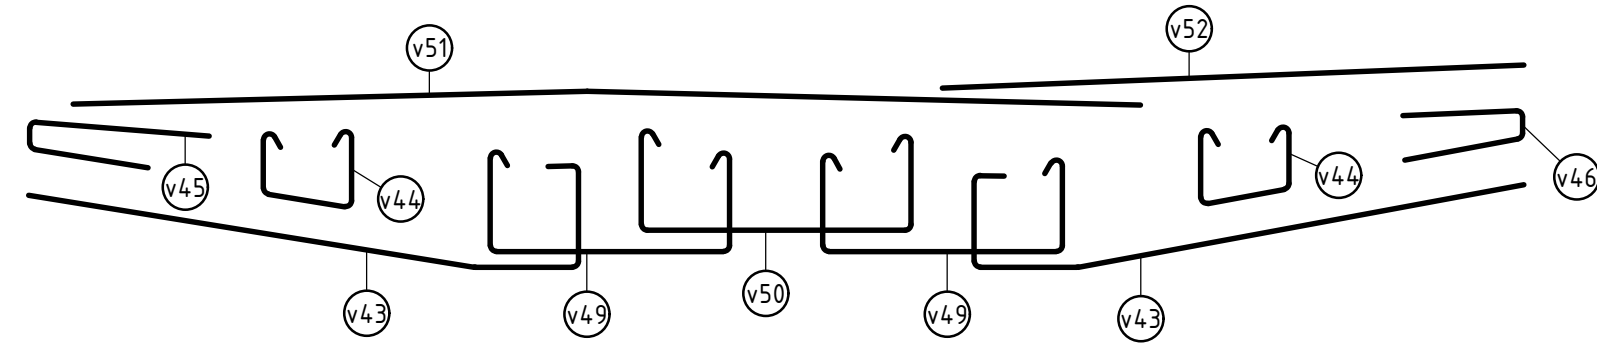

PŘÍČNÍK NAD OPĚROU 1:50

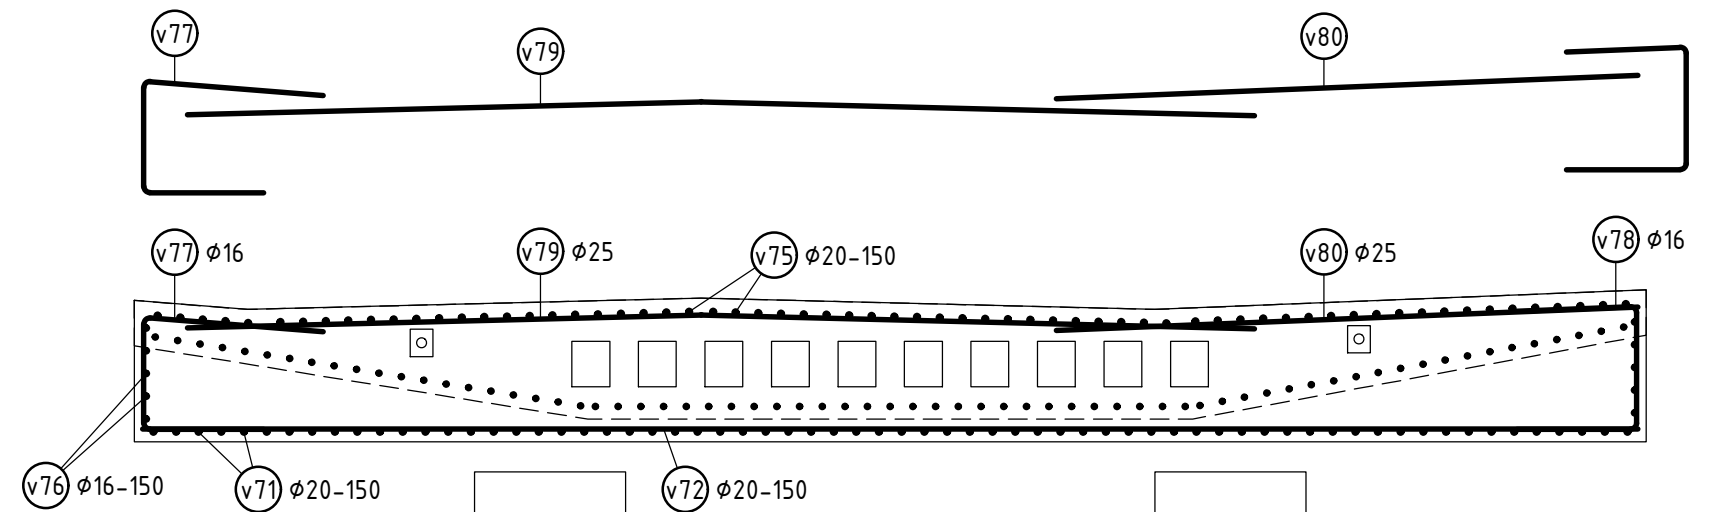

Souřadnicový systém: S-JTSK
Výškový systém: Bpv

SO 221 NADJEZD PŘELOŽKY III/2768 v km 2,200

Objednatel:



Ředitelství silnic a dálnic s. p.
Čerčanská 2023/12, Krč, 140 00 Praha 4



Valbek, spol. s r.o.
Vaňurova 505/17
460 07 Liberec 3

	Vypracoval	M. KNESPOVÁ	Zak. číslo	21-L113-001
	Zodp. projektant	ING. S. RŮŽIČKA	Datum	02/2025
	Tech. kontrola	ING. I. BELDA	Stupeň	PDPS
	Akce	I/16 MLADÁ BOLESLAV - MARTINOVICE		Počet formátů
Zhotovitel:	Příloha	SCHÉMATICKÉ VÝKRESY VÝZTUŽE 2(2)	Měřítko	-
			Č. přílohy	Paré
Valbek, spol. s r.o. Vaňurova 505/17 460 07 Liberec 3			302	