


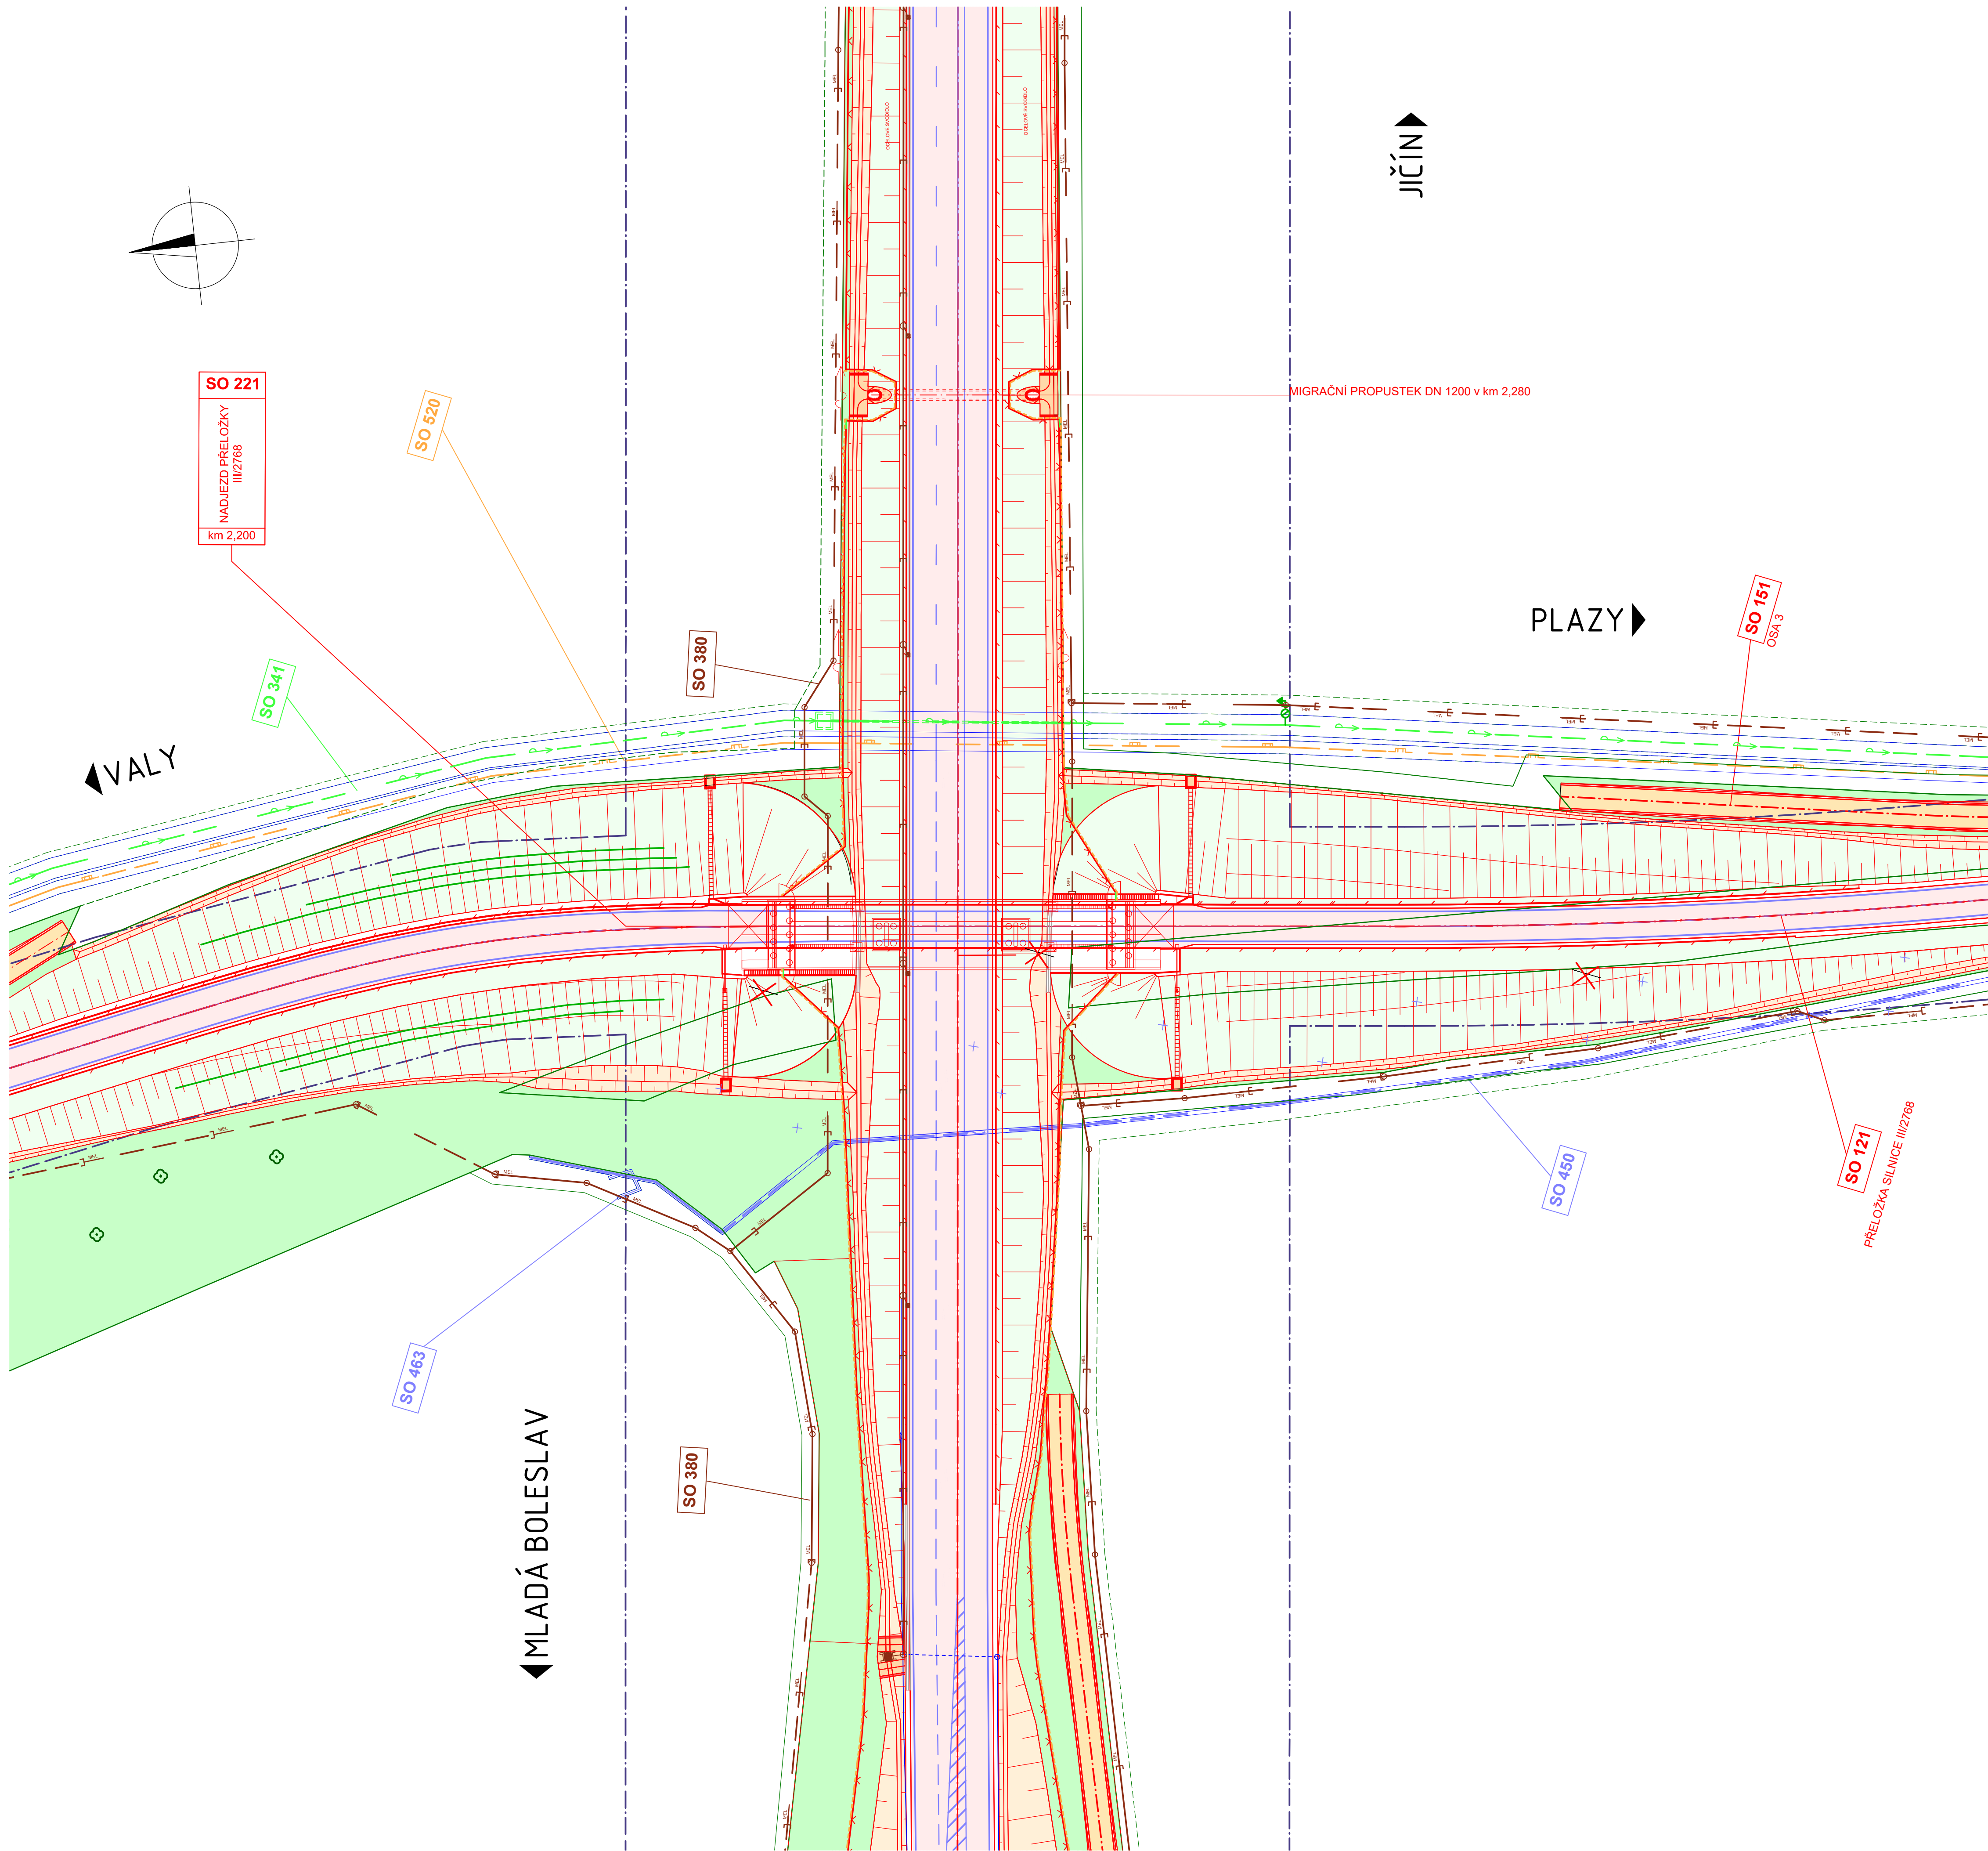

Souřadnicový systém: S-JTSK
Výškový systém: Bpv

SO 221 NADJEZD PŘELOŽKY III/2768 V KM 2,200

Objednatel:



Ředitelství silnic a dálnic s. p.
Čerčanská 2023/12, Krč, 140 00 Praha 4



Valbek, spol. s r.o.
Vaňurova 505/17
460 07 Liberec 3



Vypracoval: ING. S. RŮŽIČKA
Zodp. projektant: ING. S. RŮŽIČKA
Tech. kontrola: ING. I. BELDA
Akce: I/16 MLADÁ BOLESLAV - MARTINOVICE

Zak. číslo: 21-L113-001
Datum: 02/2025
Stupeň: PDPS
Počet formátů: 8x A4
Měřítko: 1:500
Č. přílohy: Paré

Zhotovitel:
Valbek, spol. s r.o.
Vaňurova 505/17
460 07 Liberec 3

Příloha
PŘEHLEDNÁ SITUACE

401