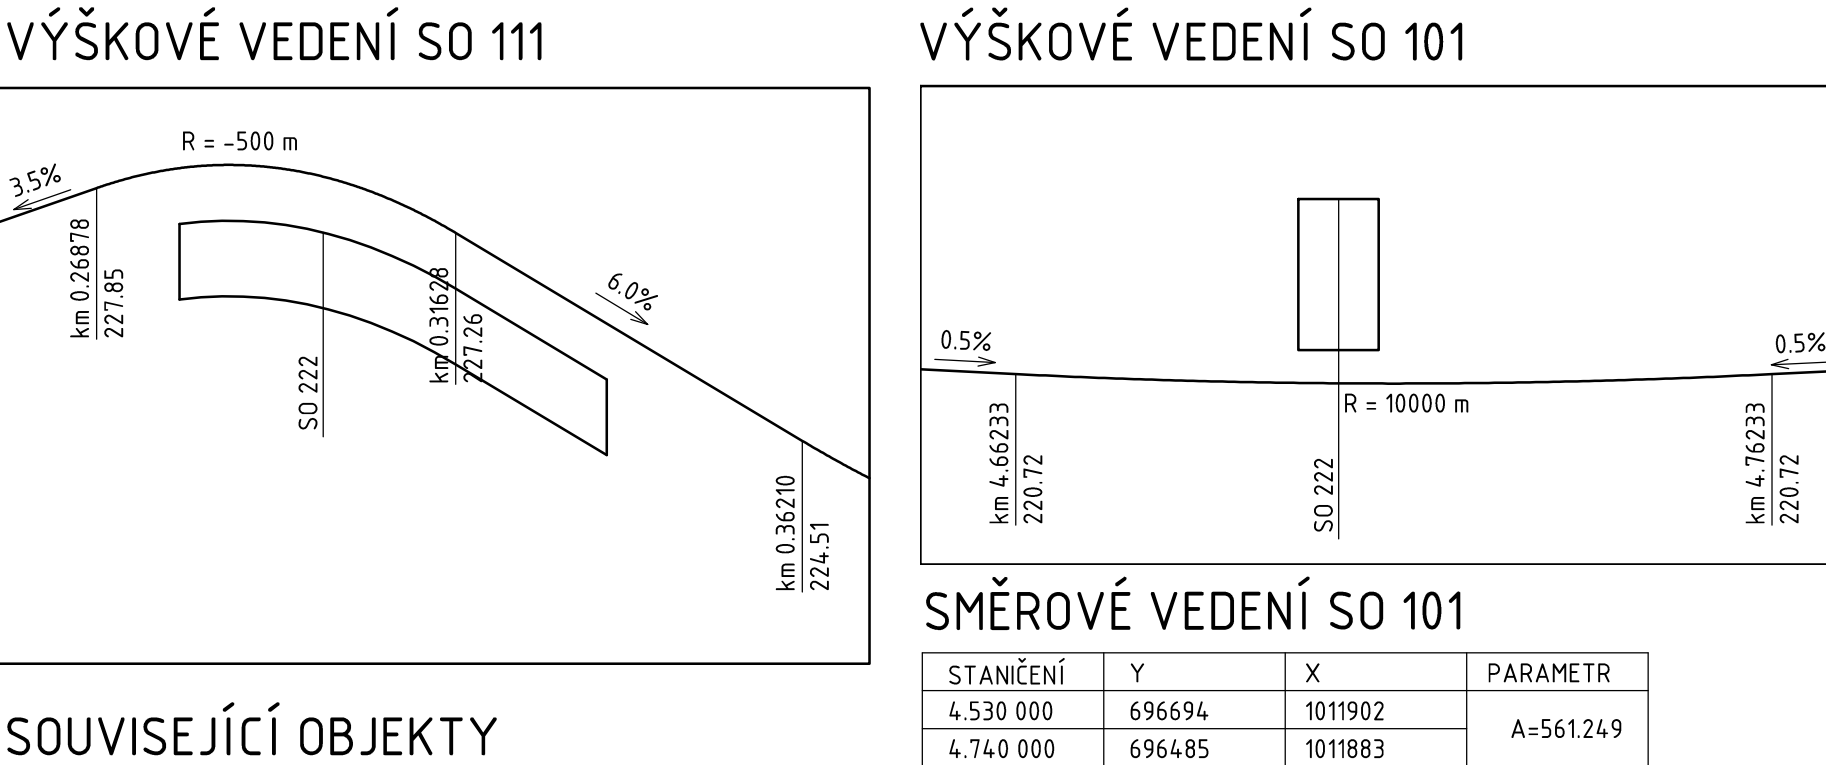
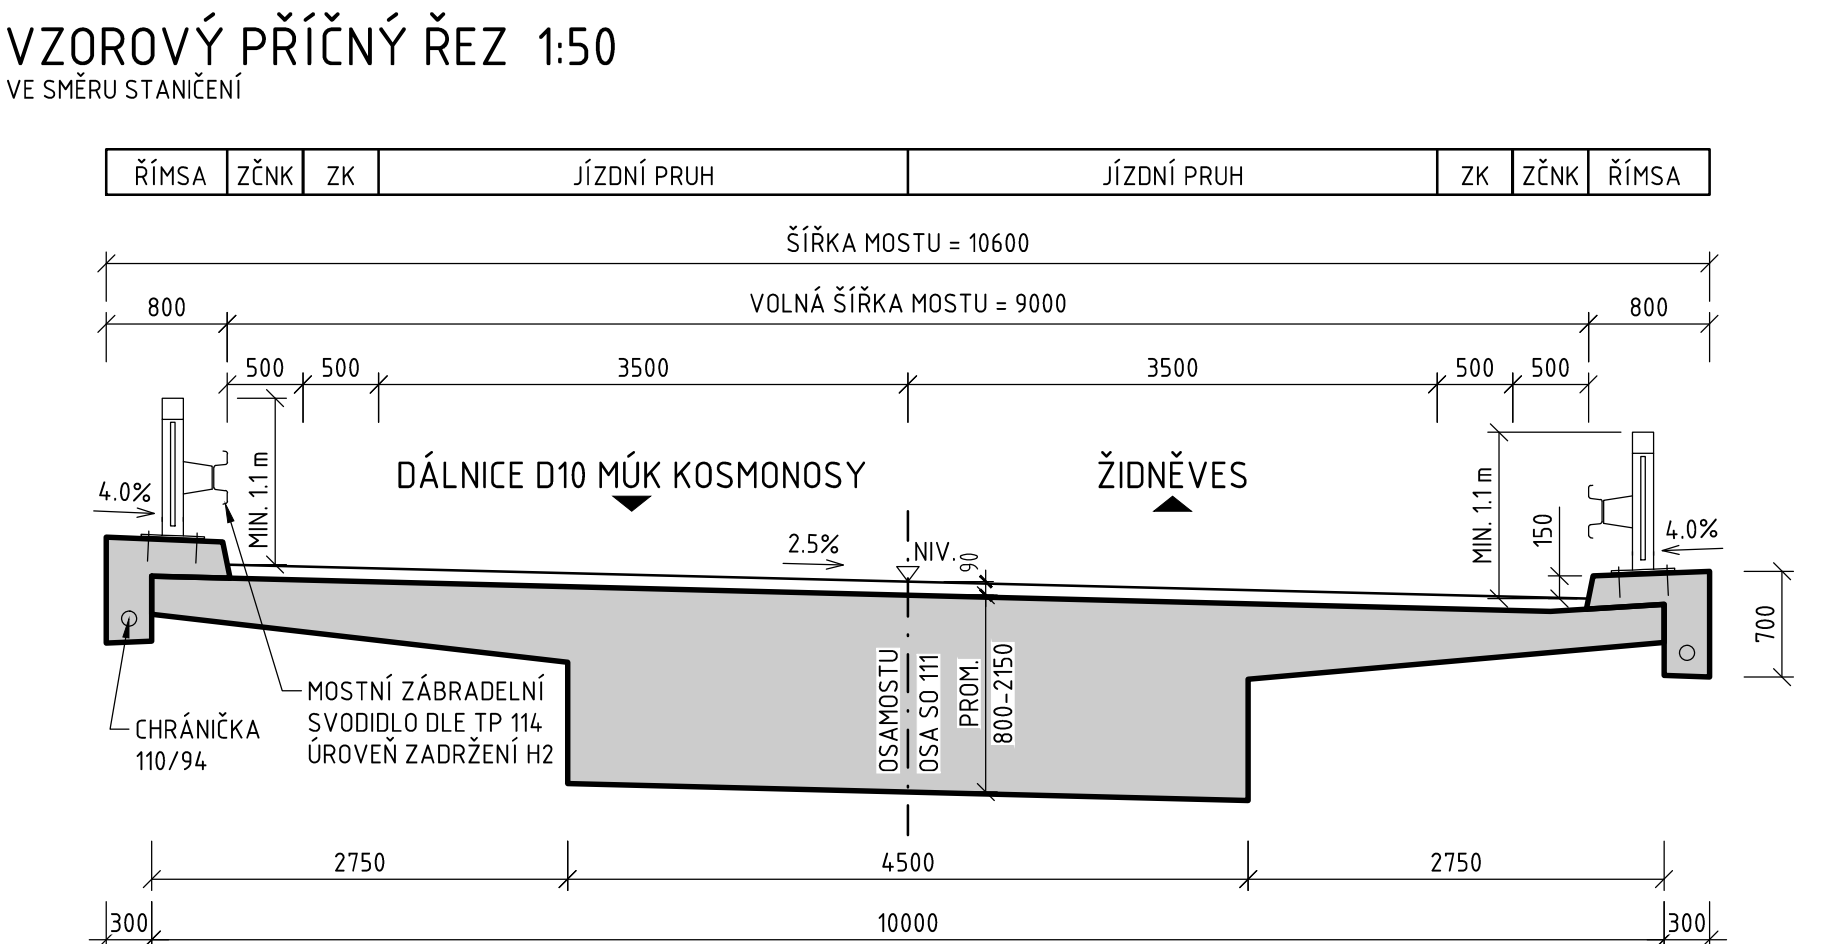
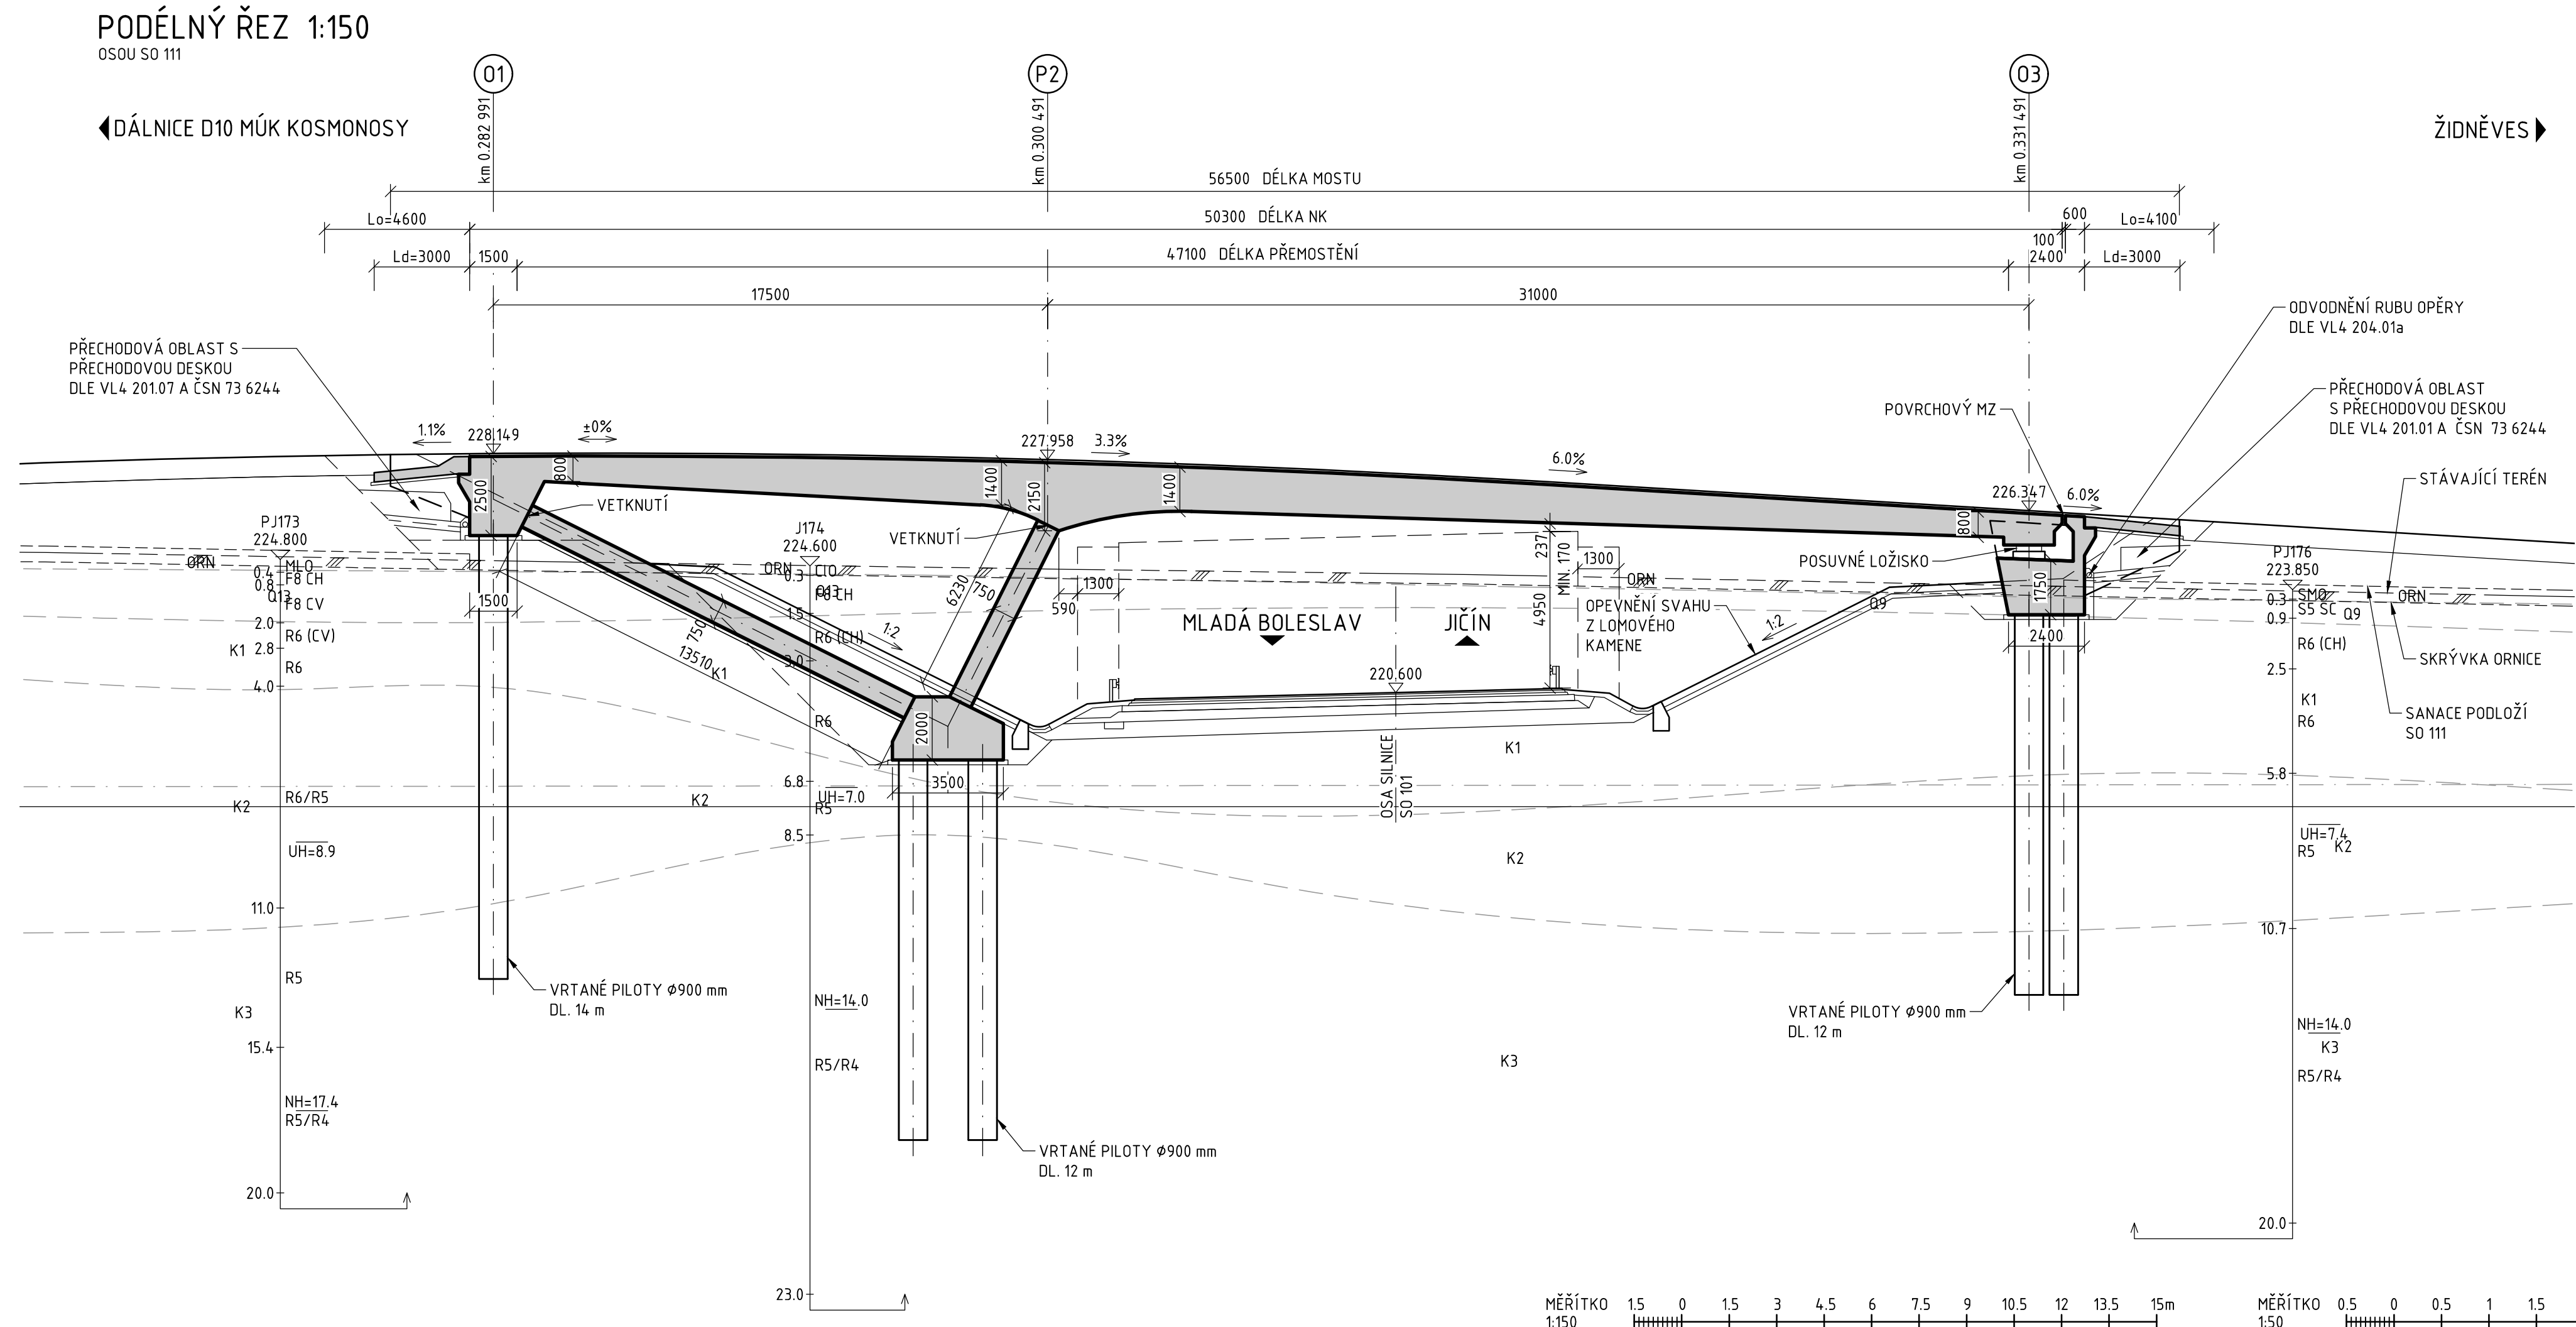
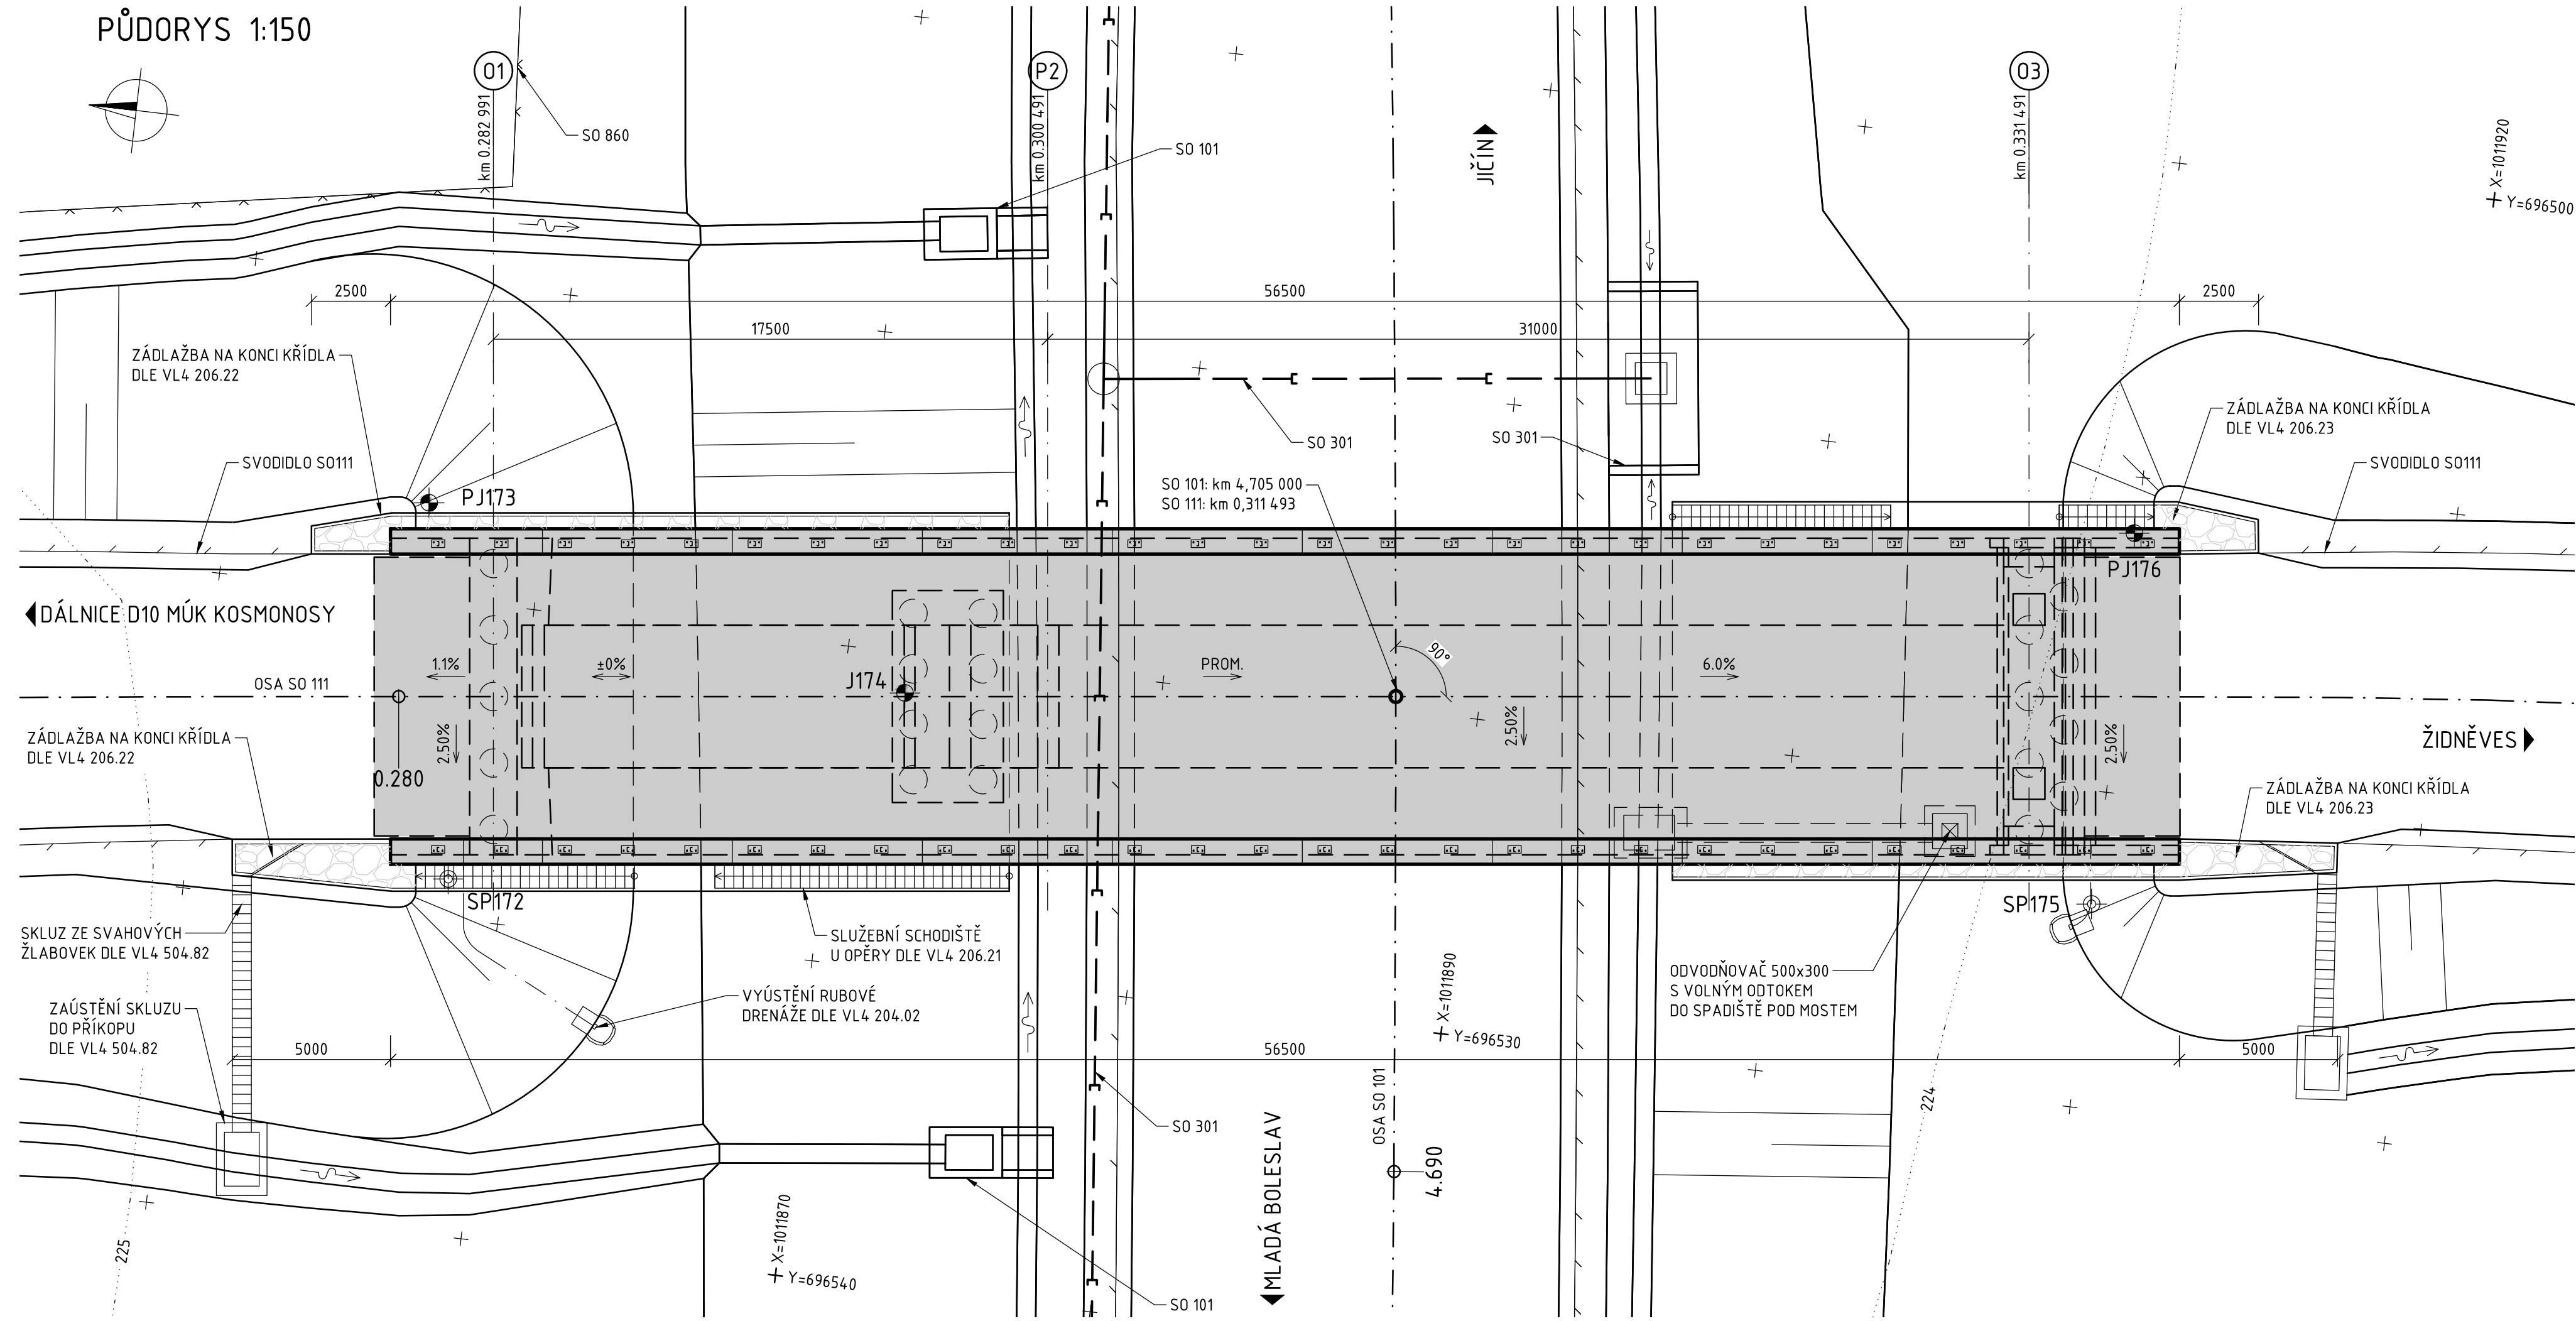


POZNÁMKY:

- NEDÍLNOU SOUČÁSTÍ VÝKRESU JSOU TECHNICKÉ SPECIFIKACE A POZNÁMKY UVEDENÉ NA VÝKRESU TECHNICKÝCH SPECIFIKACÍ A POZNÁMEK

Souřadnicový systém: S-JTSK
Výškový systém: Bpv

SO 222 NADJEZD NA MŮK ŽIDNĚVES V KM 4,705

Objednatel: Ředitelství silnic a dálnic

Ředitelství silnic a dálnic s. p.
Čerčanská 2023/12, Krč, 140 00 Praha 4

Valbek, spol. s r.o.
Vaňurova 505/17
460 07 Liberec 3

Vypracoval: ING. O. ŠABATA
Zodp. projektant: ING. O. ŠABATA
Tech. kontrola: ING. I. BELDA
Akce: I/16 MLADÁ BOLESLAV - MARTINOVICE

Zak. číslo: 21-L113-001
Datum: 02/2025
Stupeň: PDPS
Počet formátů: 8x A4
Měřítko: NA VÝKRESE
C. přílohy: Paré

Zhotovitel: Valbek, spol. s r.o.
Vaňurova 505/17
460 07 Liberec 3

Příloha: PŮDORYS, PODÉLNÝ ŘEZ, VZOROVÝ PŘÍČNÝ ŘEZ

102