




PŮDORYS 1:100

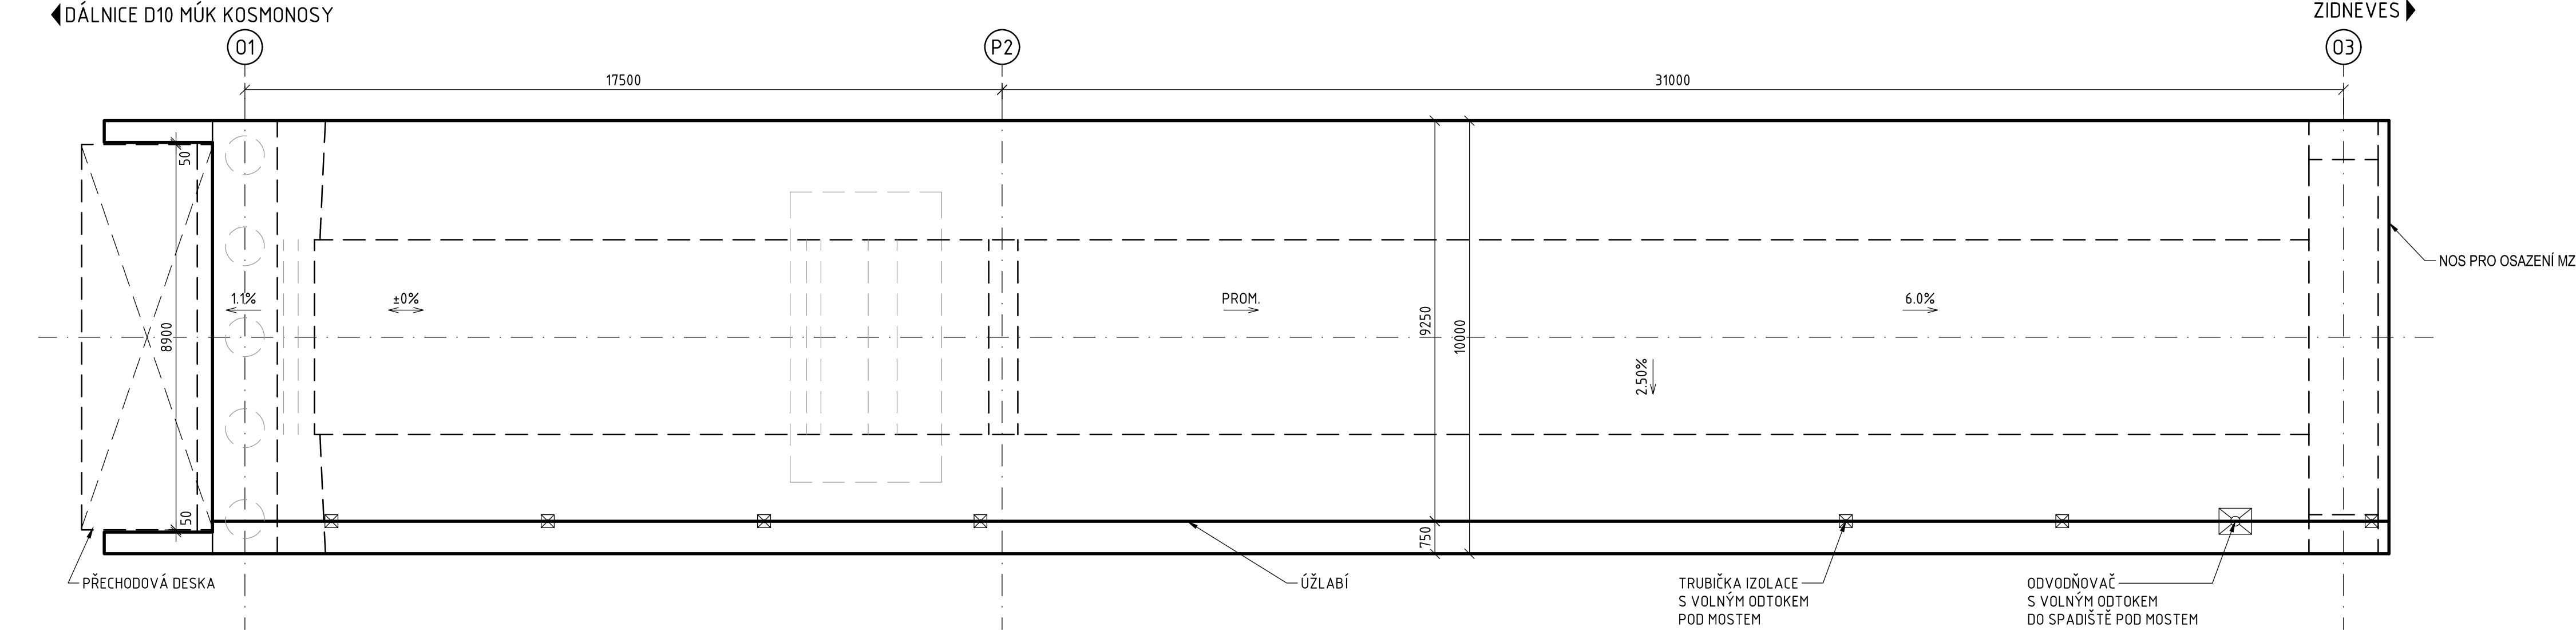


PODÉLNÝ ŘEZ 1:100

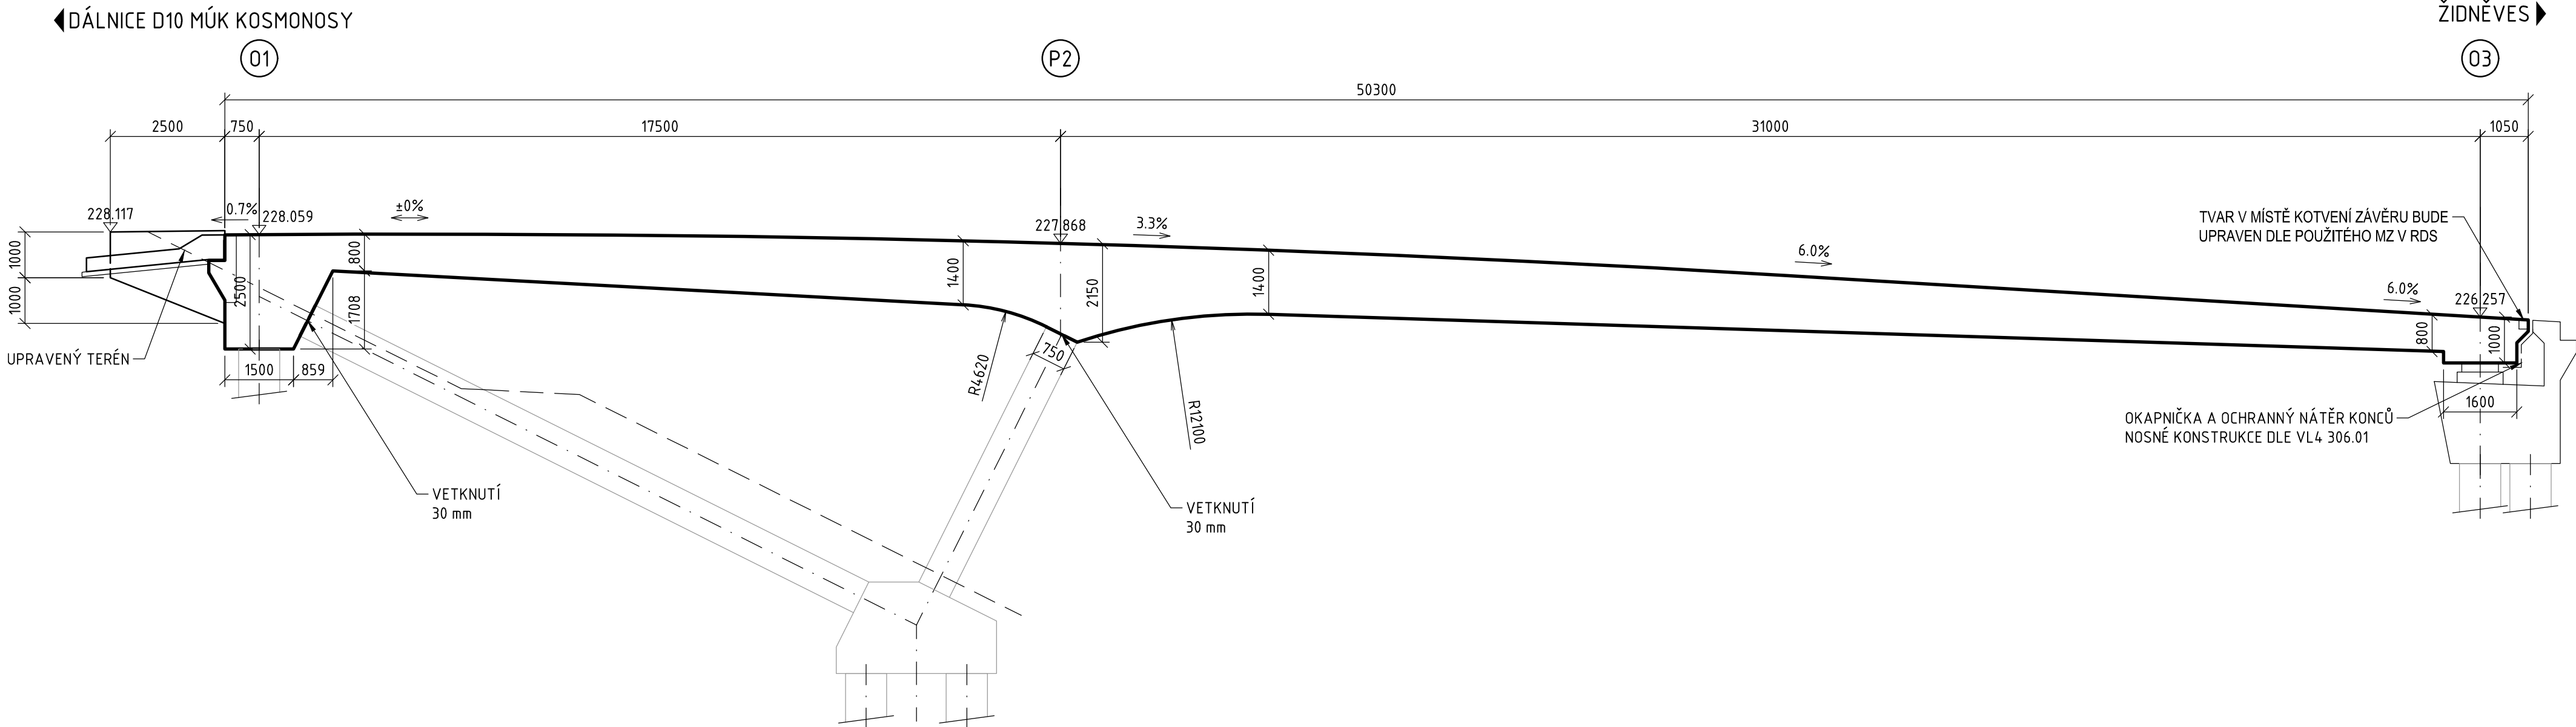


TVAR PŘÍČNÍKU V MÍSTĚ 01 1:50

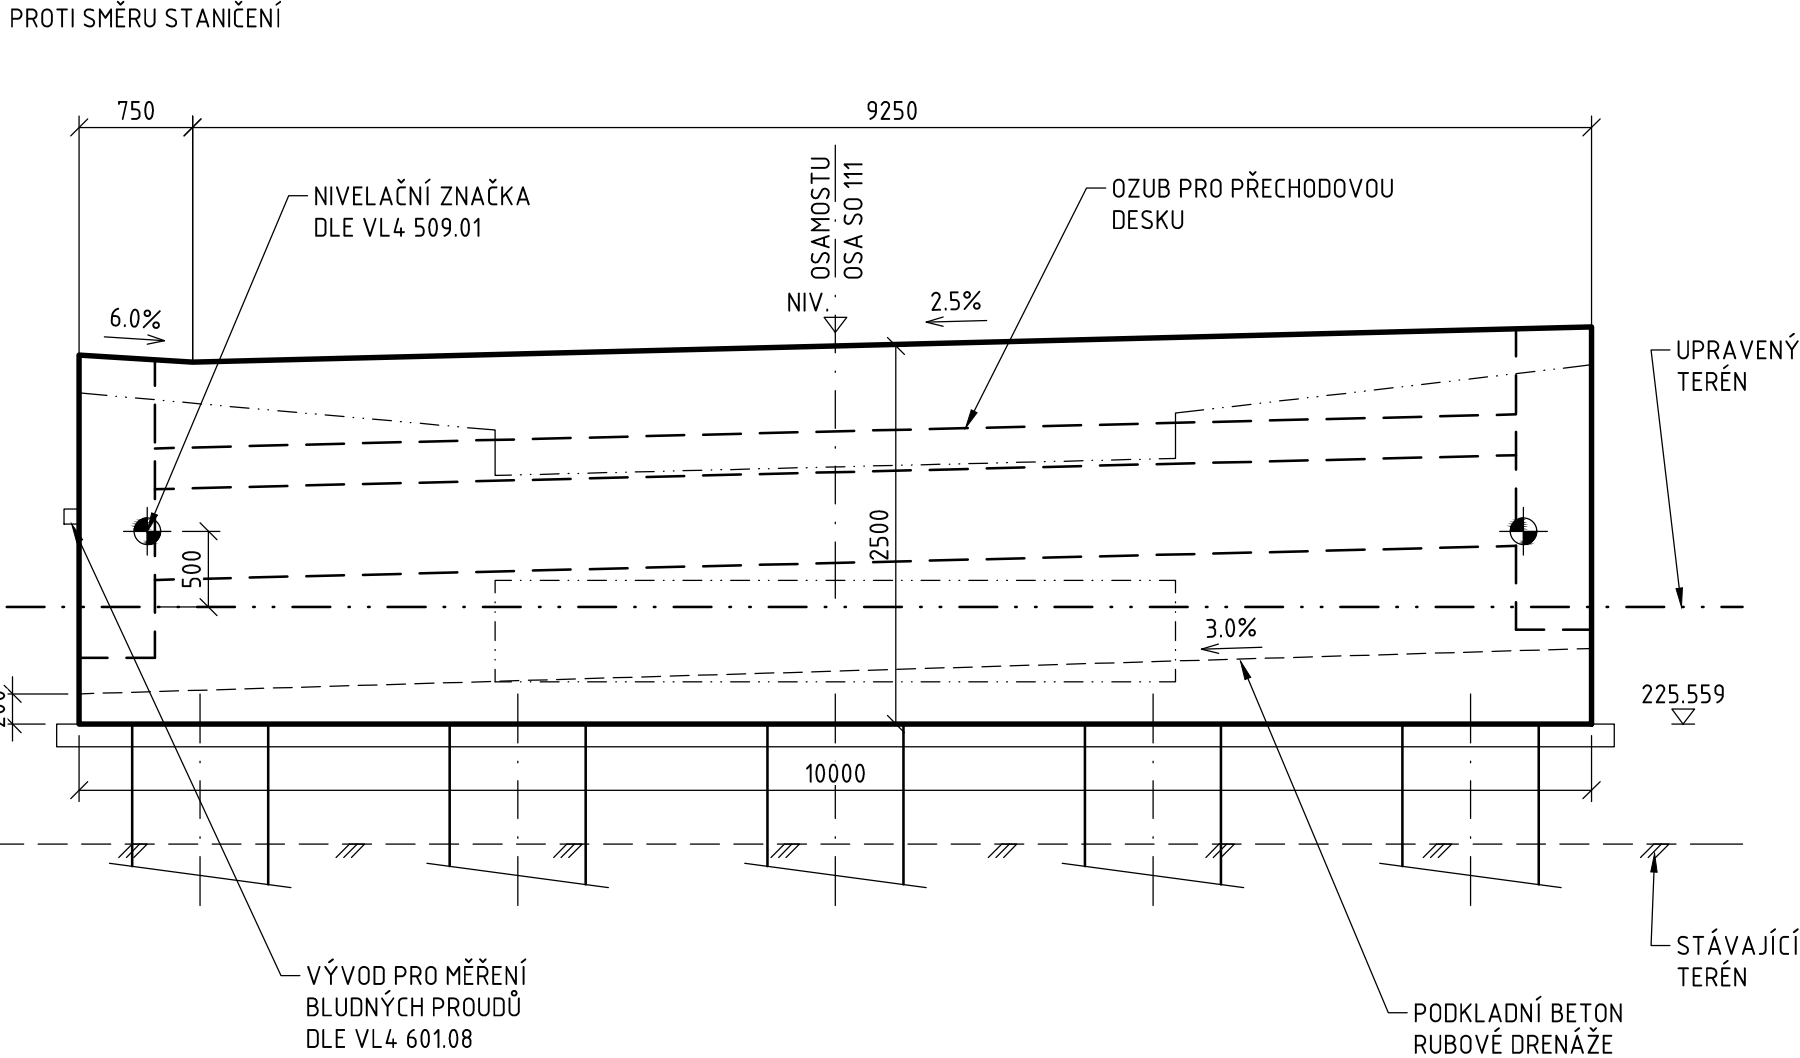


PŘÍČNÝ ŘEZ 1:50

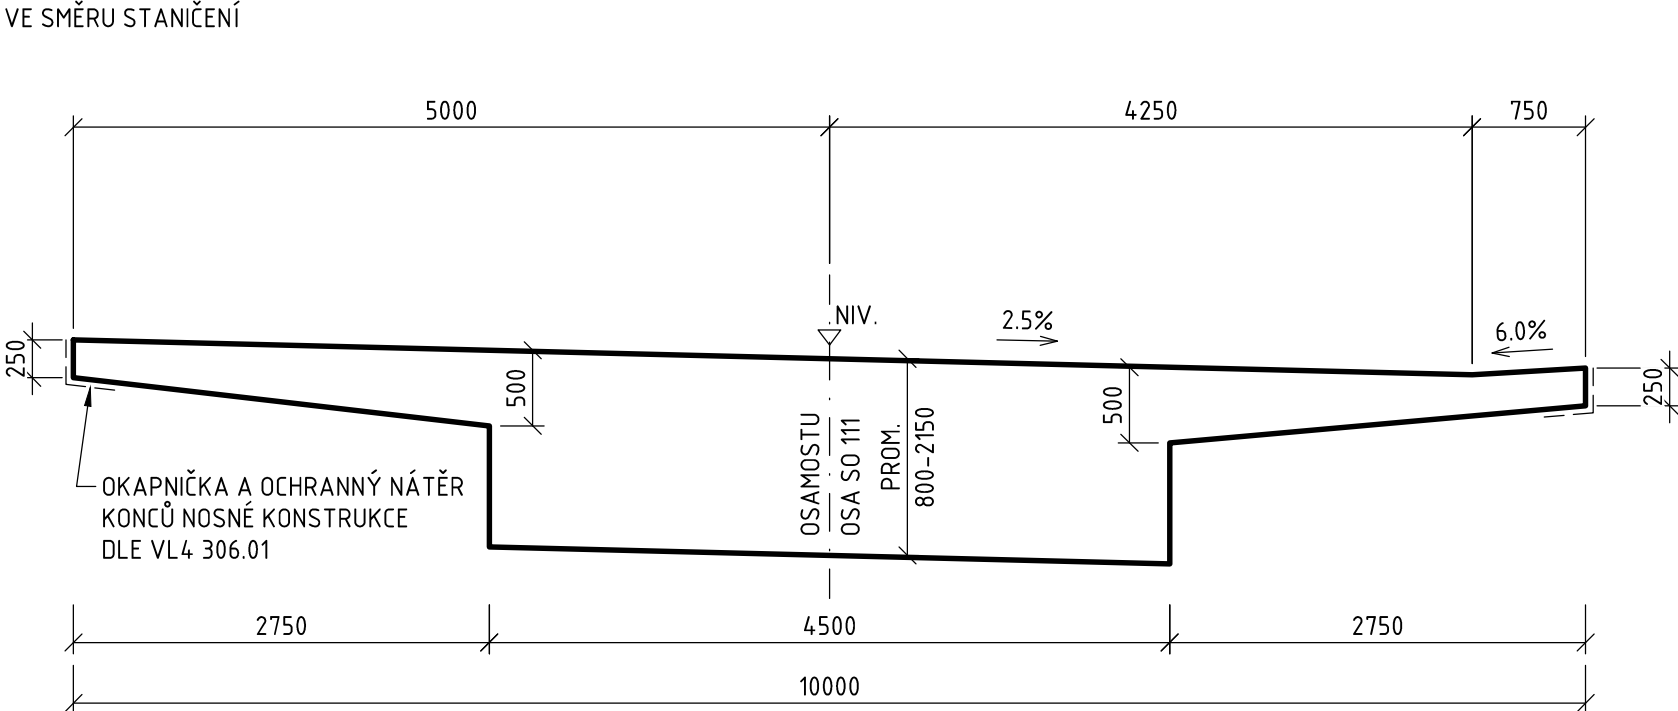

TVAR PŘÍČNÍKU V MÍSTĚ 03 1:50

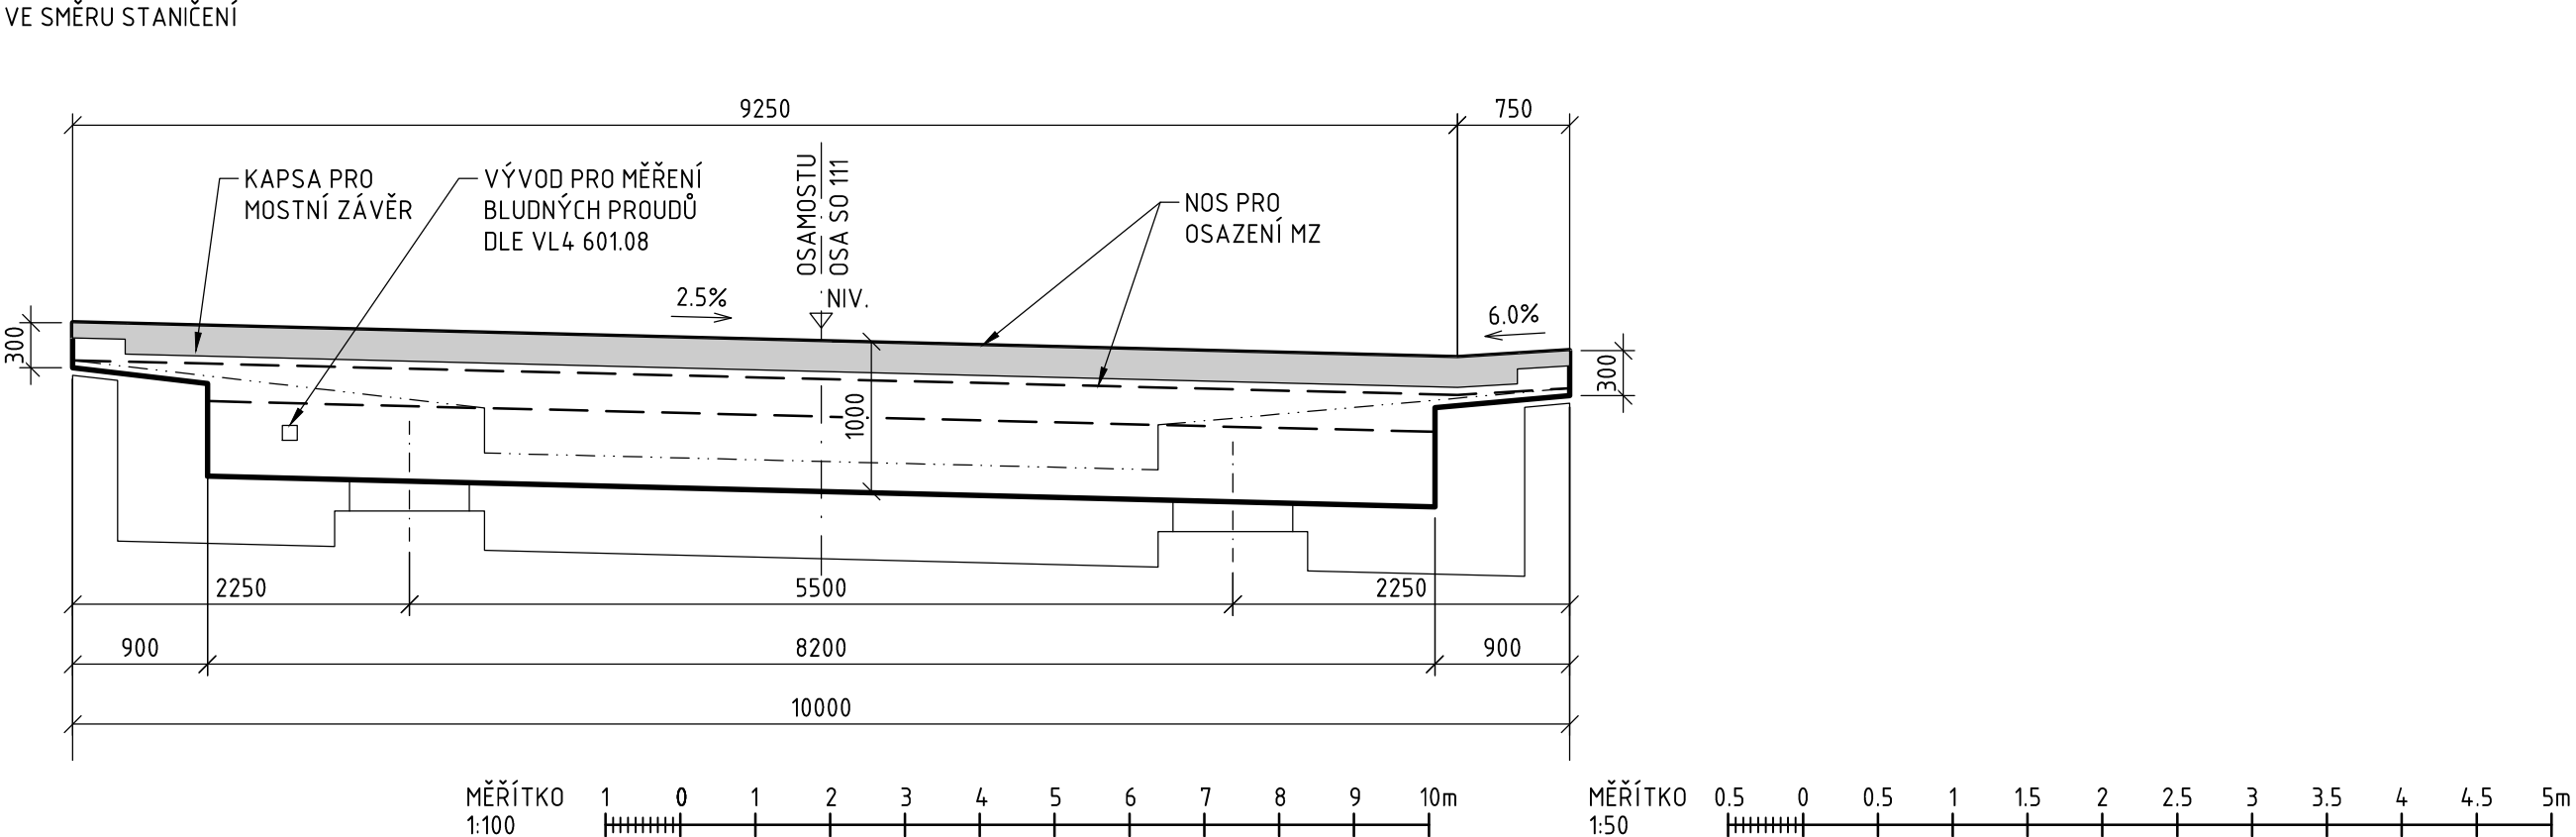

PODÉLNÝ ŘEZ PŘECHODOVOU DESKOU 1:50

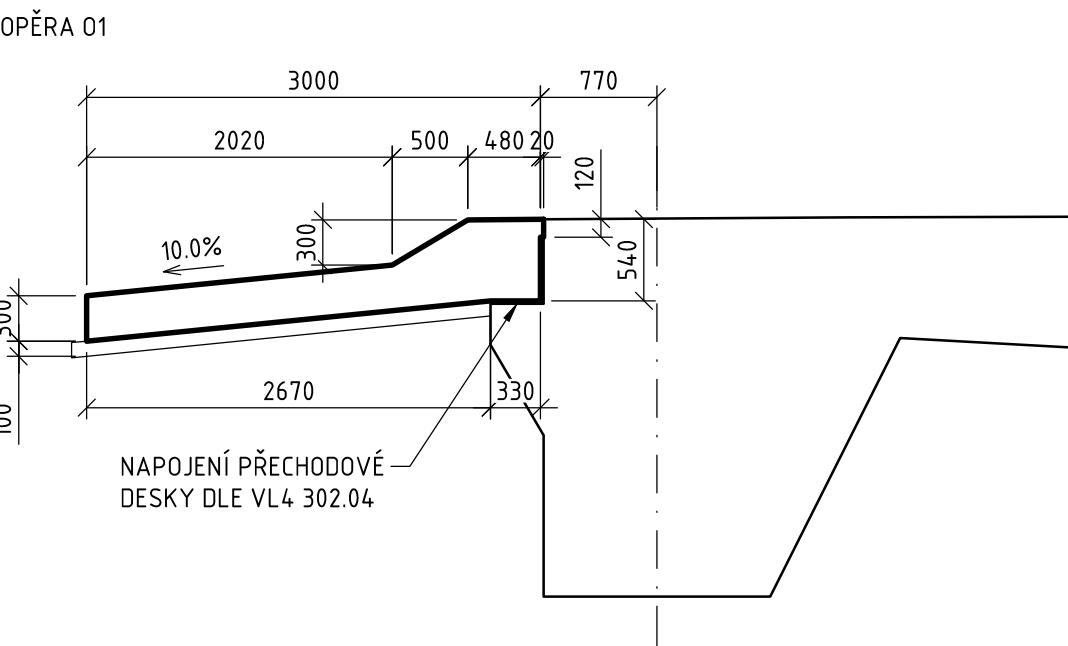

POZNÁMKY:

- NEDÍLNOU SOUČÁSTÍ VÝKRESU JSOU TECHNICKÉ SPECIFIKACE A POZNÁMKY UVEDENÉ NA VÝKRESE TECHNICKÝCH SPECIFIKACÍ A POZNÁMEK

Souřadnicový systém: S-JTSK
Výškový systém: Bpv

SO 222 NADJEZD NA MŮK ŽIDNĚVES V KM 4,705

Objednatel:



Ředitelství silnic a dálnic s. p.
Čerčanská 2023/12, Krč, 140 00 Praha 4



Valbek, spol. s r.o.
Vaňurova 505/17
460 07 Liberec 3



Vypracoval	ING. O. ŠABATA	<i>O. Šabata</i>	Zak. číslo	21-L113-001
Zodp. projektant	ING. O. ŠABATA	<i>O. Šabata</i>	Datum	02/2025
Tech. kontrola	ING. I. BELDA	<i>I. Belda</i>	Stupeň	PDPS
Akce	I/16 MLADÁ BOLESLAV - MARTINOVICE		Počet formátů	8x A4
			Měřítko	NA VÝKRESE
			C. přílohy	Paré
Zhotovitel:	Příloha		202	
Valbek, spol. s r.o. Vaňurova 505/17 460 07 Liberec 3	TVAR NOSNÉ KONSTRUKCE			