

PŘECHODOVÉ OBLASTI, PODÉLNÝ ŘEZ 1:75

PŘECHODOVÉ OBLASTI S PŘECHODOVOU DESKOU DLE VL4 201.01, 201.07 A ČSN 73 6244




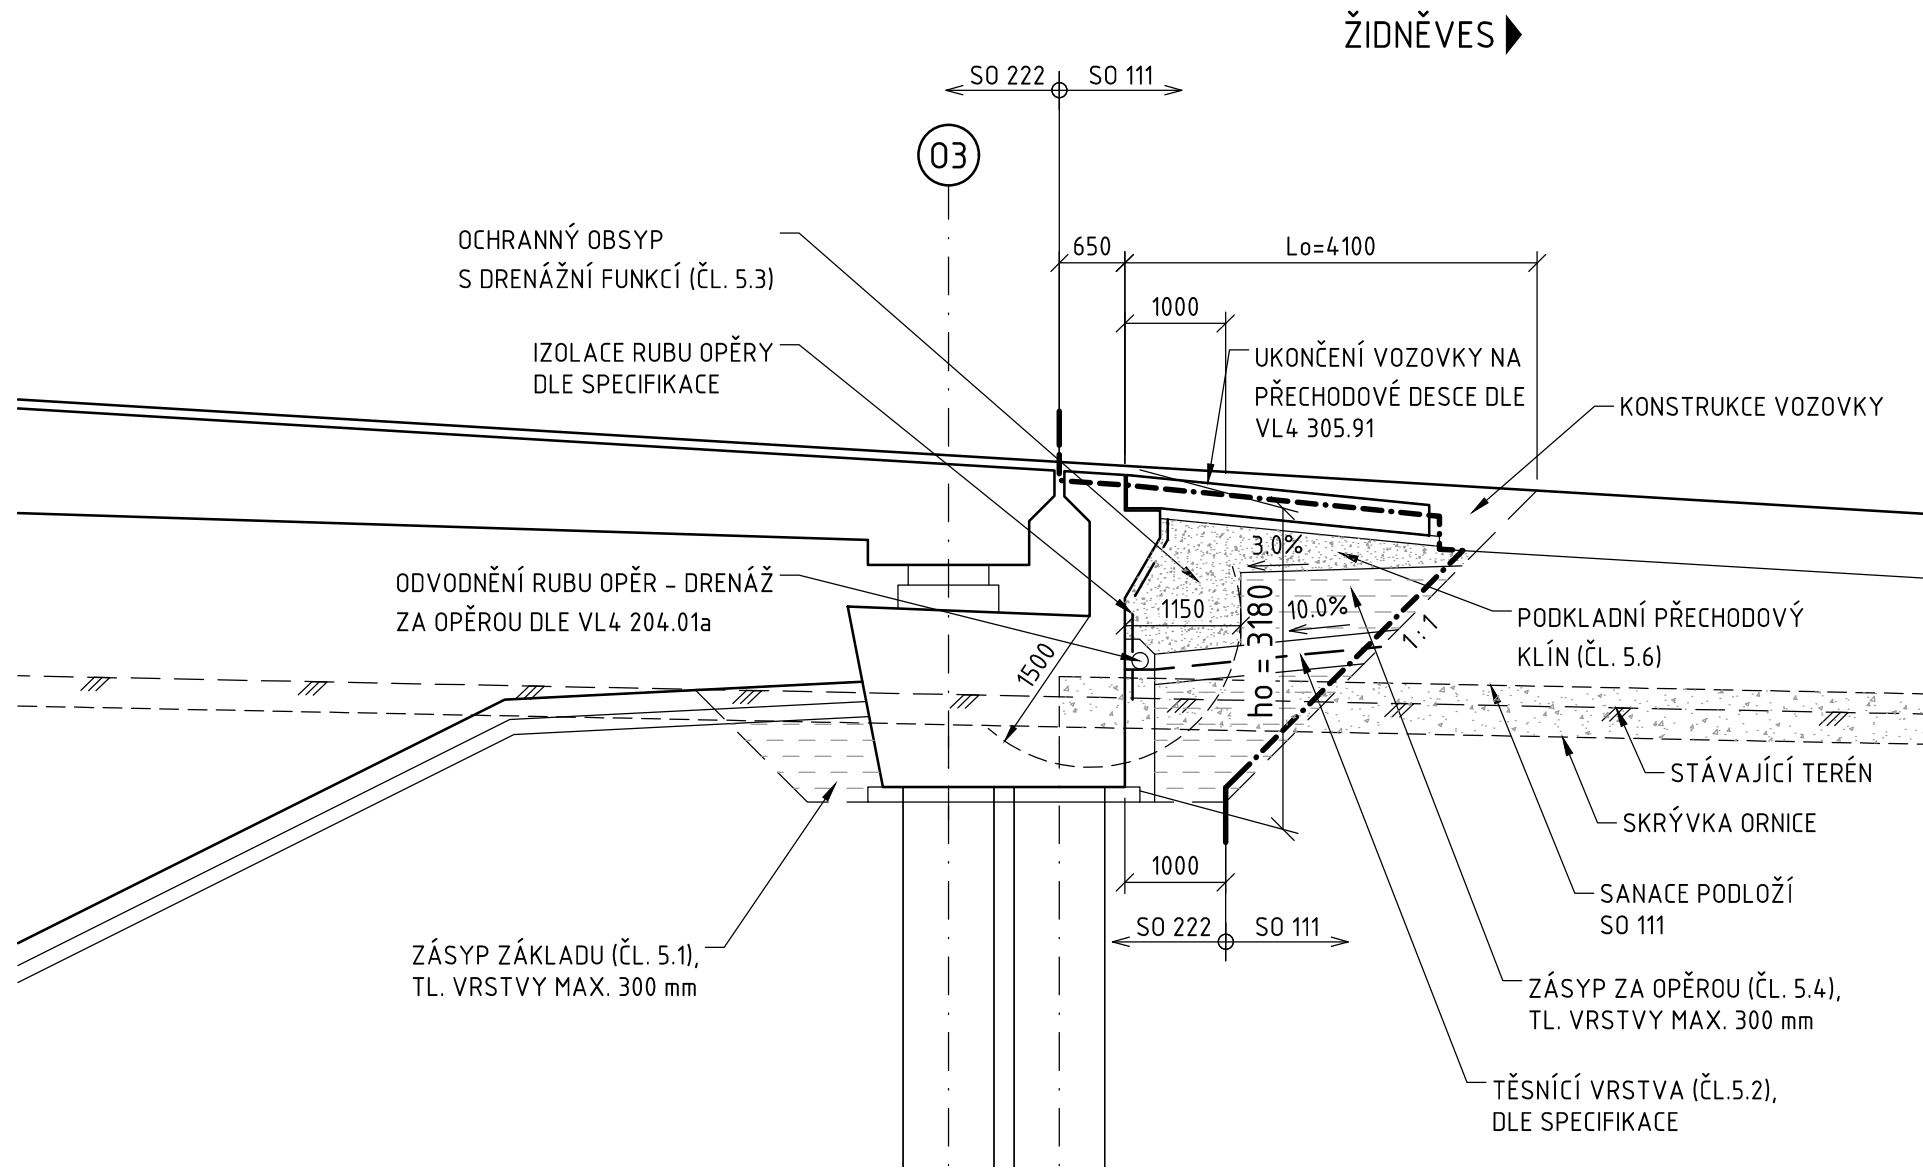



SCHÉMA PŘEDPÍNAČÍ VÝZTUŽE, PODÉLNÝ ŘEZ 1:100

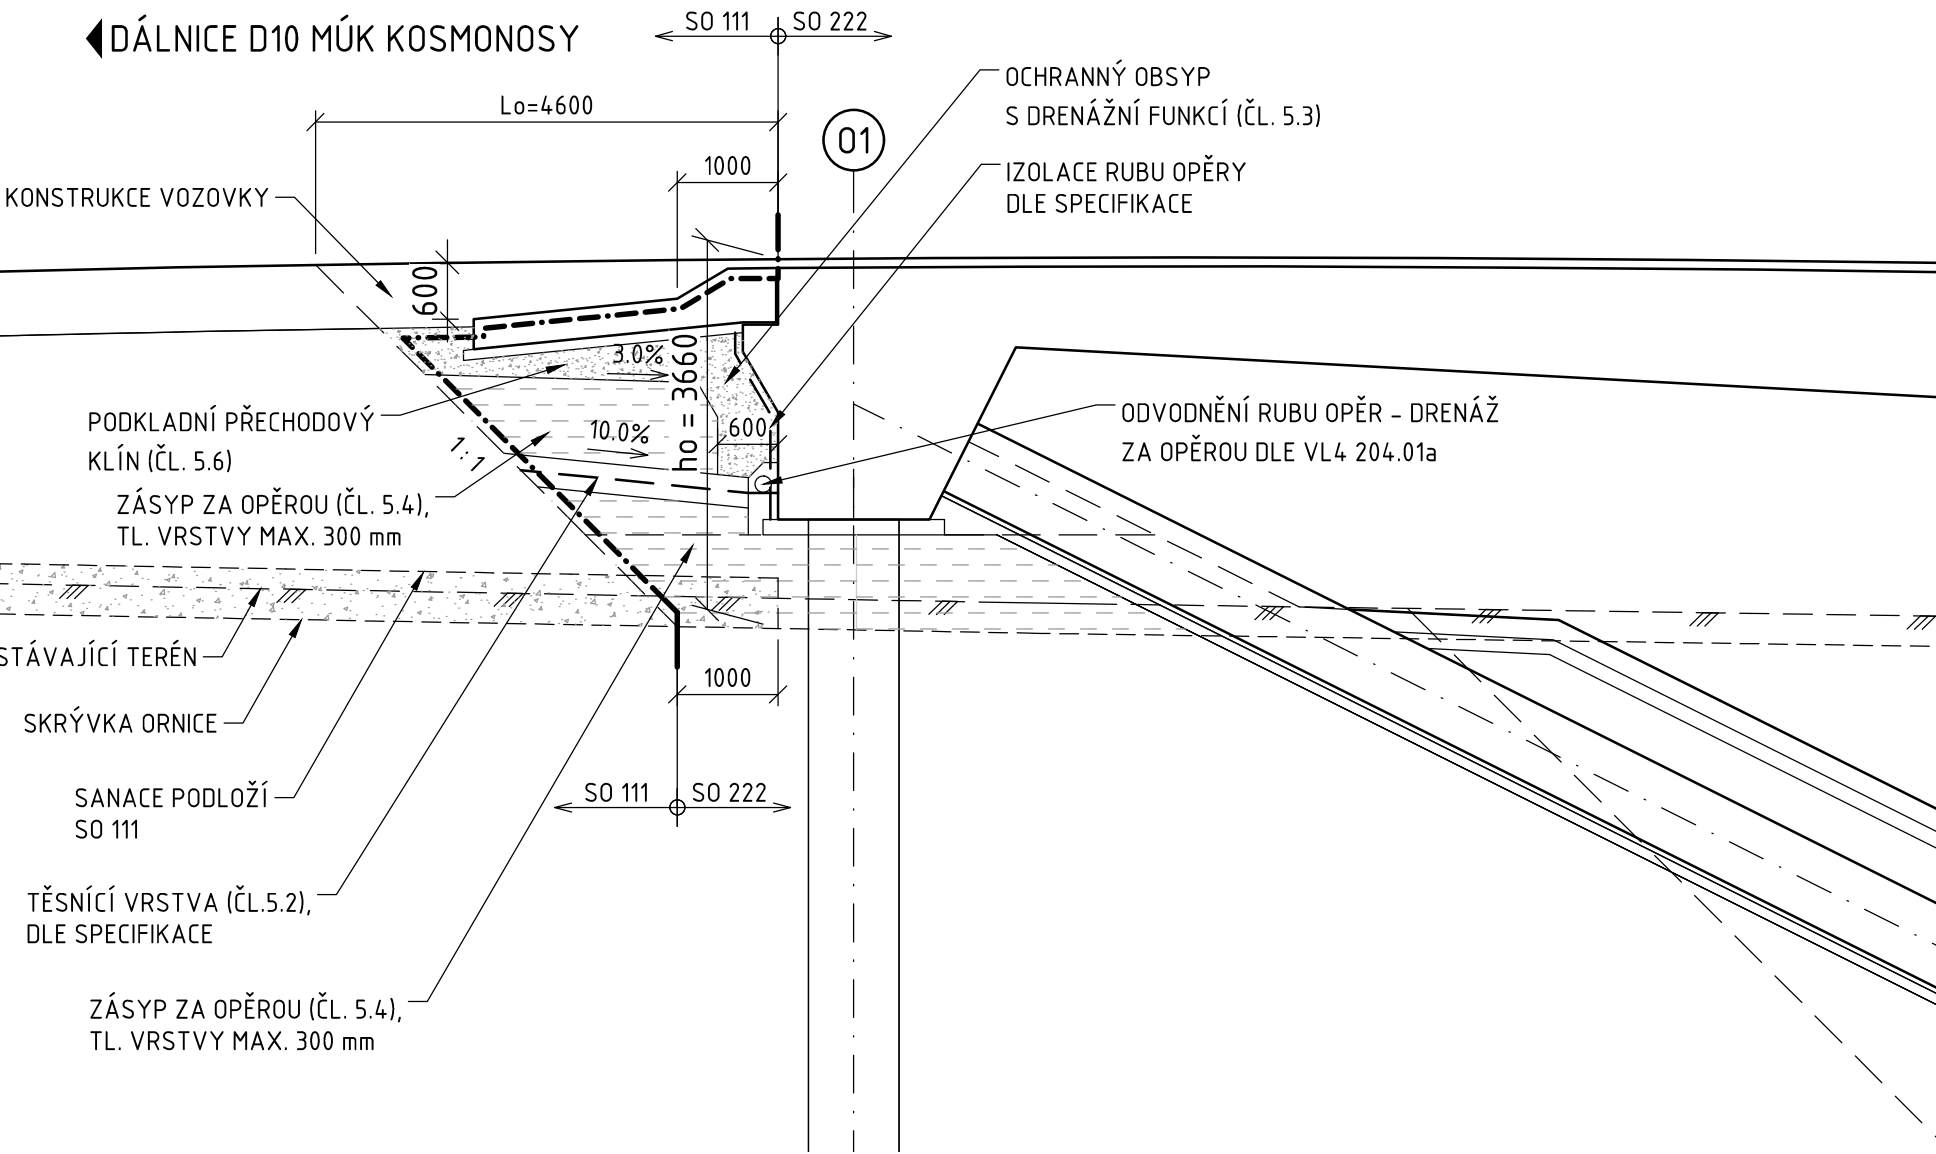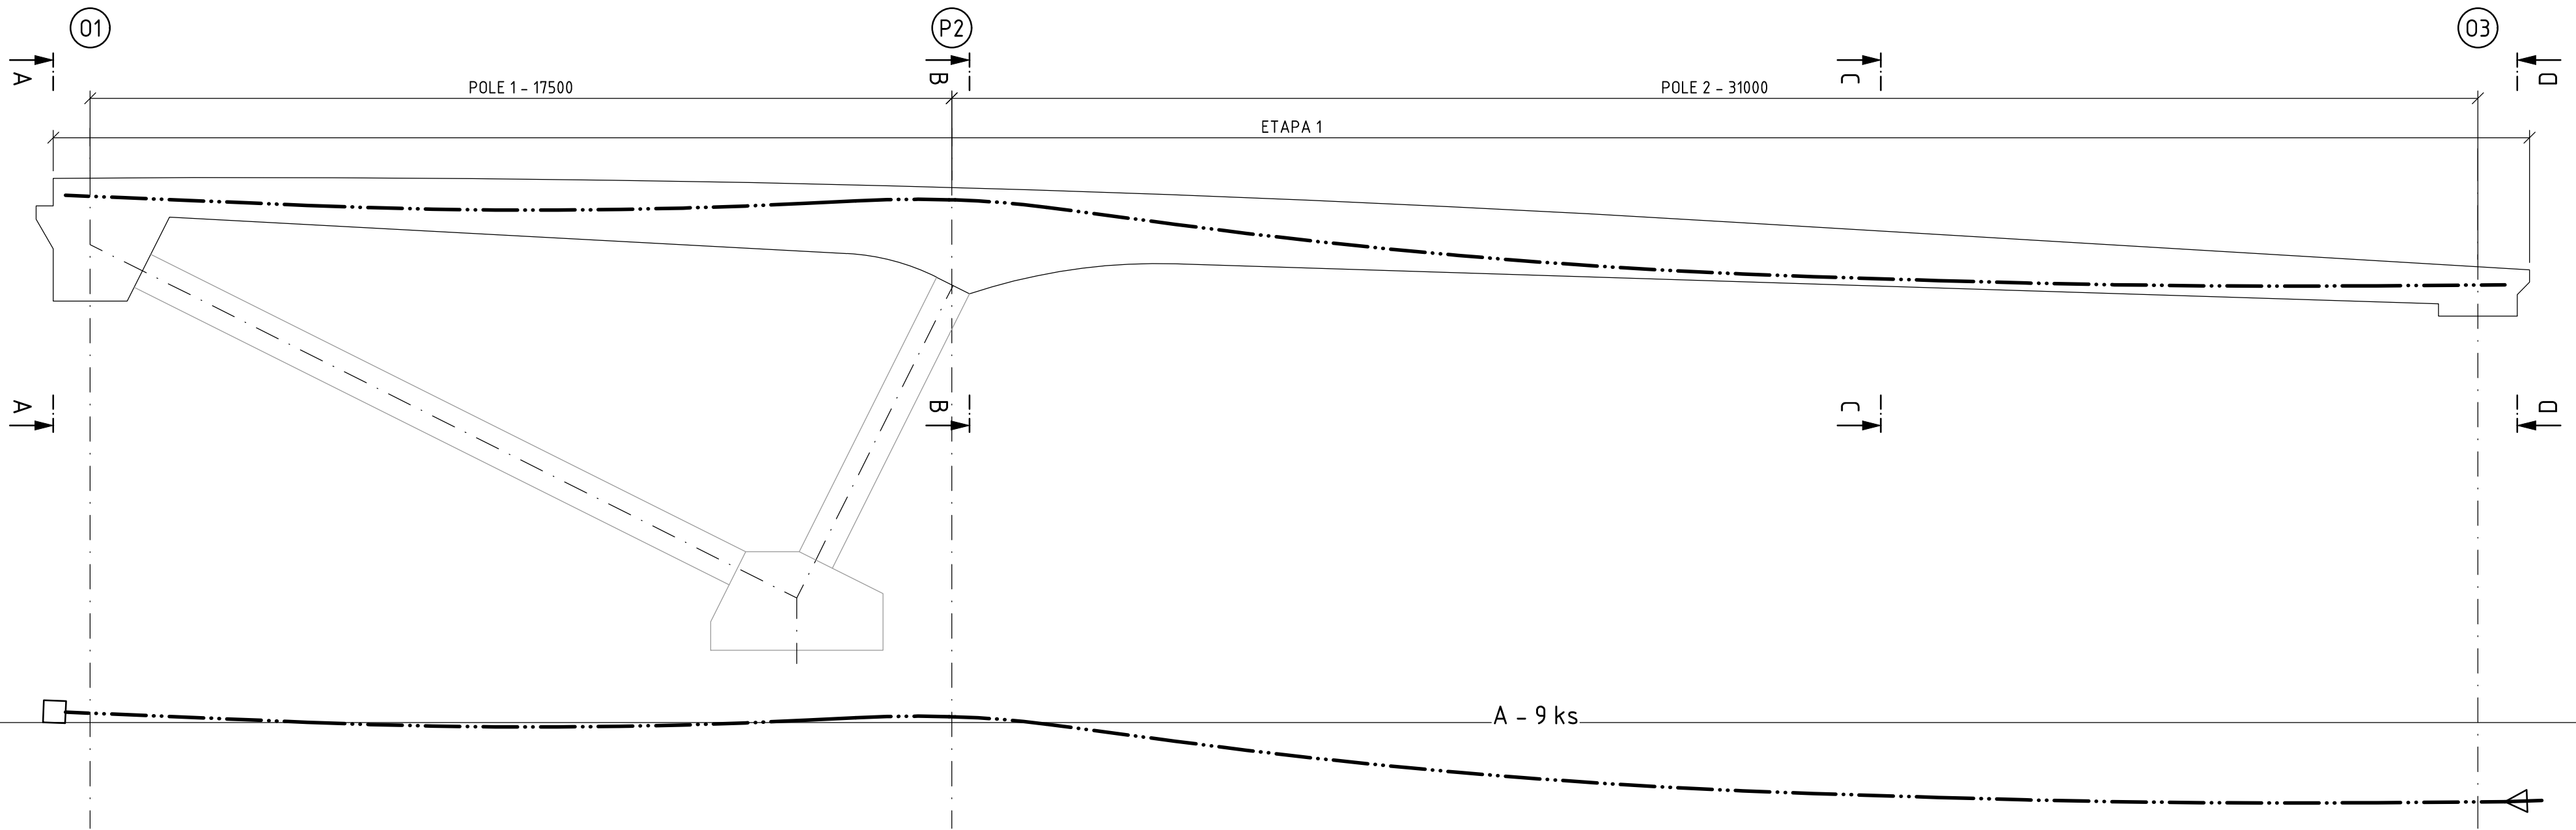

POHLED NA ČELO OPĚRY O1 A-A 1:50

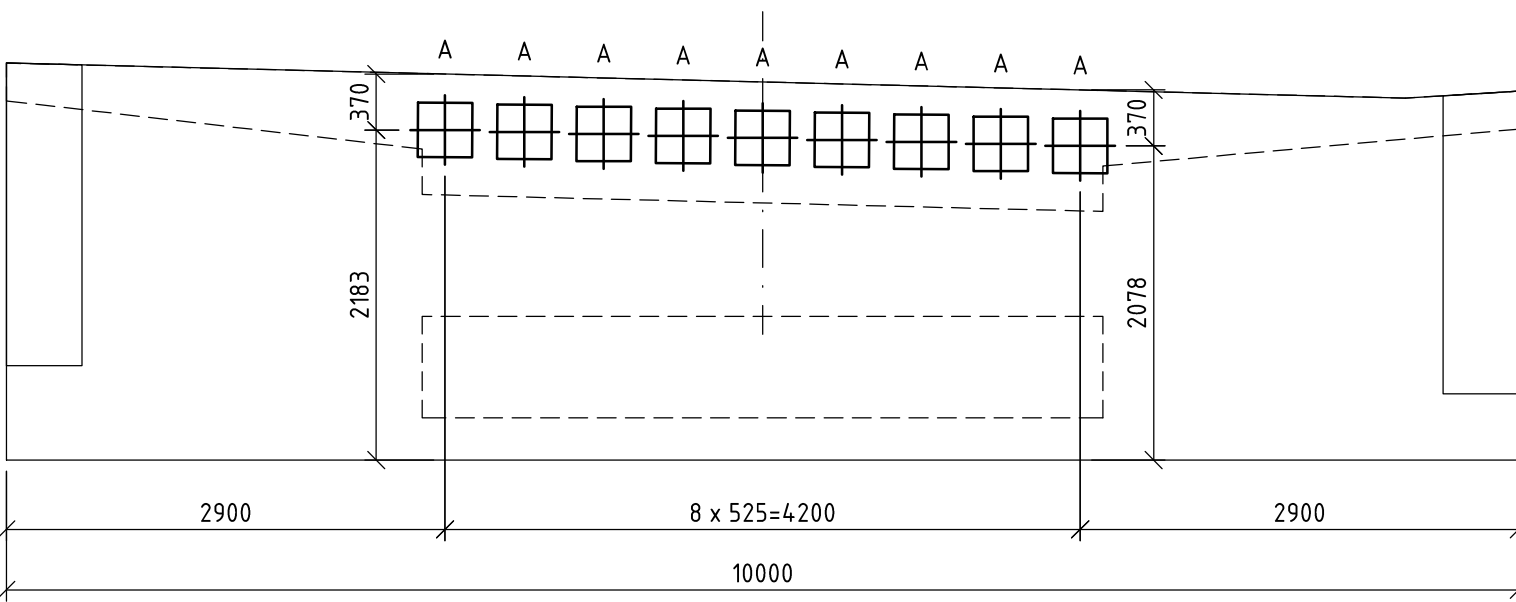

ŘEZ V POLI 2 C-C 1:50

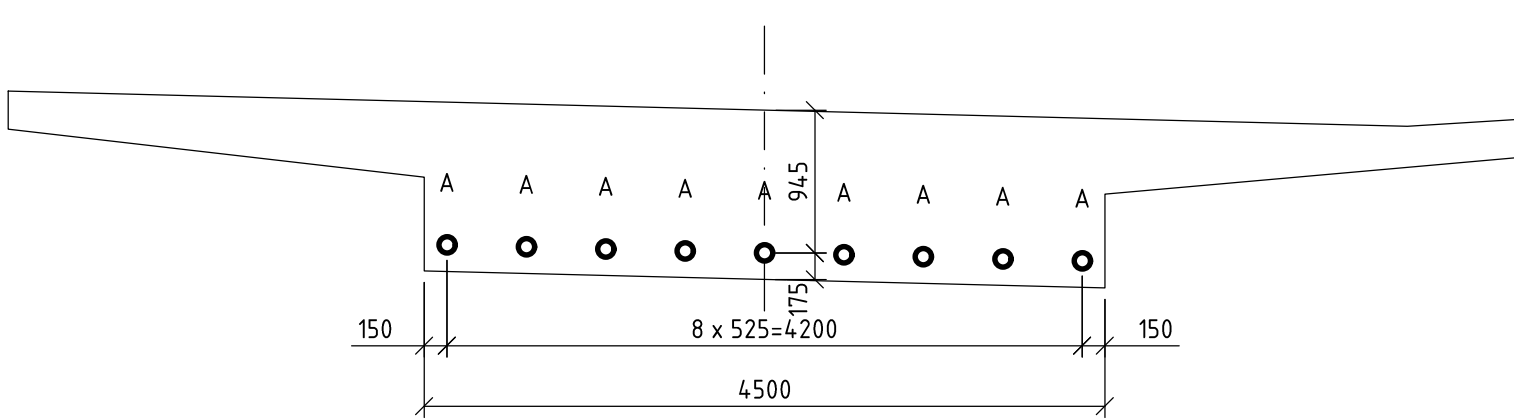


VÝKAZ PŘEDPÍNAČÍCH KABELŮ


KABEL	POČET KABELŮ [ks]	DĚLKA KABELŮ [m]	POČET LAN V 1 KABELU	HMOTNOST [kg]
A	9	49,65	22	11 600,2
CELKOVÁ HMOTNOST [t]				11 600,2

- PŘEDPÍNAČÍ VÝZTUŽ - Y1860S7-15.7-A
DLE prEN 10138-1 a 3 (150 mm²)
- KOTEVNÍ NAPĚTÍ - 14 00 MPa
- PODRŽENÍ NAPĚTÍ - 5 min

ŘEZ NAD PODPĚROU P2 B-B 1:50

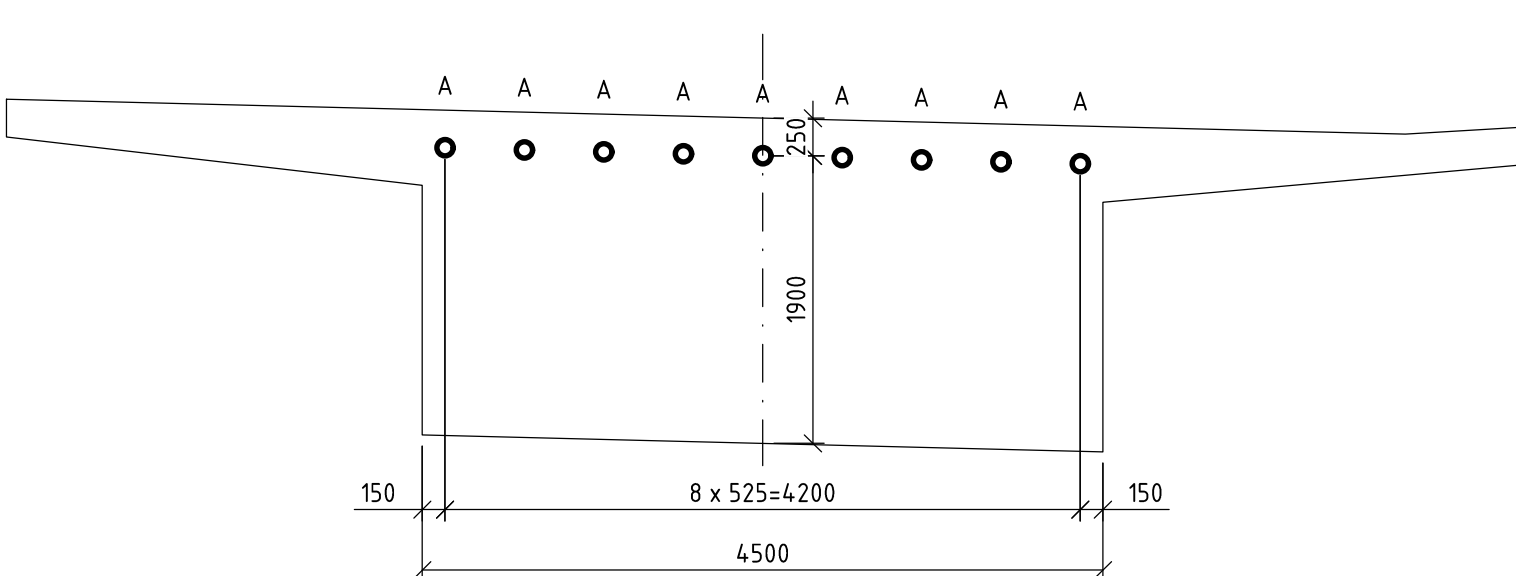

POHLED NA ČELO OPĚRY O3 D-D 1:50

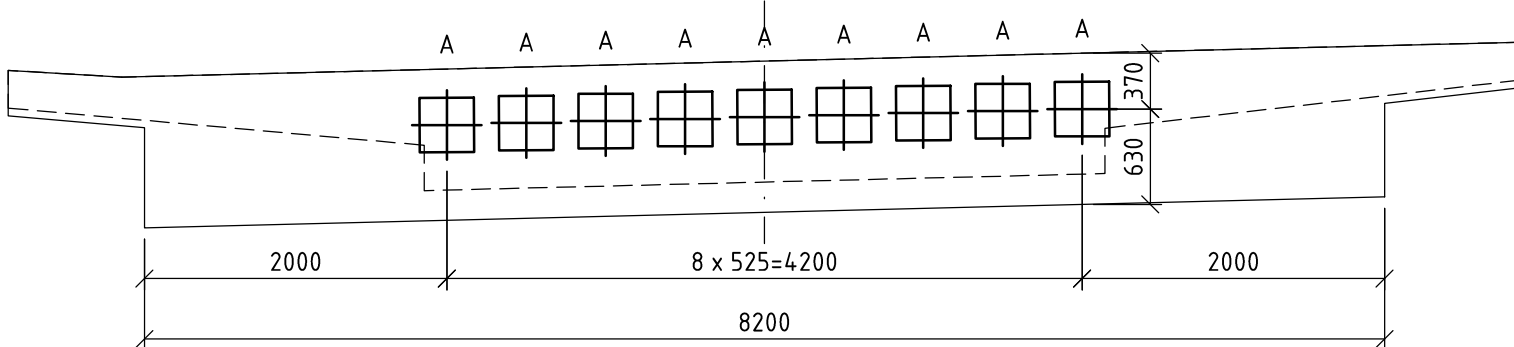

MĚŘÍTKO 1:100

1 0 1 2 3 4 5 6 7 8 9 10m

MĚŘÍTKO 1:50

0.5 0 0.5 1 1.5 2 2.5 3 3.5 4 4.5 5m

POZNÁMKY:

- NEDÍLNOU SOUČÁSTÍ VÝKRESU JSOU TECHNICKÉ SPECIFIKACE A POZNÁMKY UVEDENÉ NA VÝKRESE TECHNICKÝCH SPECIFIKACÍ A POZNÁMEK

Souřadnicový systém: S-JTSK
Výškový systém: Bpv

SO 222 NADJEZD NA MŮK ŽIDNĚVES V KM 4,705

Objednatel:

ŘEDITELSTVÍ SILNIC A DÁLNIC

Ředitelství silnic a dálnic s. p.
Čerčanská 2023/12, Krč, 140 00 Praha 4

Valbek

Valbek, spol. s r.o.
Vaňurova 505/17
460 07 Liberec 3

Valbek	Vypracoval	ING. O. ŠABATA	<i>O. Šabata</i>	Zak. číslo	21-L113-001
	Zodp. projektant	ING. O. ŠABATA	<i>O. Šabata</i>	Datum	02/2025
	Tech. kontrola	ING. I. BELDA	<i>I. Belda</i>	Stupeň	PDPS
	Akce	I/16 MLADÁ BOLESLAV - MARTINOVICE			Počet formátů 8x A4
Zhotovitel:				Měřítko	NA VÝKRESE
Valbek, spol. s r.o. Vaňurova 505/17 460 07 Liberec 3				C. přílohy	Paré
Příloha				203	
PŘECHODOVÉ OBLASTI SCHÉMA PŘEDPÍNAČÍ VÝZTUŽE					