



TVAR ŘÍMS
PŮDORYS 1:100

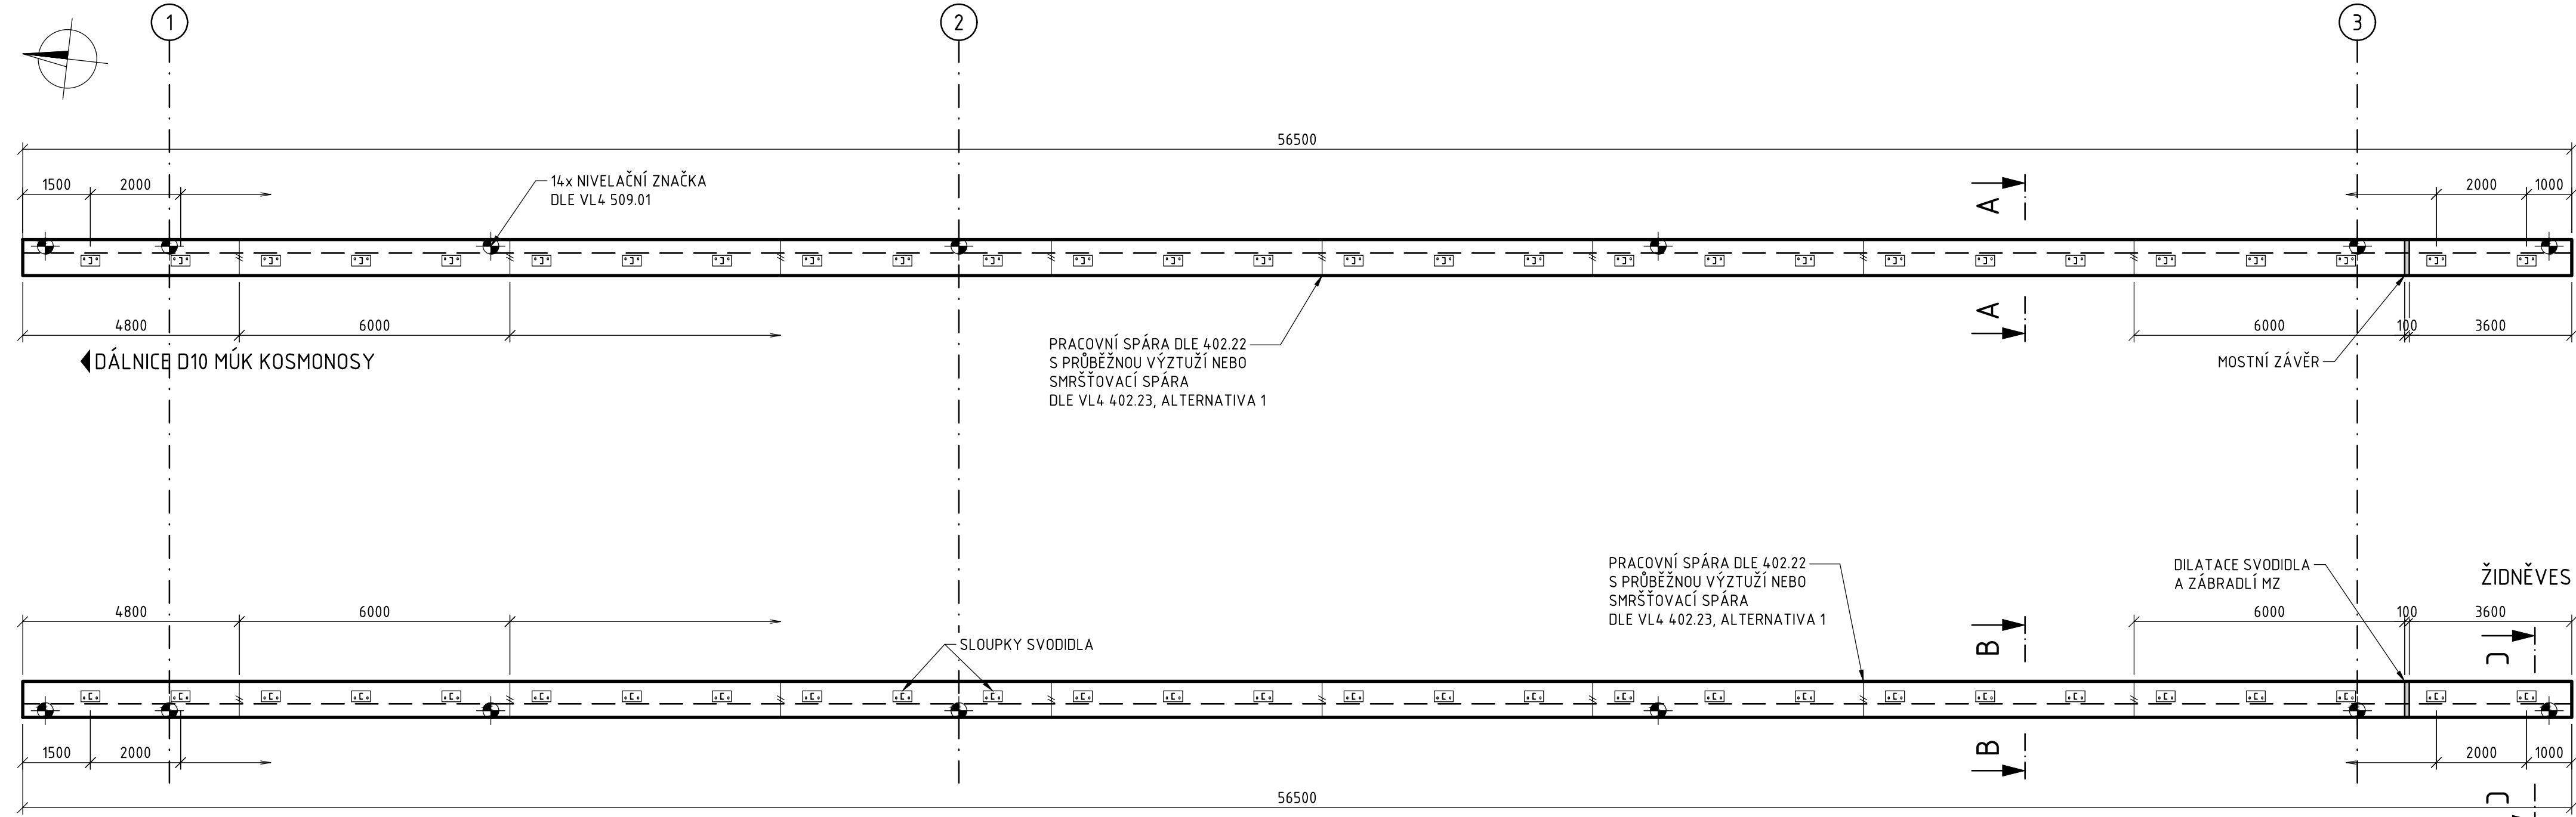


PŘÍČNÝ ŘEZ 1:20
ŘEZ A-A 1:20

KRAJNÍ ŘÍMSA SE ZÁBRADELNÍM SVODIDLEM
DLE VL4 101.05

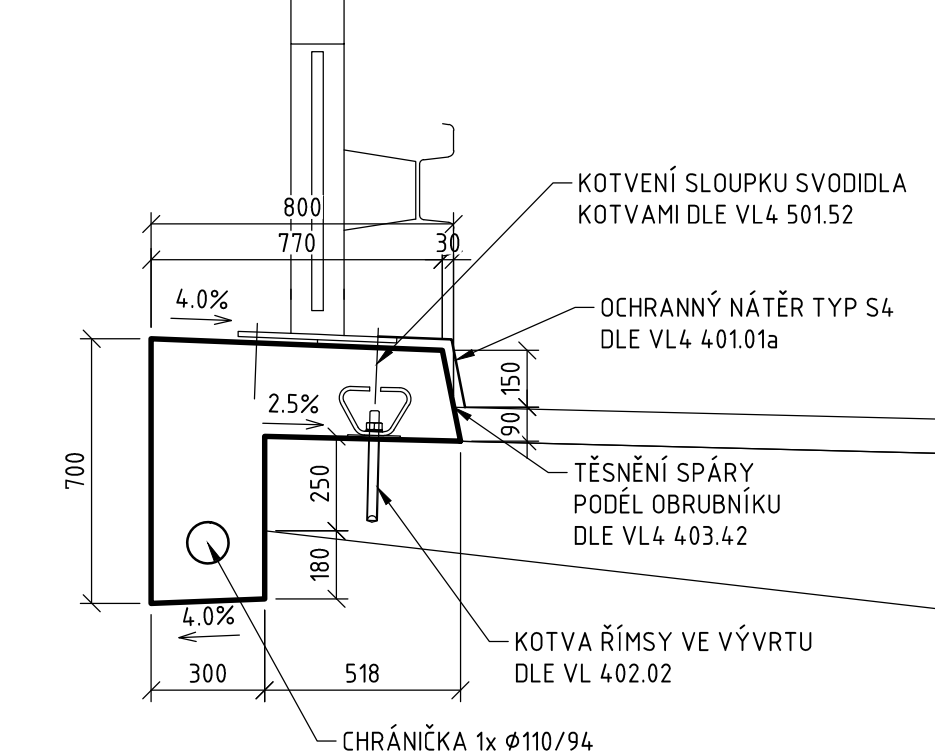


ŘEZ B-B 1:20

KRAJNÍ ŘÍMSA SE ZÁBRADELNÍM SVODIDLEM
DLE VL4 101.07

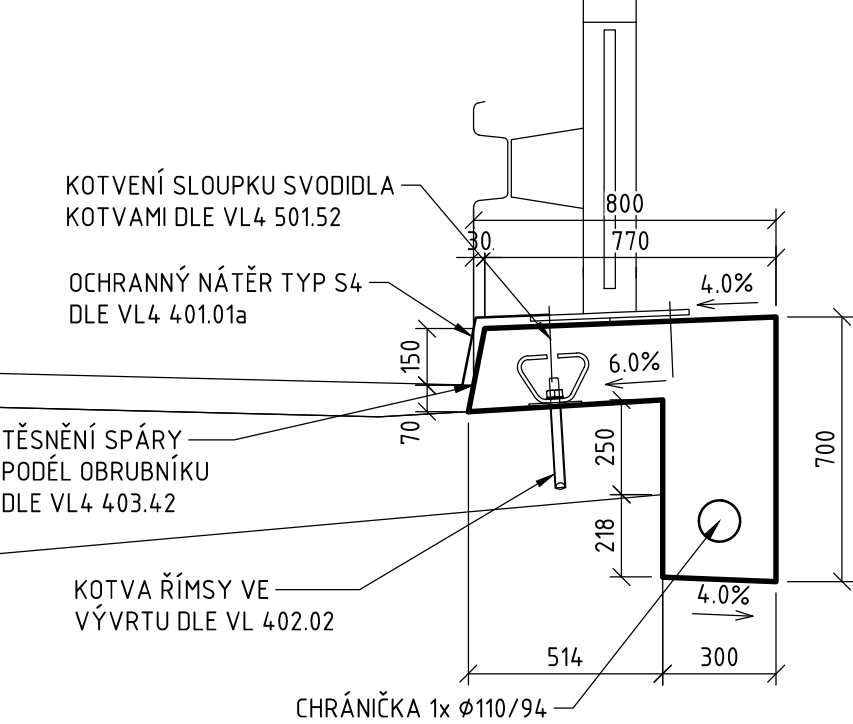

ŘEZ C-C 1:20




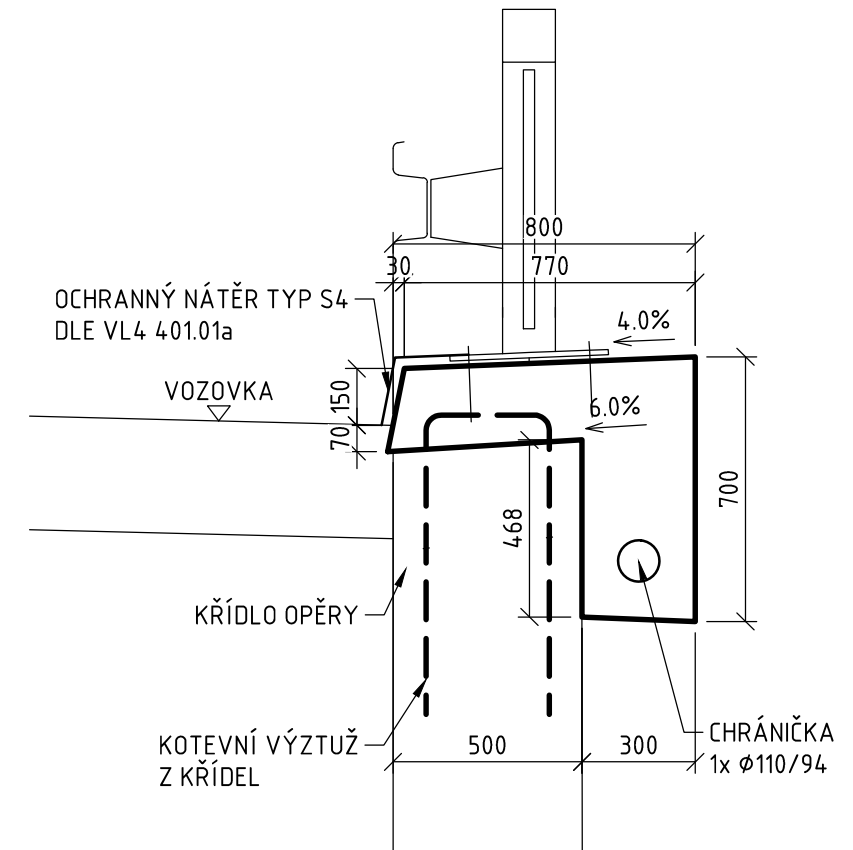


SOUŘADNICE VB

BOD	Y [m]	X [m]	Z [m]
101	696518.280	1011855.239	228.117
102	696517.992	1011857.722	225.559
103	696517.819	1011859.212	225.559
104	696527.752	1011860.366	225.559
105	696527.925	1011858.876	225.559
106	696528.214	1011856.392	228.117
901	696522.872	1011859.044	-
201	696518.091	1011871.177	218.468
202	696517.687	1011874.654	218.468
203	696524.342	1011875.426	218.468
204	696524.746	1011871.950	218.468
902	696521.217	1011873.302	-
301	696512.387	1011905.998	223.057
302	696512.110	1011908.382	223.057
303	696511.764	1011911.362	225.910
304	696521.697	1011912.515	225.910
305	696522.043	1011909.535	223.057
306	696522.320	1011907.151	223.057
903	696517.278	1011907.220	-

POZNÁMKY:

- VYTÝČOVACÍ ODCHYLKY: VIZ PŘÍLOHA E.4.5.1 - GVS - SEZNAM SOUŘADNIC
- NEDÍLNOU SOUČÁSTÍ VÝKRESU JSOU TECHNICKÉ SPECIFIKACE A POZNÁMKY UVEDENÉ NA VÝKRESE TECHNICKÝCH SPECIFIKACÍ A POZNÁMEK

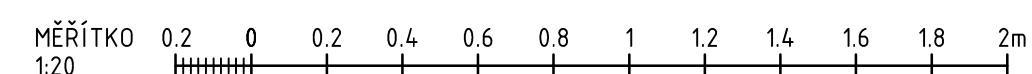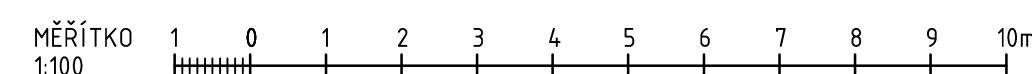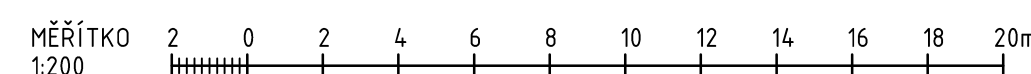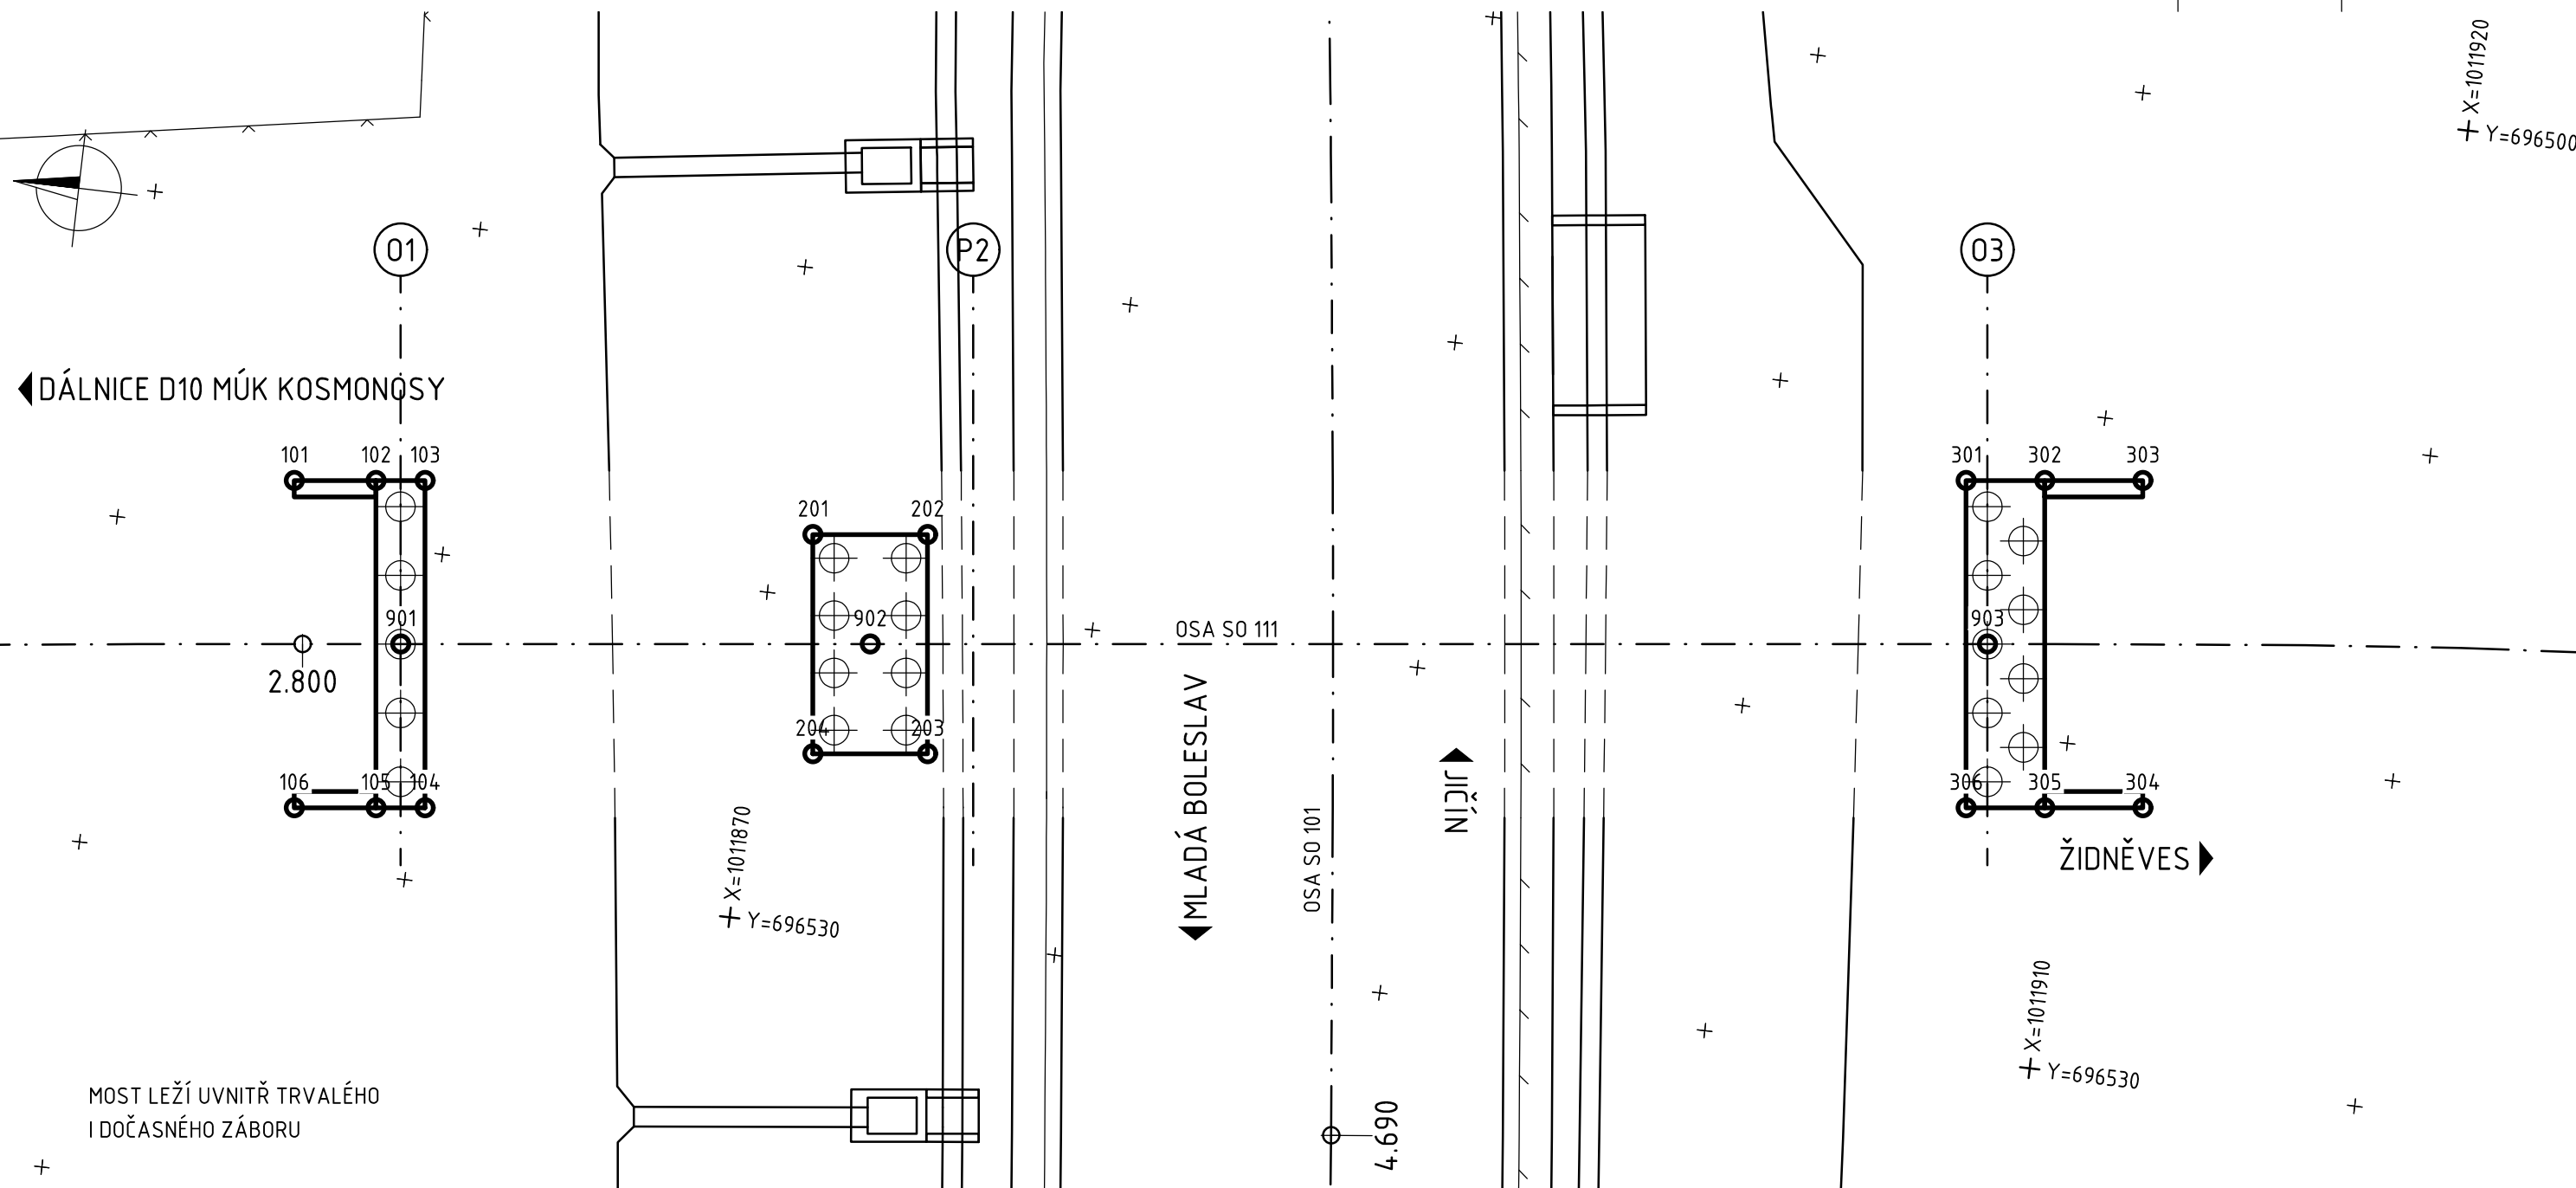

Souřadnicový systém: S-JTSK
Výškový systém: Bpv

SO 222 NADJEZD NA MÚK ŽIDNĚVES V KM 4,705

Objednatel: Ředitelství silnic a dálnic
Ředitelství silnic a dálnic s. p.
Čerčanská 2023/12, Krč, 140 00 Praha 4

Valbek, spol. s r.o.
Vaňurova 505/17
460 07 Liberec 3

Valbek
I/16 MLADÁ BOLESLAV - MARTINOVICE
204