




SCHÉMA ODVODNĚNÍ
PODÉLNÝ ŘEZ 1:100
◀ DÁLNIČE D10 MŮK KOSMONOSY

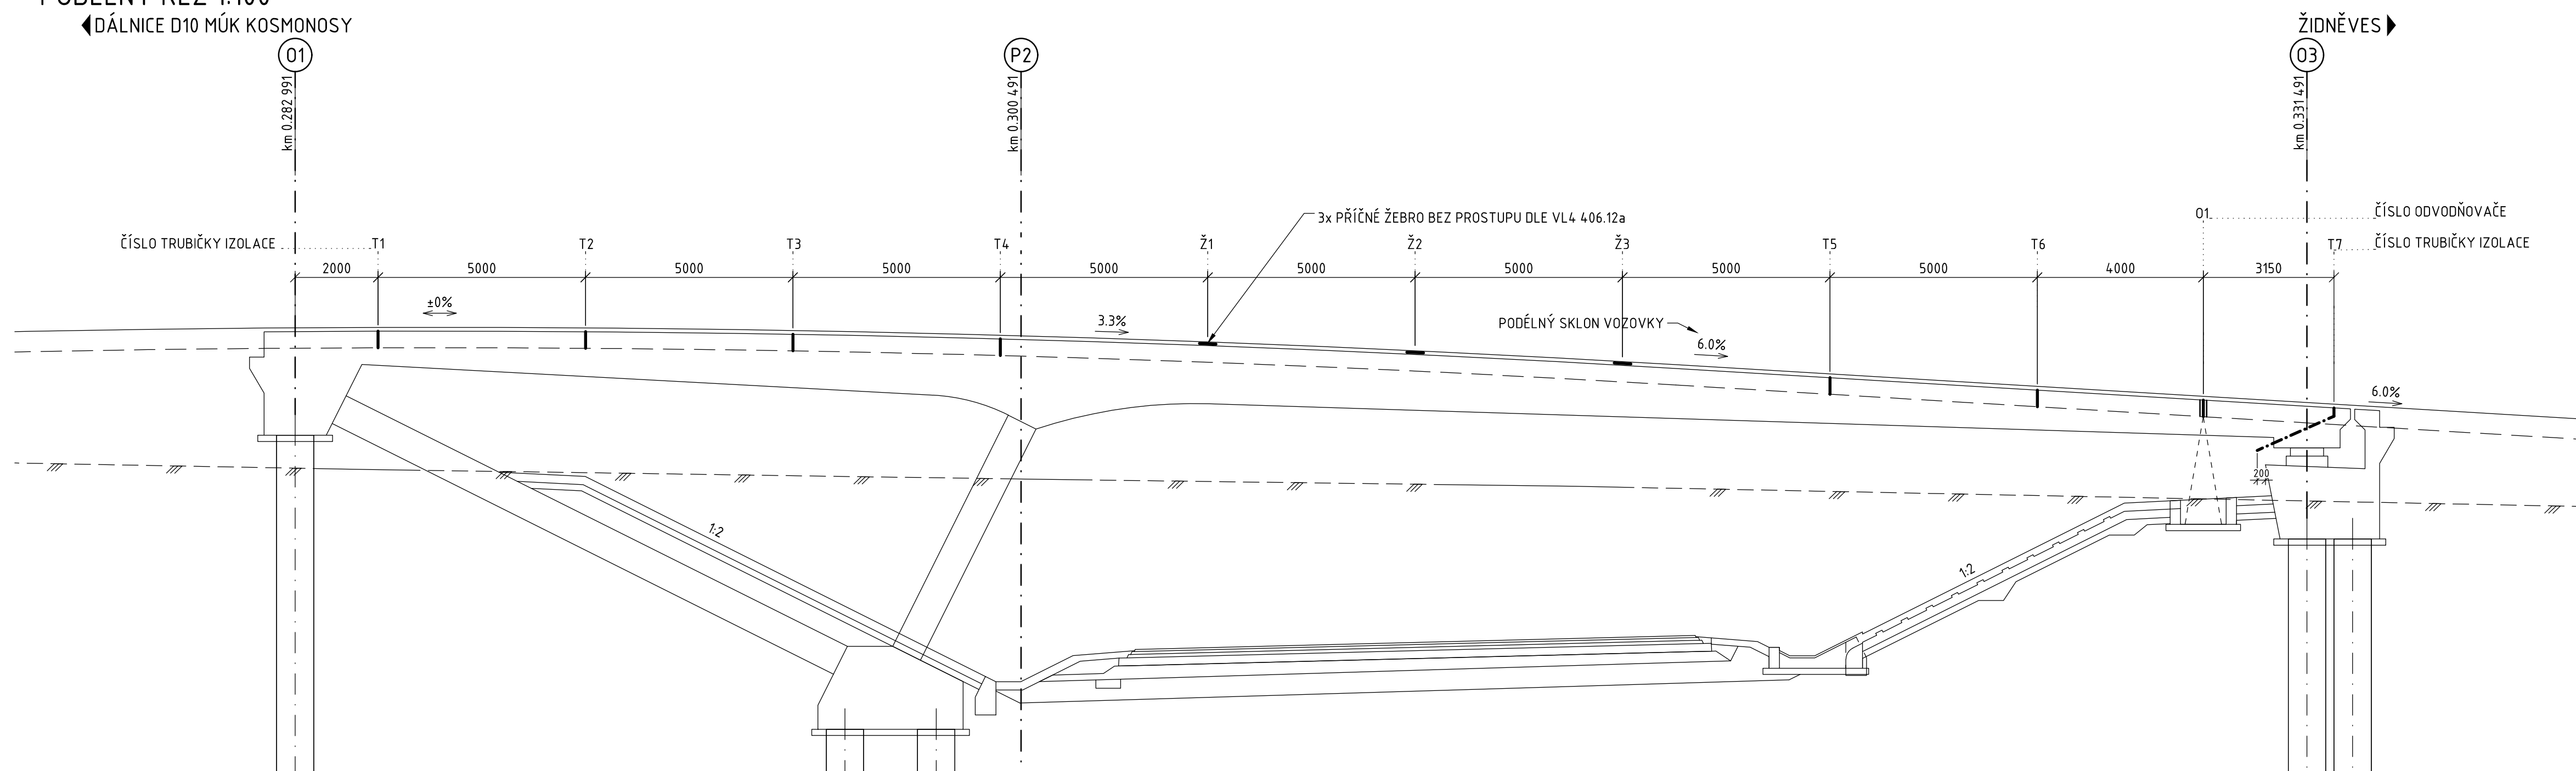


PŘÍČNÝ ŘEZ 1:50

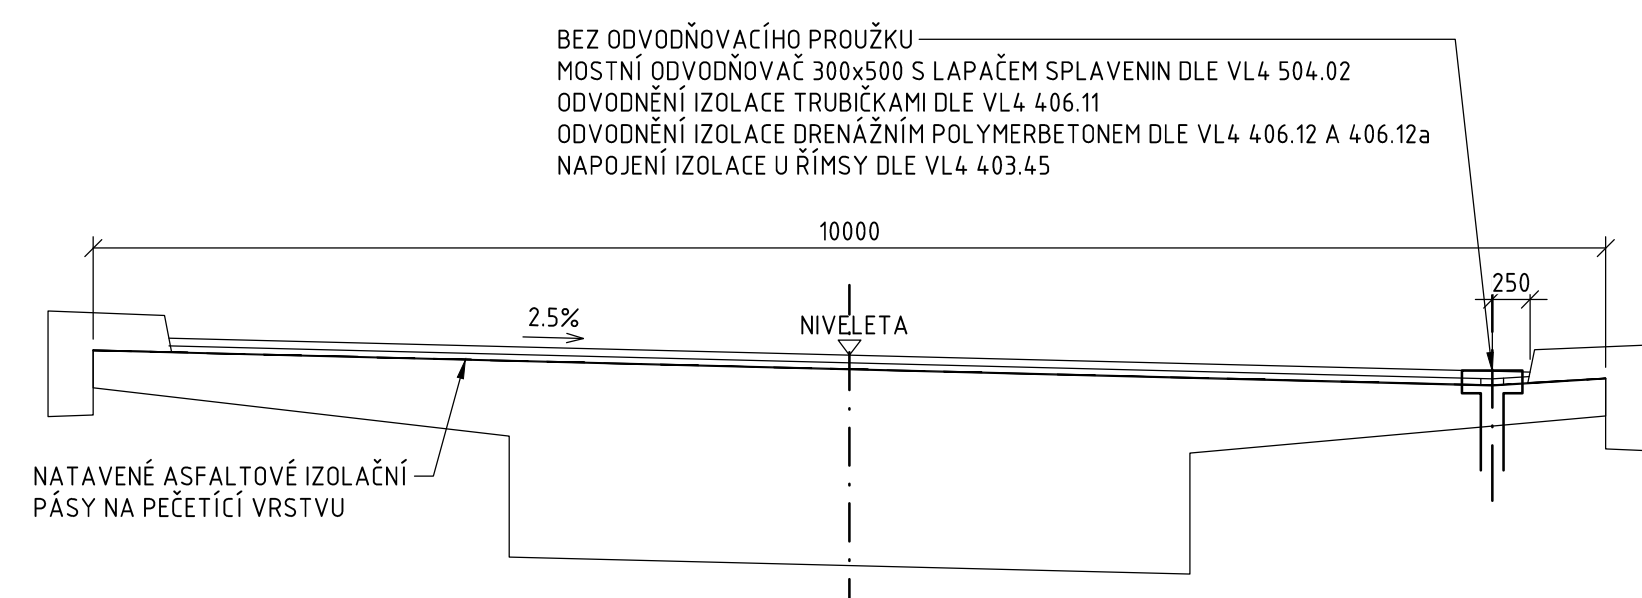

MOSTNÍ ZÁVĚR
PŘÍČNÝ ŘEZ NK V MÍSTĚ MZ 1:50

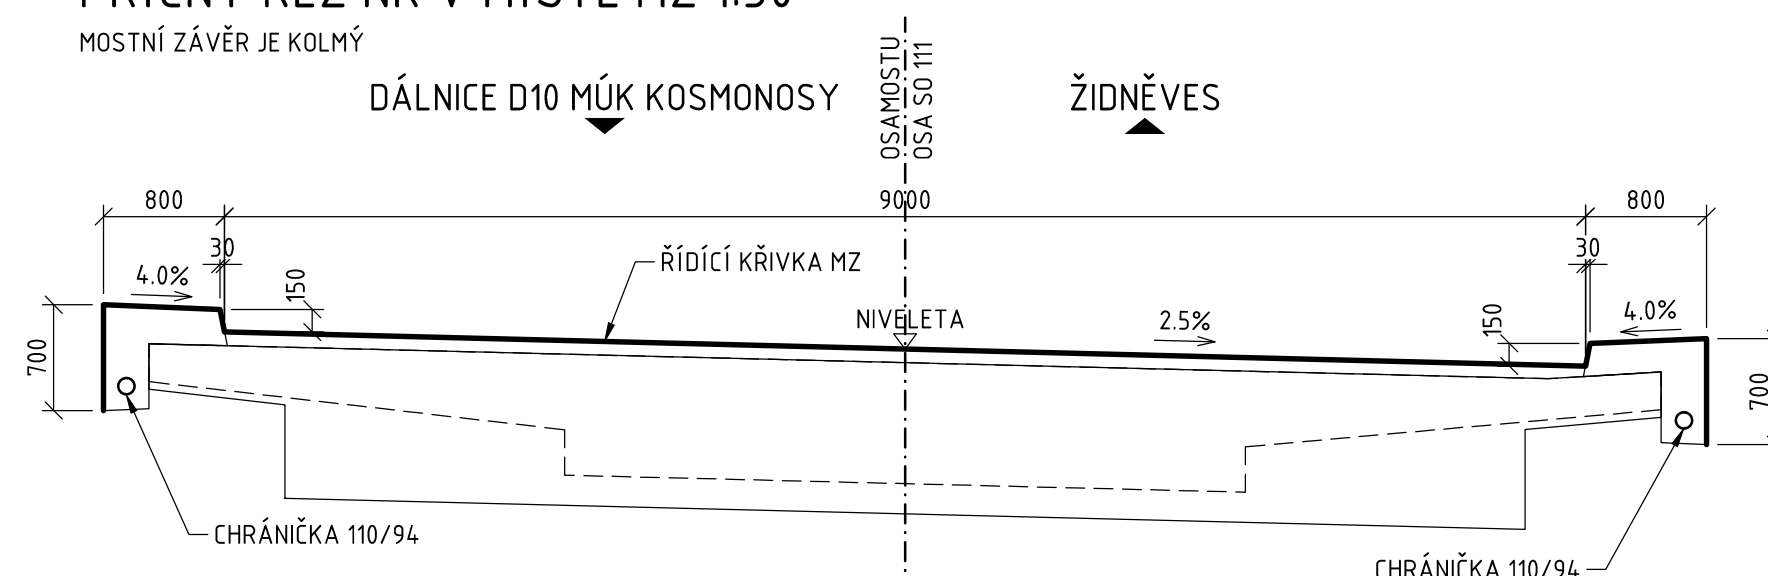

PŘÍČNÝ ŘEZ MOSTNÍM ZÁVĚREM VE
VOZOVCE 1:50

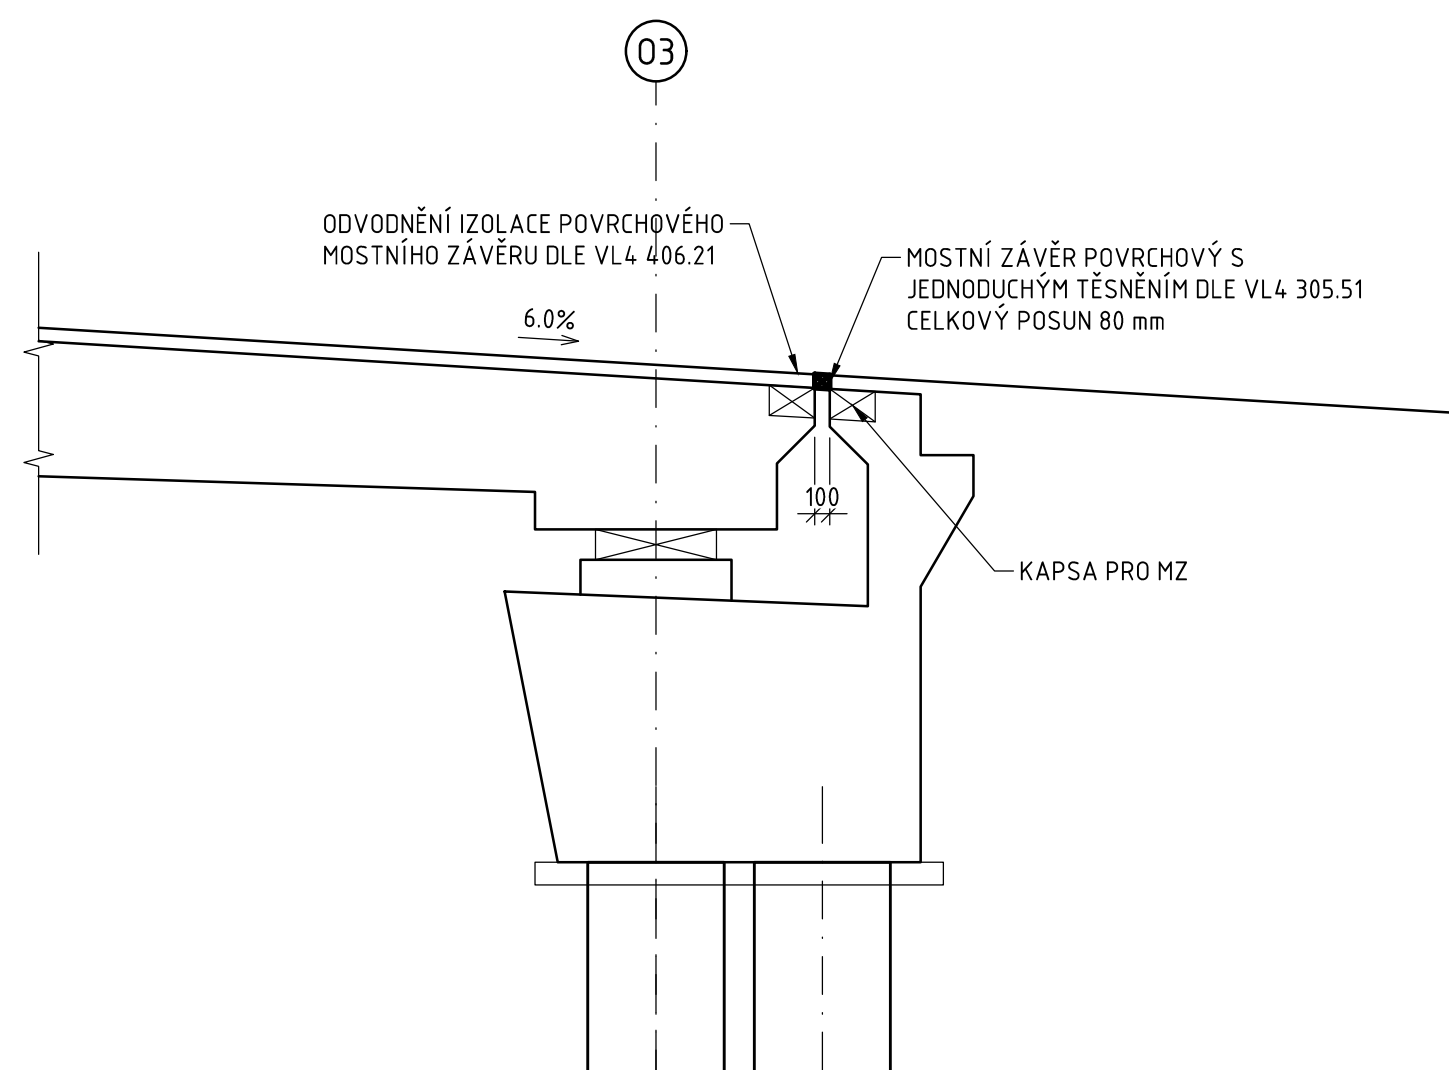

ROZMÍSTĚNÍ LOŽISEK – PŮDORYS

PODPĚRA	(01)	(P2)	(03)	×	VETKNUTÍ
ČÍSLO LOŽISKA	×	×	1		LOŽISKO JEDNOSMĚRNĚ POSUVNÉ
ČÍSLO LOŽISKA	×	×	2		LOŽISKO VŠESMĚRNĚ POSUVNÉ

TABULKA LOŽISEK

PODPĚRA		OPĚRA 3	
ČÍSLO LOŽISKA		1	2
DRUH LOŽISKA		HRNCOVÉ	HRNCOVÉ
POPIS		PODÉLNĚ POSUVNÉ	VŠESMĚRNĚ POSUVNÉ
MAX. SVISLÉ PROVOZNÍ ZATÍŽENÍ (MSP)	[kN]	2700	2700
MAX. SVISLÉ NÁVRHOVÉ ZATÍŽENÍ (MSÚ)	[kN]	3600	3600
MIN. SVISLÉ NÁVRHOVÉ ZATÍŽENÍ (MSÚ)	[kN]	1600	1600
MAX. VODOROVNÉ NÁVRHOVÉ ZATÍŽENÍ PODÉLNĚ (MSÚ)	[kN]	0	0
MAX. VODOROVNÉ NÁVRHOVÉ ZATÍŽENÍ PŘÍČNĚ (MSÚ)	[kN]	140	0
POSUN PODÉLNĚ CELKOVÝ (MSÚ) (z mostu + do mostu)	[mm]	90	90
POSUN PODÉLNĚ CELKOVÝ (MSP) (z mostu + do mostu)	[mm]	73	73
POSUN PŘÍČNĚ CELKOVÝ (MSÚ)	[mm]	0	7

POZNÁMKY:

- NEDÍLNOU SOUČÁSTÍ VÝKRESU JSOU TECHNICKÉ SPECIFIKACE A POZNÁMKY UVEDENÉ NA VÝKRESE
TECHNICKÝCH SPECIFIKACÍ A POZNÁMEK

Souřadnicový systém: S-JTSK
Výškový systém: Bpv

SO 222 NADJEZD NA MÚK ŽIDNĚVES V KM 4.705

Objednatel:

Ředitelství silnic a dálnic s. p.
Čerčanská 2023/12, Krč, 140 00 Praha 4



Valbek, spol. s r.o.
Vaňurova 505/17
460 07 Liberec 3

	Vypracoval	T. MALIKOVÁ	<i>Tatky Salaty</i>	Zak. číslo	21-LH3-001
	Zodp. projektant	ING. O. ŠABATA	<i>Tatky Salaty</i>	Datum	02/2025
	Tech. kontrola	ING. I. BELDA	<i>BELDA</i>	Stupeň	PDPS
	Akce	I/16 MLADÁ BOLESLAV - MARTINOVICE			Počet formátů
				Měřítko	NA VÝKRES
				C. přílohy	Pare
Zhotovitel: Valbek, spol. s r.o. Valbarkova 805/17 460 01 Ústí nad Labem 3	Příloha	SCHÉMA ODVODNĚNÍ, MOSTNÍ ZÁVĚRY, SCHÉMA LOŽISEK			205

