






PŮDORYS 1:150

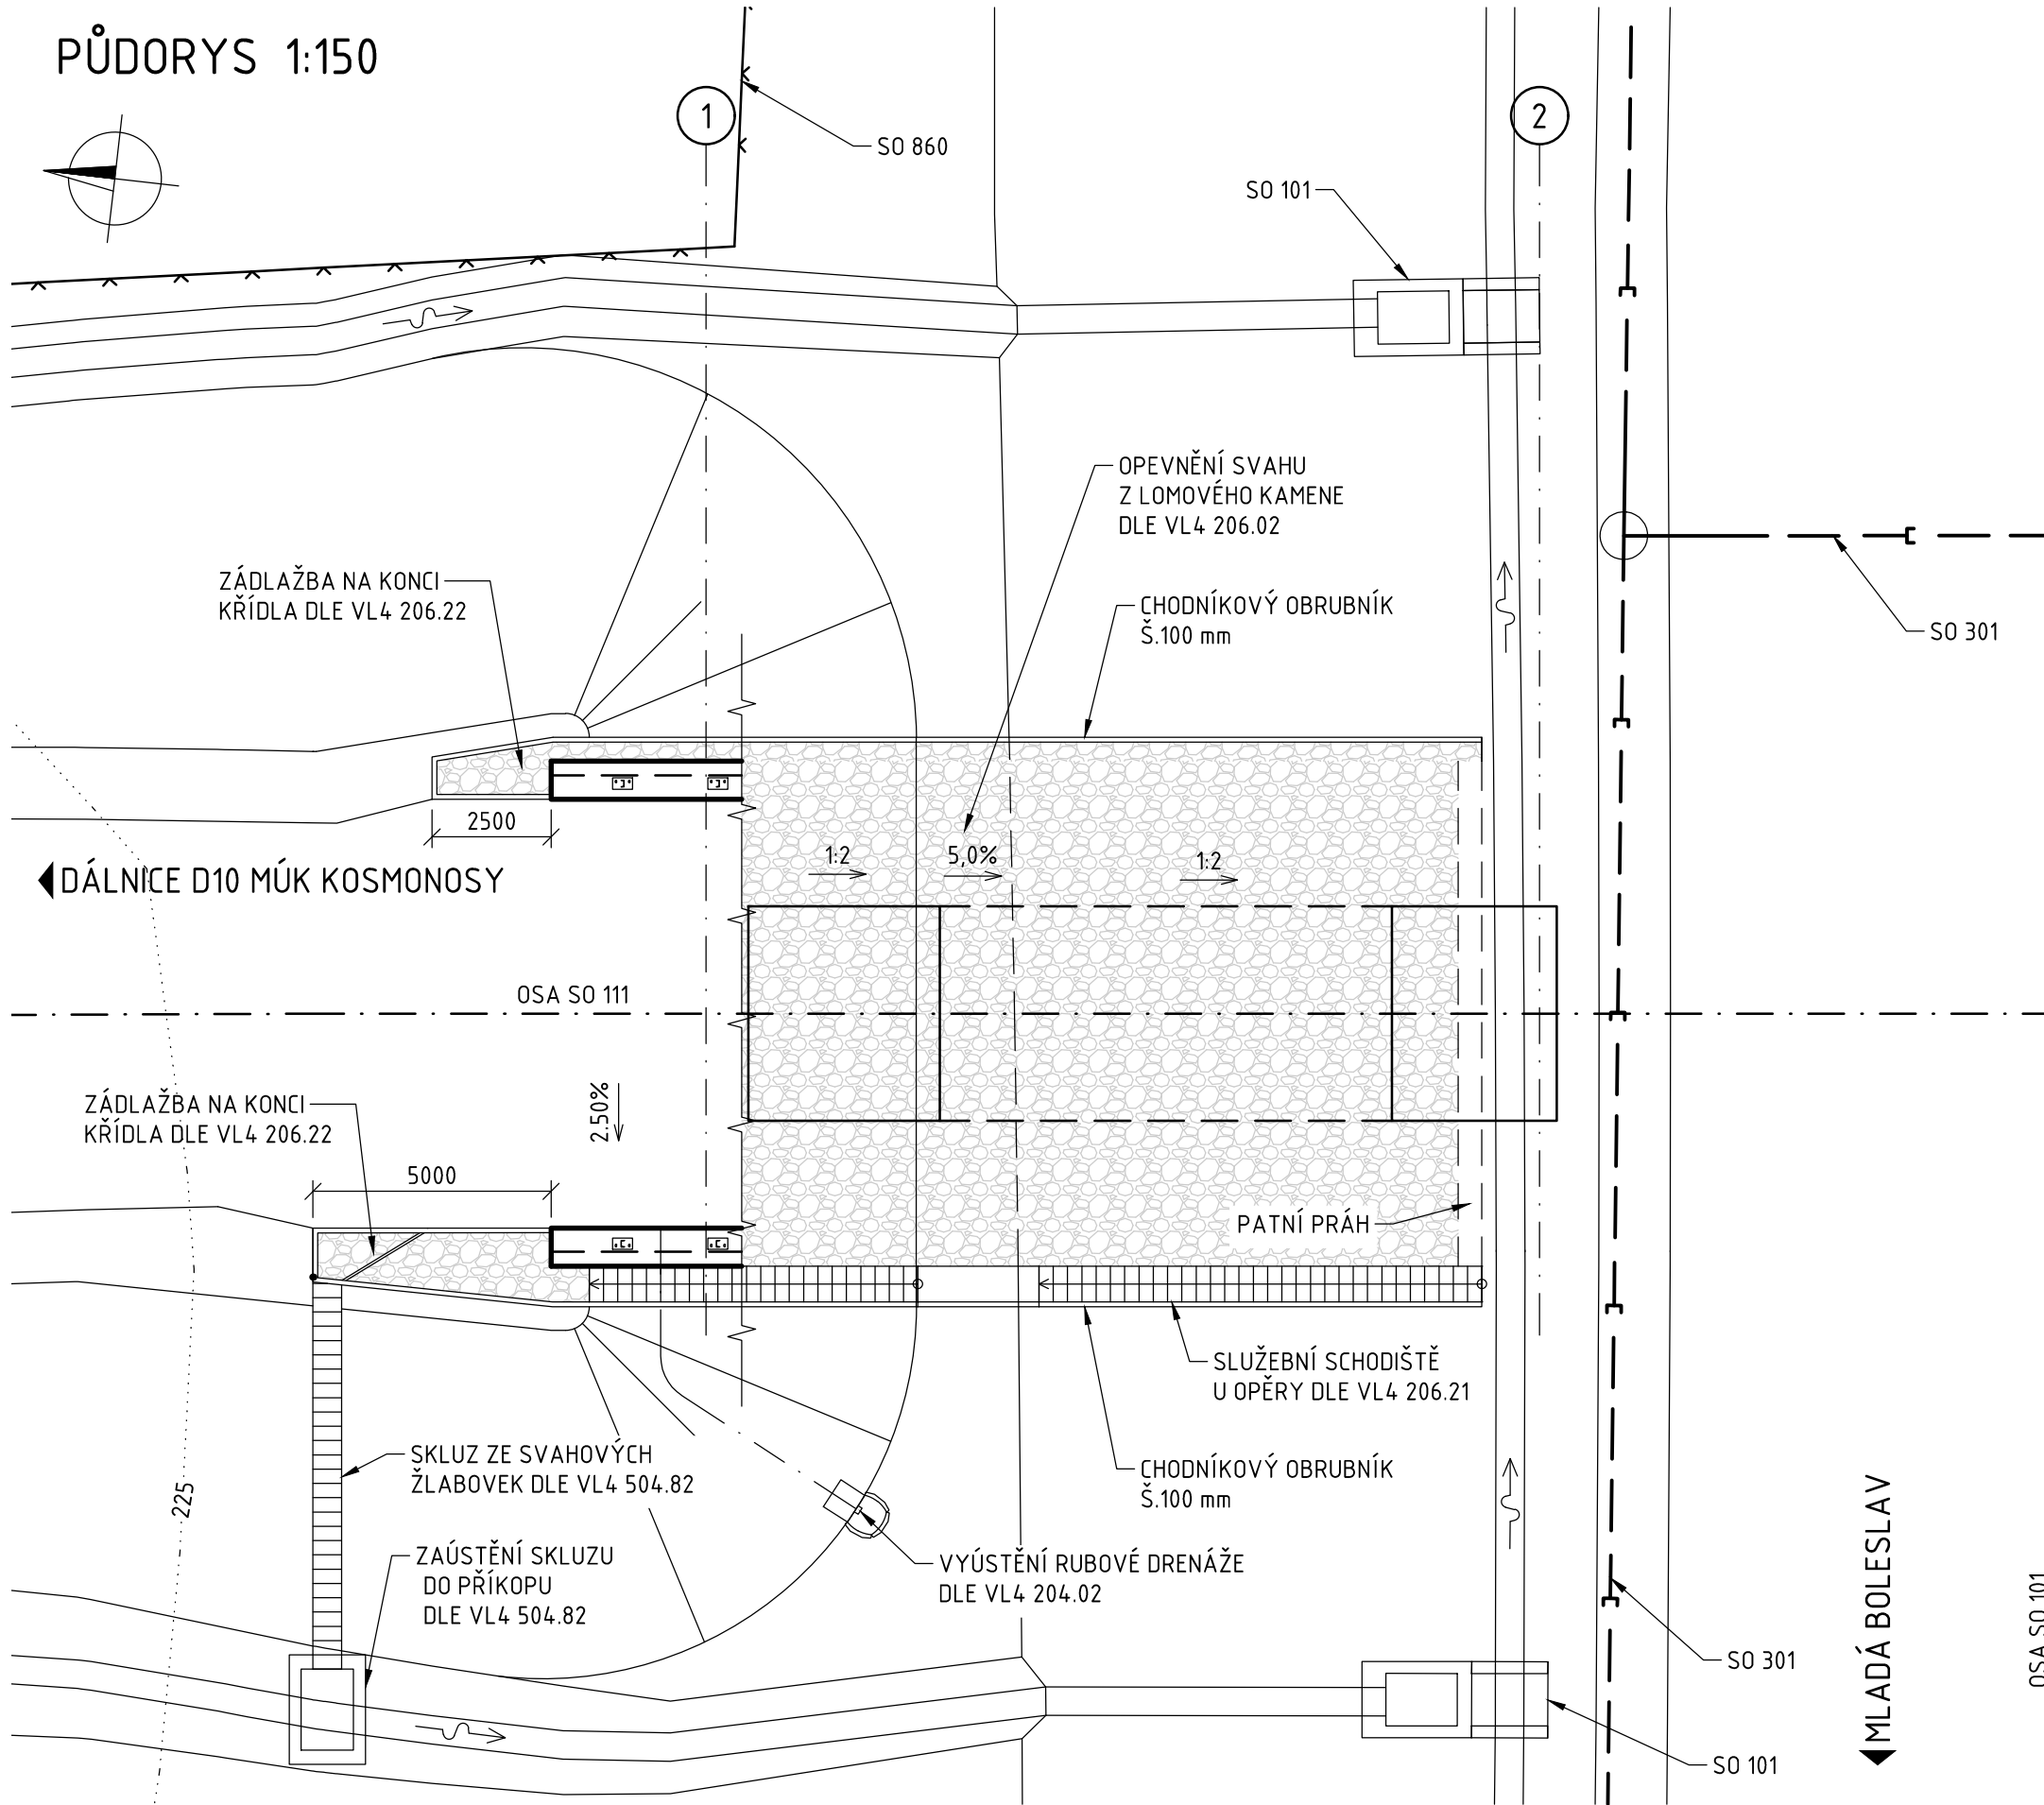


SLUŽEBNÍ SCHODIŠTĚ PODÉL KŘÍDLA OPĚRY 01 1: 100

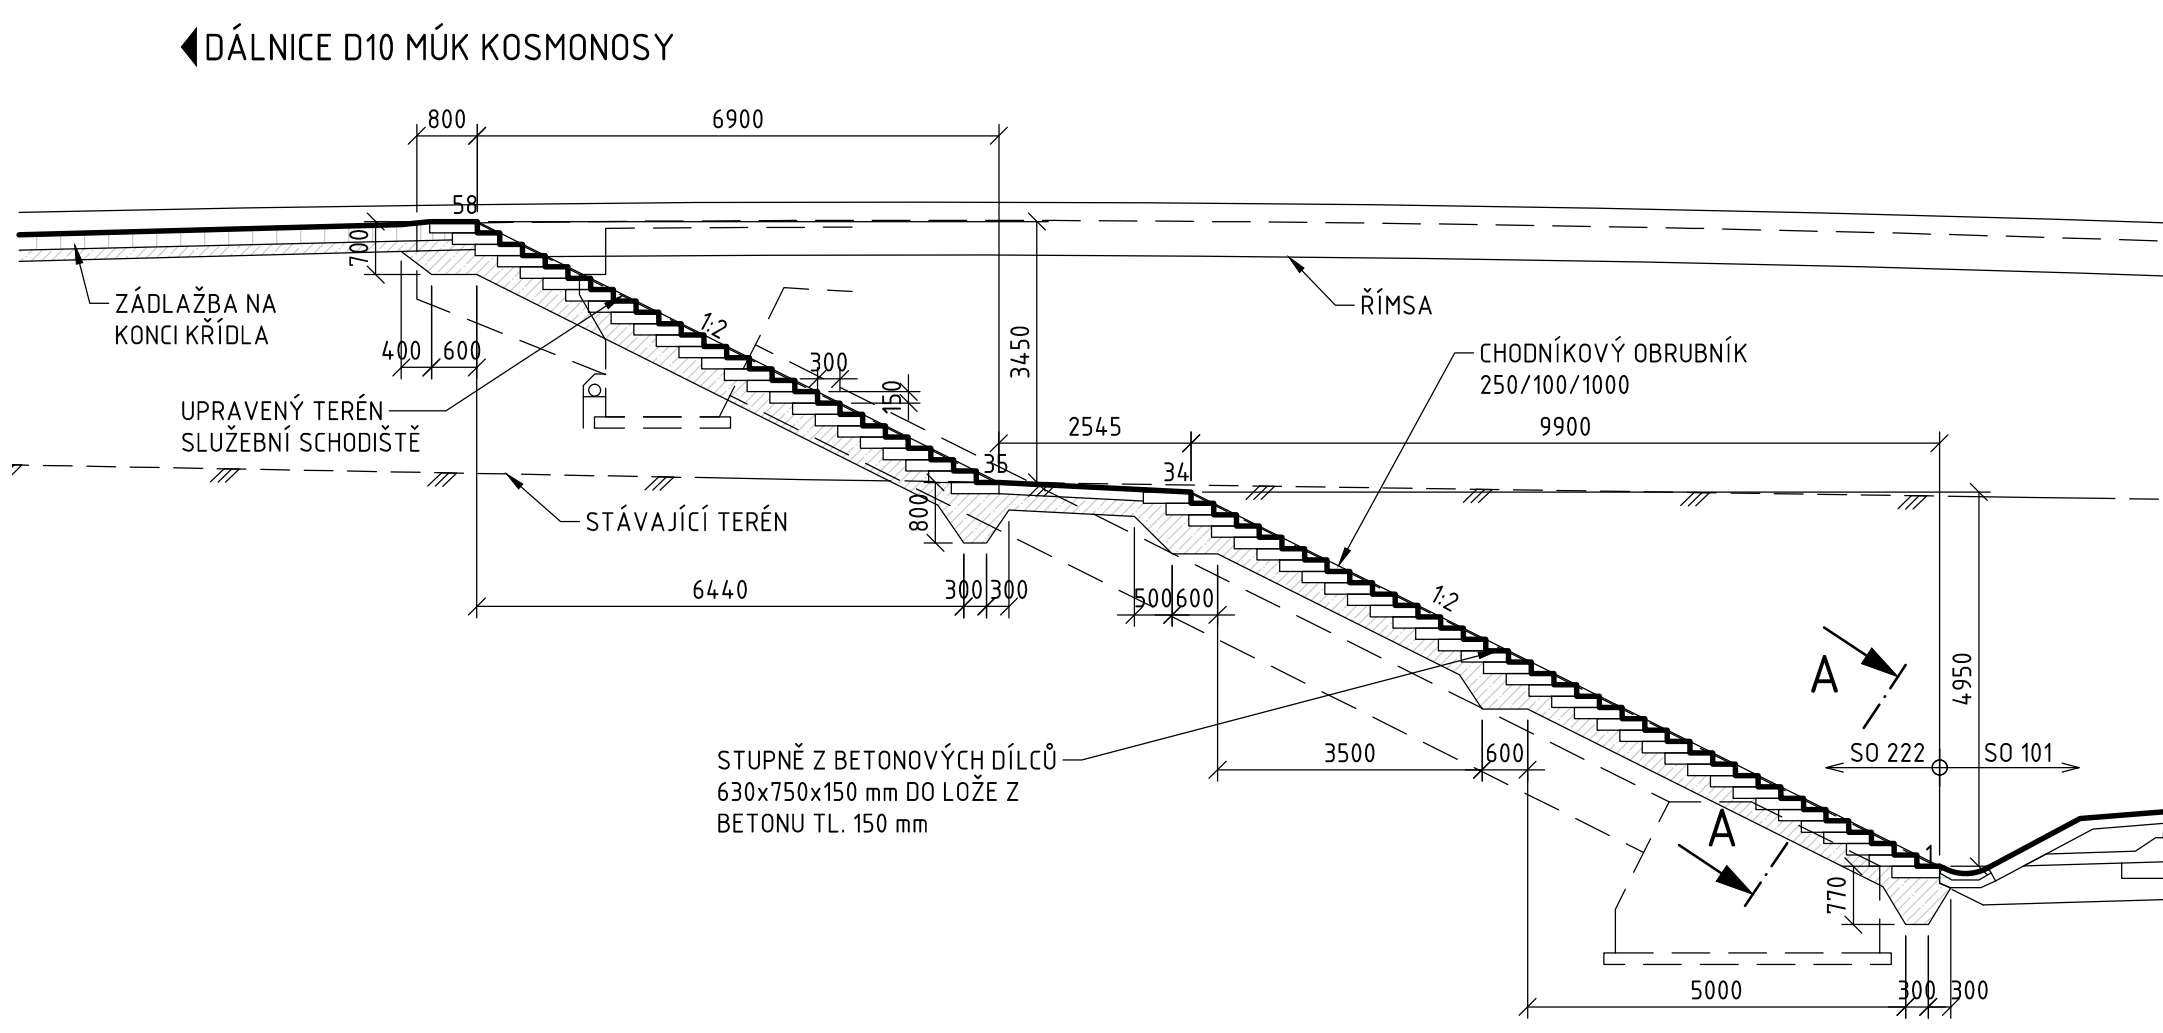



PODÉLNÝ ŘEZ ODLÁŽDĚNÍM POD MOSTEM 1:75

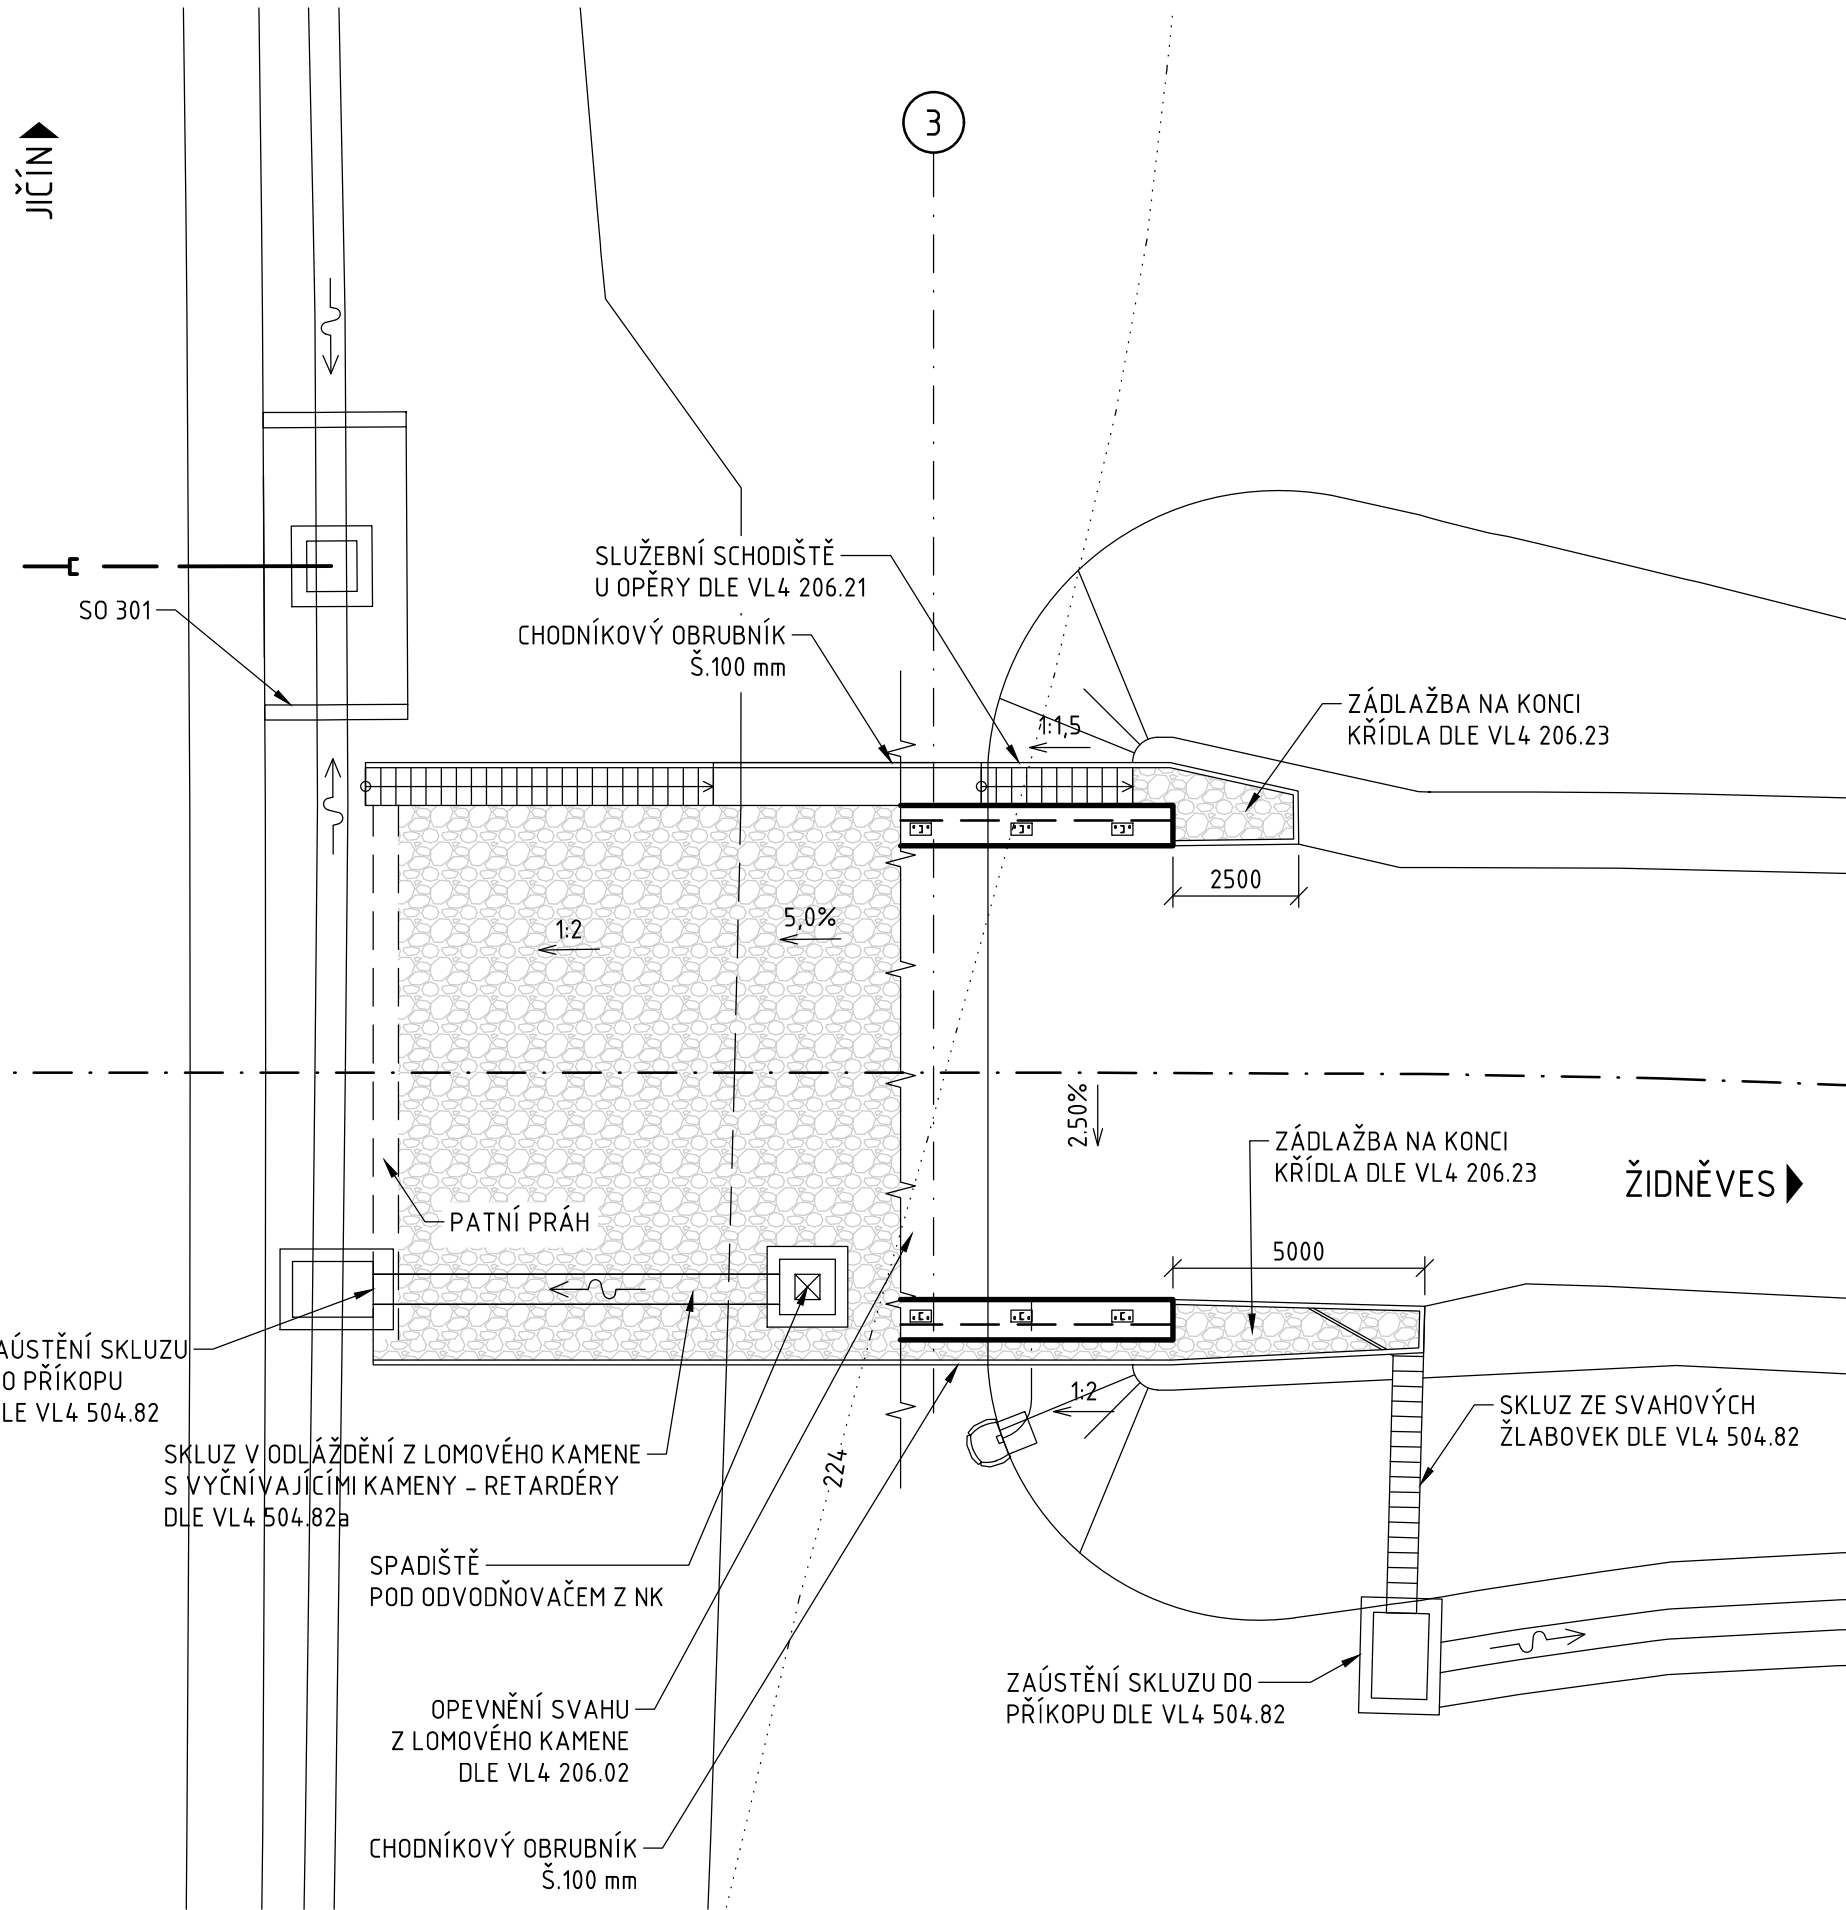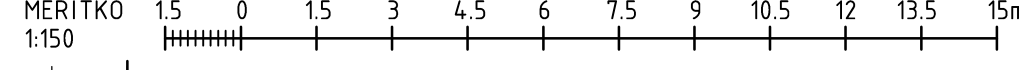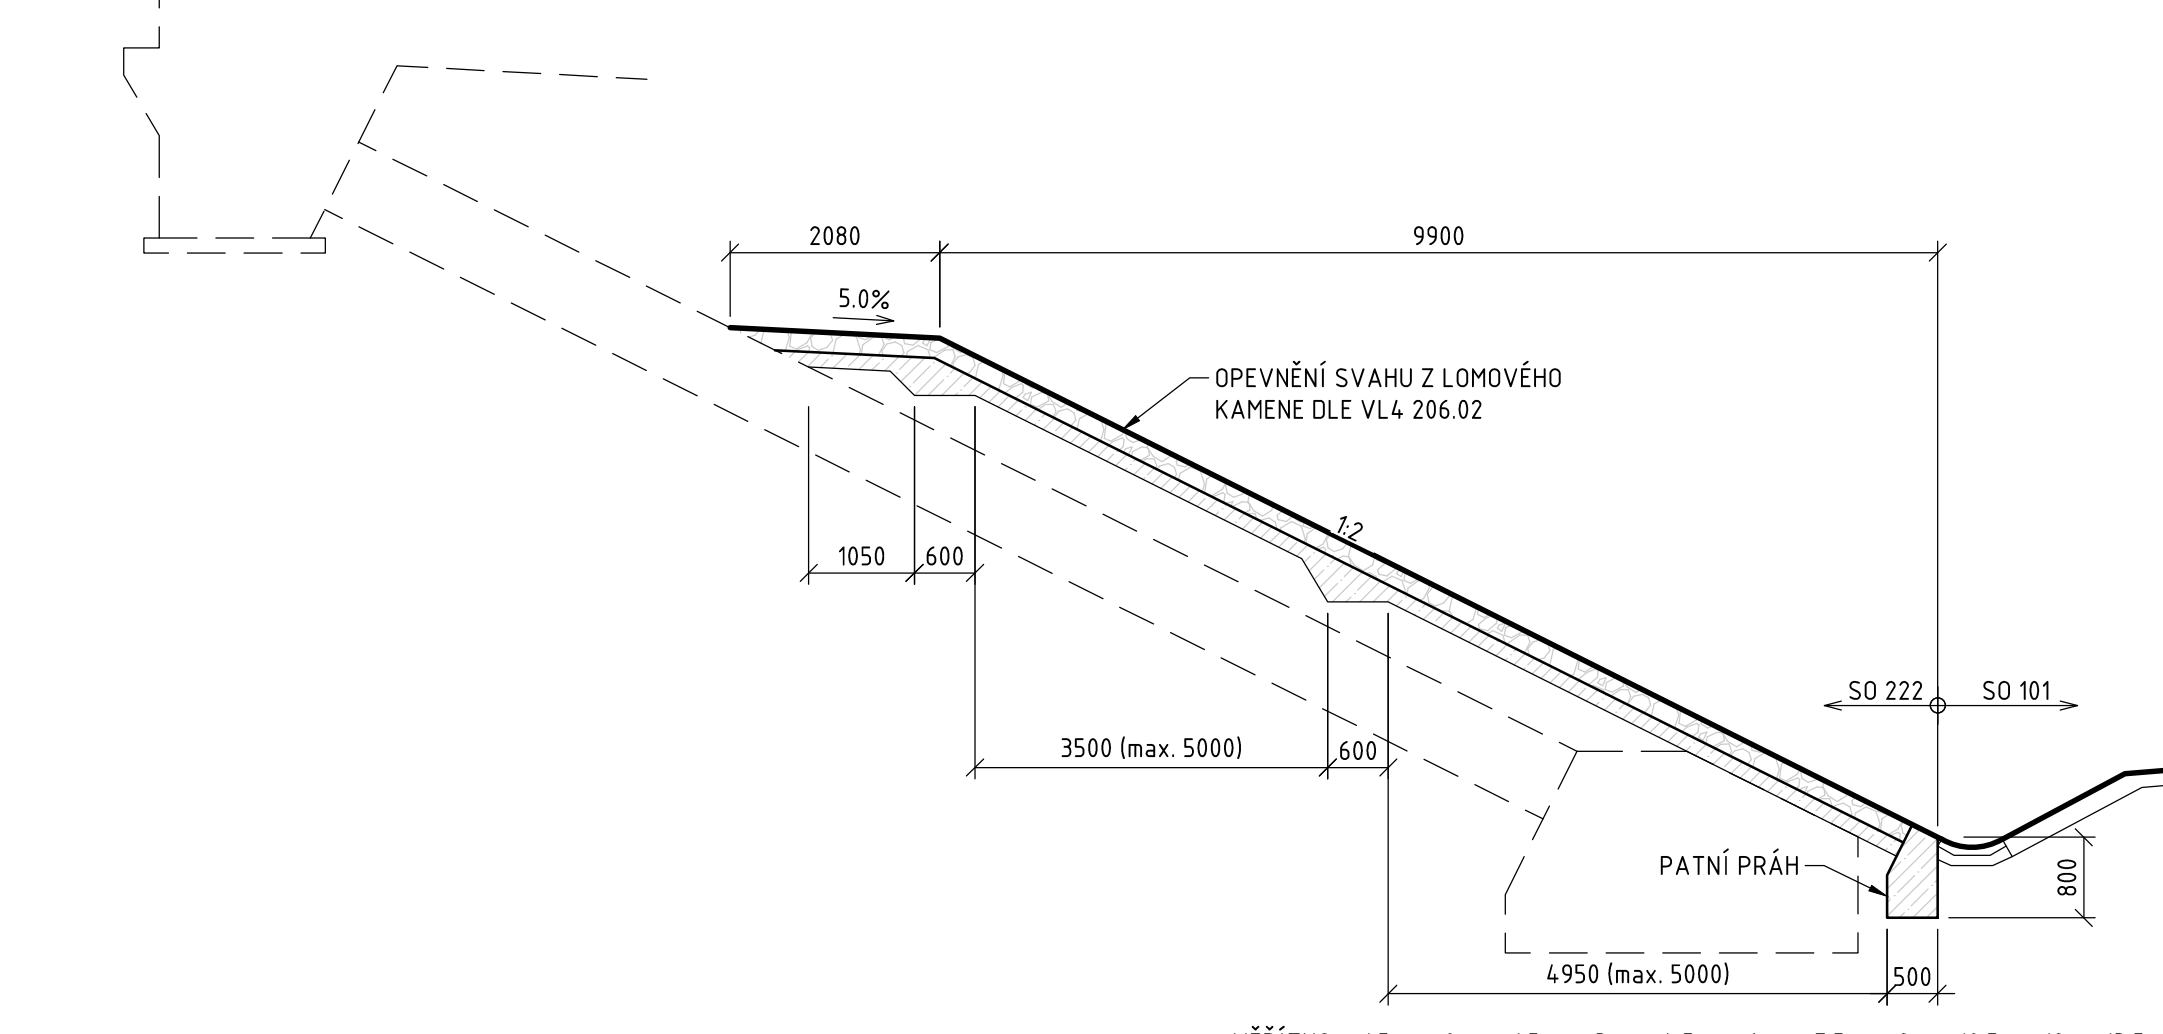


SLUŽEBNÍ SCHODIŠTĚ PODÉL KŘÍDLA OPĚRY 03 1: 100

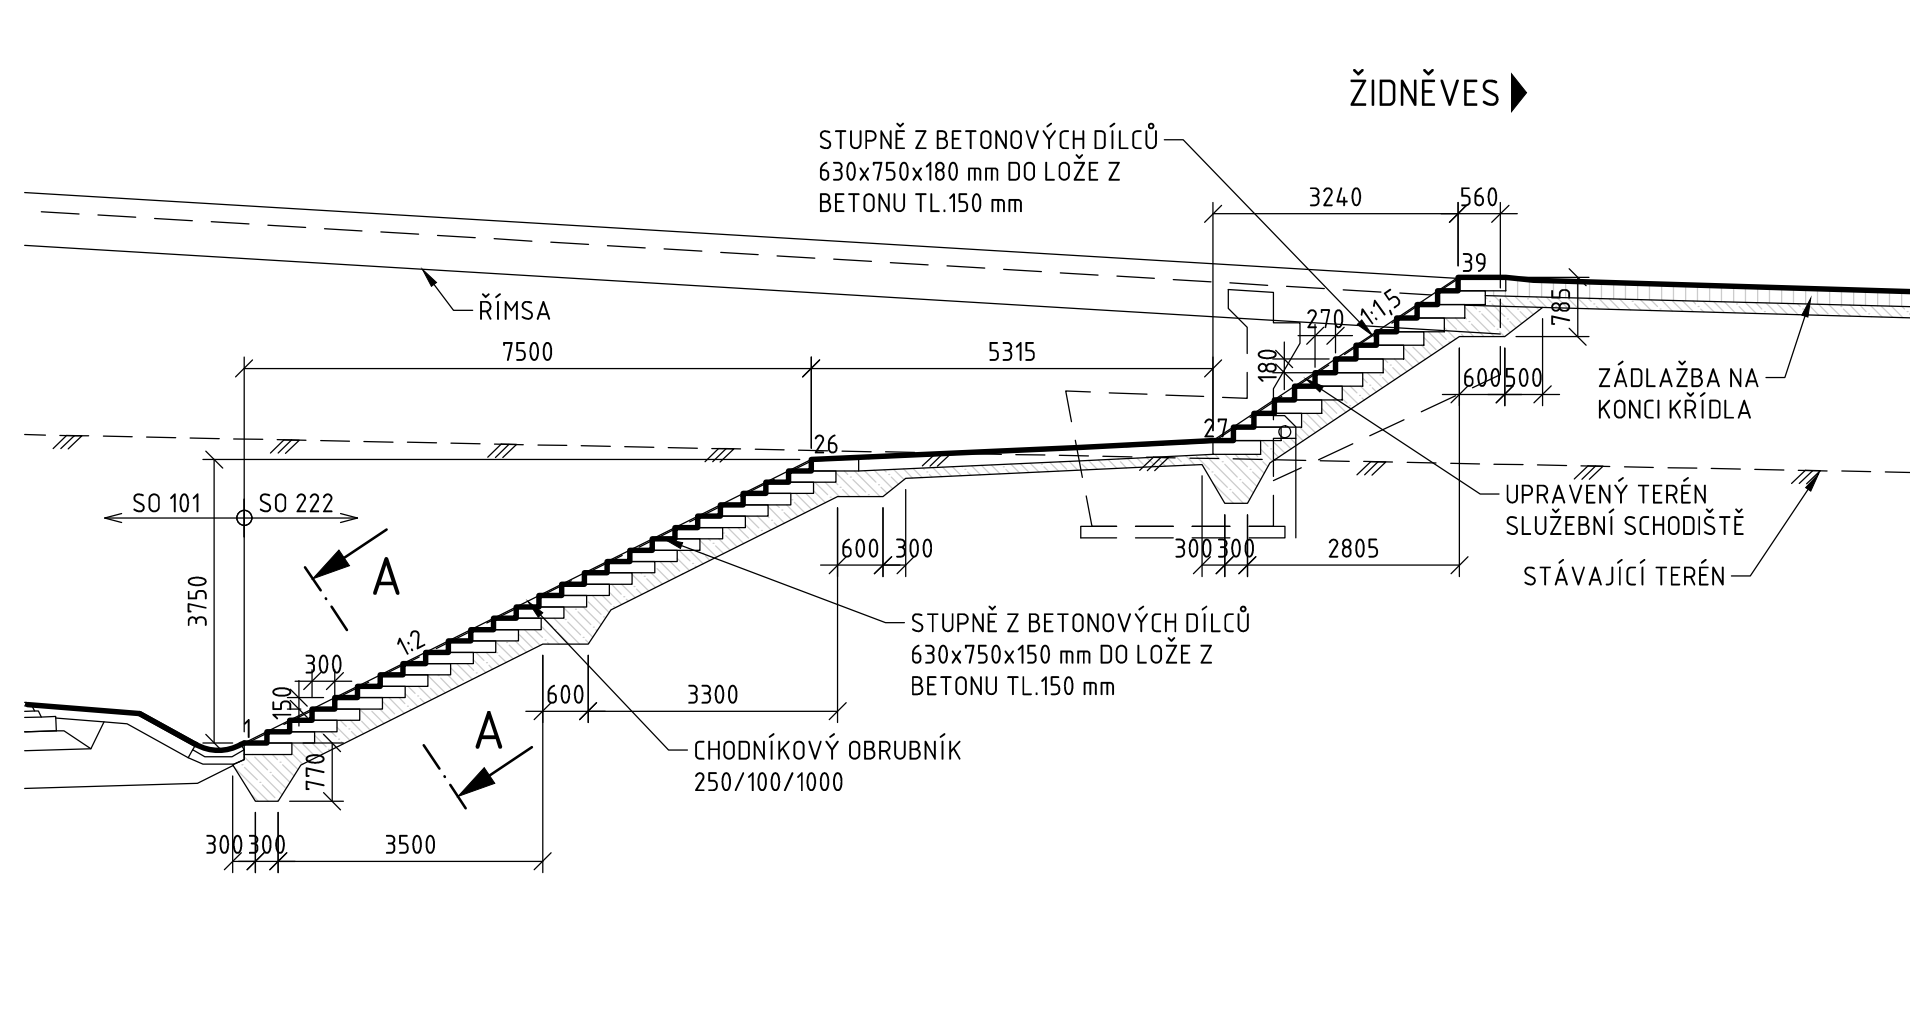


PODÉLNÝ ŘEZ ODLÁŽDĚNÍM POD MOSTEM 1:75

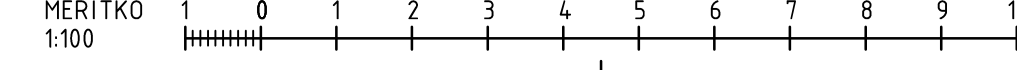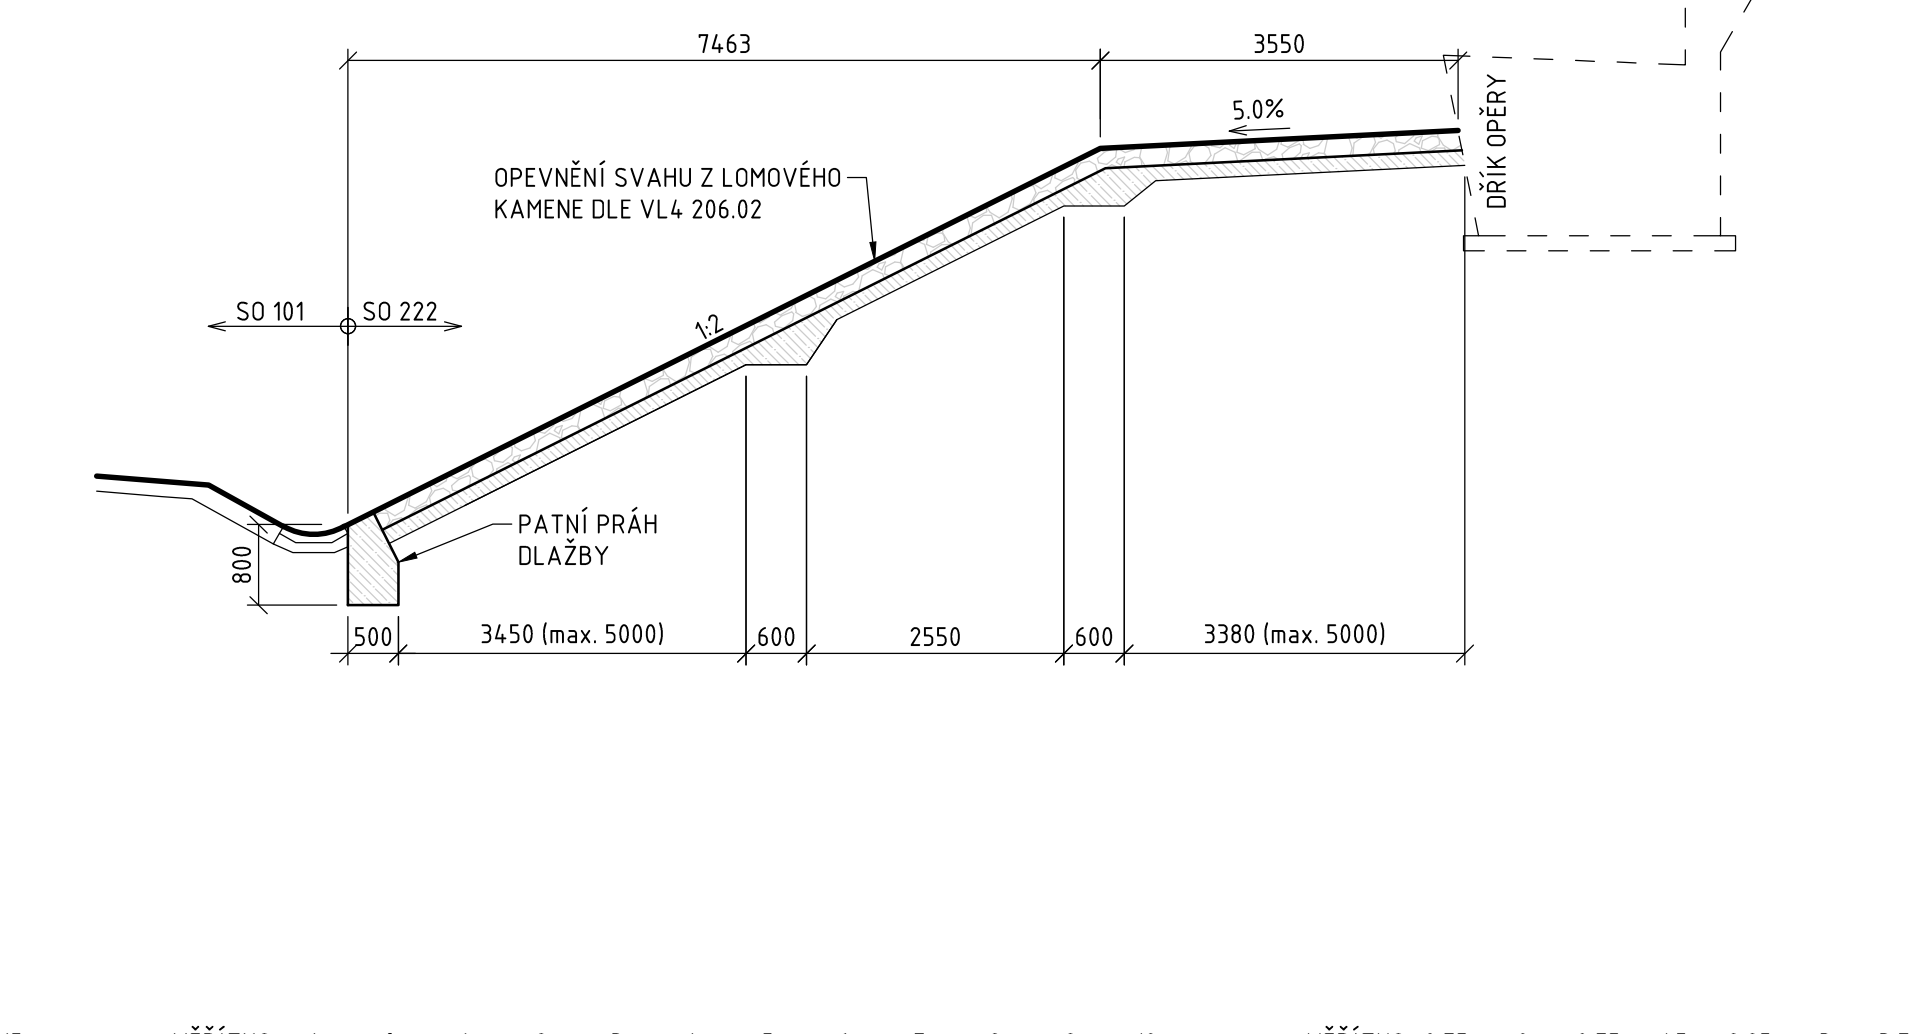


PODÉLNÝ ŘEZ SKLUZEM V ODLÁŽDĚNÍ POD MOSTEM 1:75

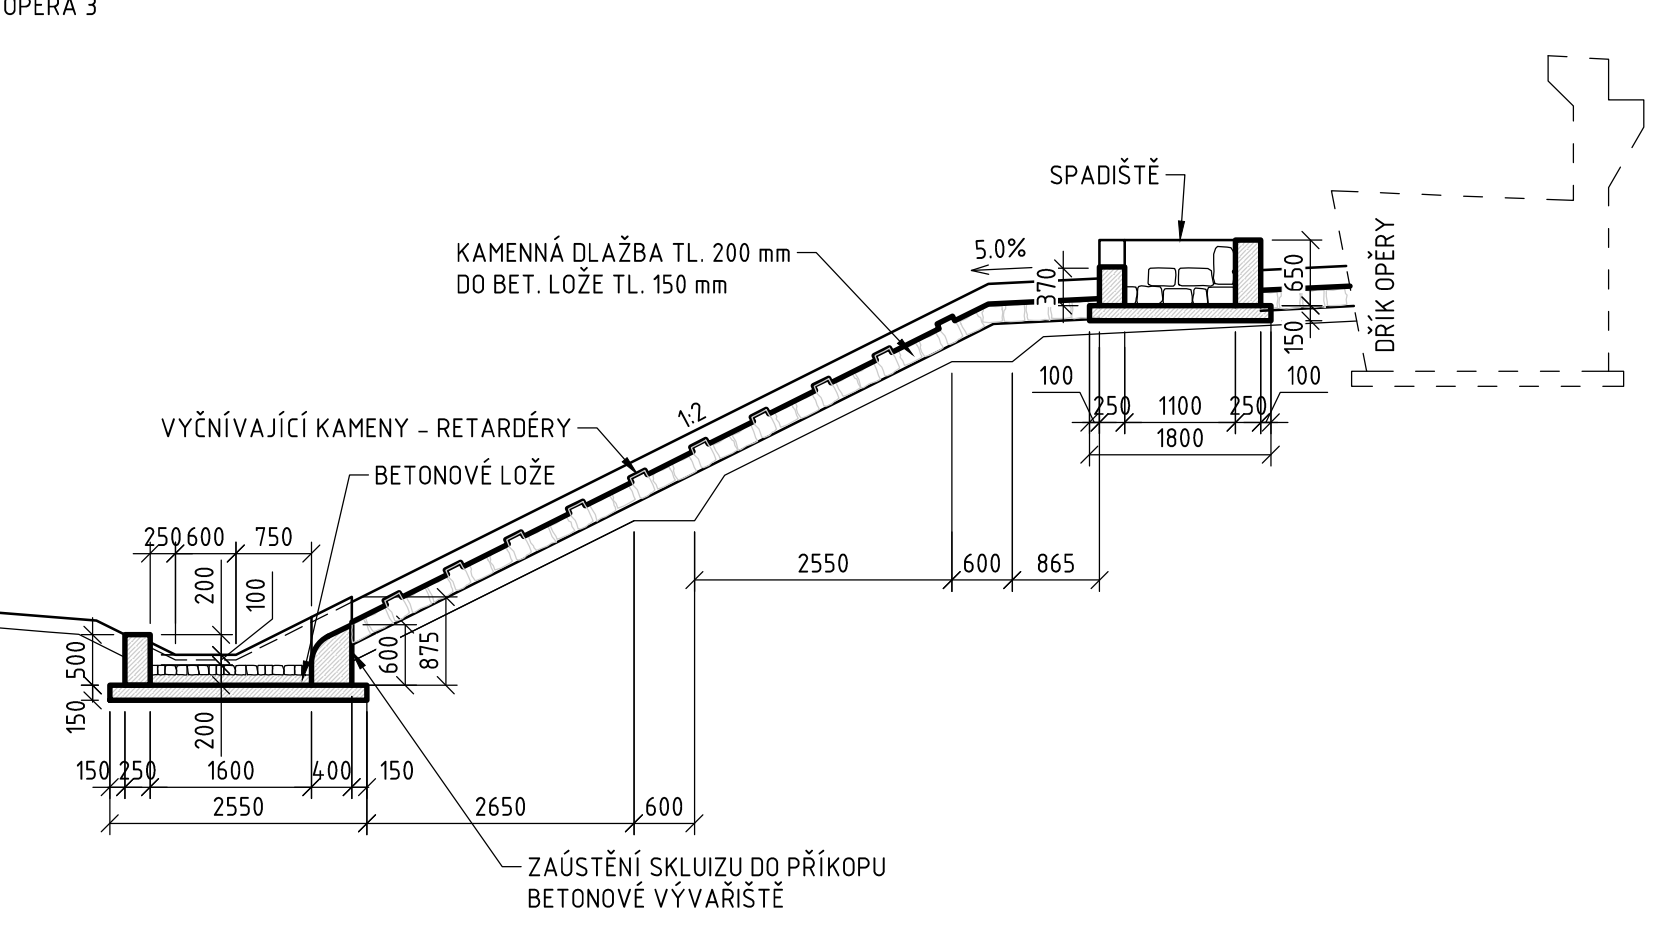

ŘEZ A-A 1:25

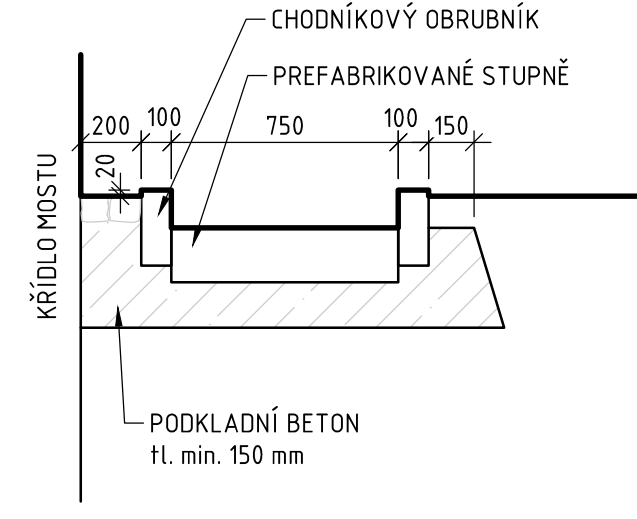

PŘÍČNÝ ŘEZ SKLUZEM

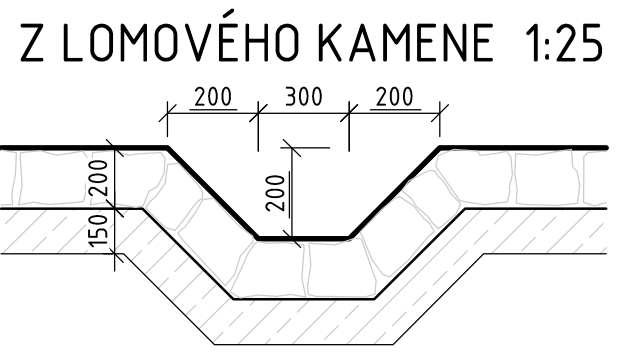

POZNÁMKY:
- NEJEDNOU SOUČÁSTÍ VÝKRESU JSOU TECHNICKÉ SPECIFIKACE A POZNÁMKY UVEDENÉ NA VÝKRESE
TECHNICKÝCH SPECIFIKACÍ A POZNÁMEK

Souřadnicový systém: S-JTSK Výškový systém: Bpv		SO 222 NADJEZD NA MÚK ŽIDNĚVES V KM 4,705	
Objednatel: ŘEDITELSTVÍ SILNIC A DÁLNIC		Ředitelství silnic a dálnic s. p. Čerčanská 2023/12, Krč, 140 00 Praha 4	
Valbek, spol. s r.o. Vaňurova 505/17 460 07 Liberec 3		Zak. číslo 21-L113-001	
Valbek, spol. s r.o. Vaňurova 505/17 460 07 Liberec 3		Datum 02/2025	
Valbek, spol. s r.o. Vaňurova 505/17 460 07 Liberec 3		Stupeň PDPS	
Valbek, spol. s r.o. Vaňurova 505/17 460 07 Liberec 3		Počet formátů 8x A4	
Valbek, spol. s r.o. Vaňurova 505/17 460 07 Liberec 3		Měřítko NA VÝKRESE	
Valbek, spol. s r.o. Vaňurova 505/17 460 07 Liberec 3		Paré	
Příloha ÚPRAVY POD MOSTEM, SLUŽEBNÍ SCHODIŠTĚ		206	