

ROZMÍSTĚNÍ VÝZTUŽE NK V PODÉLNÉM SMĚRU 1:100



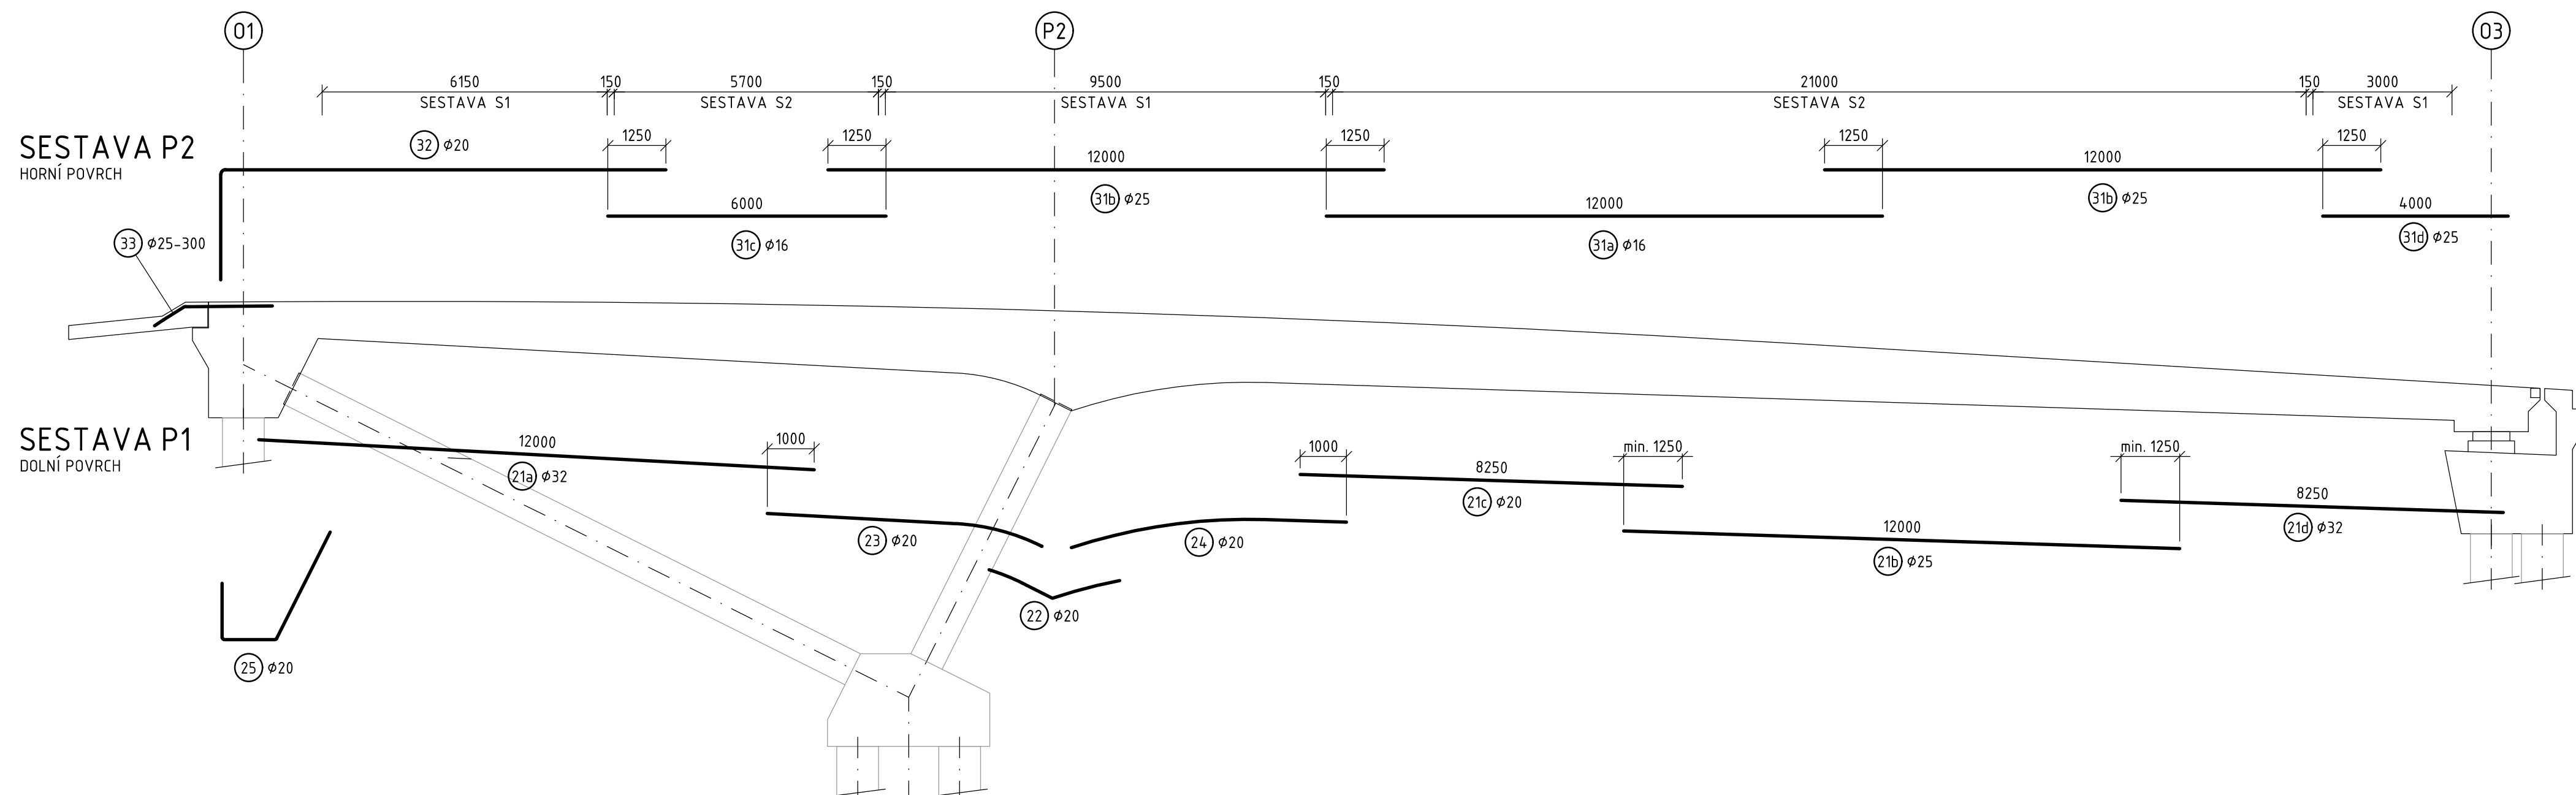


SCHÉMA VÝZTUŽE NK
PŘÍČNÝ ŘEZ 1:50

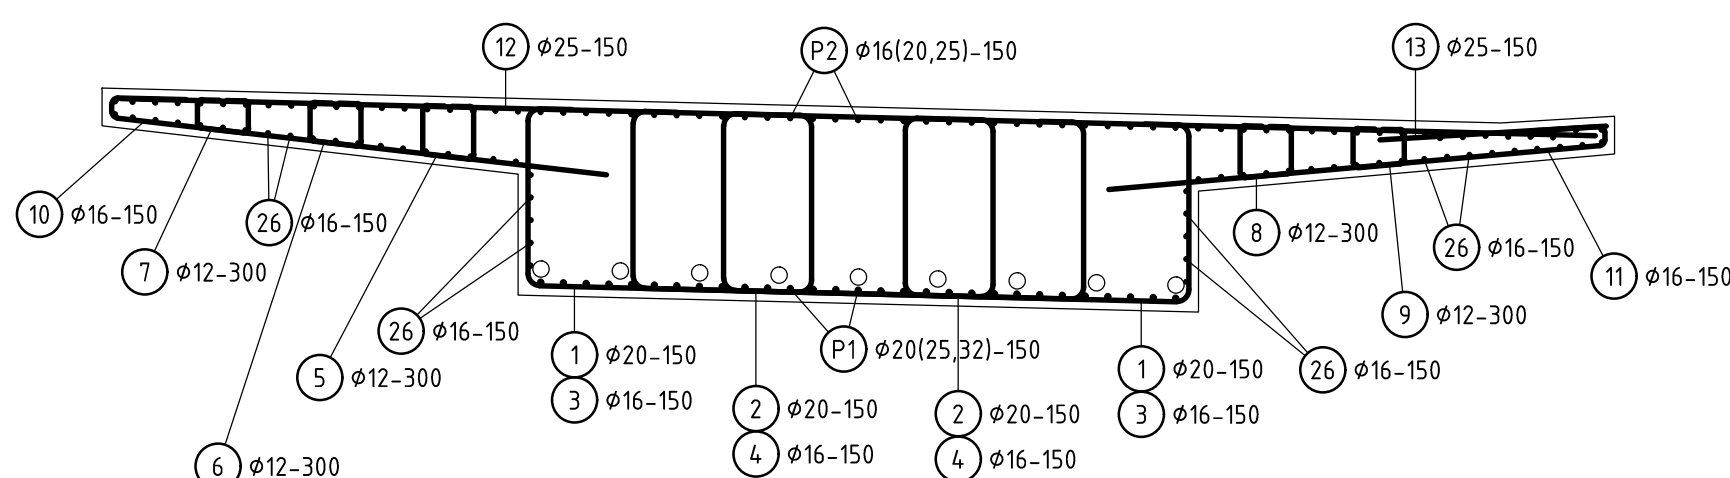

SESTAVA S1

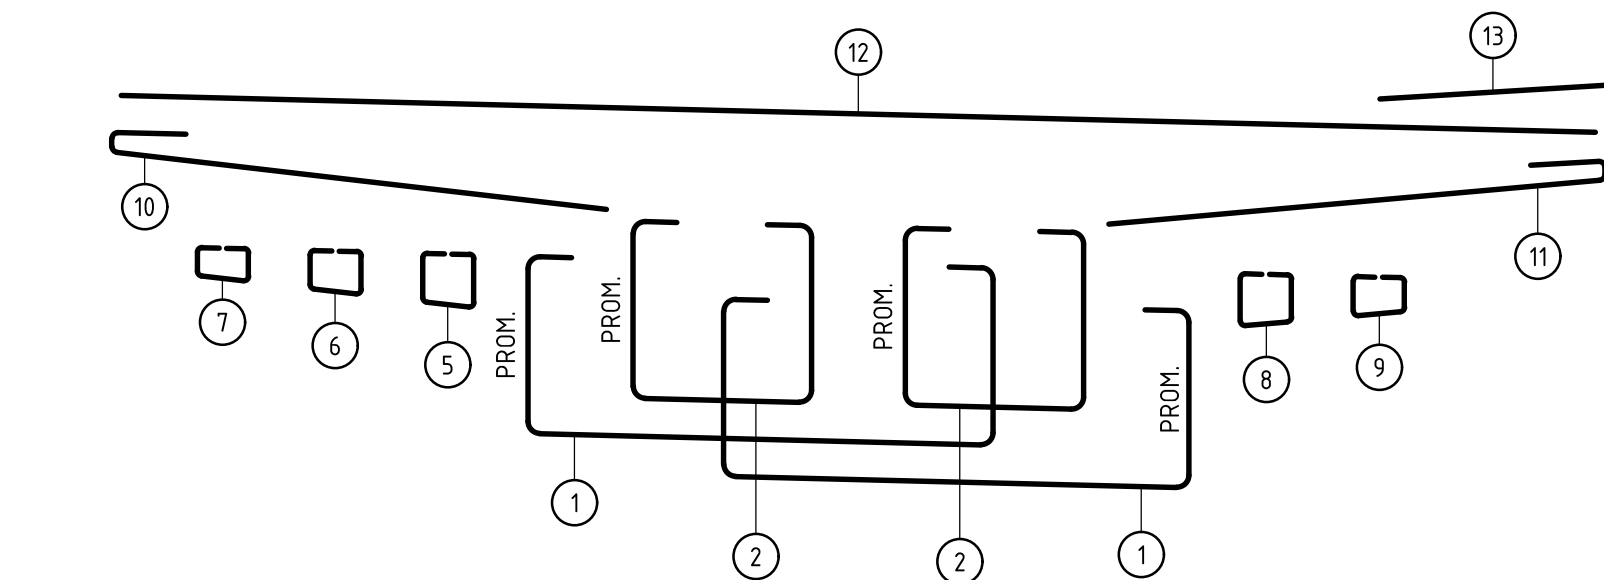

SESTAVA S2

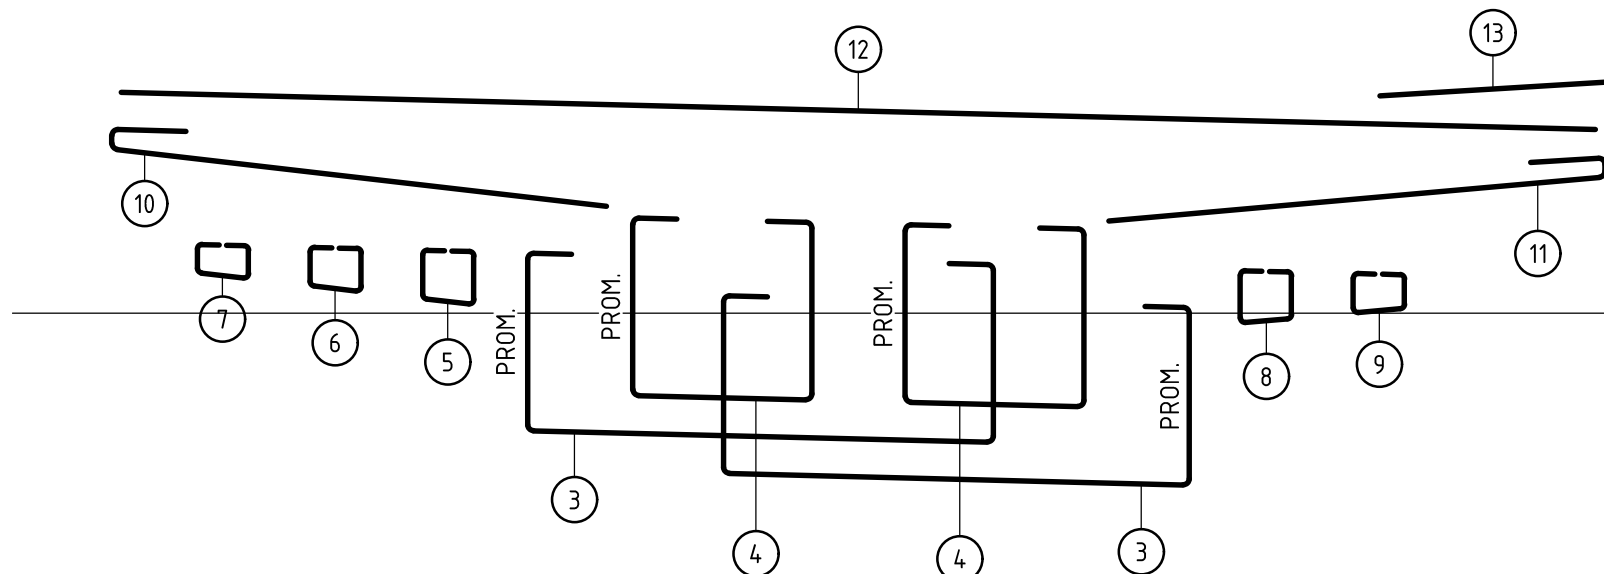


SCHÉMA VÝZTUŽE PODPĚRY P2 1:75

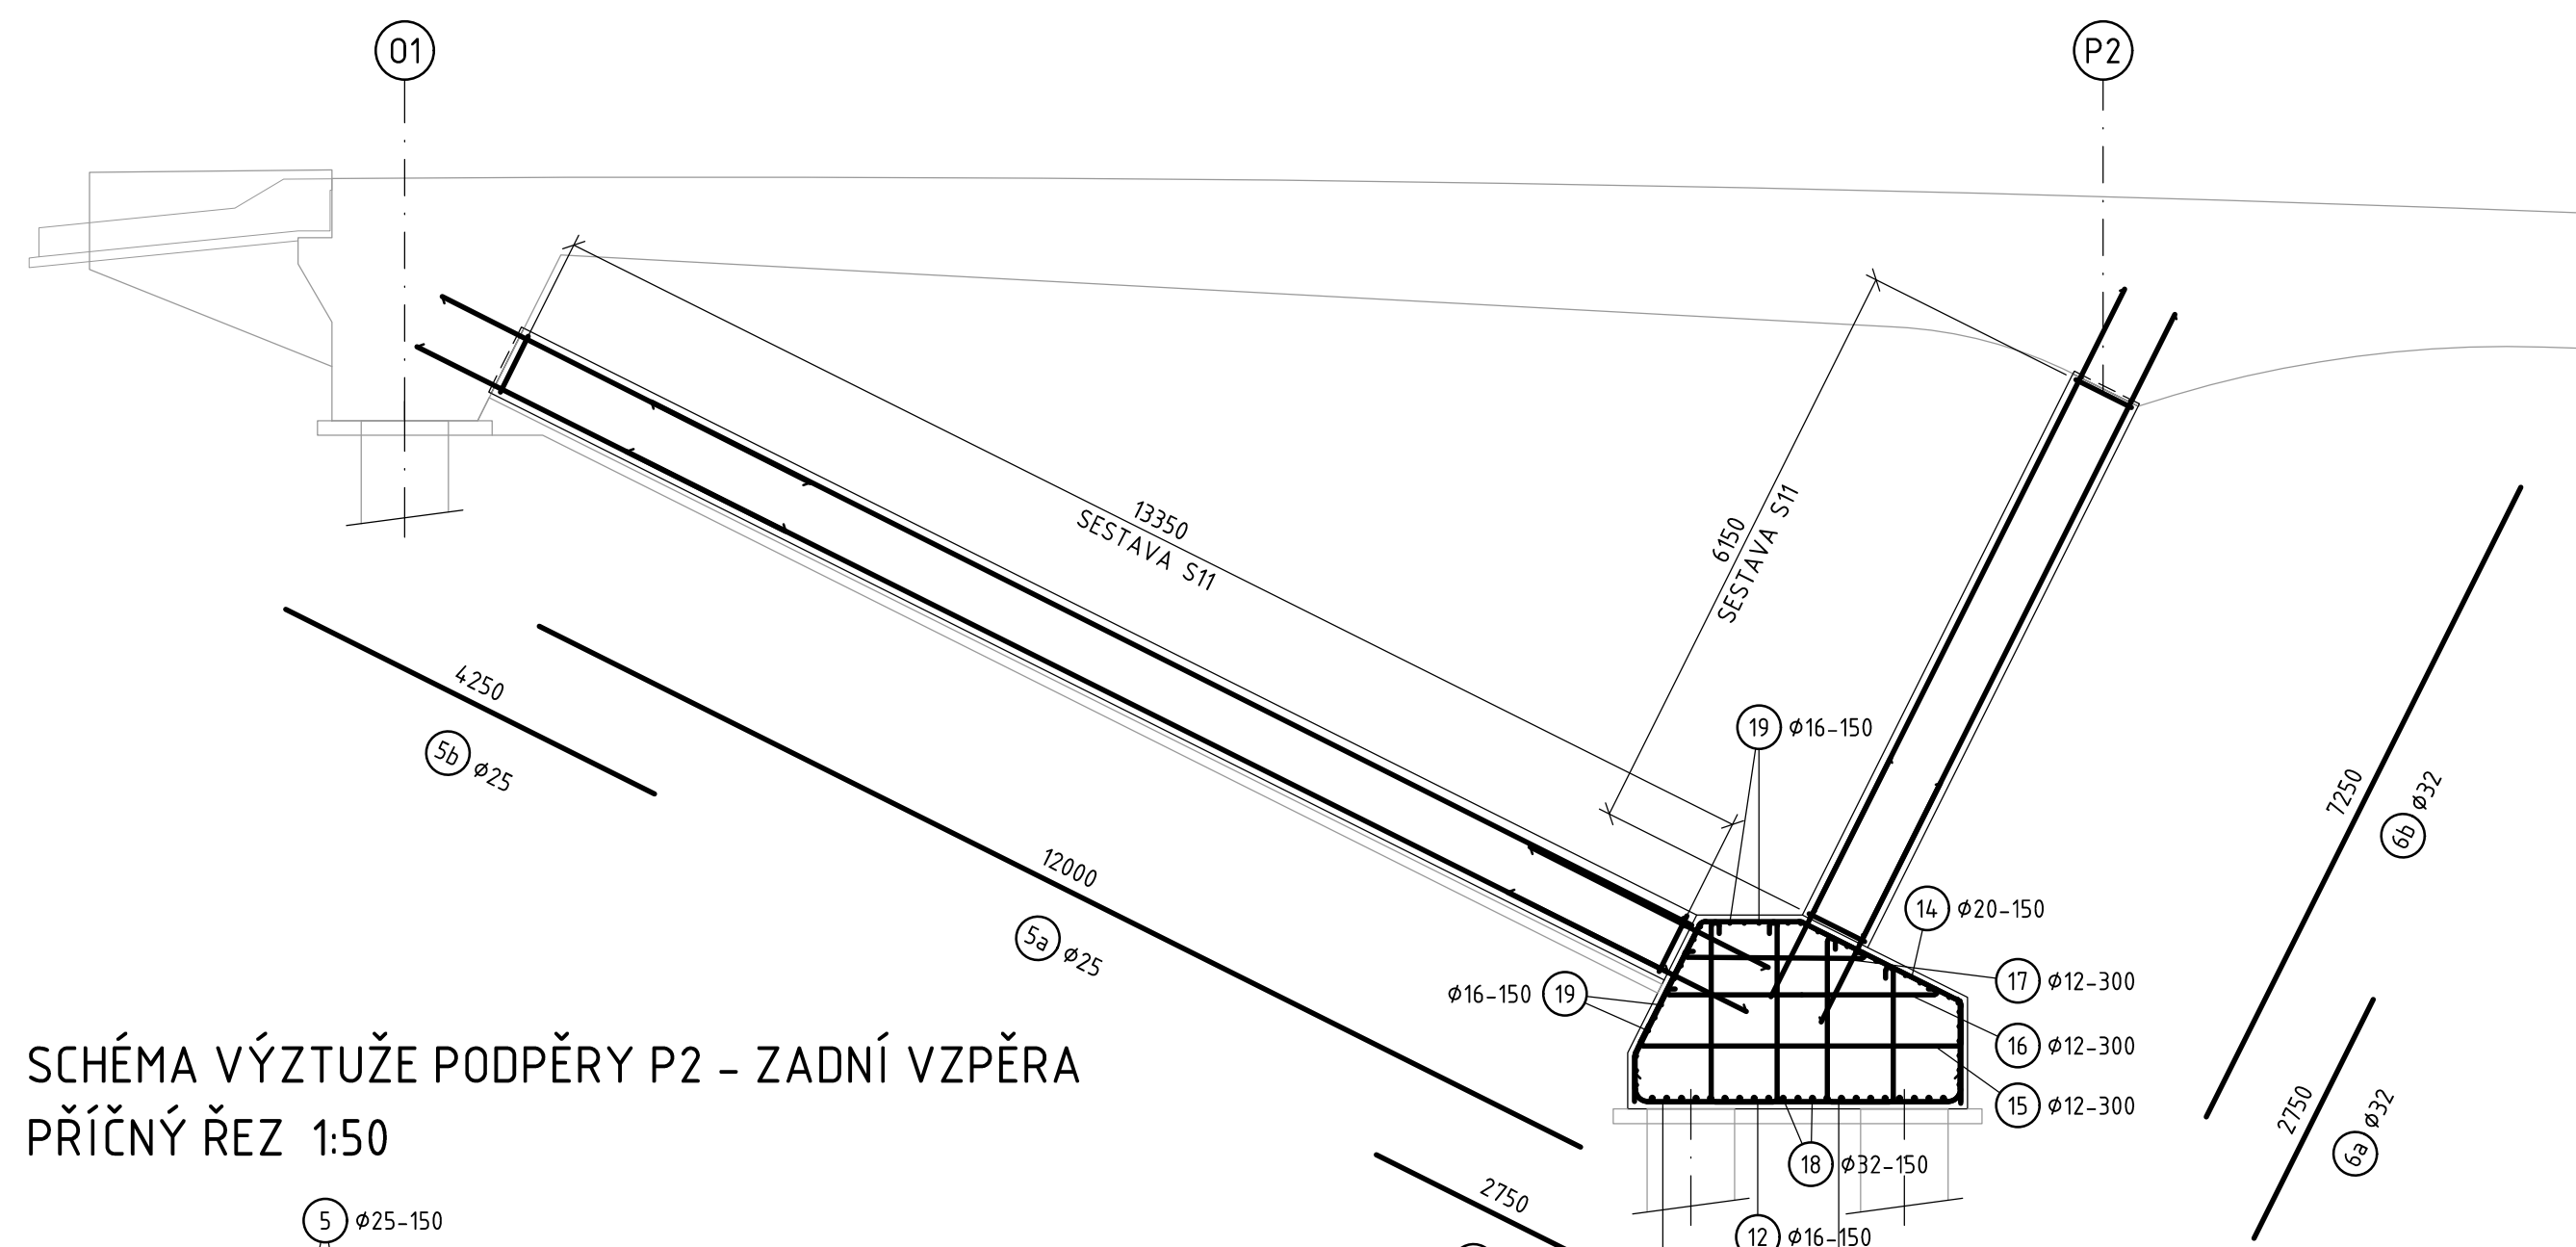


SCHÉMA VÝZTUŽE PODPĚRY P2 - ZADNÍ VZPĚRA
PŘÍČNÝ ŘEZ 1:50



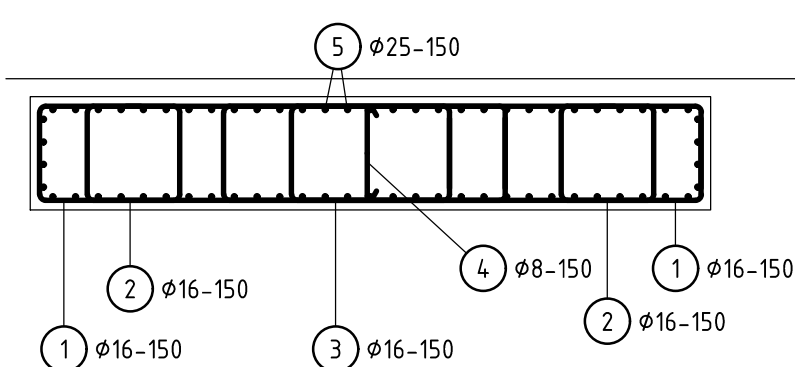


SCHÉMA VÝZTUŽE PODPĚRY P2 - PŘEDNÍ VZPĚRA
PŘÍČNÝ ŘEZ 1:50

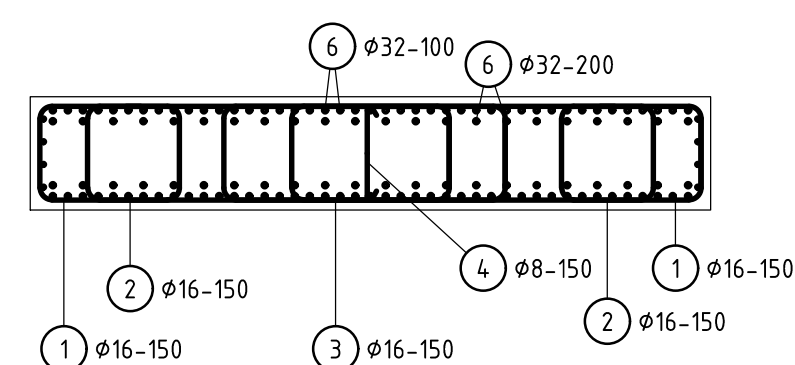


SESTAVA S11

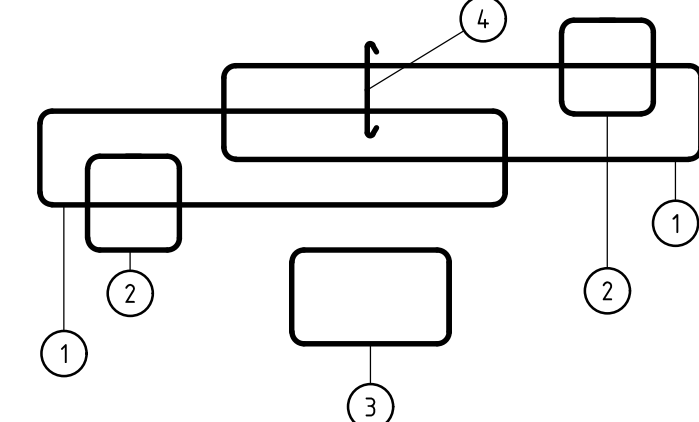

ODHAD MNOŽSTVÍ BETONÁŘSKÉ VÝTUŽE SO 222	MNOŽSTVÍ VÝTUŽE V %	MNOŽSTVÍ VÝT. V KG/M
VÝTUŽ PILOT, D 900MM	1.55%	121.7
VÝTUŽ ZÁKLADU PODPĚRY P2	1.35%	106.0
VÝTUŽ VZPĚR	3.65%	286.5
VÝTUŽ DŘÍKU A KŘÍDEL OPĚRY O3	1.35%	106.0
VÝTUŽ NOSNÉ KONSTRUKCE	1.75%	137.4
VÝTUŽ ŘÍMS	1.80%	141.3
VÝTUŽ PŘECHODOVÝCH DESEK	2.00%	157.0

SCHÉMA VÝZTUŽE OPĚRY 03
PŘÍČNÝ ŘEZ 1:50

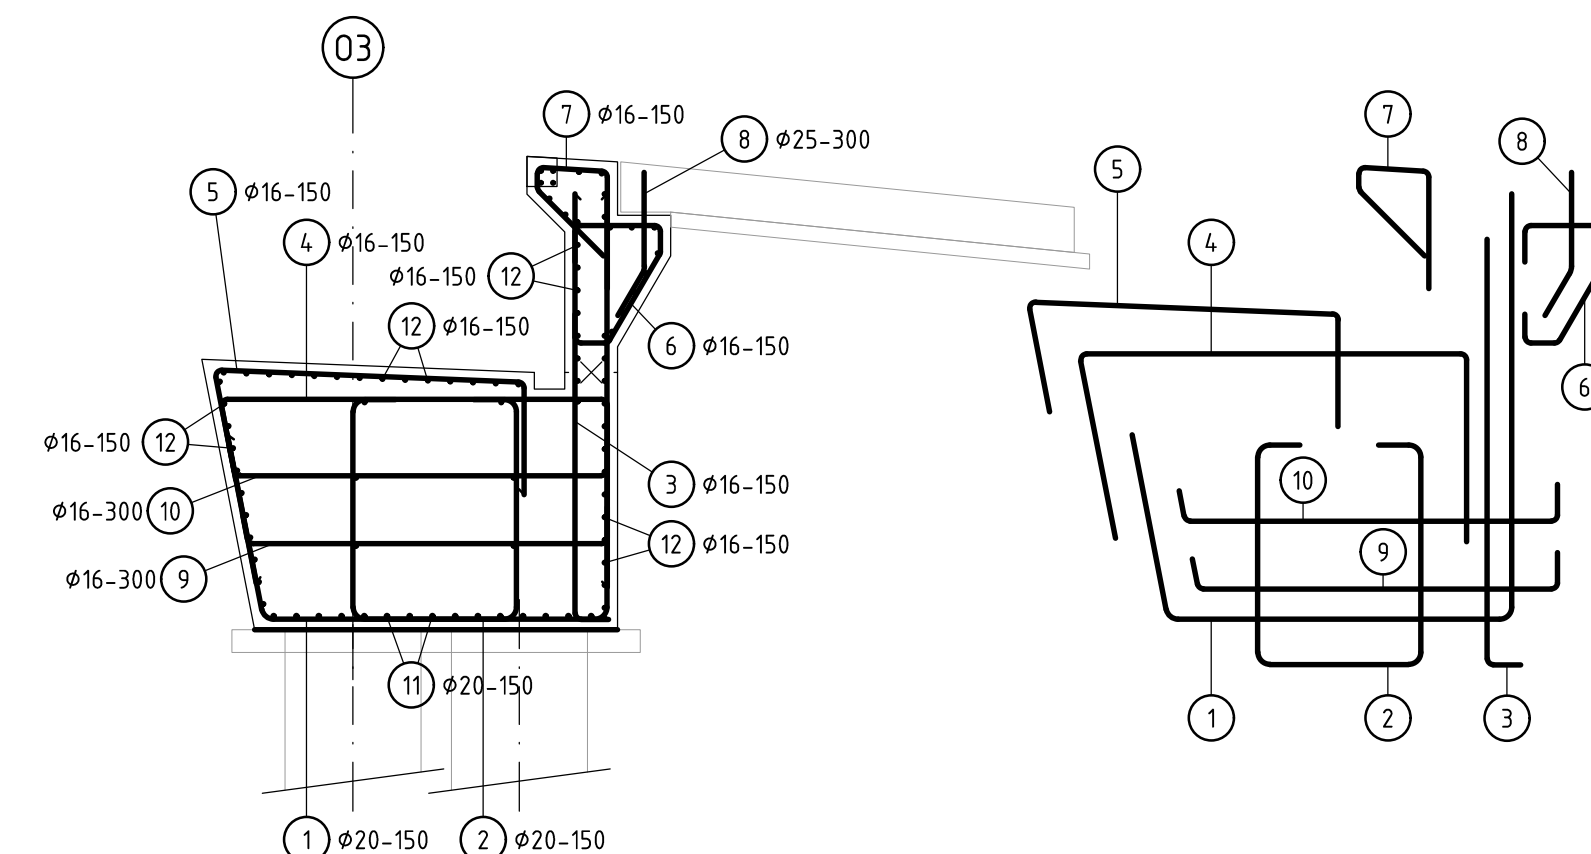

POZNÁMKY:



- NEDÍLNOU SOUČÁSTÍ VÝKRESU JSOU TECHNICKÉ SPECIFIKACE A POZNÁMKY UVEDENÉ NA VÝKRESE
TECHNICKÝCH SPECIFIKACÍ A POZNÁMEK

Souřadnicový systém: S-JTSK
Výškový systém: Bpv

SO 222	NADJEZD NA MÚK ŽIDNĚVES V KM 4,705
---------------	------------------------------------

Objednatel:  ŘEDITELSTVÍ SILNIC A DÁLNIC	Ředitelství silnic a dálnic s. p. Čertánská 2023/12, Krč, 140 00 Praha 4
--	---

	Valbek, spol. s r.o. Vaňurova 505/17 460 07 Liberec 3
---	---

  	Vypracoval	ING. O. ŠABATA	  	Zak. číslo	21-L113-001
	Zodp. projektant	ING. O. ŠABATA		Datum	03/2025
	Tech. kontrola	ING. I. BELDA		Stupeň	PDPS
	Akce	I/16 MLADÁ BOLESLAV - MARTINOVICE		Počet formátů	A4 A4
				Měřítko	-
				Č. přílohy	Paré
Zhotovitel: Valbek, spol. s r.o. Valbuřova 502/17 460 07, Liberec 3	Příloha SCHÉMATICKÉ VÝKRESY VÝZTUŽE	301			