


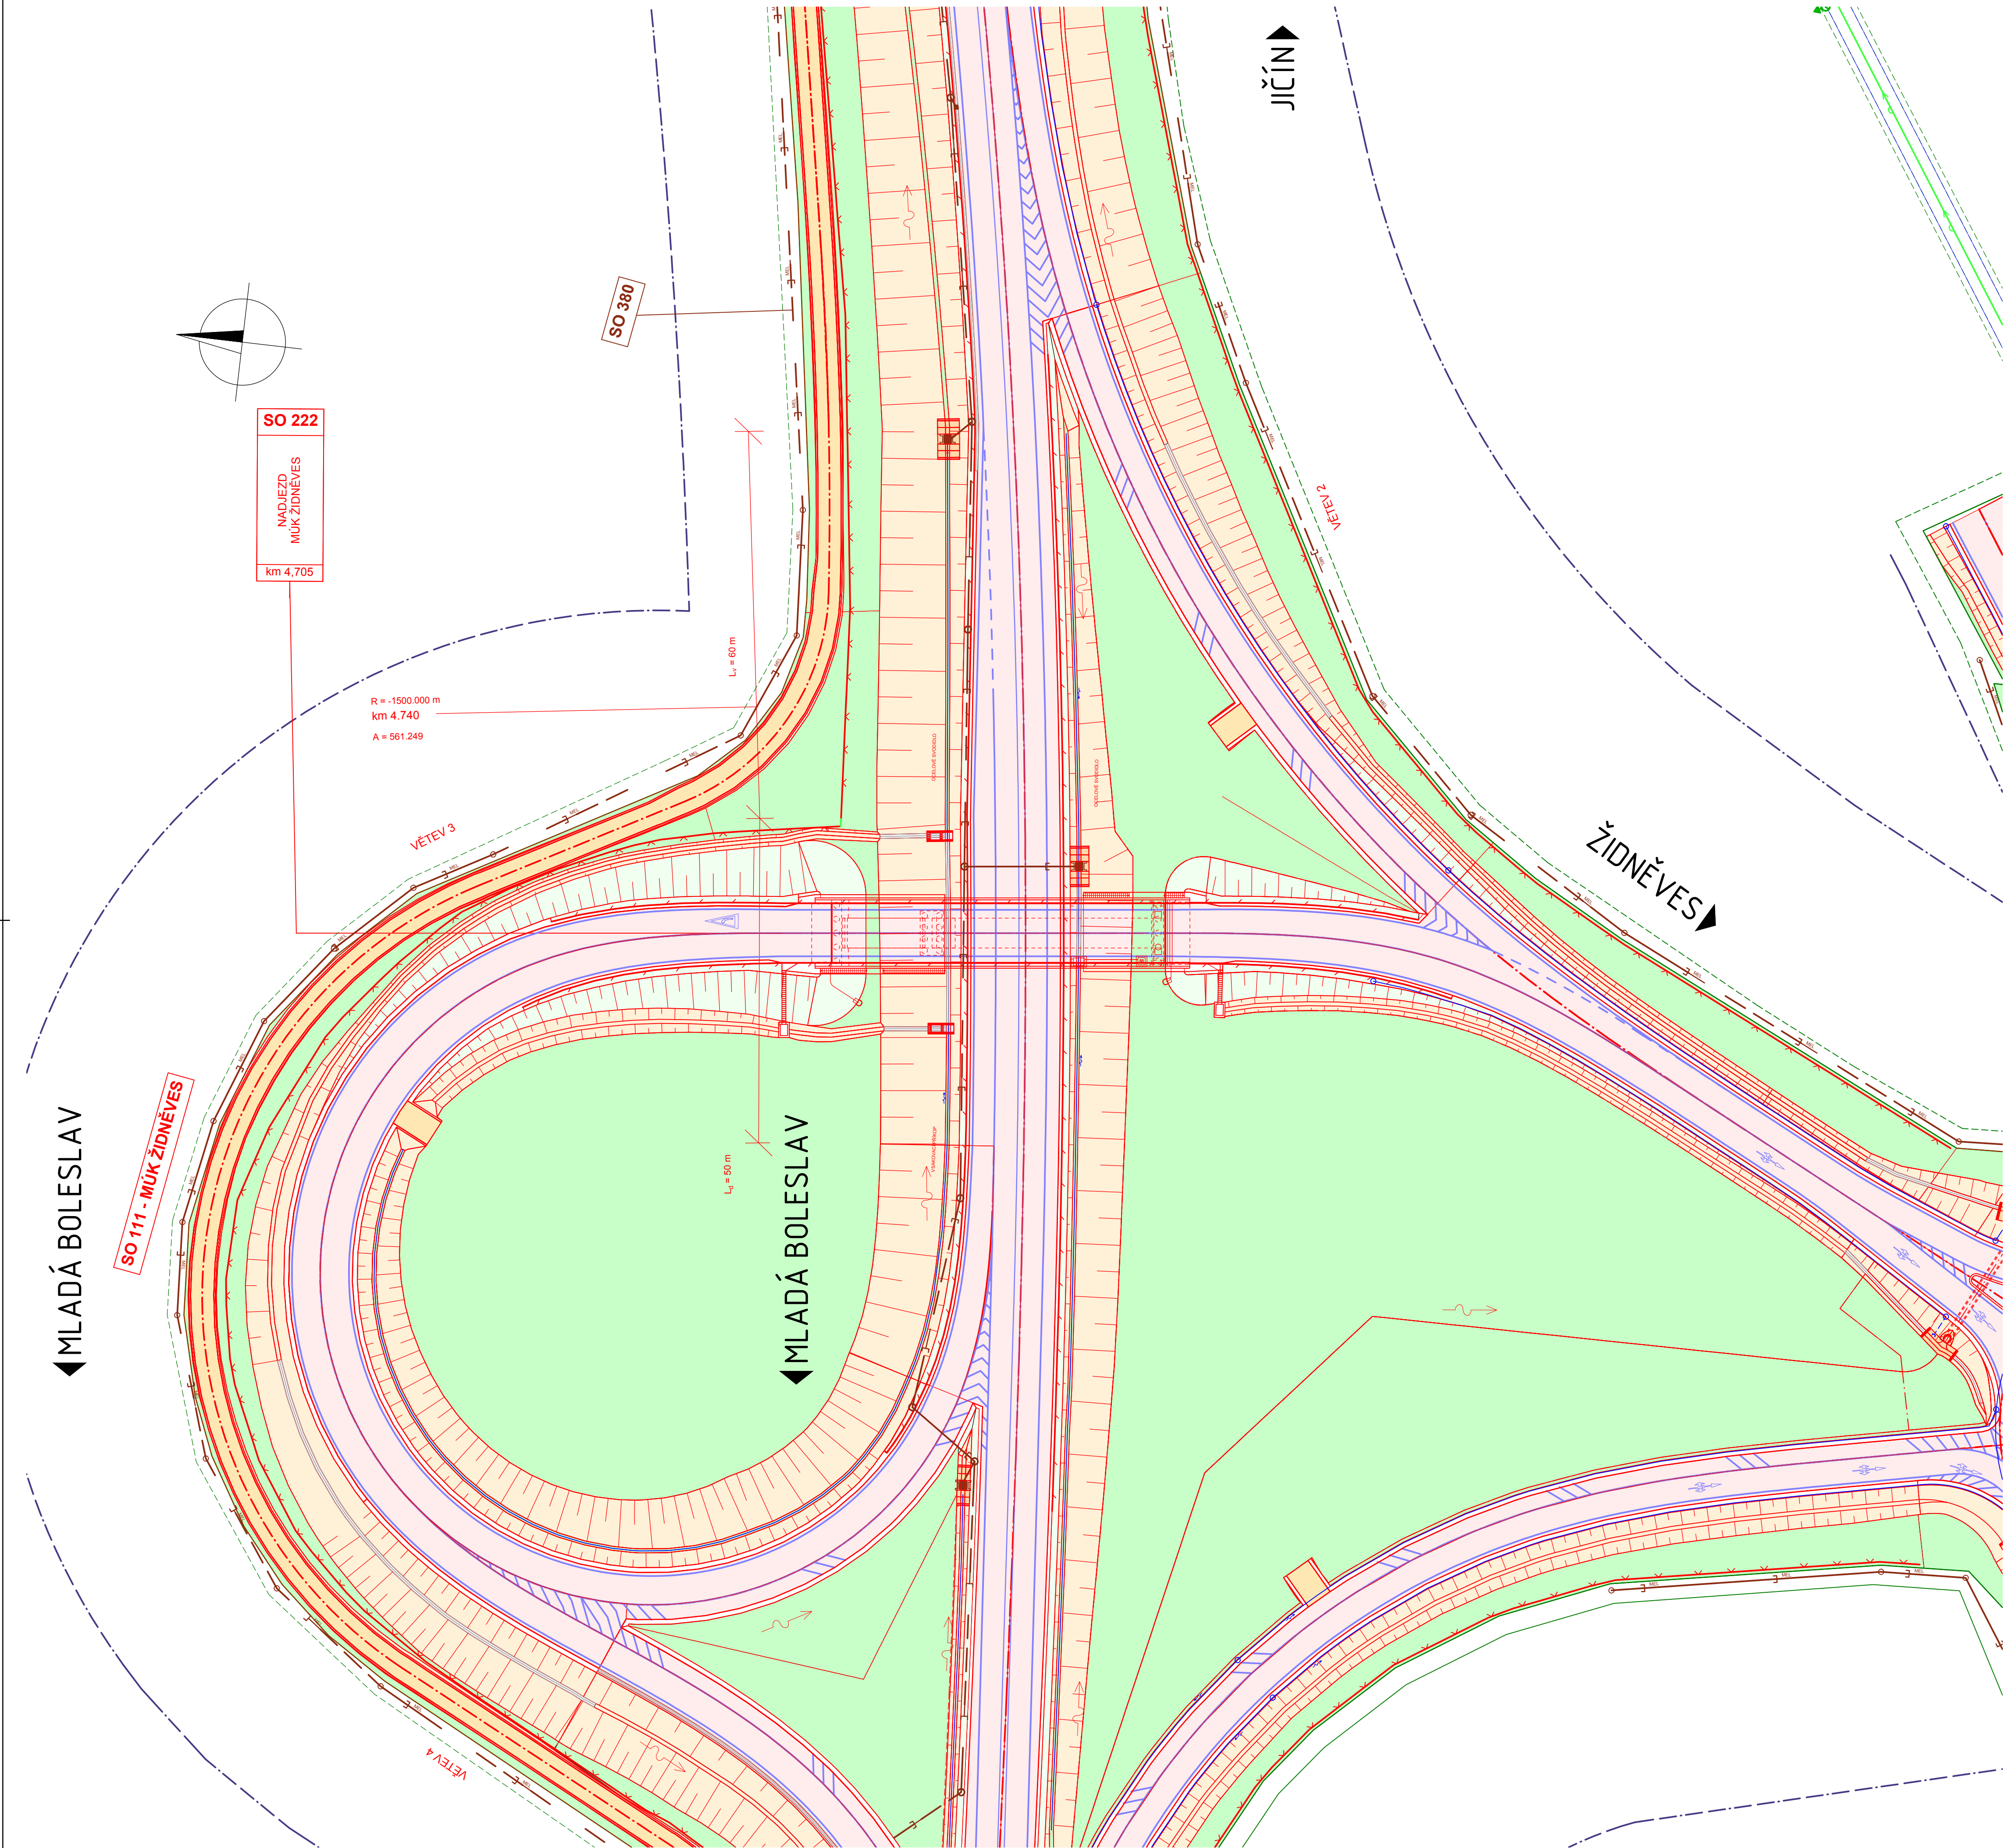

Souřadnicový systém: S-JTSK
Výškový systém: Bpv

SO 222 NADJEZD NA MÚK ŽIDNĚVES V KM 4,705

Objednatel:



Ředitelství silnic a dálnic s. p.
Čerčanská 2023/12, Krč, 140 00 Praha 4



Valbek, spol. s r.o.
Vaňurova 505/17
460 07 Liberec 3



Vypracoval	ING. O. ŠABATA	<i>O. Šabata</i>	Zak. číslo	21-L113-001
Zodp. projektant	ING. O. ŠABATA	<i>O. Šabata</i>	Datum	02/2025
Tech. kontrola	ING. I. BELDA	<i>I. Belda</i>	Stupeň	PDPS
Akce	I/16 MLADÁ BOLES LAV - MARTINOVICE		Počet formátů	8x A4
Zhotovitel:	Valbek, spol. s r.o.		Měřítko	1:500
Vaňurova 505/17	Příloha		Č. přílohy	Paré
460 07 Liberec 3	PŘEHLEDNÁ SITUACE		401	