
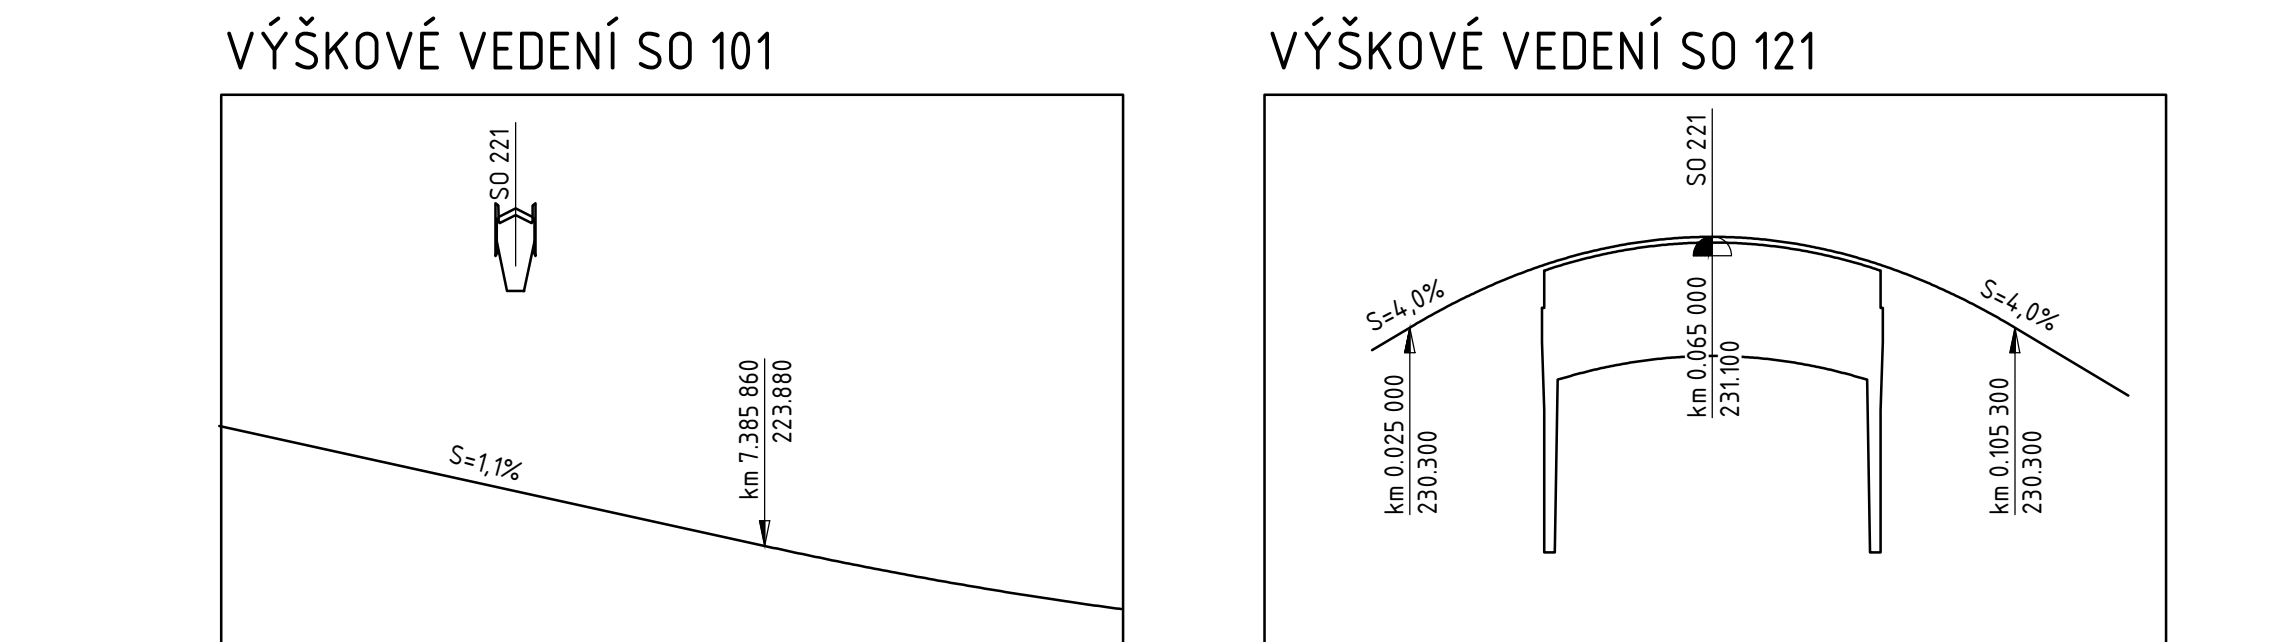


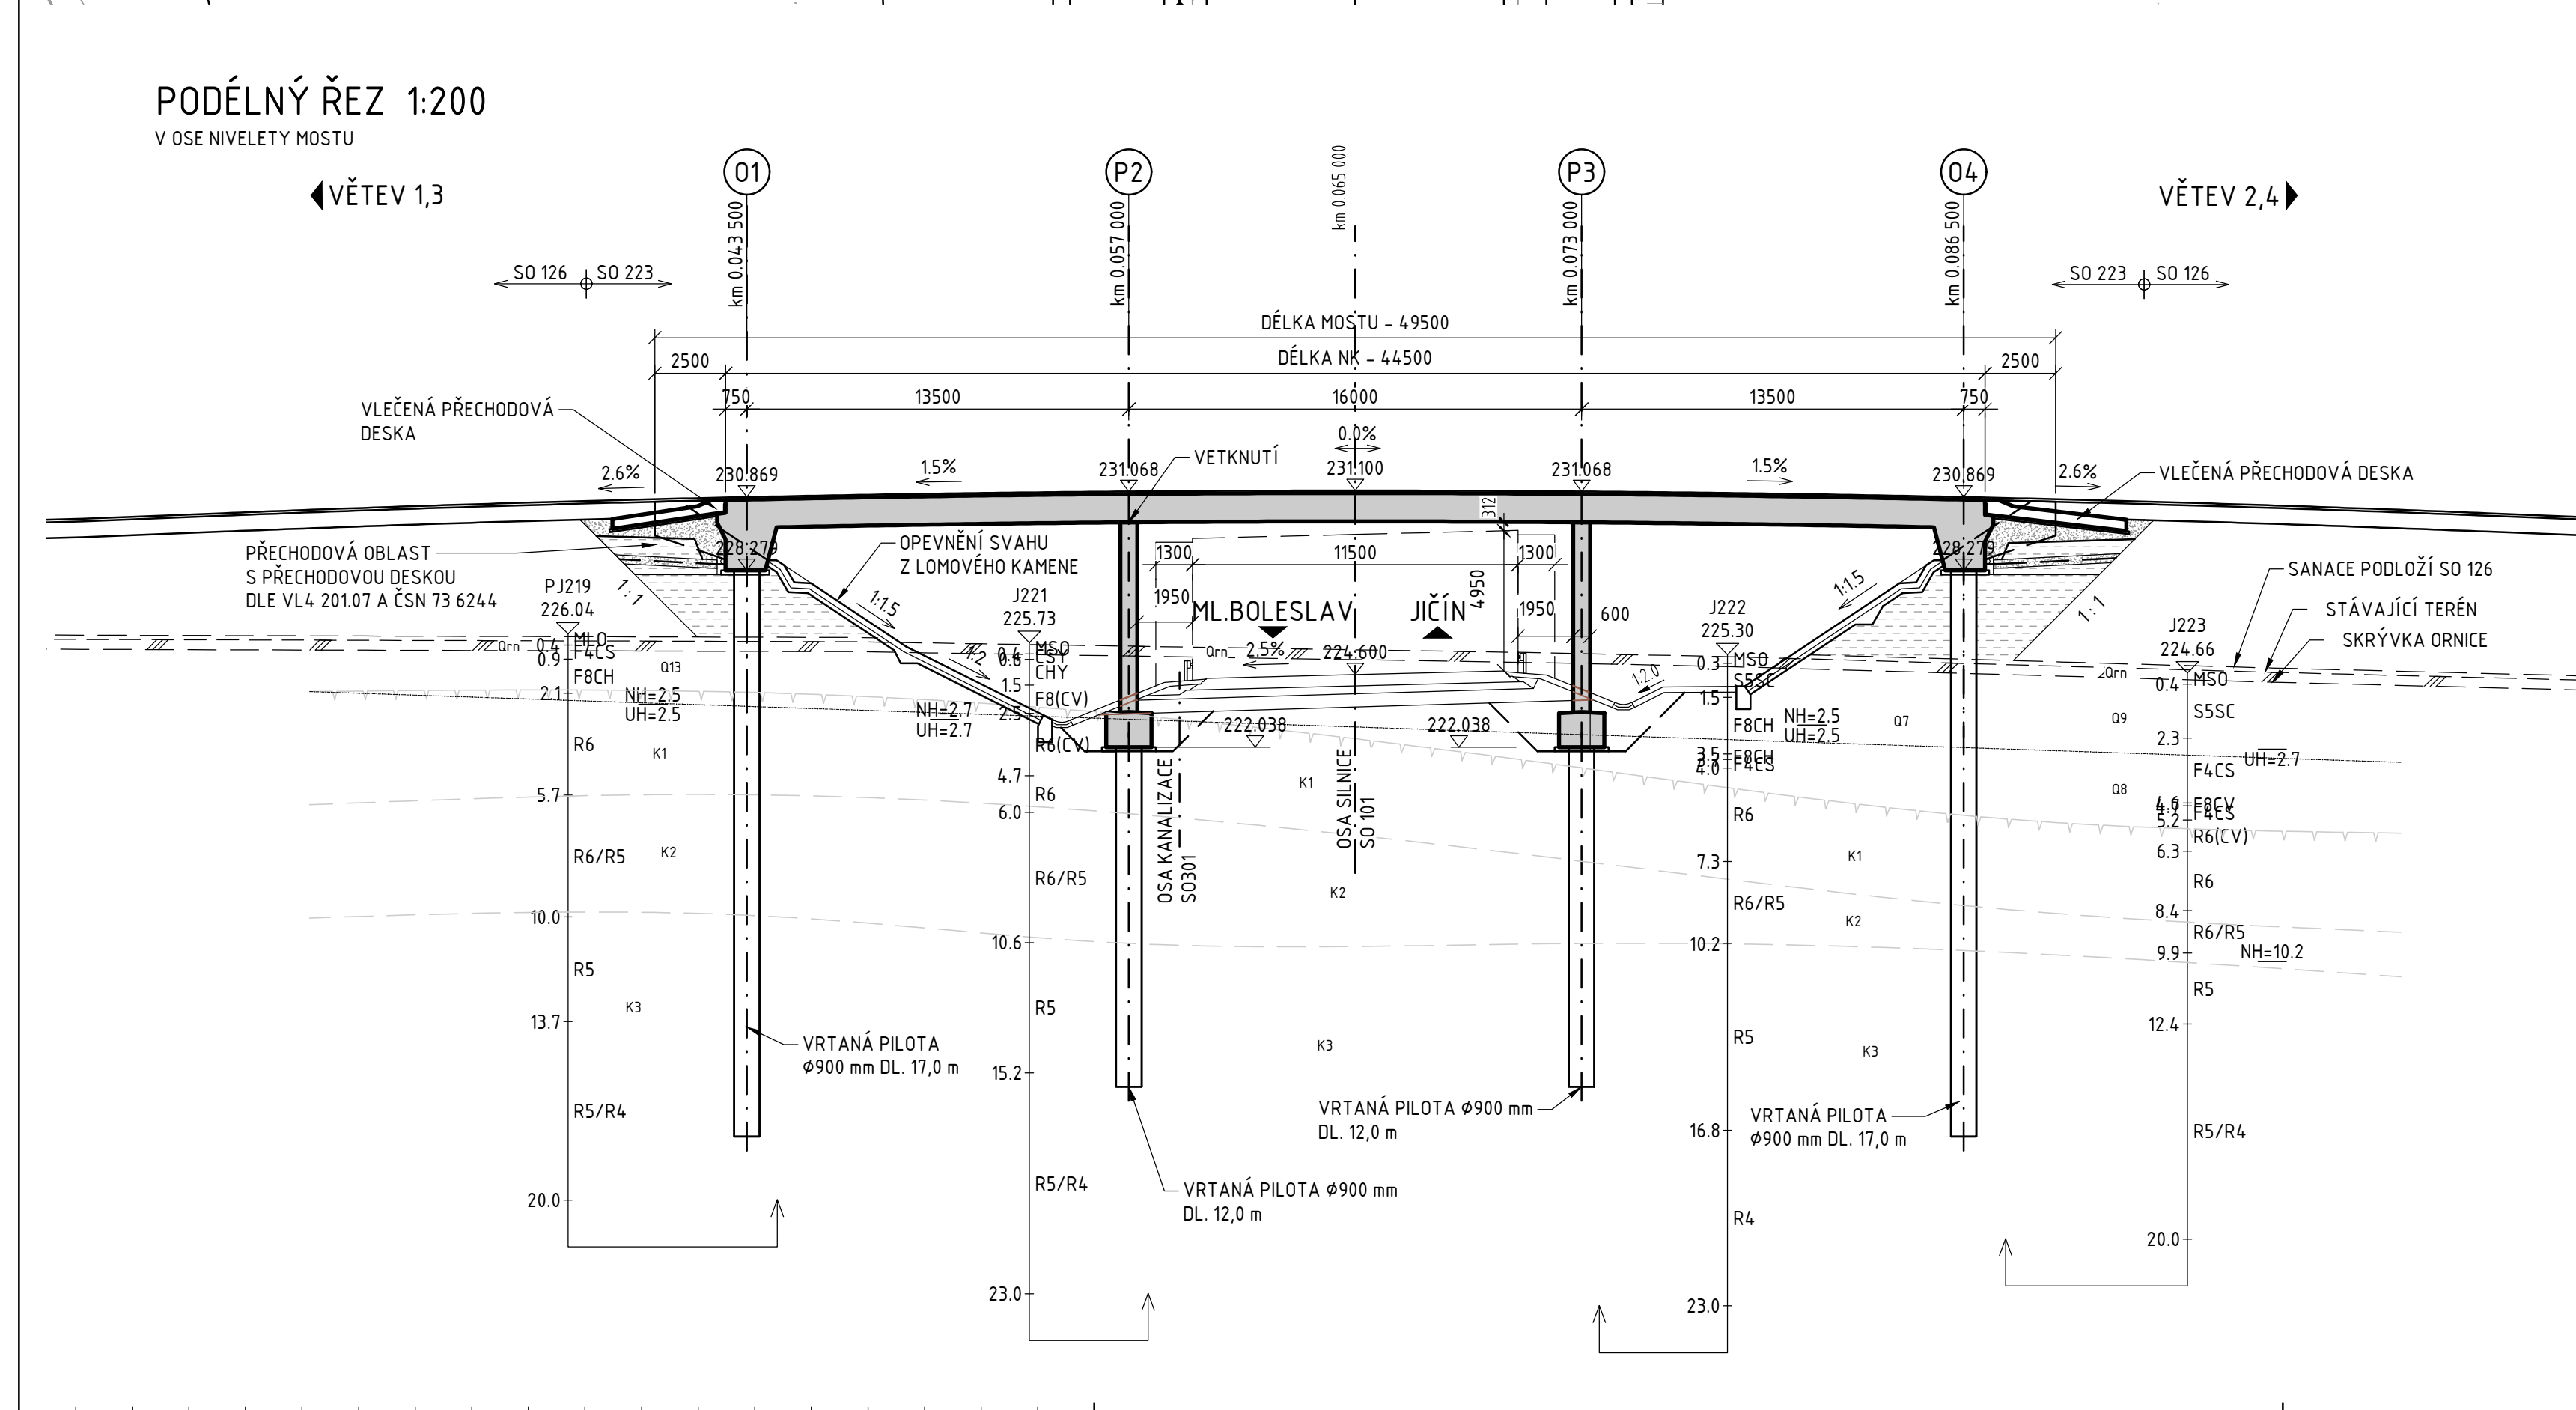

LEGENDA

TRVALÝ ZÁBOR ————

DOČASNÝ ZÁBOR nad 1 rok - - - - -

DOČASNÝ ZÁBOR do 1 roku ————

STANIČNÍ	X	Y	PARAMETR
km 0.020 000	694 224.075	1 010 824.385	PŘÍMÁ
km 0.120 000	694 223.672	1 010 924.384	

MĚŘÍTKO
 1:200

MĚŘÍTKO
 1:75

	Valbek, spol. s r.o. Vaňurova 505/17 460 07 Liberec 3
---	---

	Vypracoval	ING. S. RŮŽIČKA	<i>Růžička</i>	Zak. číslo	21-L113-001	
	Zodp. projektant	ING. S. RŮŽIČKA	<i>Růžička</i>	Datum	02/2025	
	Tech. kontrola	ING. I. BELDA	<i>Belda</i>	Stupeň	PPDS	
	Akce	I/16 MLADÁ BOLESLAV - MARTINOVICE			Počet formátů	8x A4
					Měřitko	1:200,50
				Č. přílohy	Paré	
Zhotovitel: Valbek, spol. s r.o. Vahurova 555/17 460 07 Liberec 3	Příloha	PŮDORYS, PODÉLNÝ ŘEZ VZOROVÝ PŘÍČNÝ ŘEZ			102	