




ŘEZ A-A 1:100
OSA ULOŽENÍ 01

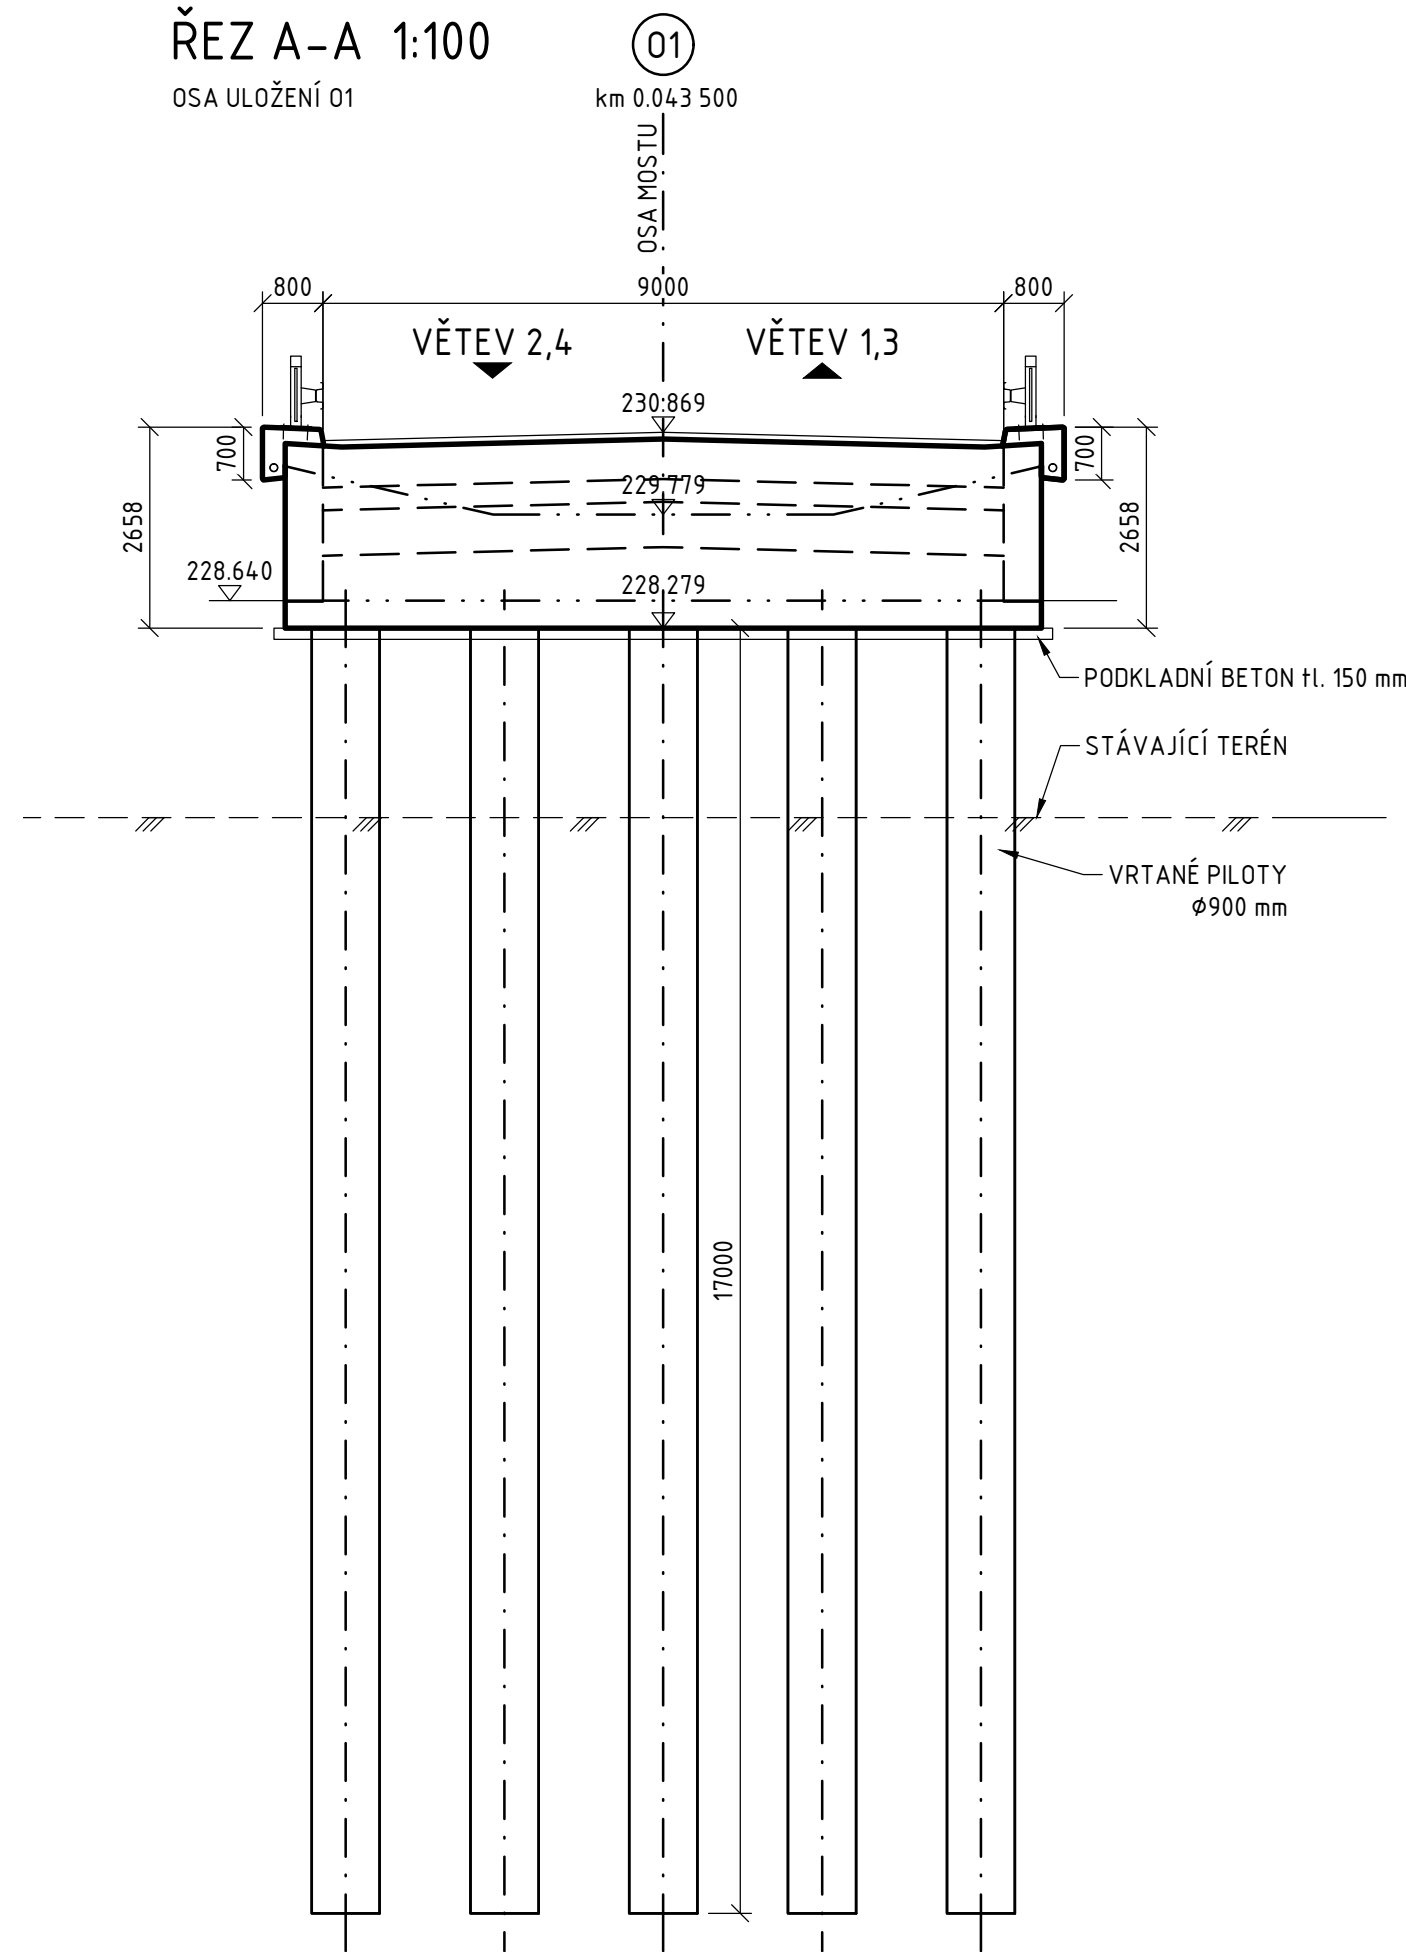

ŘEZ B-B 1:100
OSA ULOŽENÍ P2

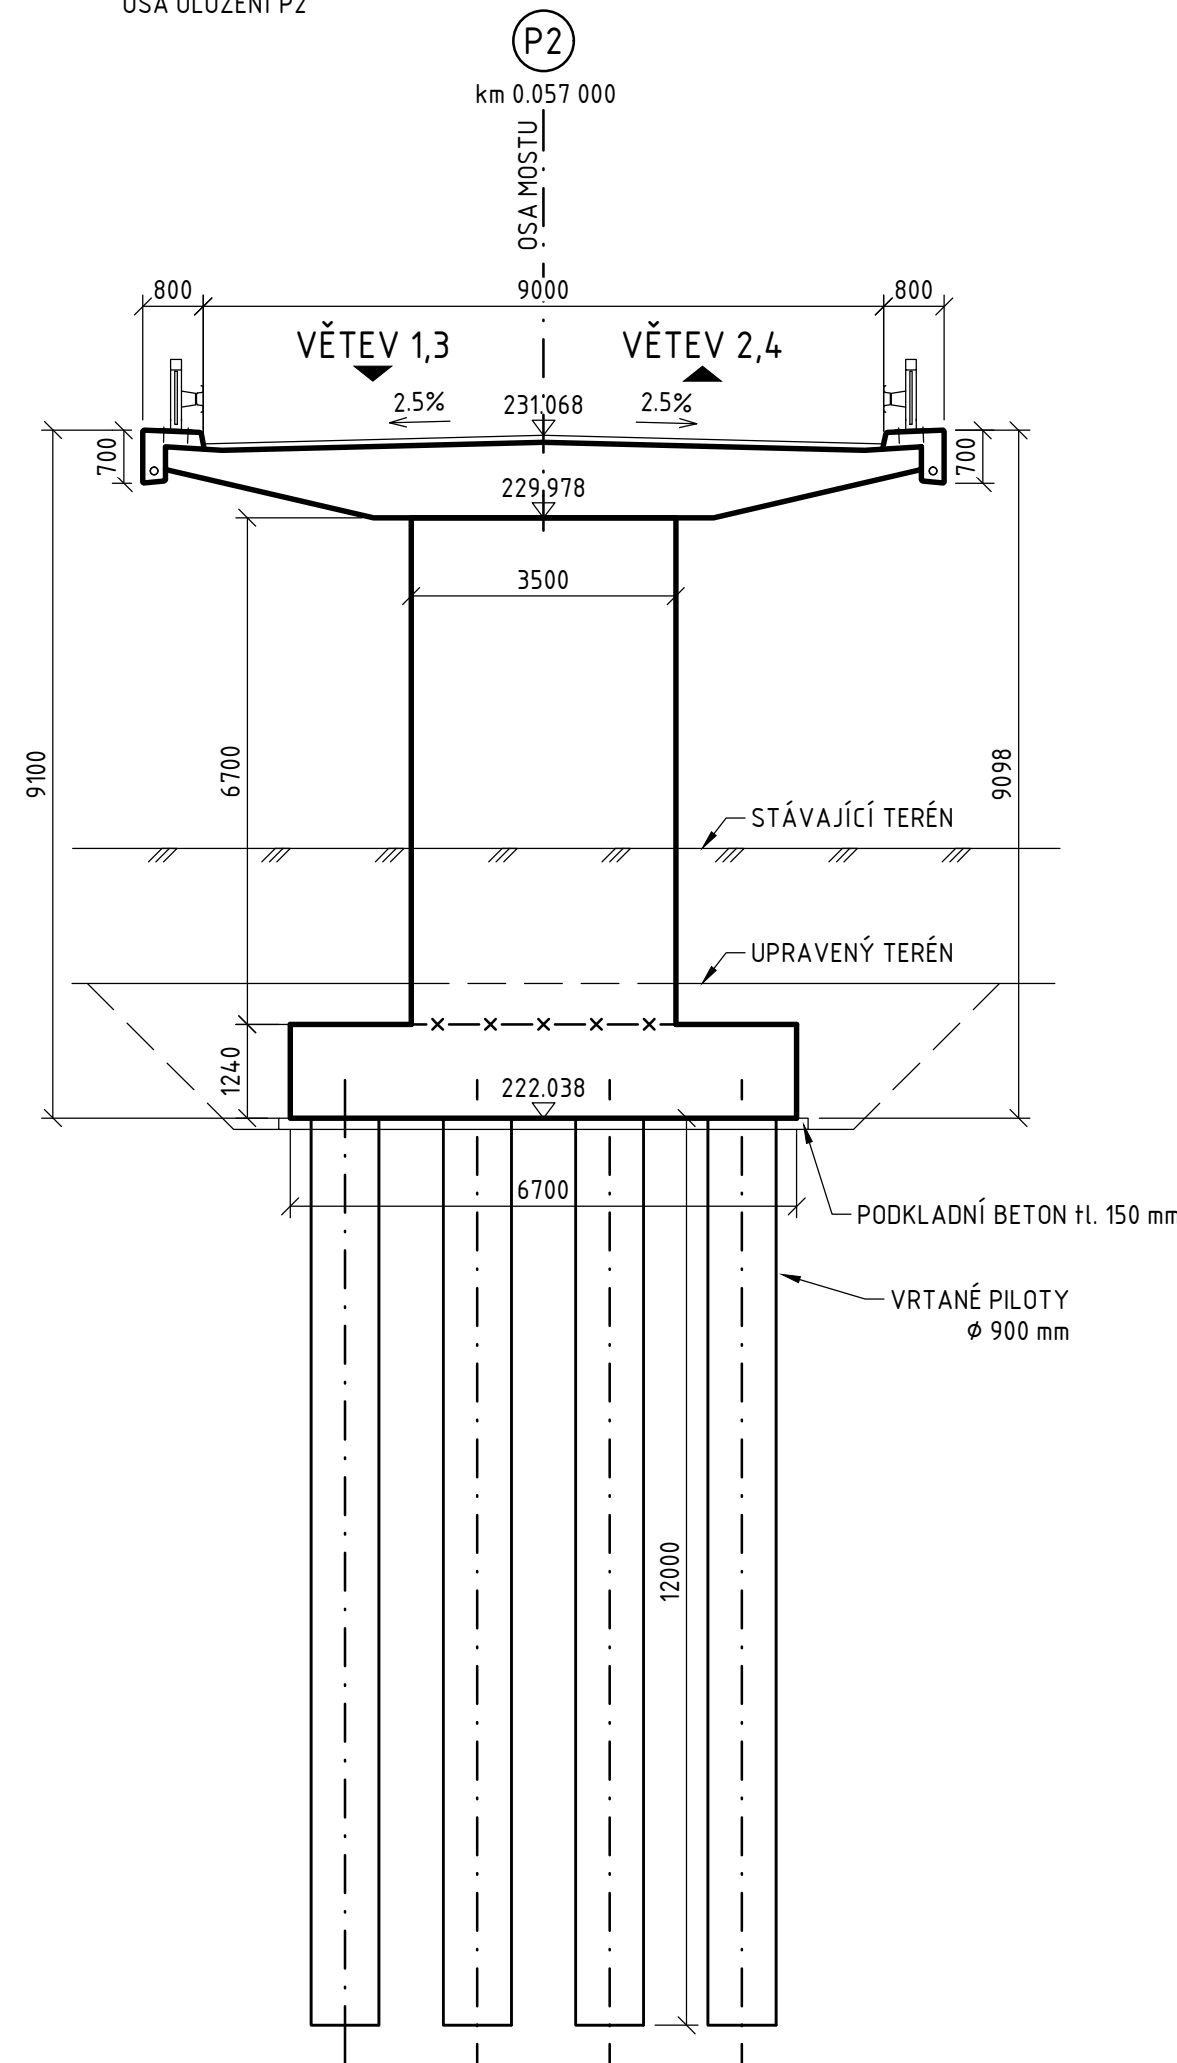


ŘEZ C-C 1:100
OSA ULOŽENÍ P3

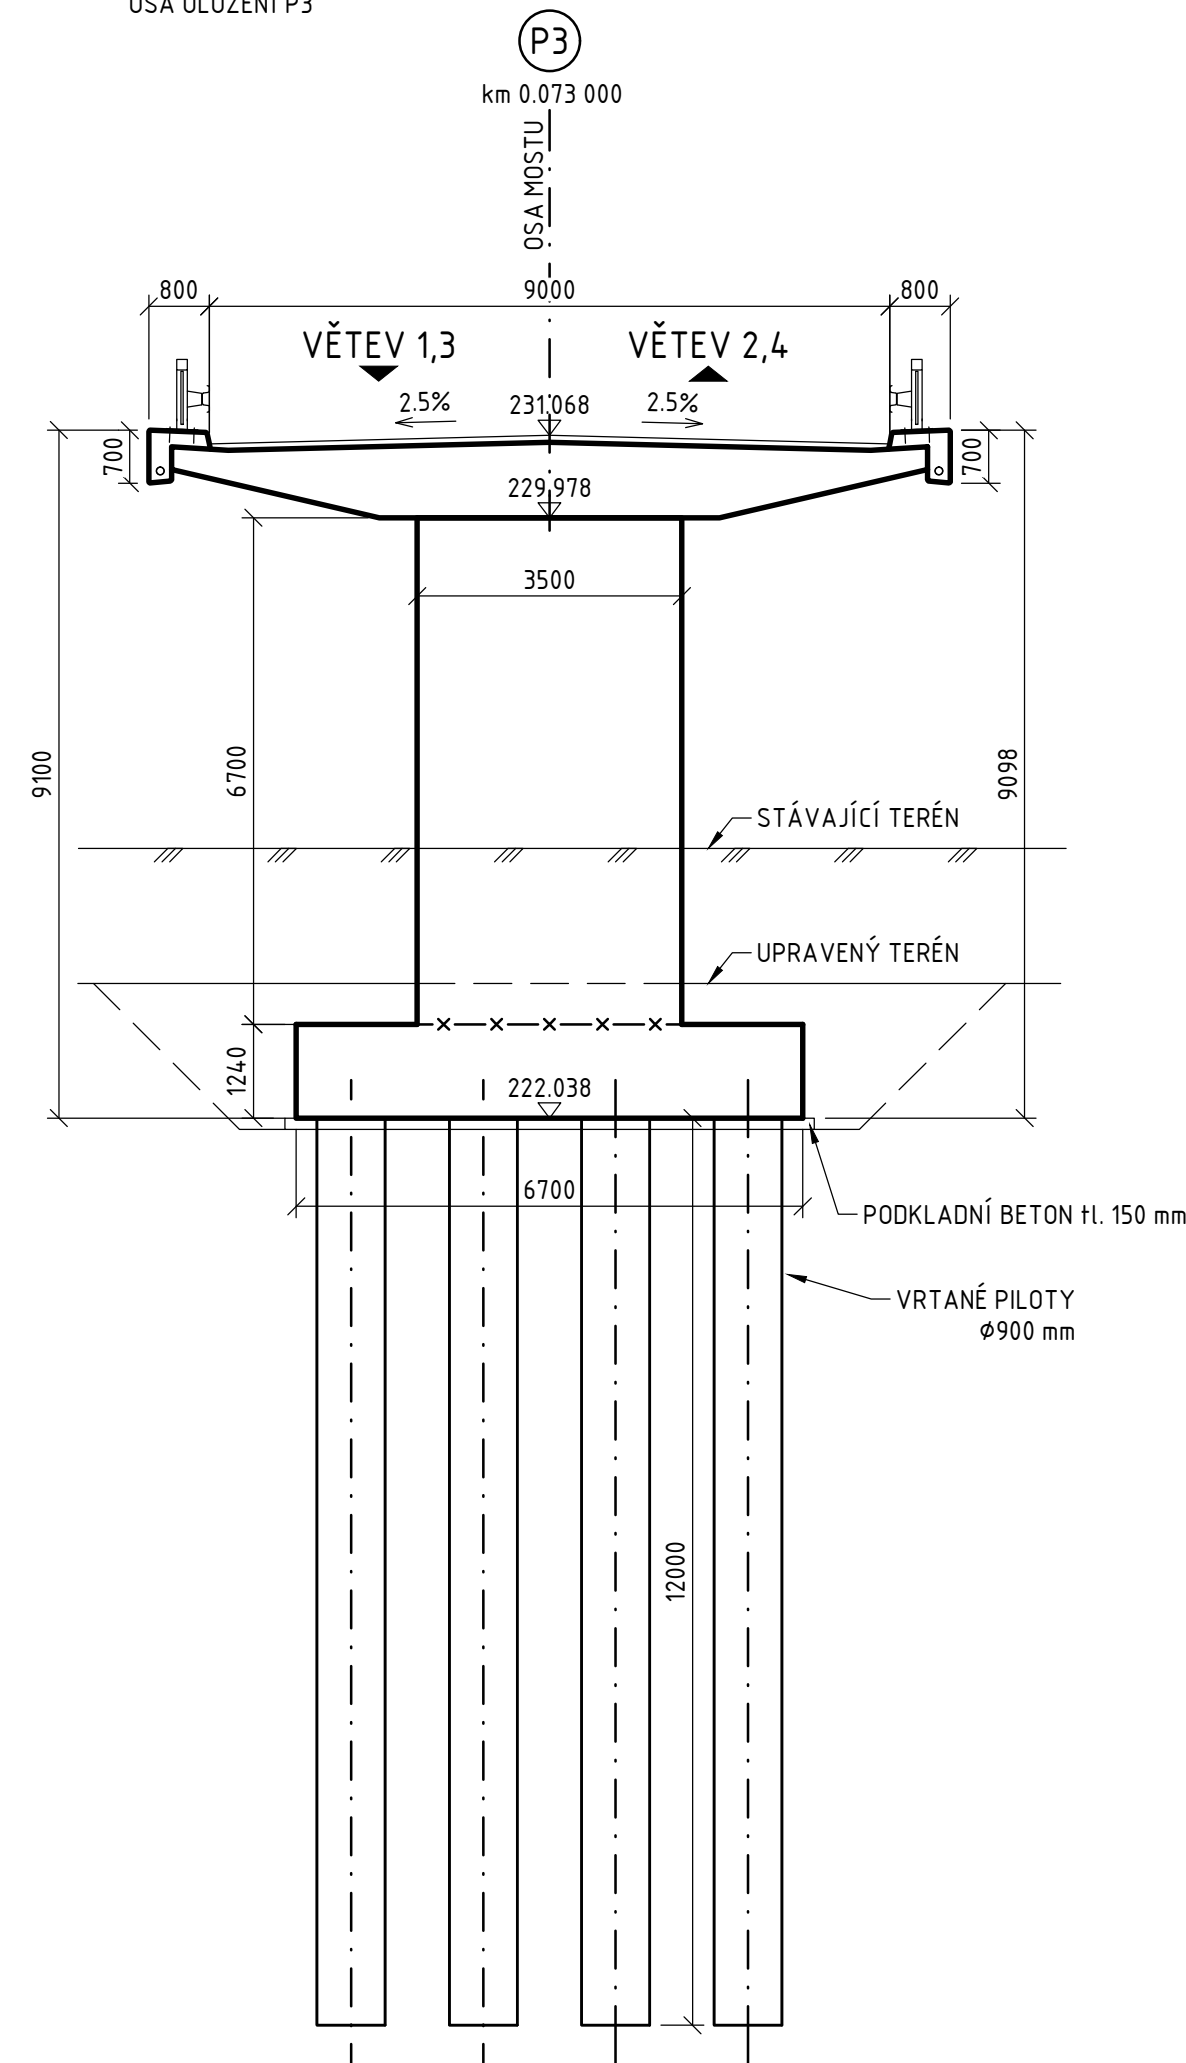


POZNÁMKY:

- NEJÍLNOU SOUČÁSTÍ VÝKRESU JSOU POZNÁMKY A SPECIFIKACE UVEDENÉ NA VÝKRESE POZNÁMEK A TECHNICKÝCH SPECIFIKACÍ

ŘEZ D-D 1:100
OSA ULOŽENÍ 04

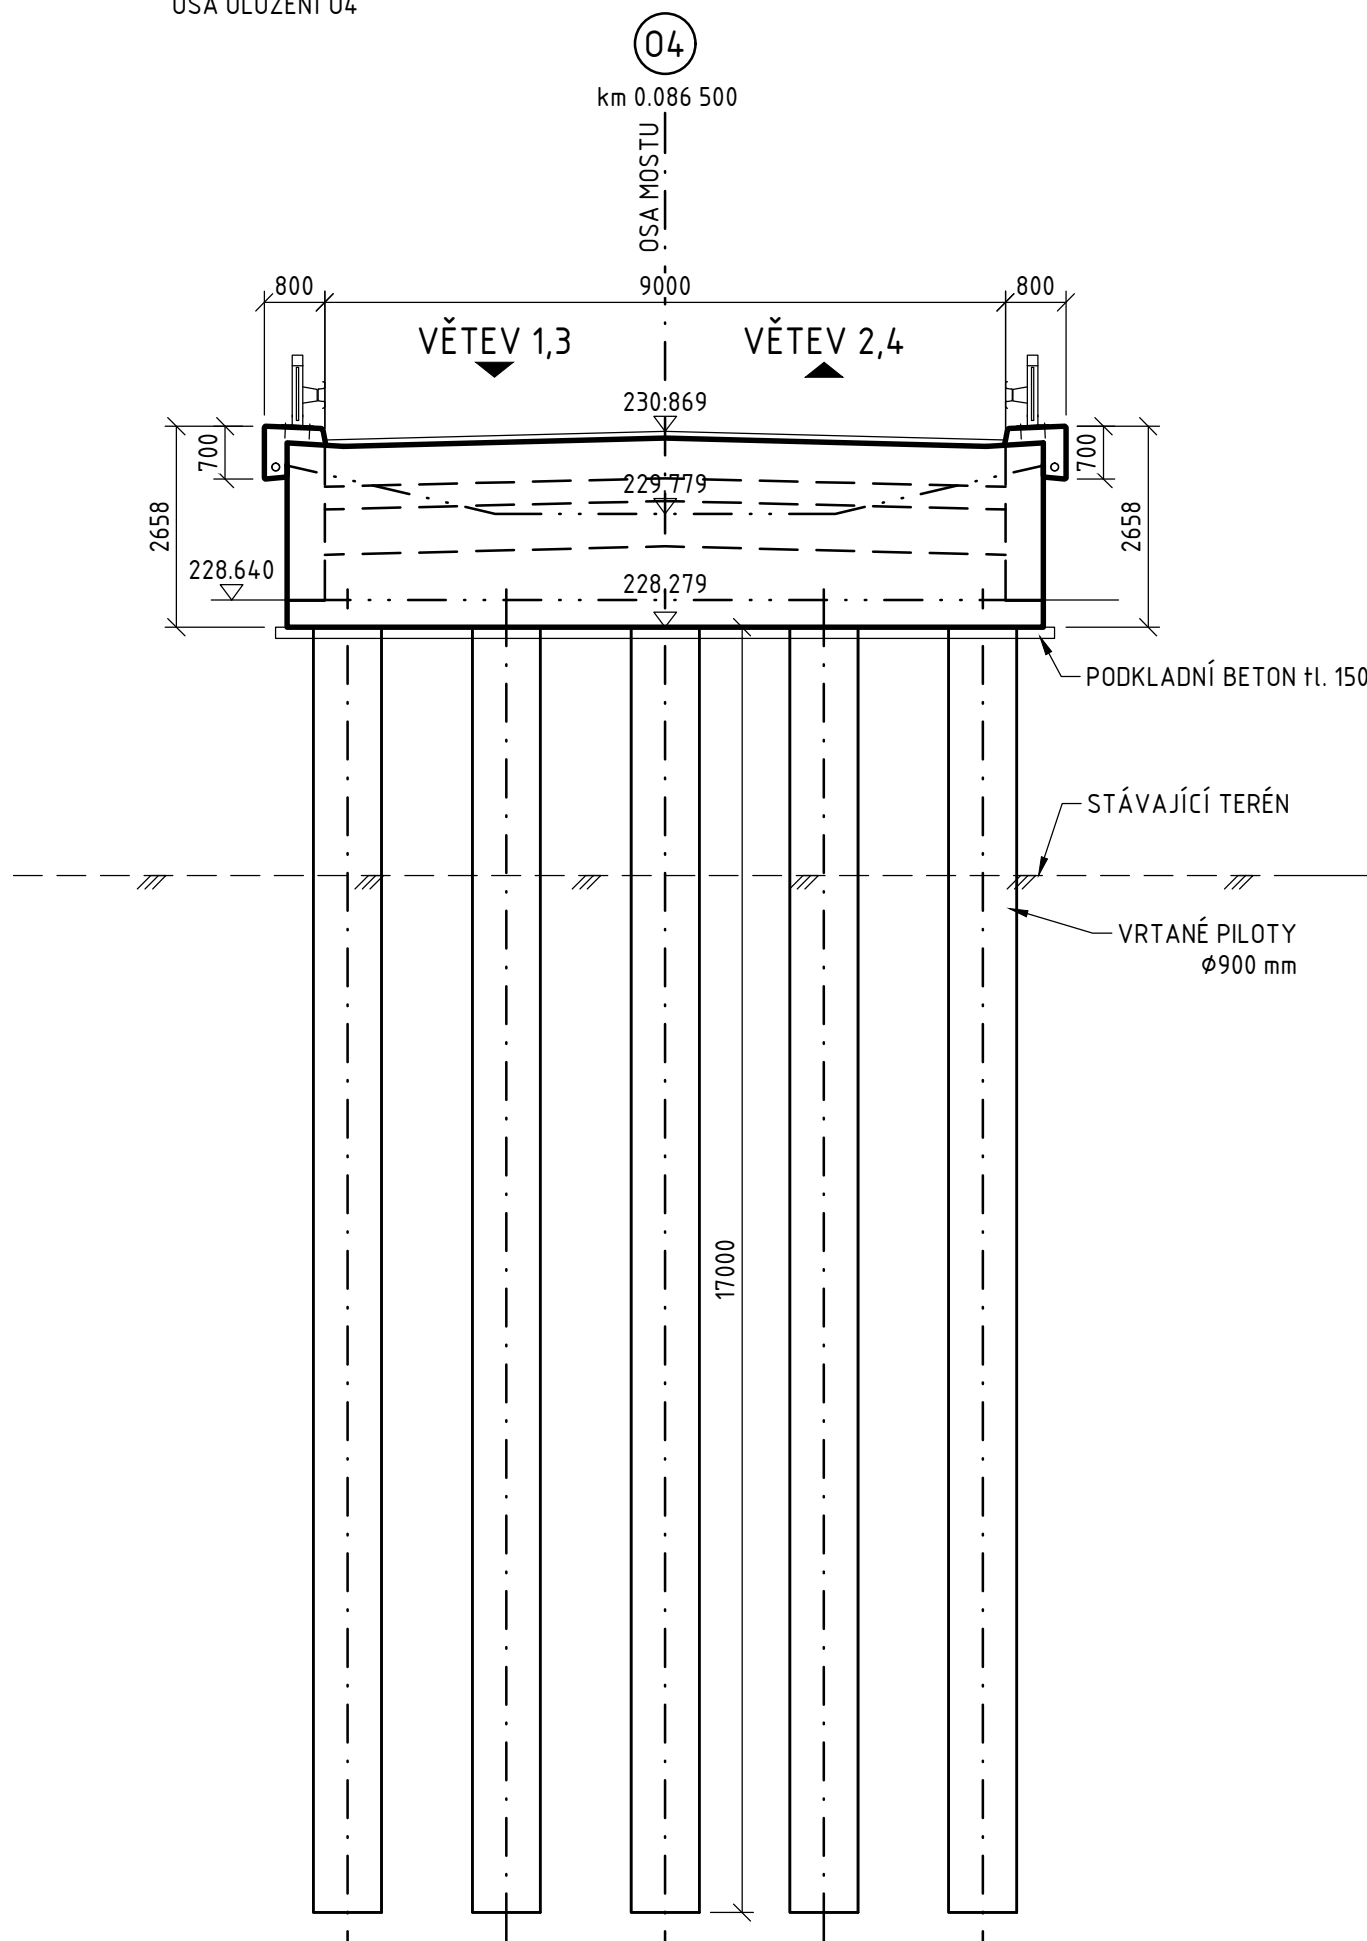

PŮDORYSNÉ SCHÉMA ŘEZŮ

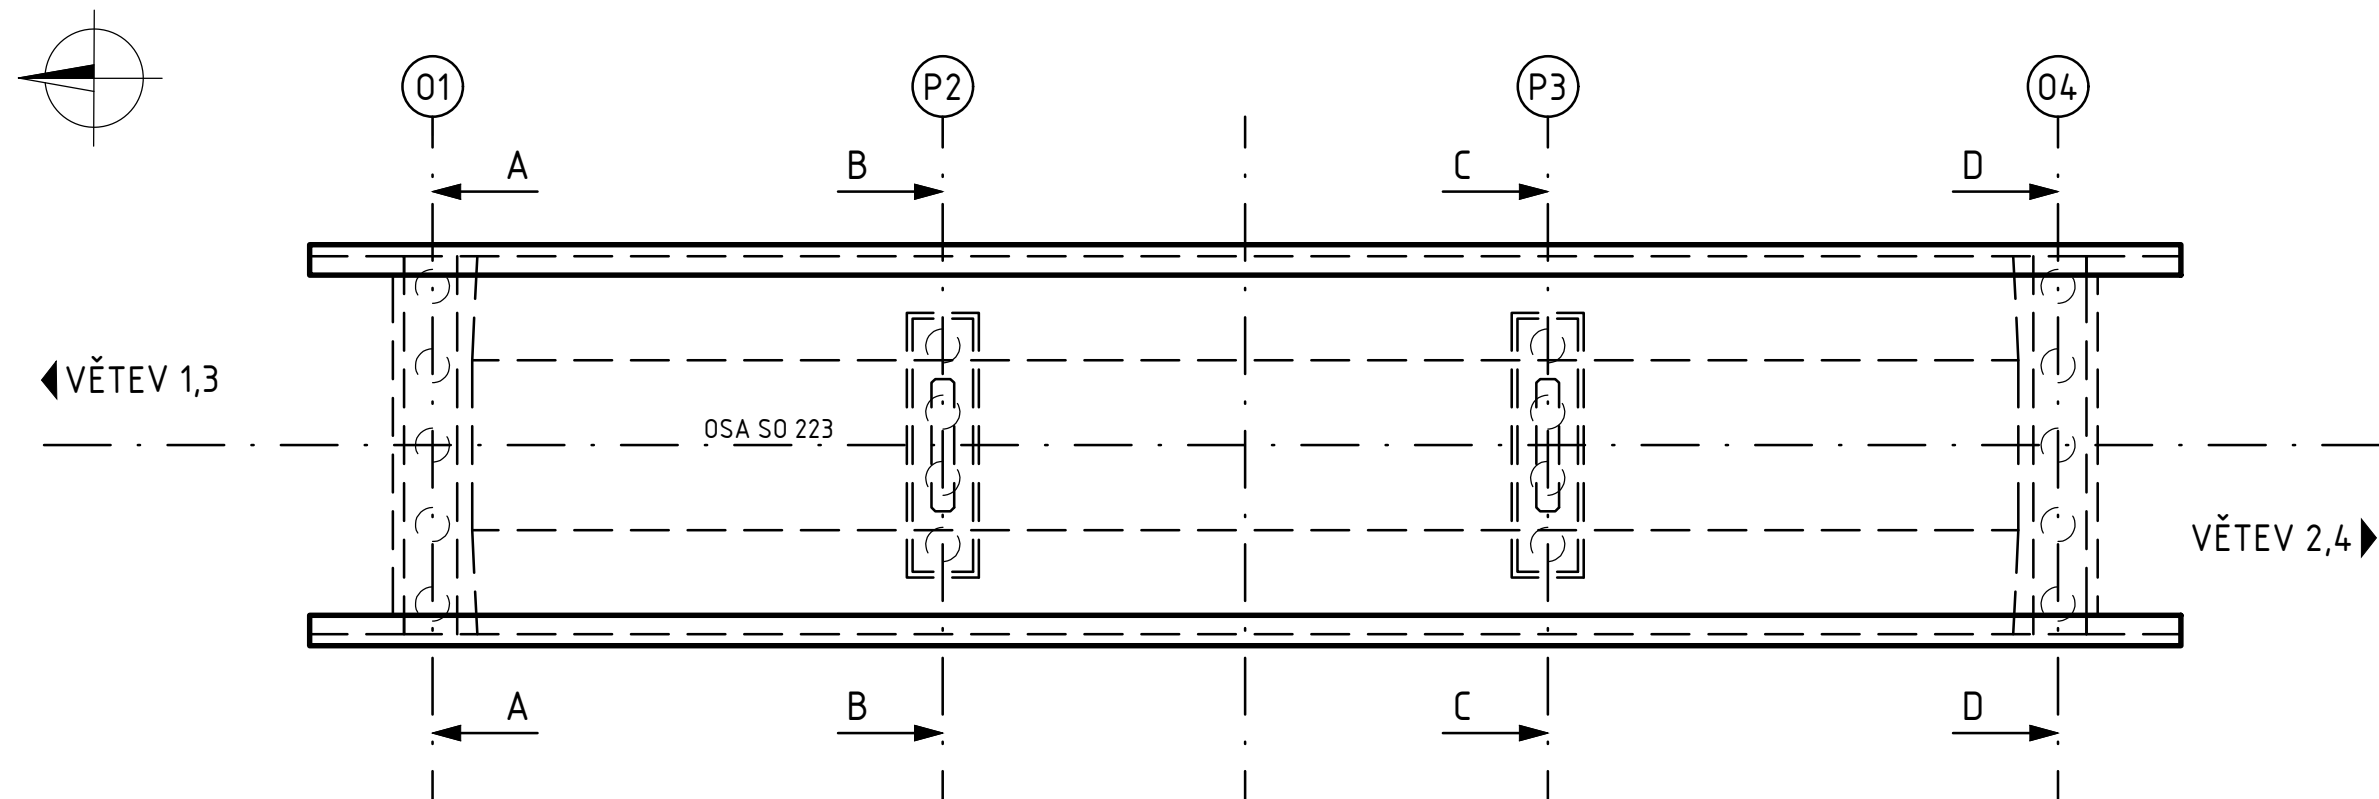

Souřadnicový systém: S-JTSK
Výškový systém: Bpv

SO 223 NADJEZD MŮK MARTINOVICE V KM 7,320

Objednatel:



Ředitelství silnic a dálnic s. p.
Čerčanská 2023/12, Krč, 140 00 Praha 4



Valbek, spol. s r.o.
Vaňurova 505/17
460 07 Liberec 3



	Vypracoval	M. KNESPLOVÁ	Zak. číslo	21-L113-001
	Zodp. projektant	ING. S. RŮŽIČKA	Datum	02/2025
	Tech. kontrola	ING. I. BELDA	Stupeň	PDPS
	Akce		Počet formátů	8x A4
I/16 MLADÁ BOLESLAV - MARTINOVICE		Měřítko	1:100	201
Zhotovitel:		Č. přílohy	Paré	
Příloha				
Valbek, spol. s r.o. Vaňurova 505/17 460 07 Liberec 3		PRÍČNÉ ŘEZY V MÍSTĚ PODPĚR		

MĚŘÍTKO 1:100

1 0 1 2 3 4 5 6 7 8 9 10m