




OPĚRA 01
POHLED 2 1:100

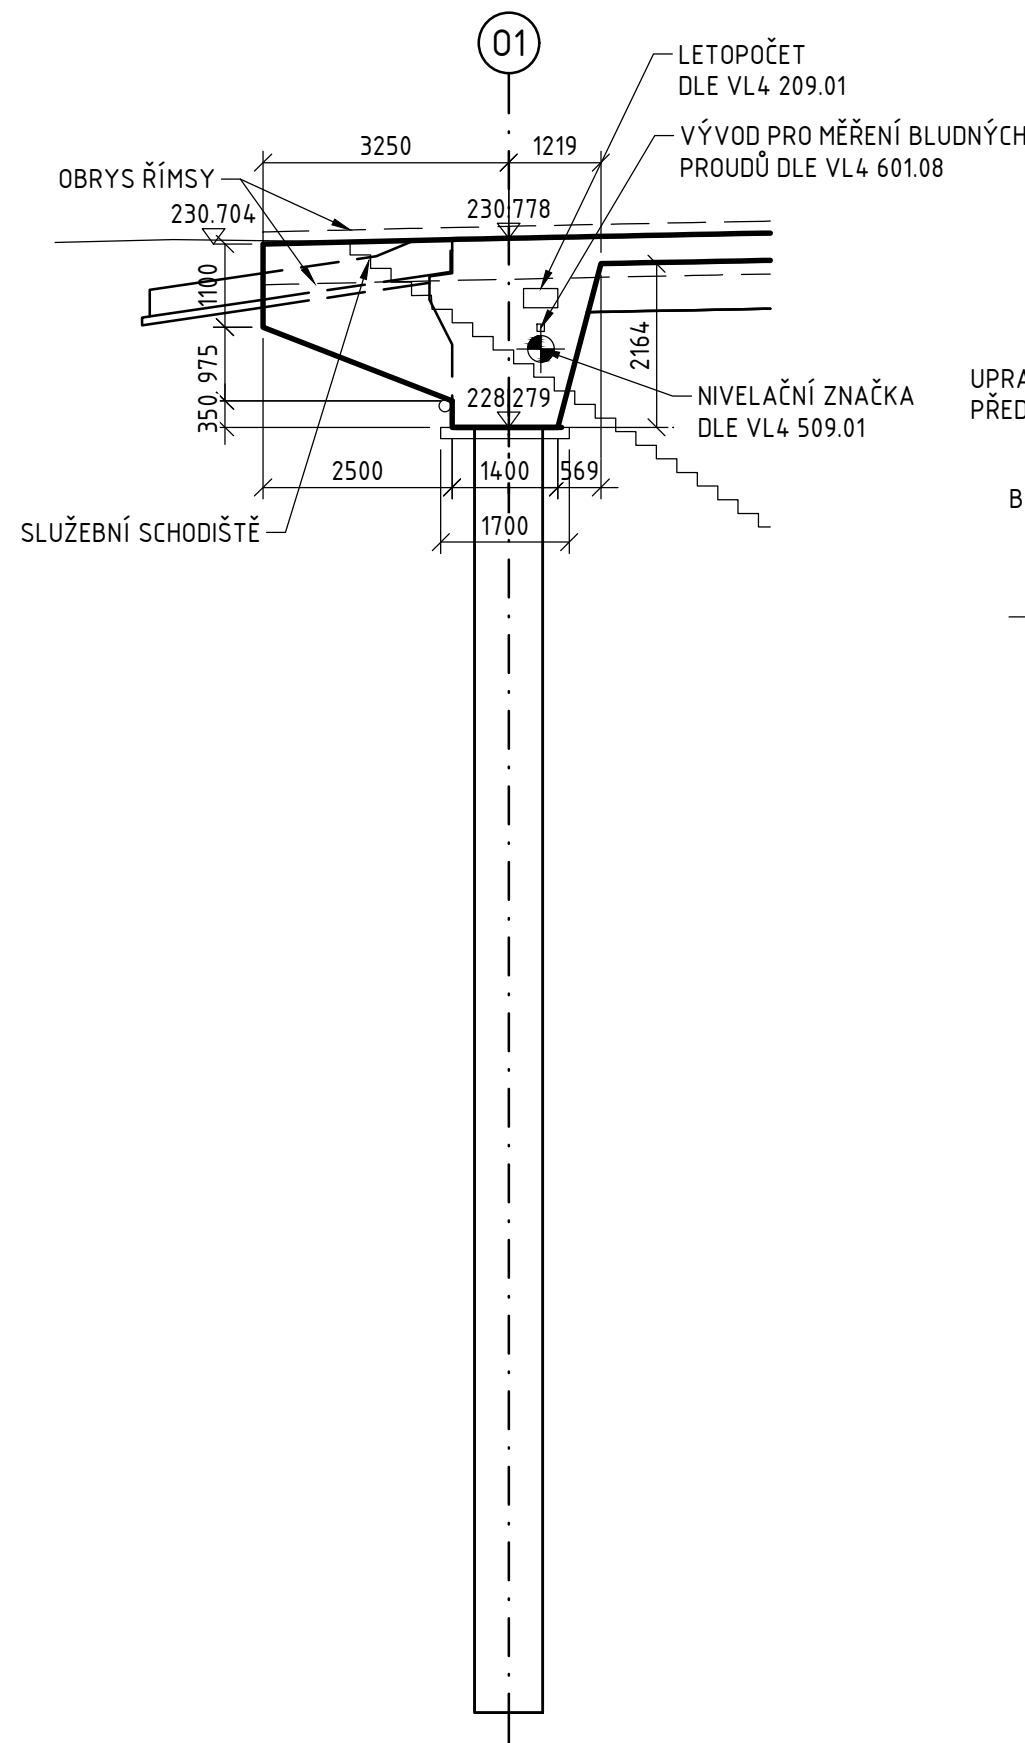


ŘEZ A-A 1:100
OSA ULOŽENÍ 01

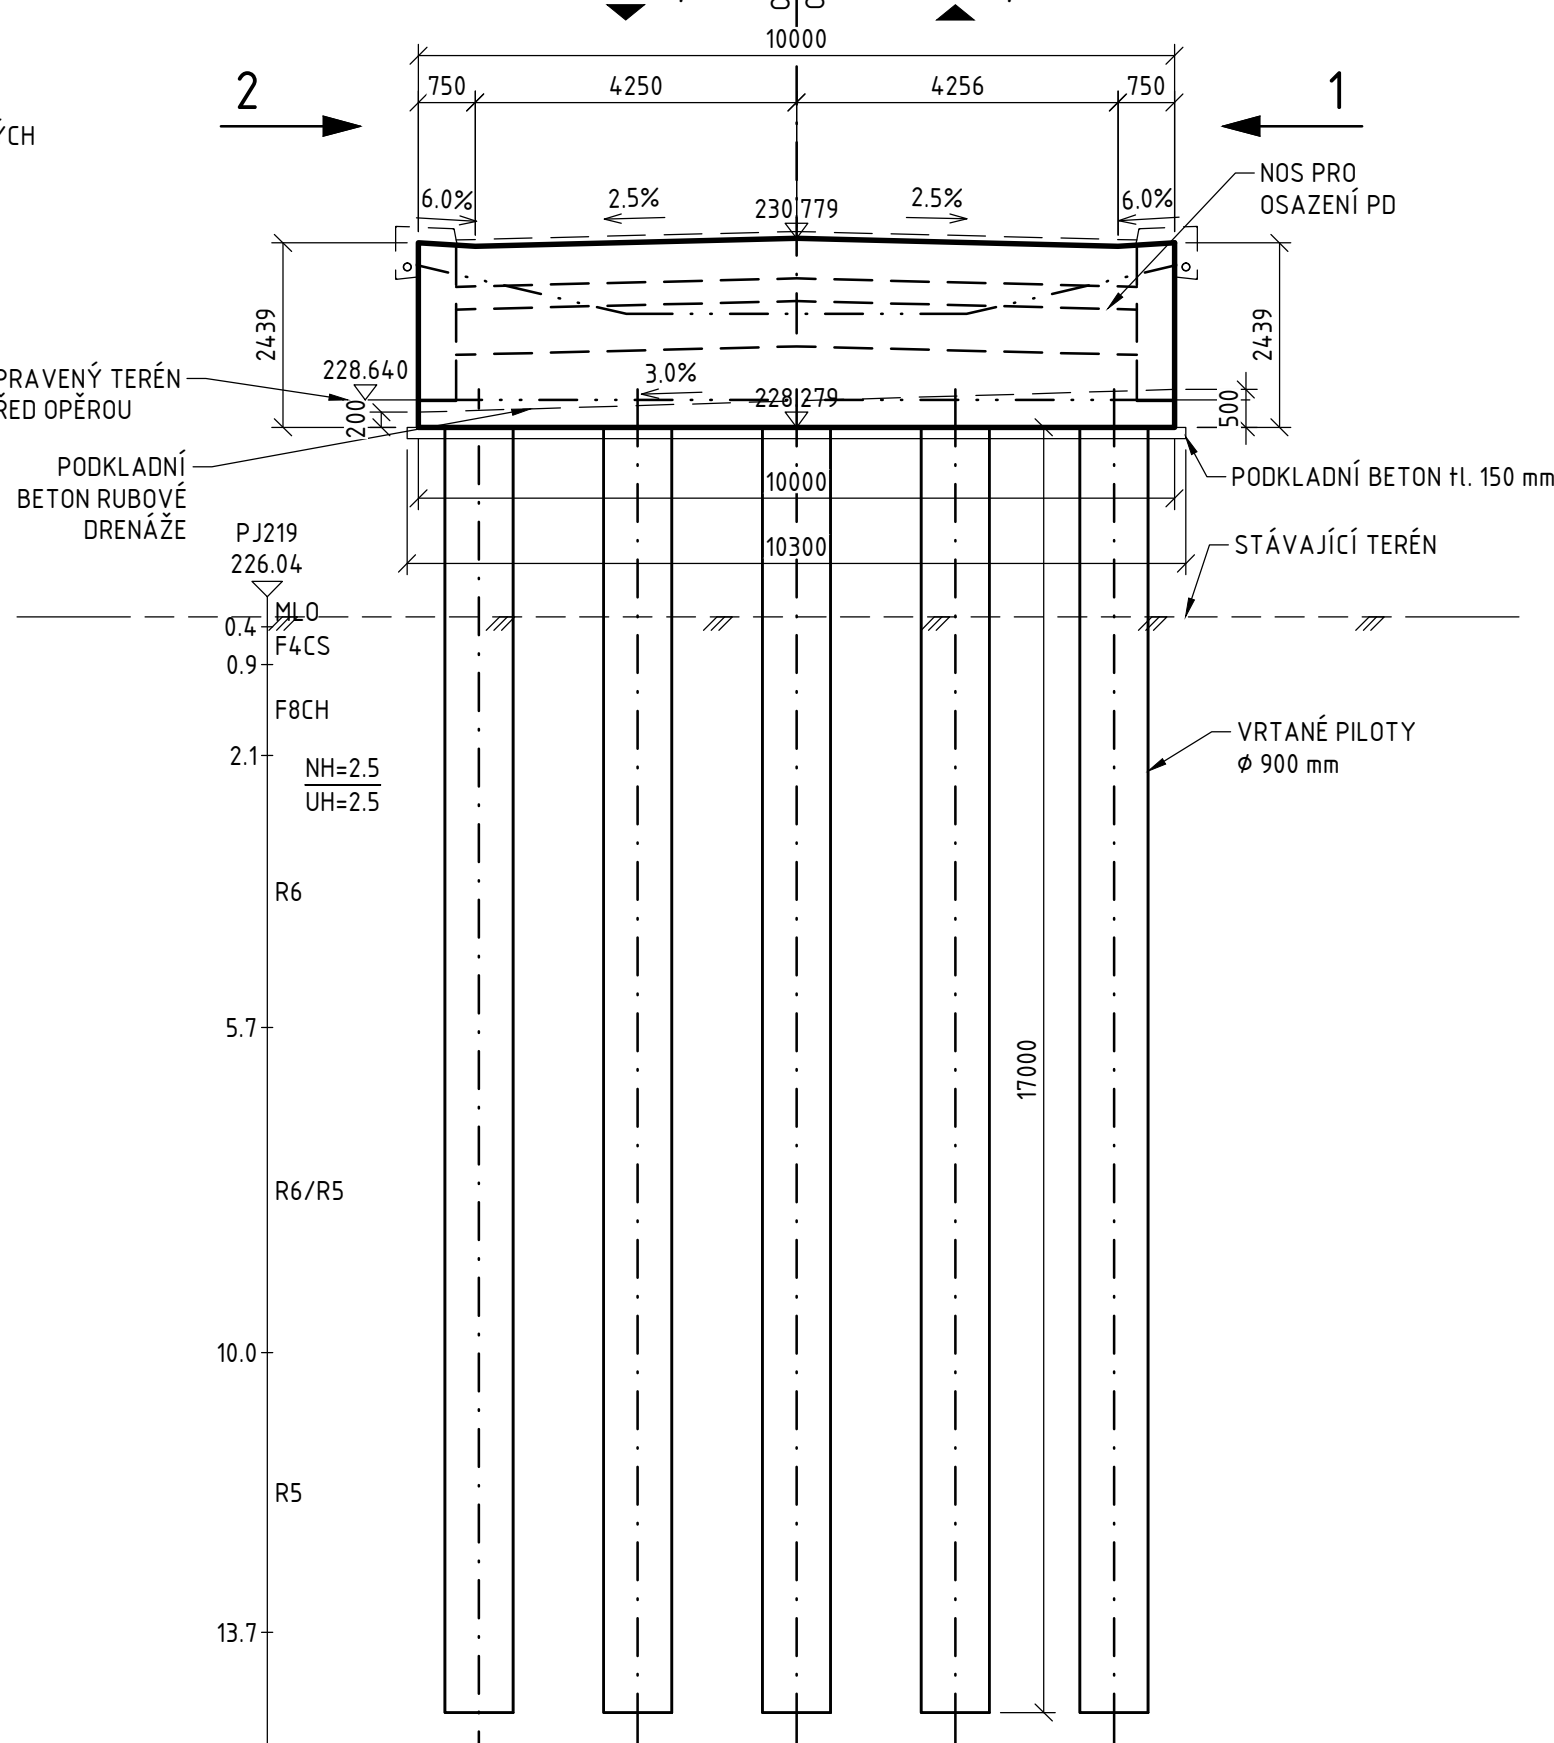


POHLED 1 1:100

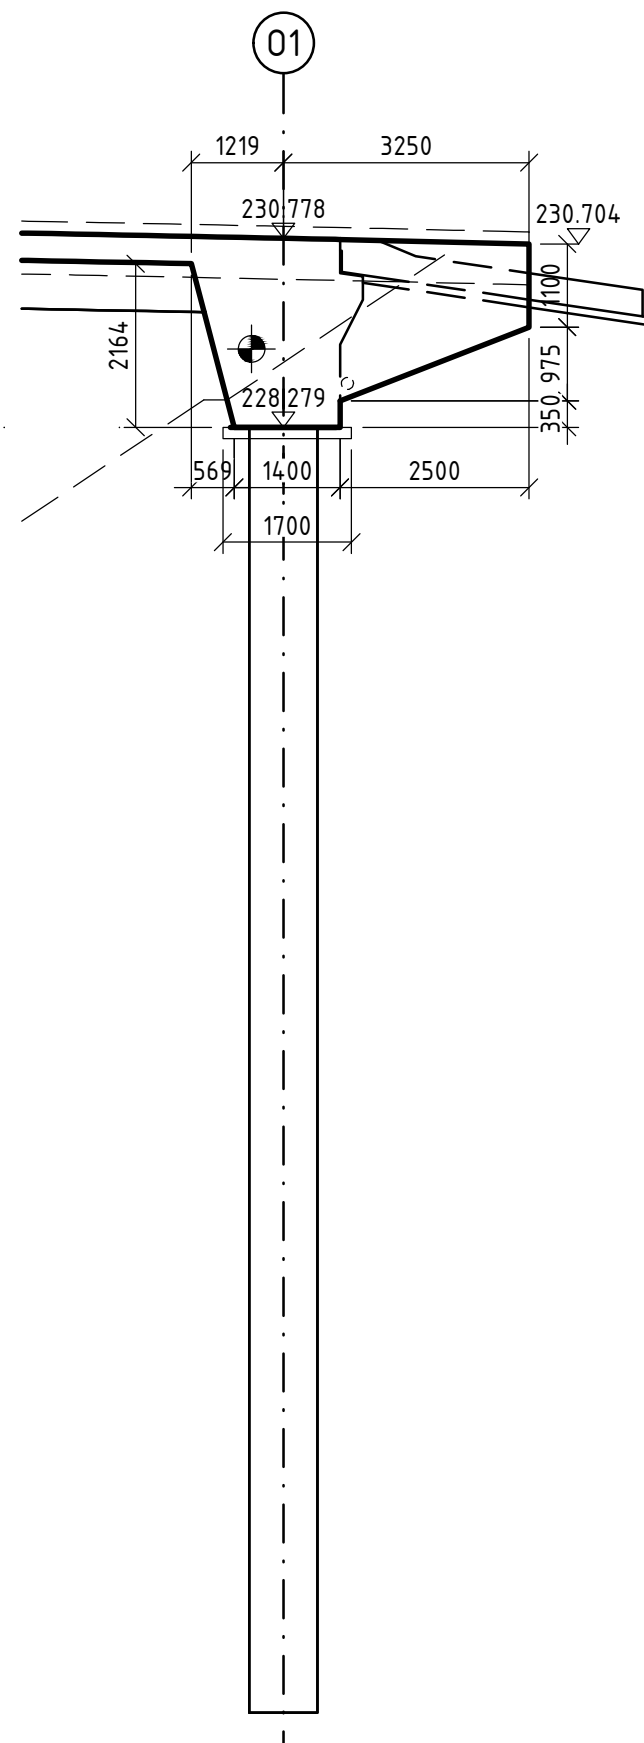


PODÉLNÝ ŘEZ 1:200

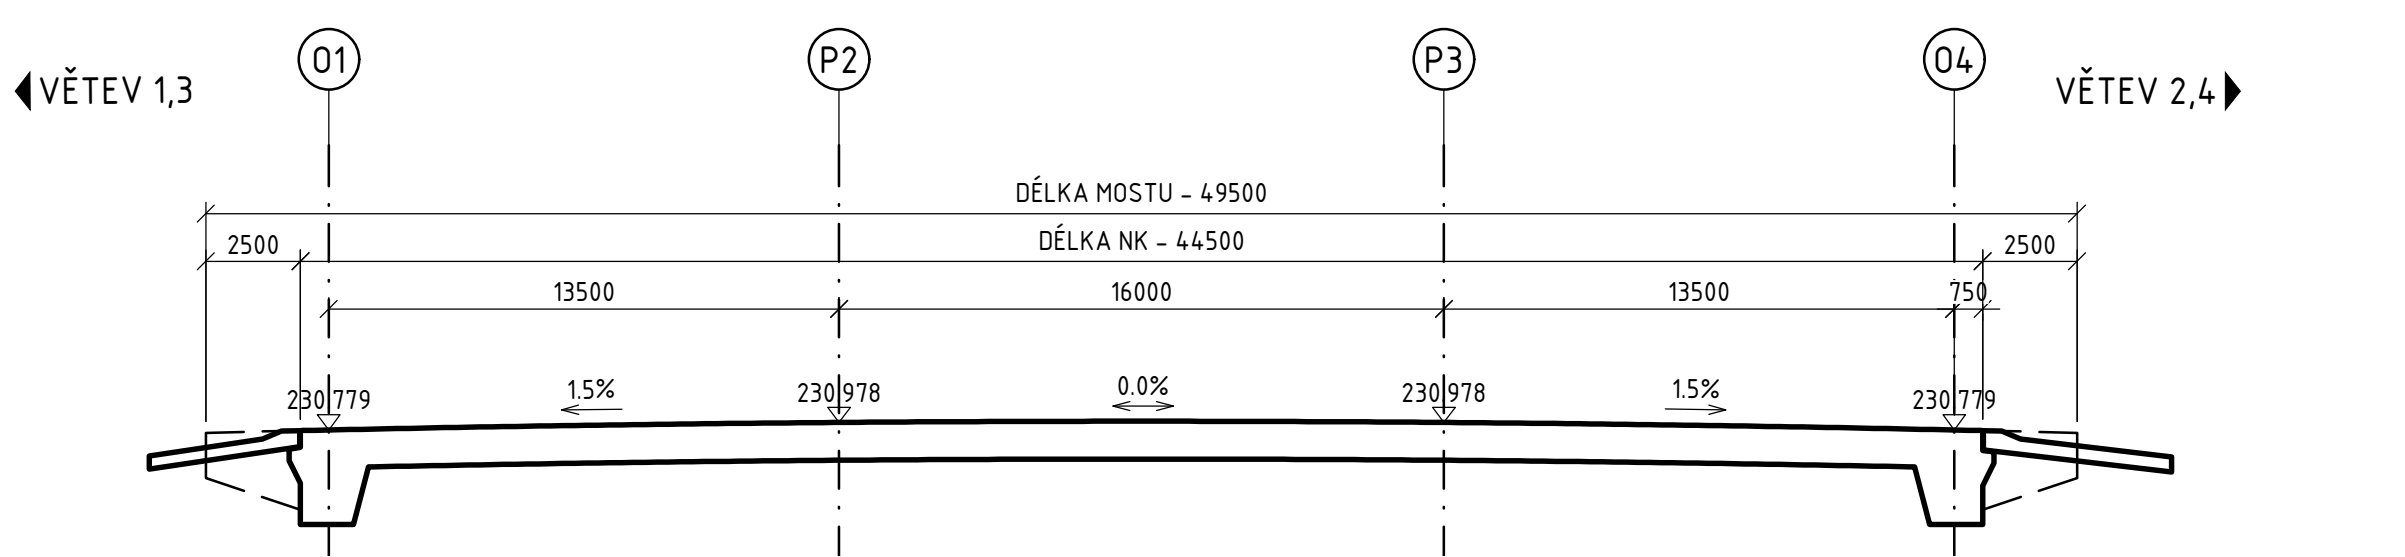

PŮDORYS 1:200

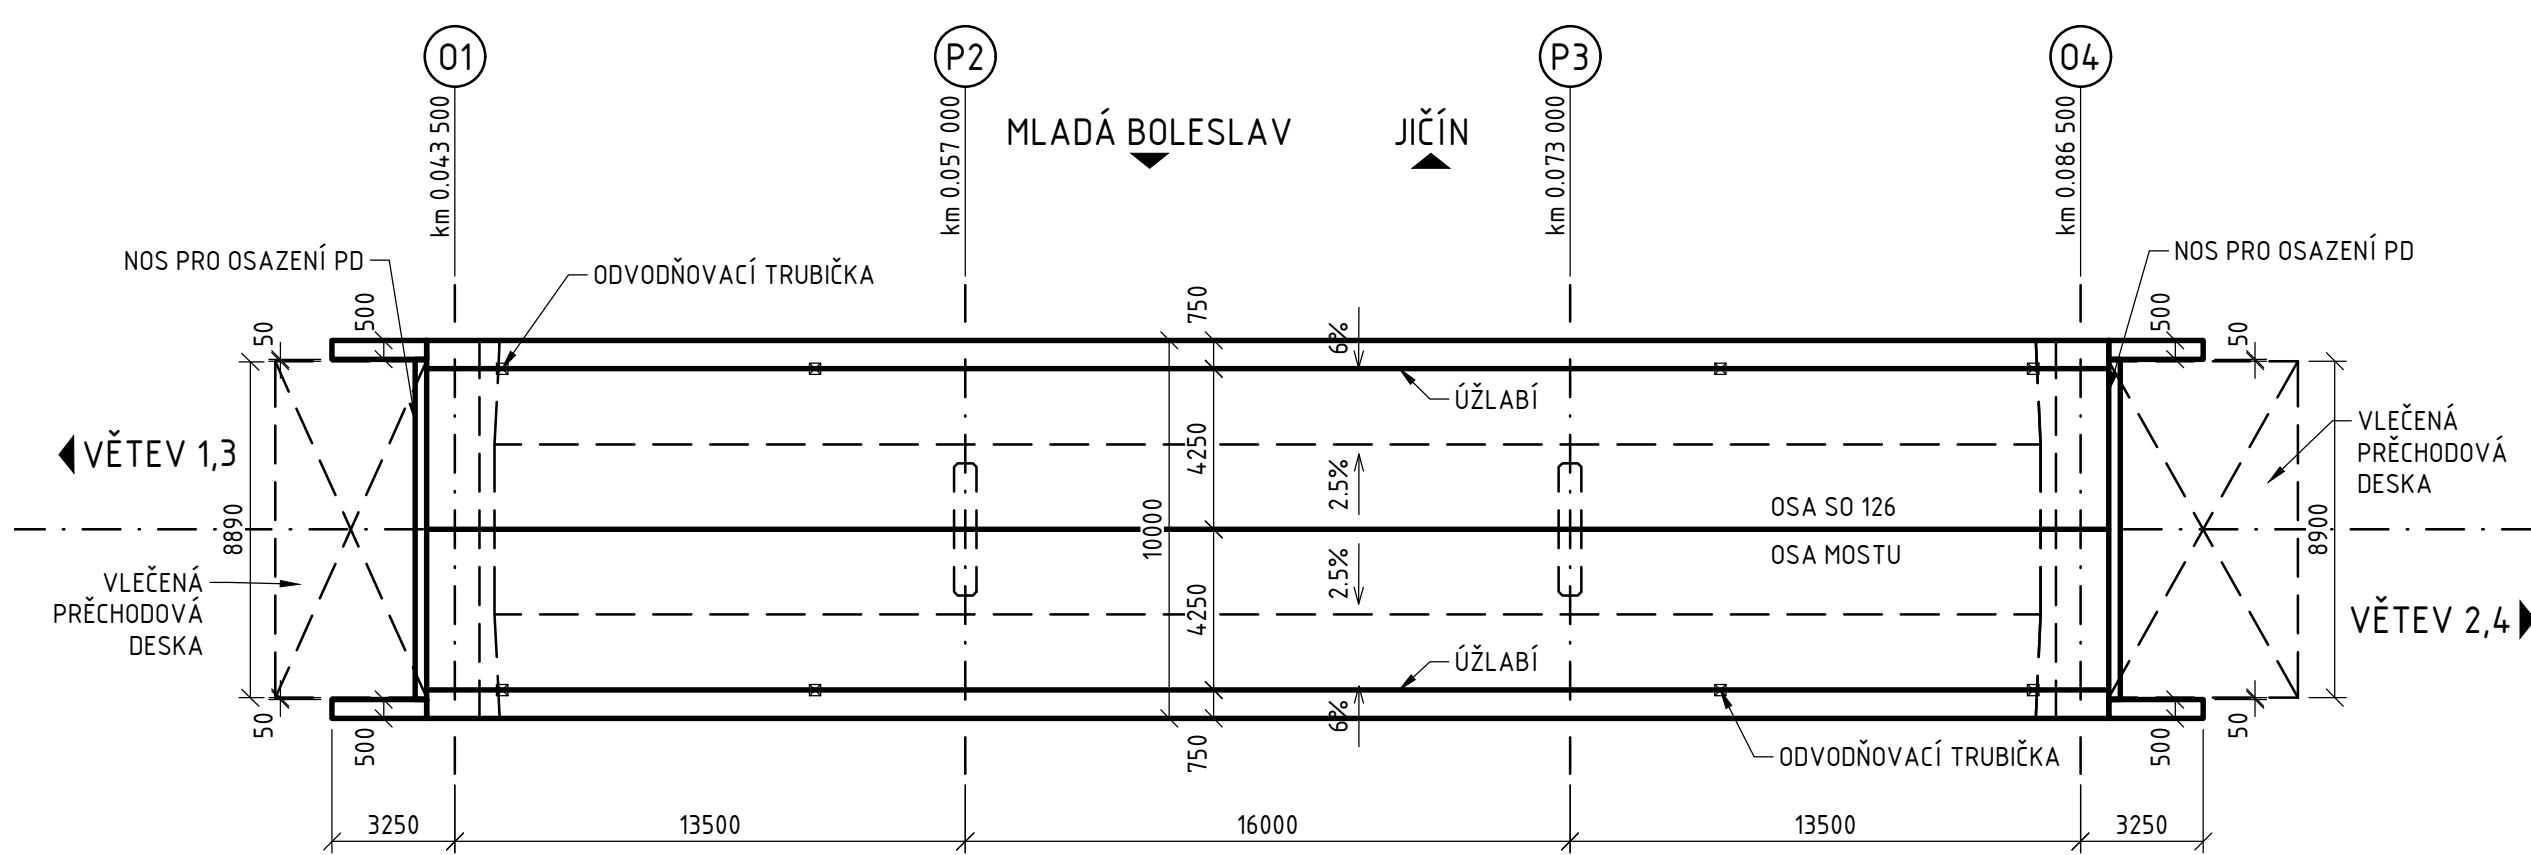

PŘÍČNÝ ŘEZ NK 1:75

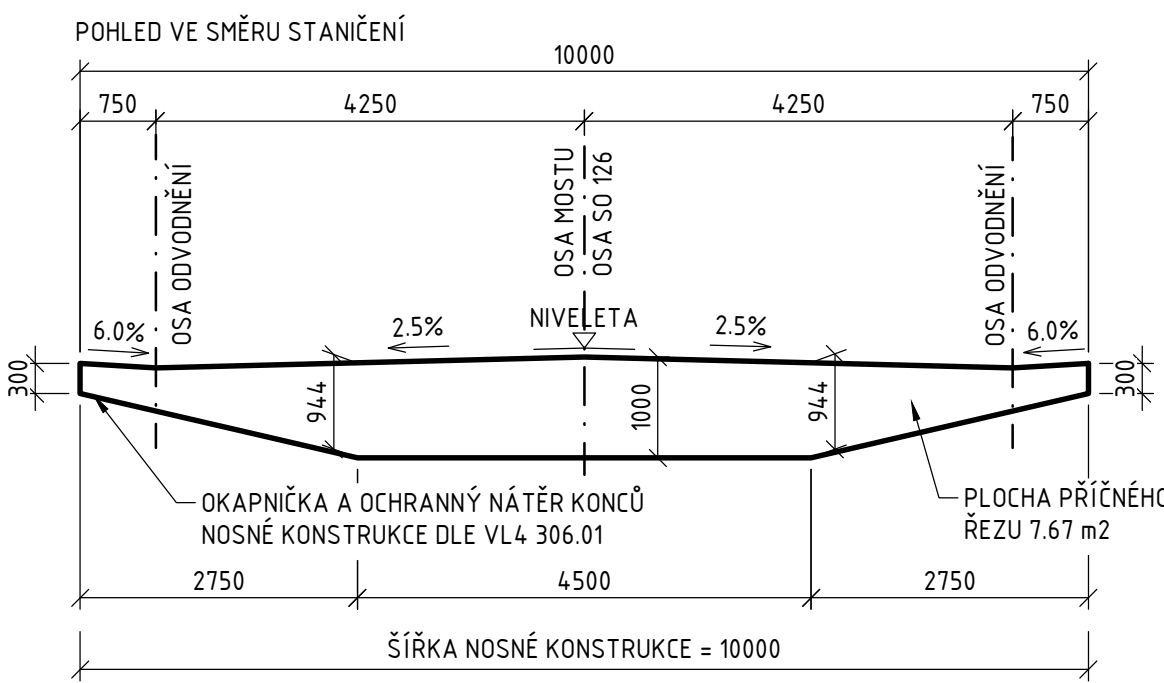


POZNÁMKY:

- NEDÍLNOU SOUČÁSTÍ VÝKRESU JSOU POZNÁMKY A SPECIFIKACE UVEDENÉ NA VÝKRESE POZNÁMEK A TECHNICKÝCH SPECIFIKACÍ


OPĚRA 04

POHLED 3 1:100

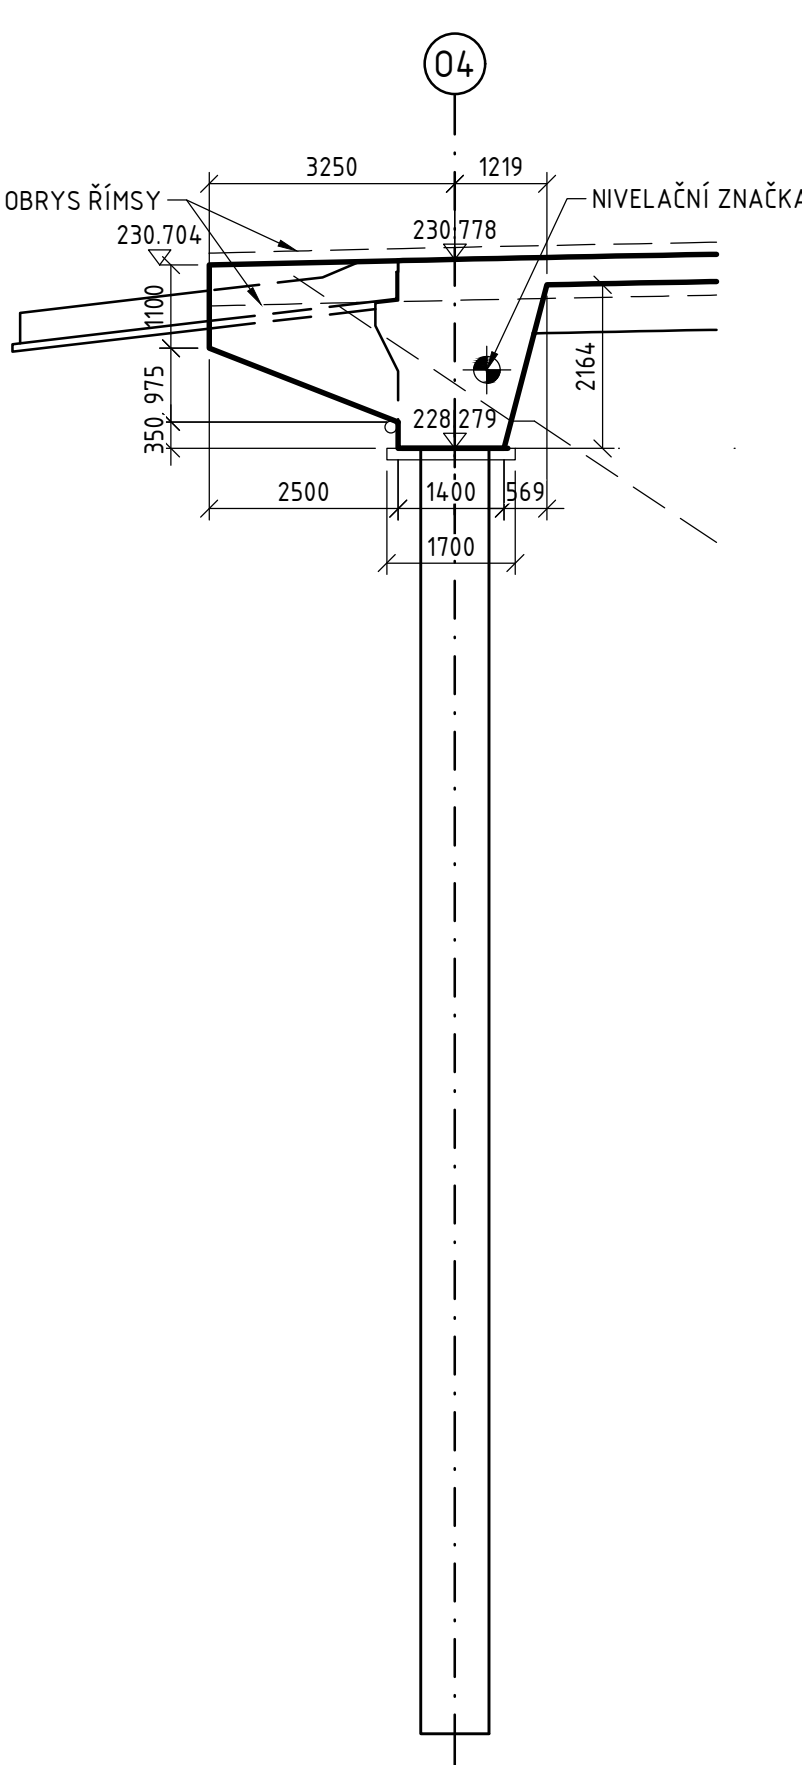


ŘEZ A-A 1:100


OSA ULOŽENÍ 04

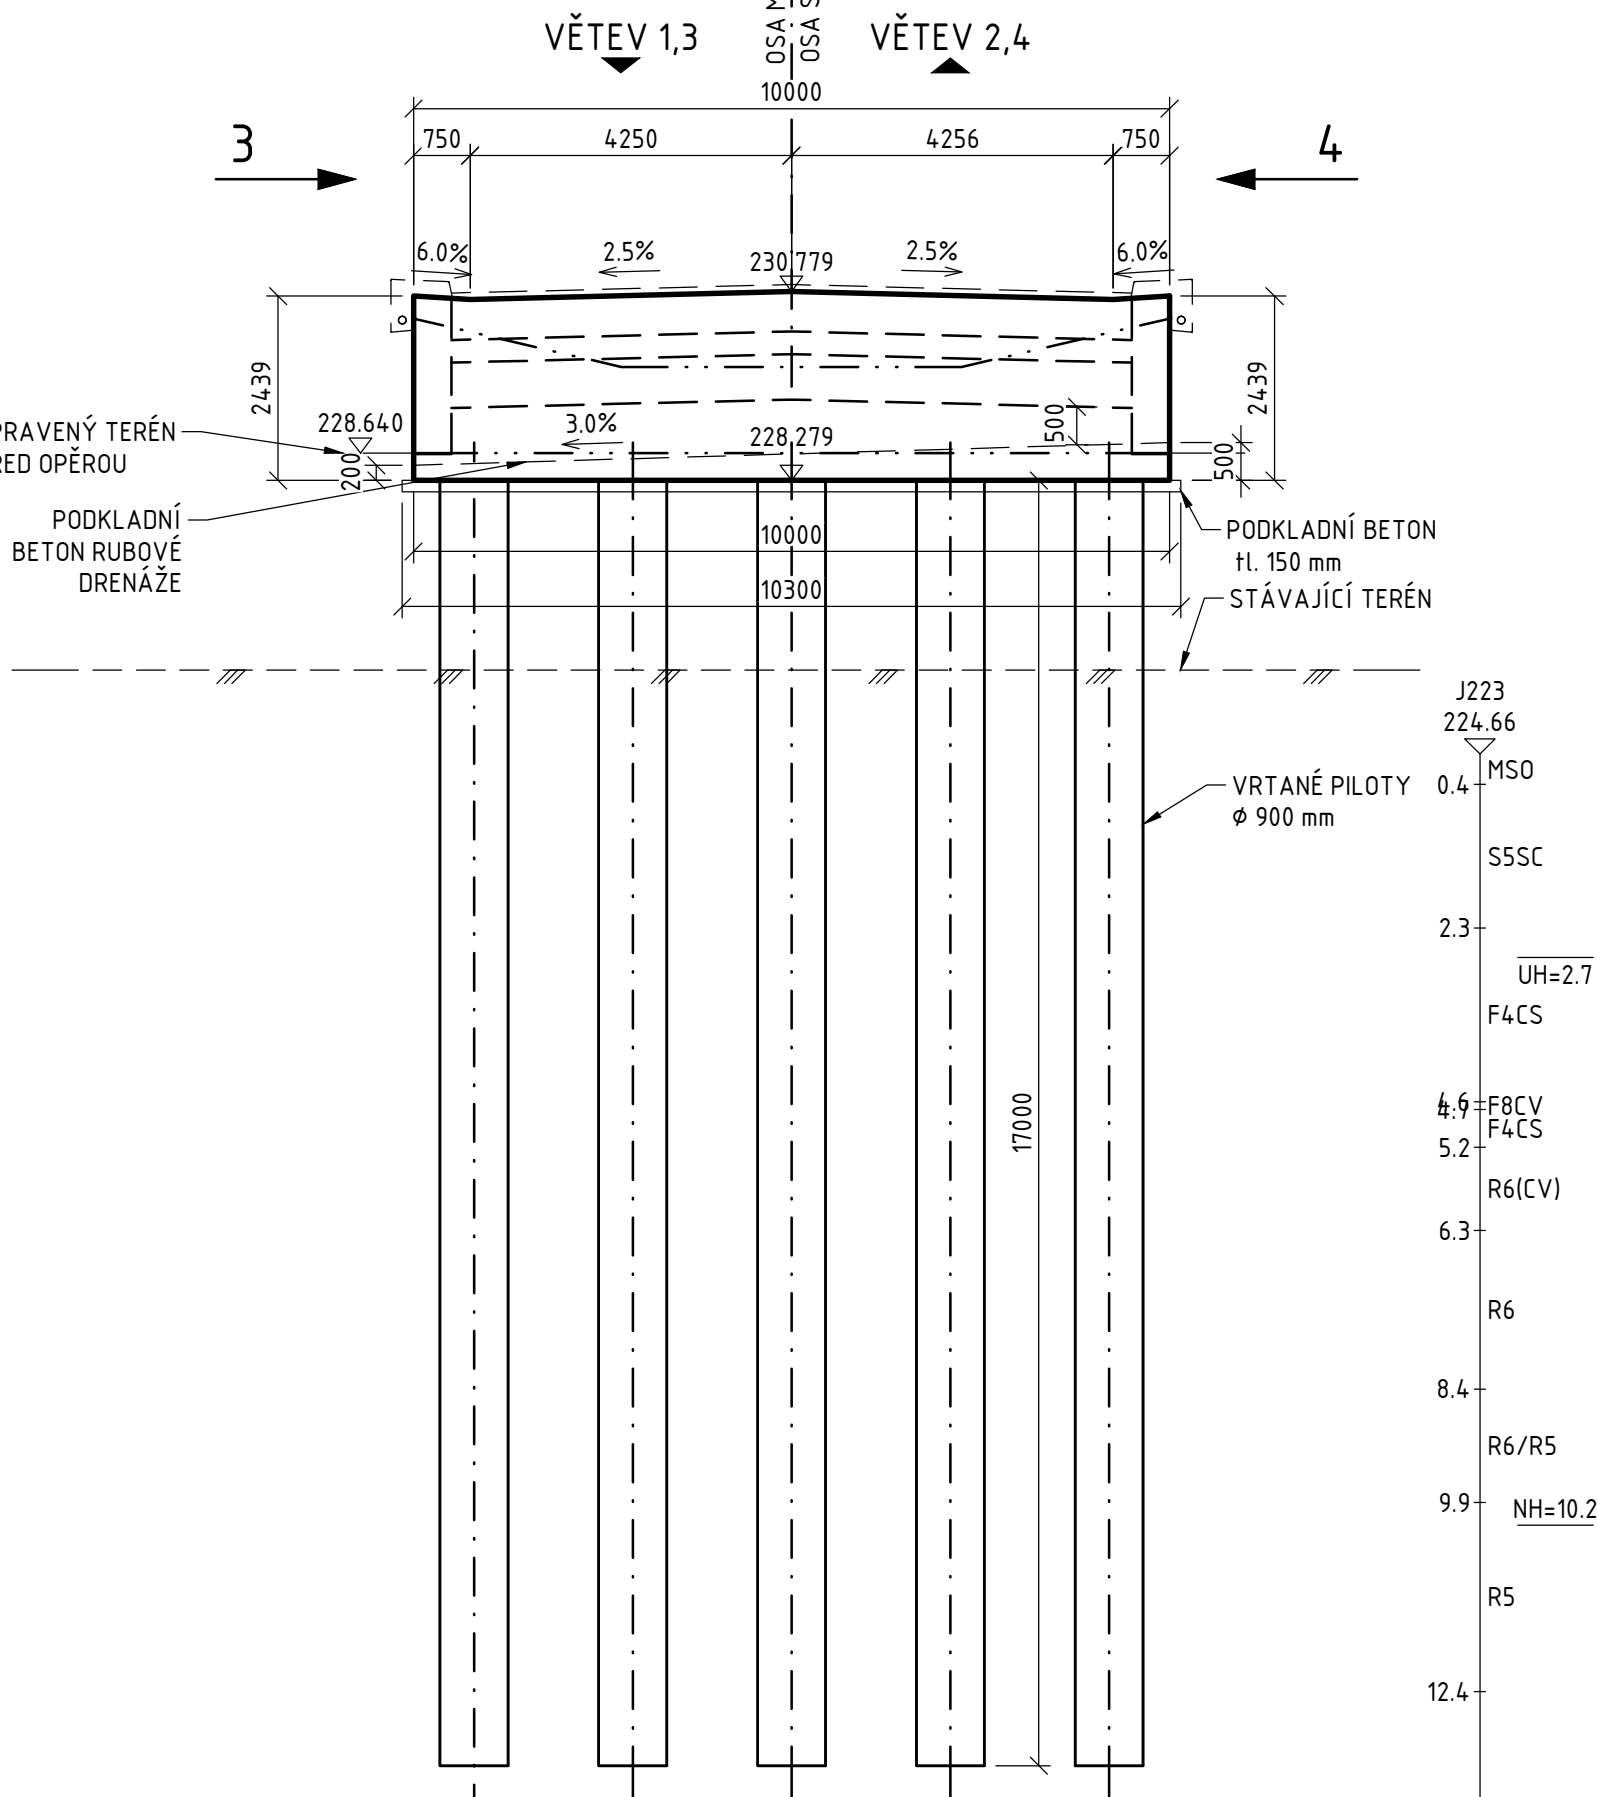


POHLED 4 1:100

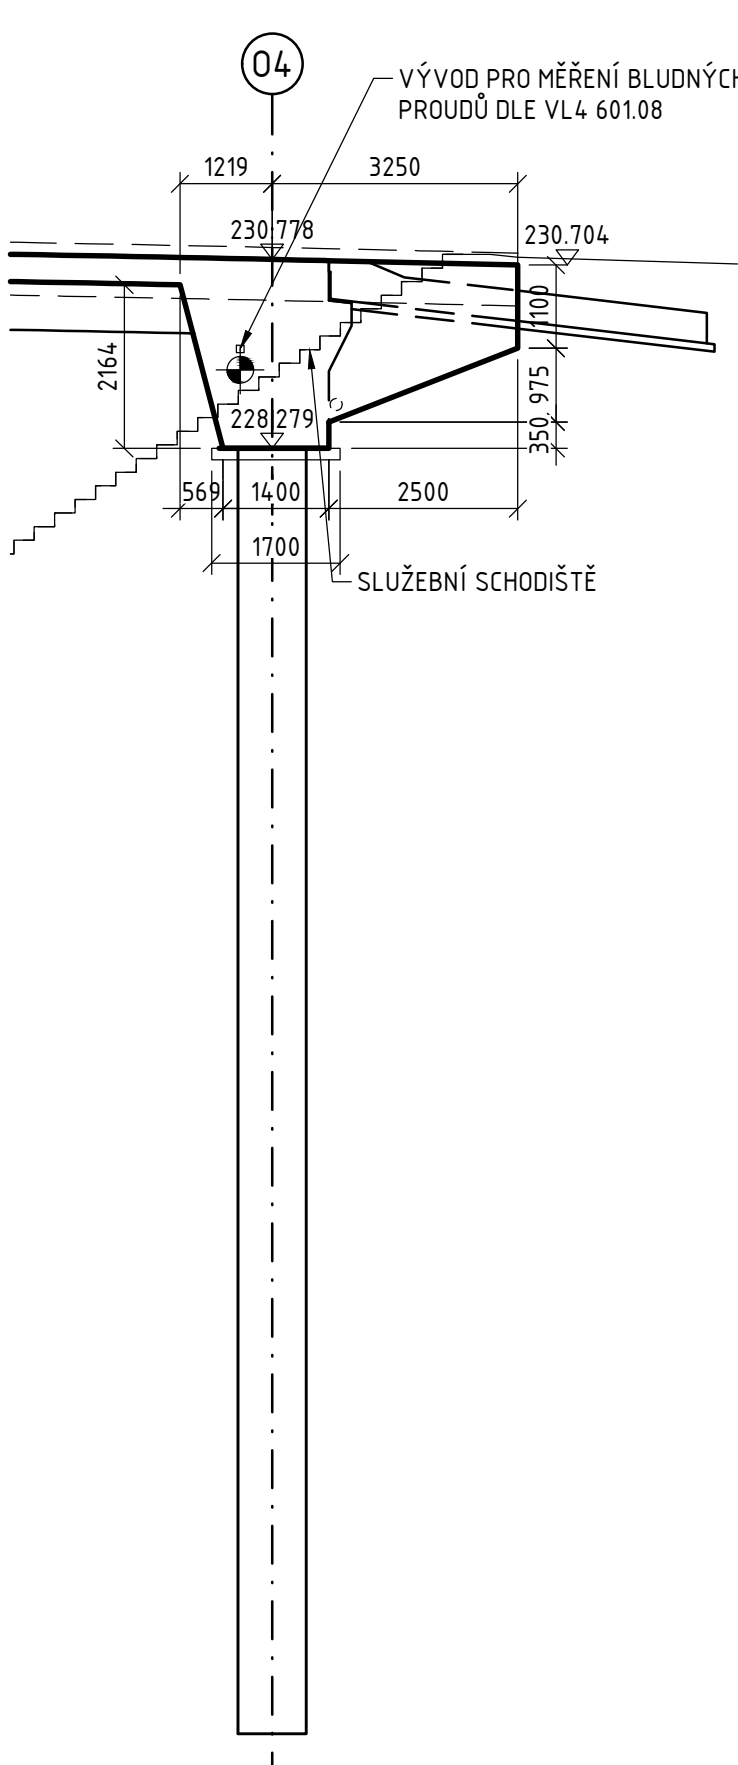

PODÉLNÝ ŘEZ PŘECHODOVOU DESKOU 1:50

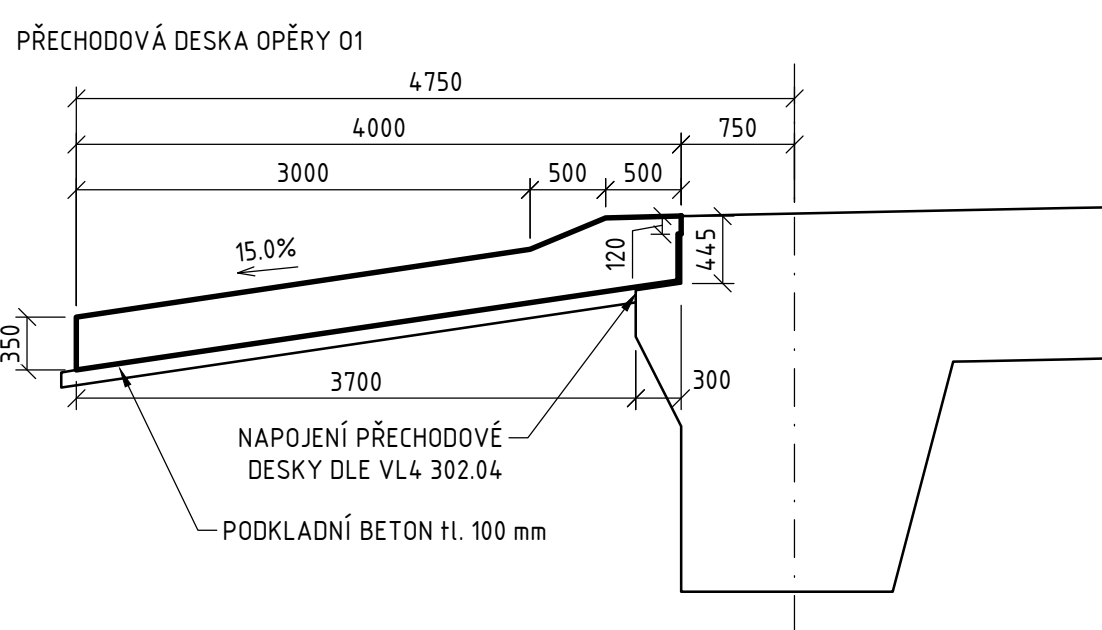

PODÉLNÝ ŘEZ PŘECHODOVOU DESKOU 1:50

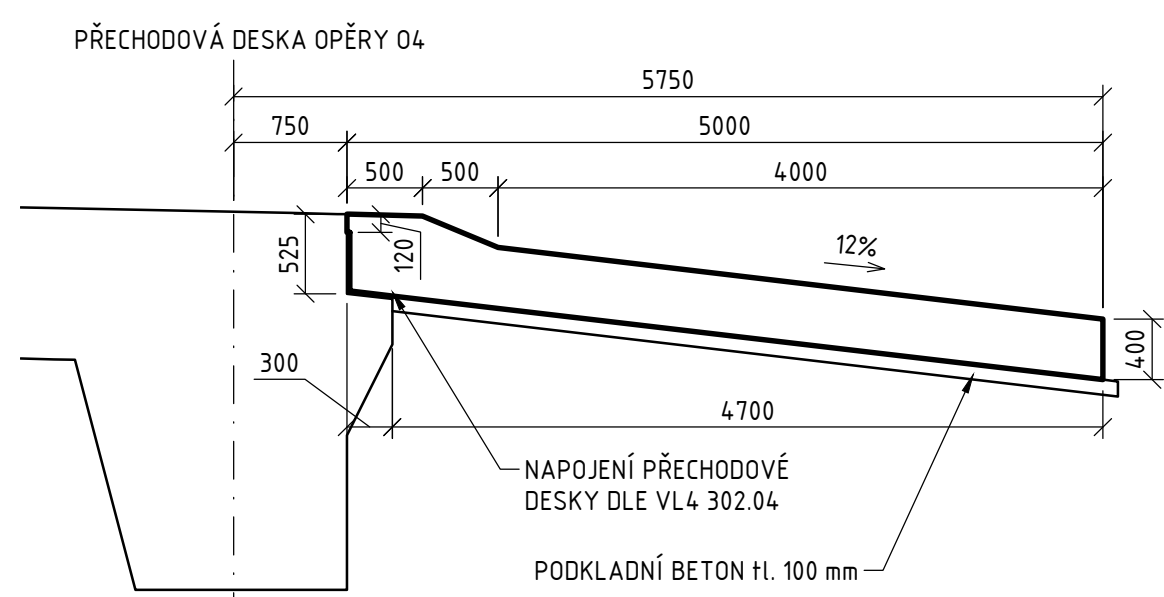

Souřadnicový systém: S-JTSK
Výškový systém: Bpv

SO 223 NADJEZD MŮK MARTINOVICE V KM 7,320

Objednatel:

ŘEDITELSTVÍ
SILNIC
A DÁLNIC

Ředitelství silnic a dálnic s. p.
Čerčanská 2023/12, Krč, 140 00 Praha 4

Valbek

Valbek, spol. s r.o.
Vaňurova 505/17
460 07 Liberec 3

Valbek

Vypracoval	M. KNESPLOVÁ	Zak. číslo	21-L113-001
Zodp. projektant	ING. S. RŮŽIČKA	Datum	02/2025
Tech. kontrola	ING. I. BELDA	Stupeň	PDP5
Akce		Počet formátů	8x A4
		Měřítko	1:200, 100, 75, 50
		C. přílohy	Paré
Zhotovitel:	Příloha		
Valbek, spol. s r.o. Vaňurova 505/17 460 07 Liberec 3	HLUBINNÉ ZALOŽENÍ TVAR OPĚR 01,04 TVAR NOSNÉ KONSTRUKCE		

202

