




ŘEZ A-A 1:50

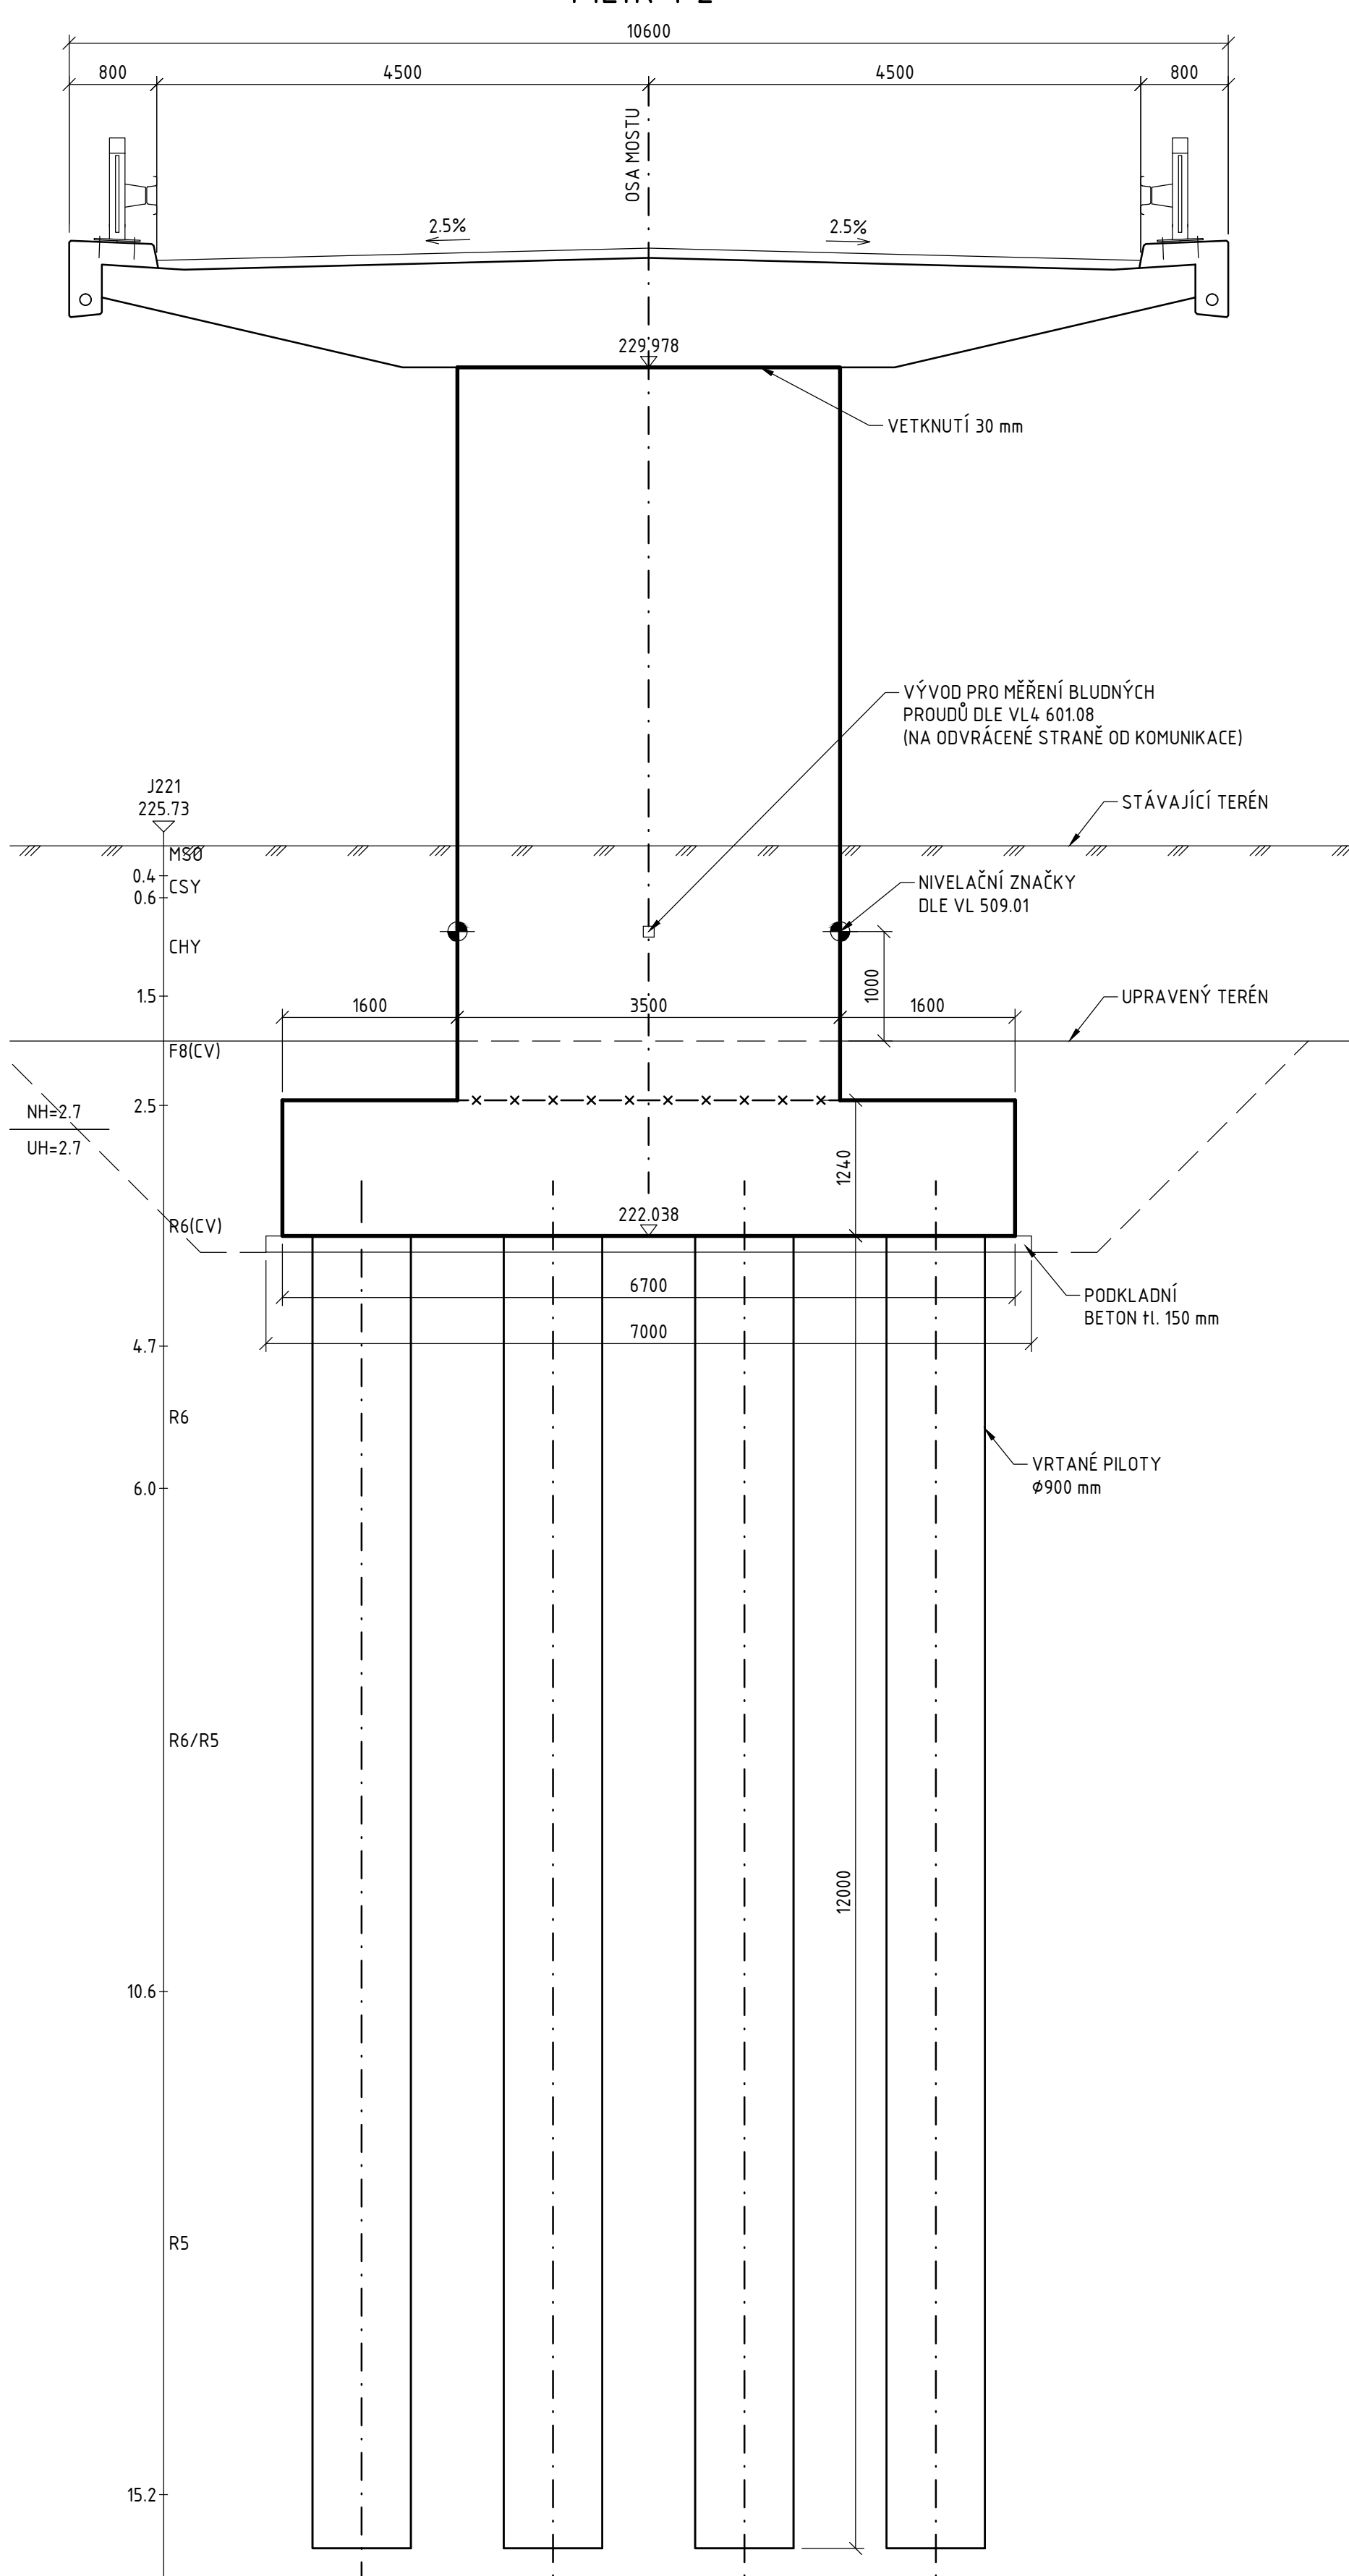



PŮDORYS ZÁKLADU 1:50

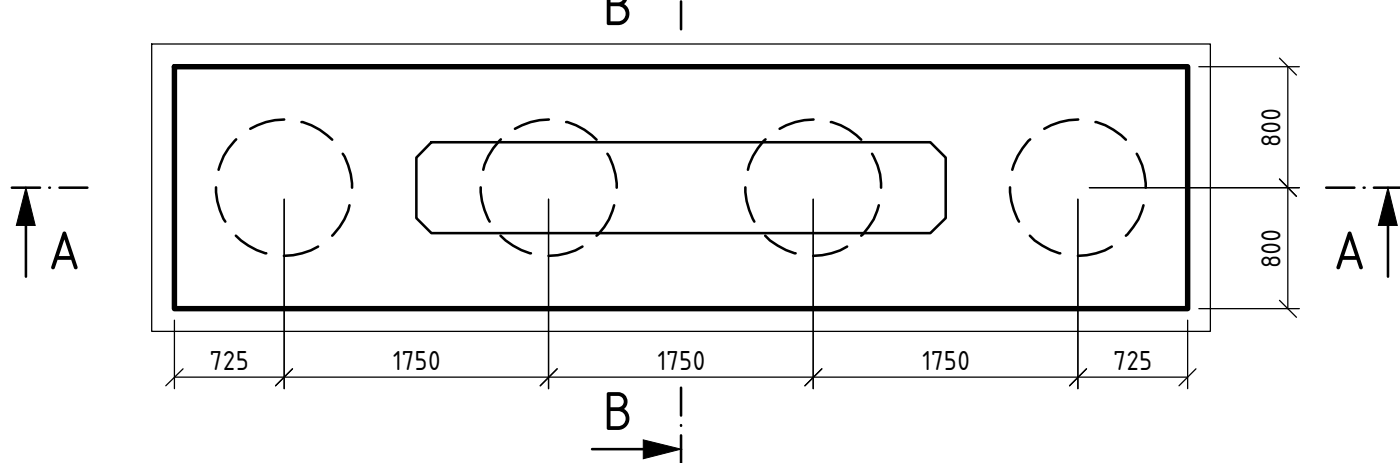


ŘEZ B-B 1:50

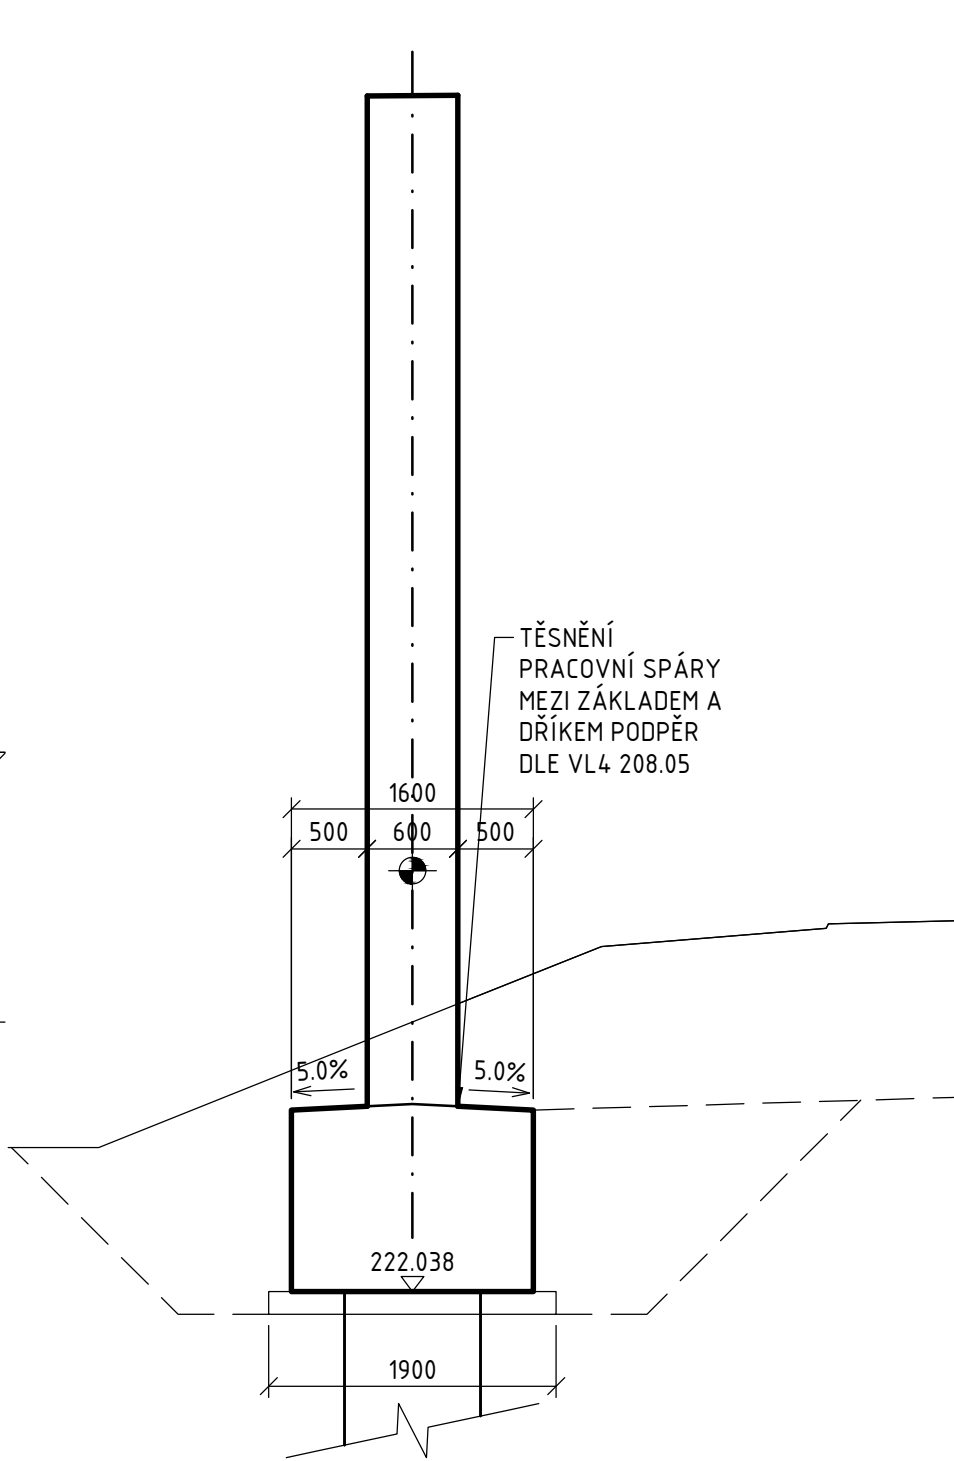


ŘEZ STOJKOU 1:50

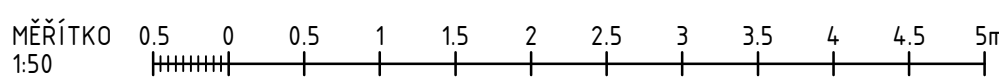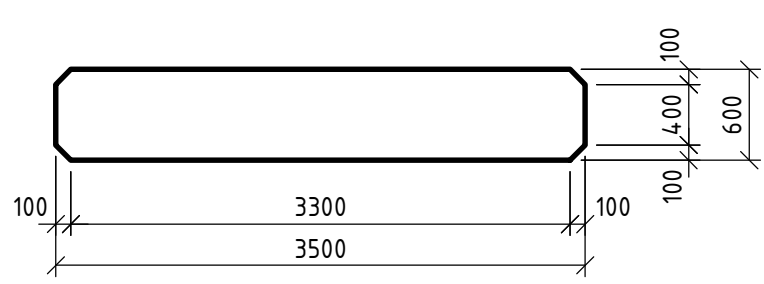


ŘEZ C-C 1:50

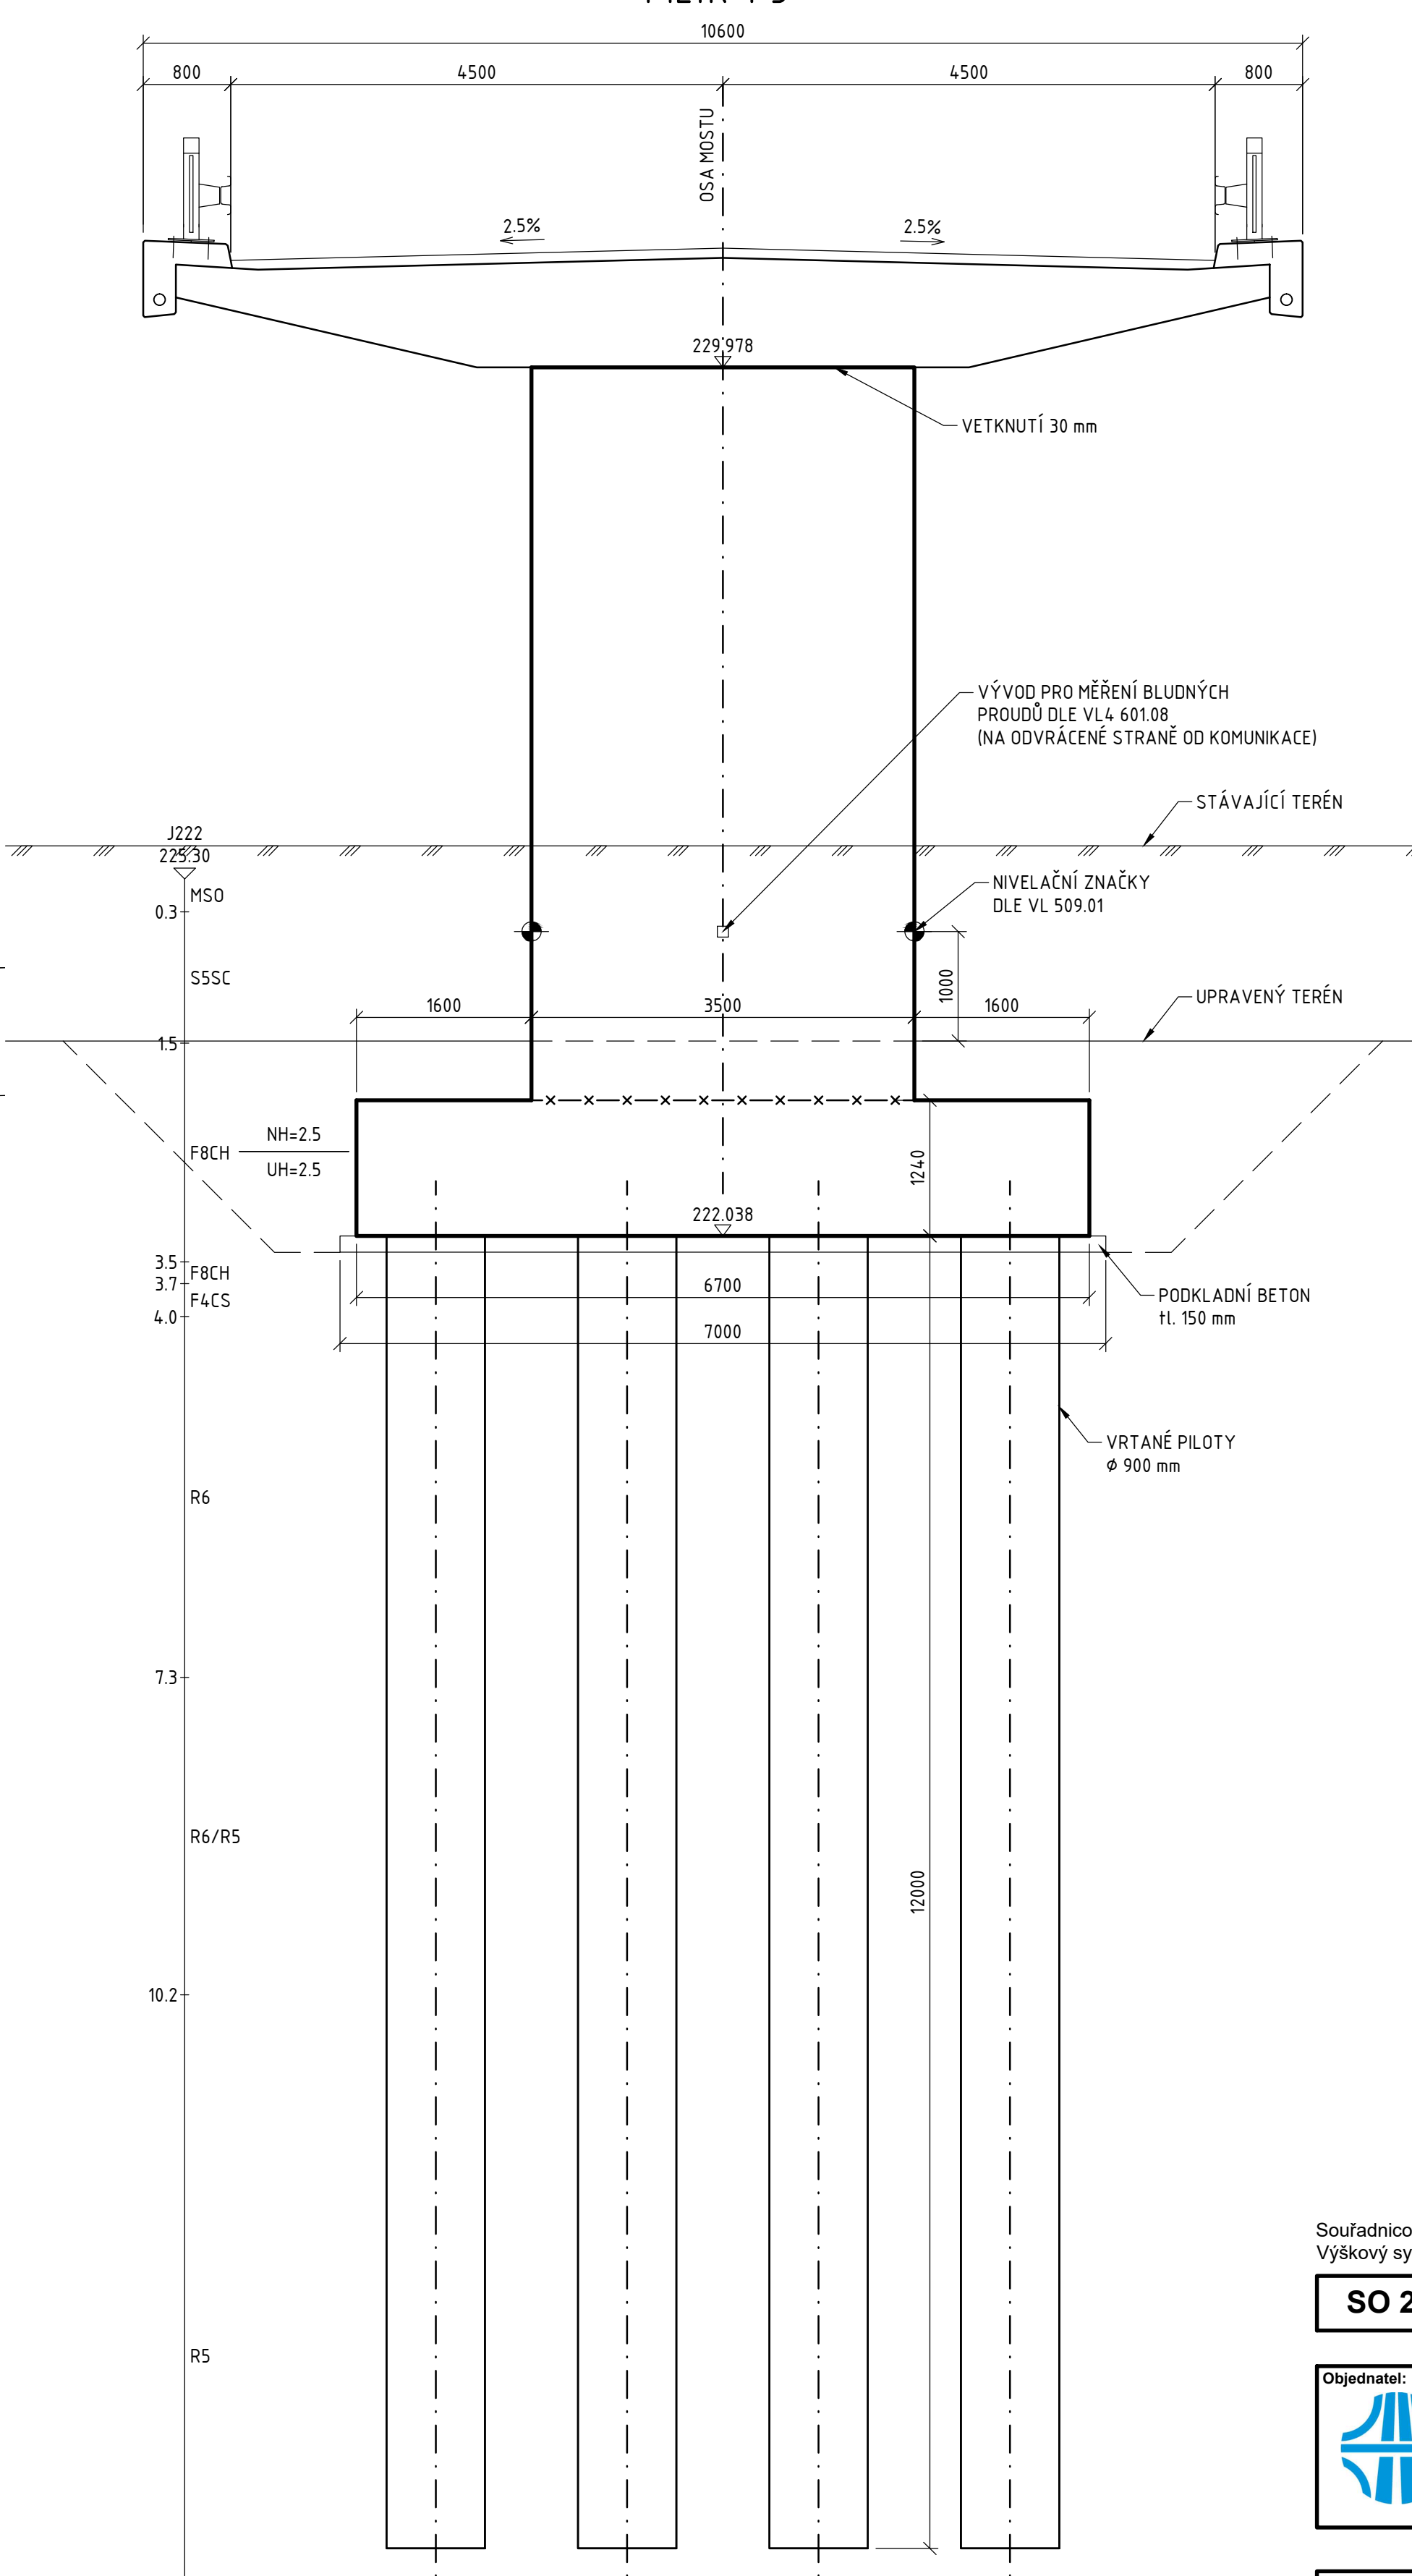

PŮDORYS ZÁKLADU 1:50

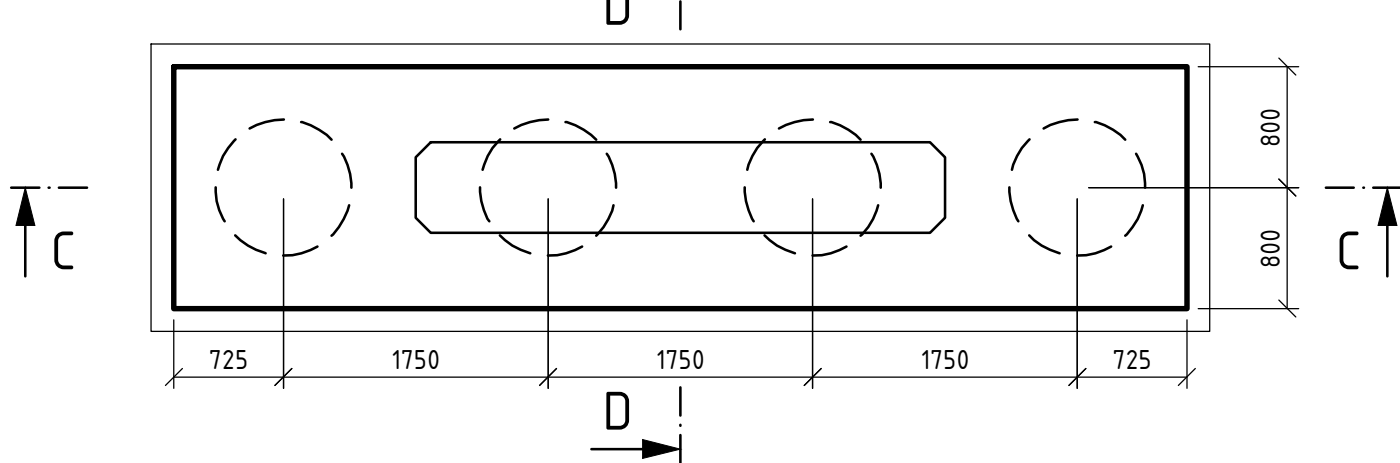

ŘEZ D-D 1:50

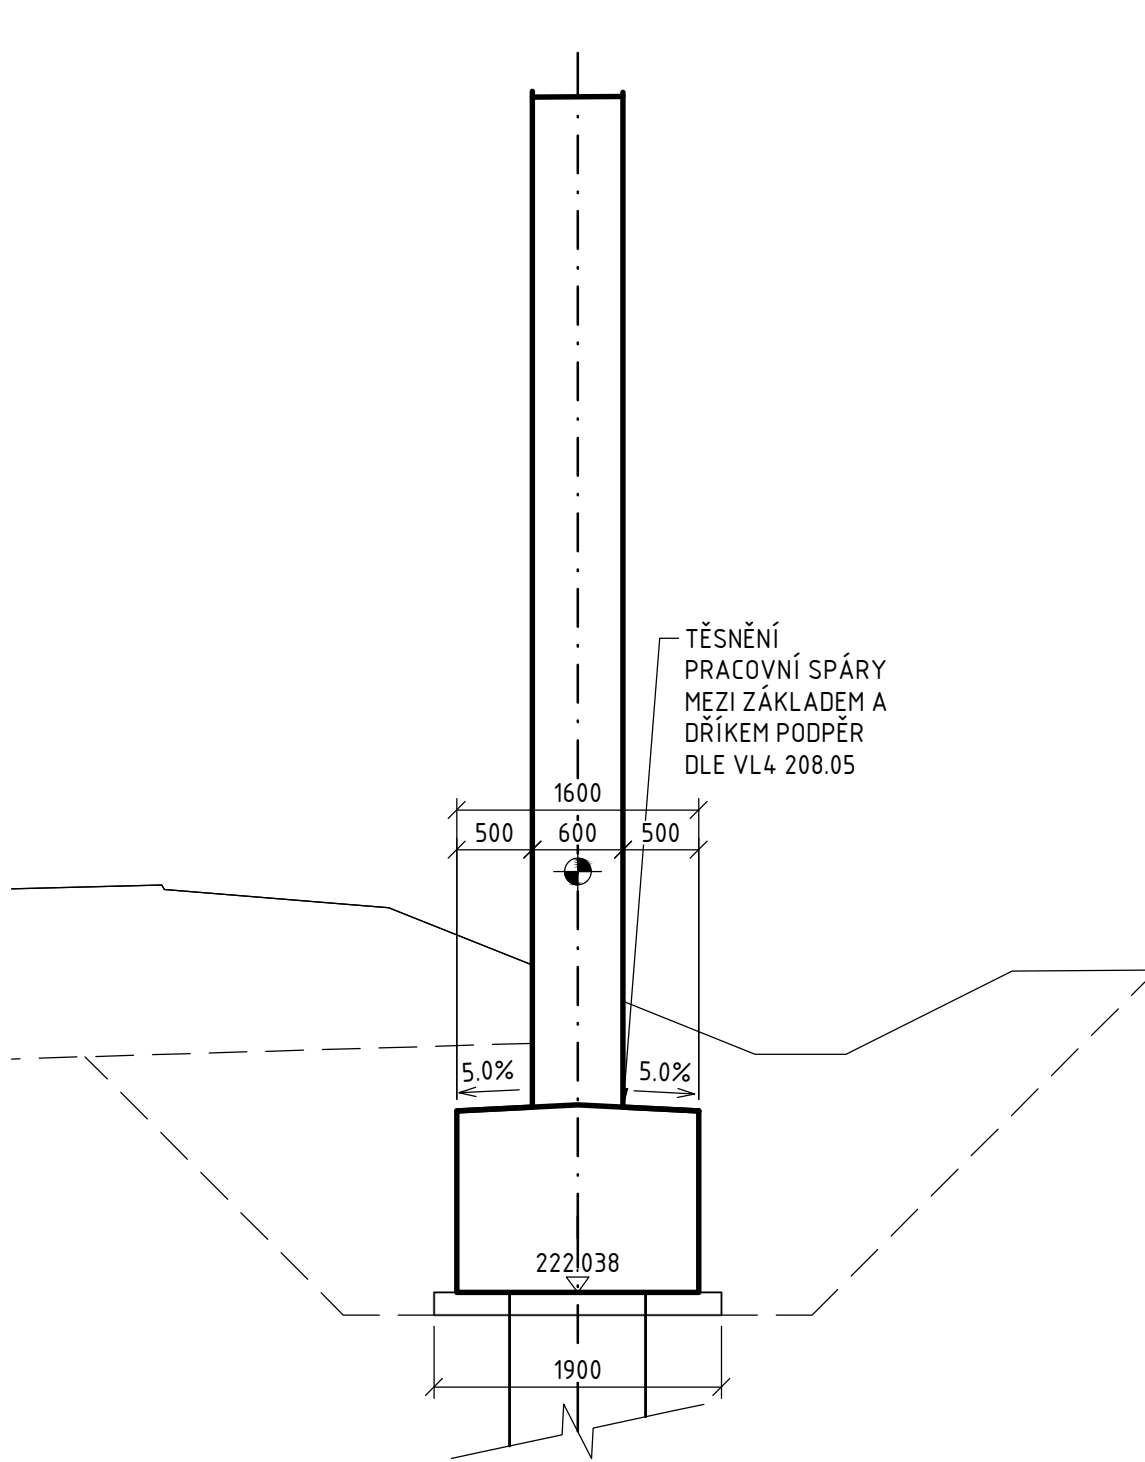

POZNÁMKY:

- NEDÍLNOU SOUČÁSTÍ VÝKRESU JSOU POZNÁMKY A SPECIFIKACE UVEDENÉ NA VÝKRESE POZNÁMEK A TECHNICKÝCH SPECIFIKACÍ

Souřadnicový systém: S-JTSK
Výškový systém: Bpv

SO 223 NADJEZD MŮK MARTINOVICE V KM 7,320

Objednatel: **Ředitelství silnic a dálnic**
Ředitelství silnic a dálnic s. p.
Čerčanská 2023/12, Krč, 140 00 Praha 4

Valbek, spol. s r.o.
Vaňurova 505/17
460 07 Liberec 3

	Vypracoval	M. KNESPOVÁ	Zak. číslo	21-L113-001
	Zodp. projektant	ING. S. RŮŽIČKA	Datum	02/2025
	Tech. kontrola	ING. I. BELDA	Stupeň	PDPS
	Akce	I/16 MLADÁ BOLESLAV - MARTINOVICE		
Zhotovitel: Valbek, spol. s r.o. Vaňurova 505/17 460 07 Liberec 3	Příloha	TVAR PILÍŘŮ P2,P3	203	
			Počet formátů	8x A4
			Měřítko	1:50
			Č. přílohy	Paré