
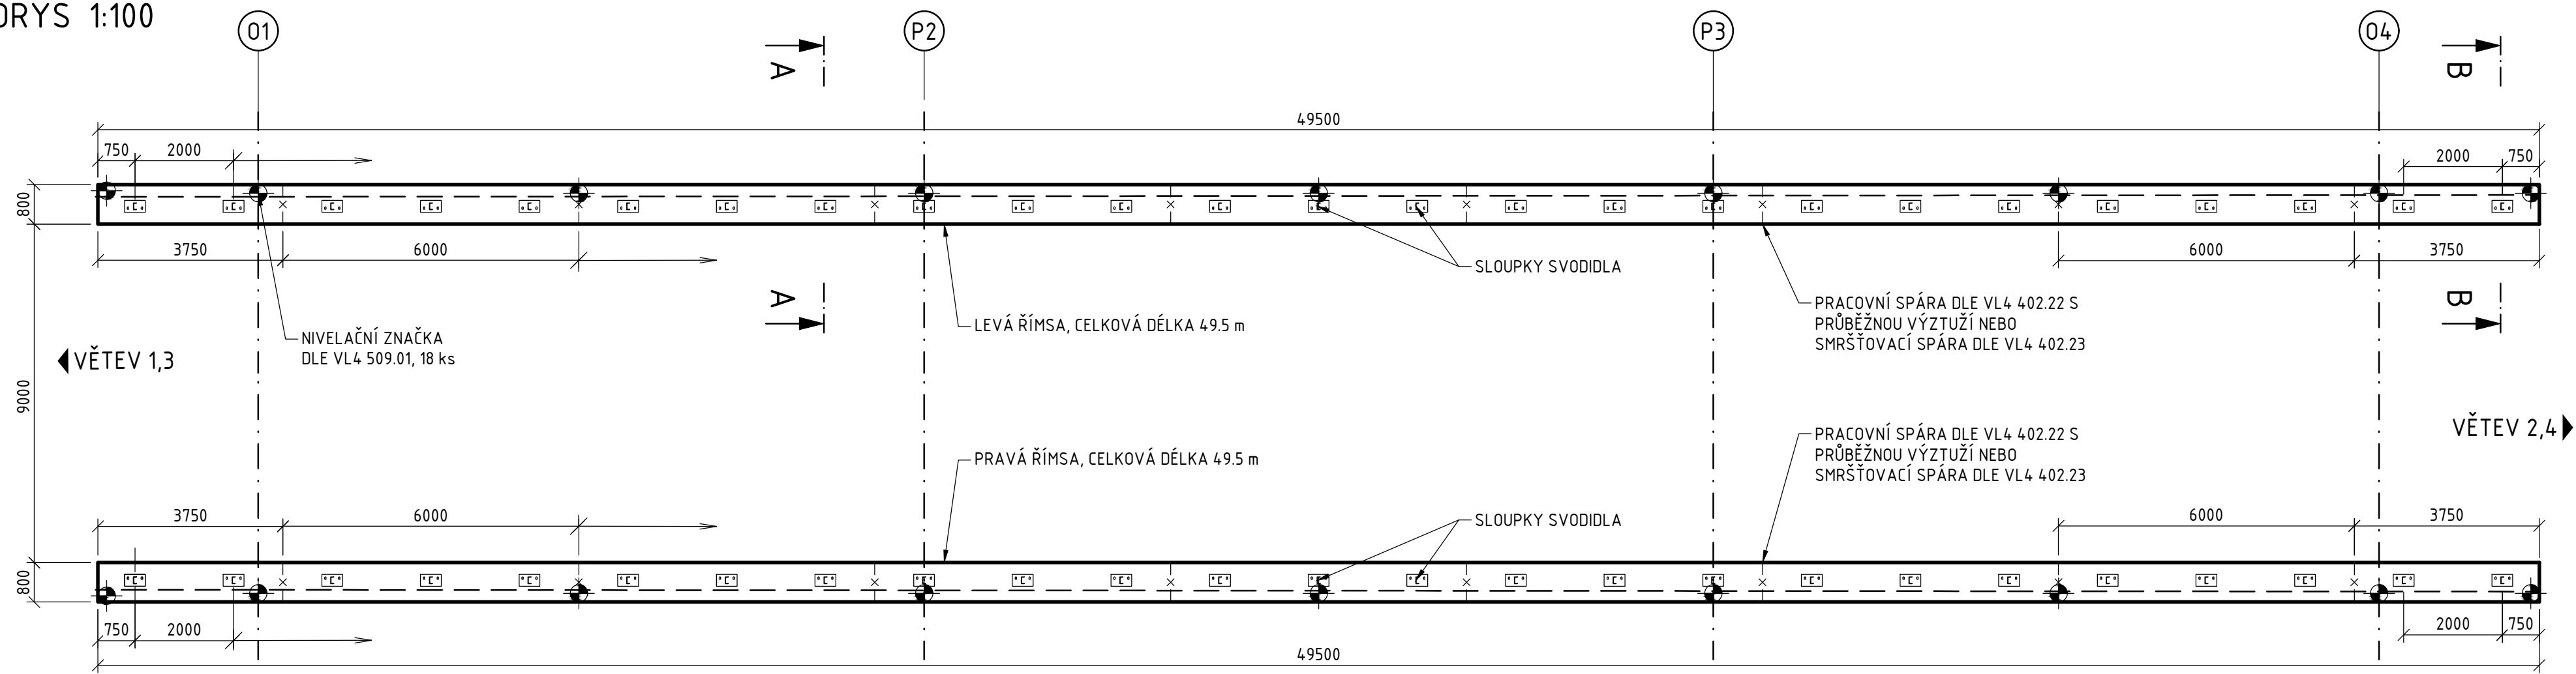
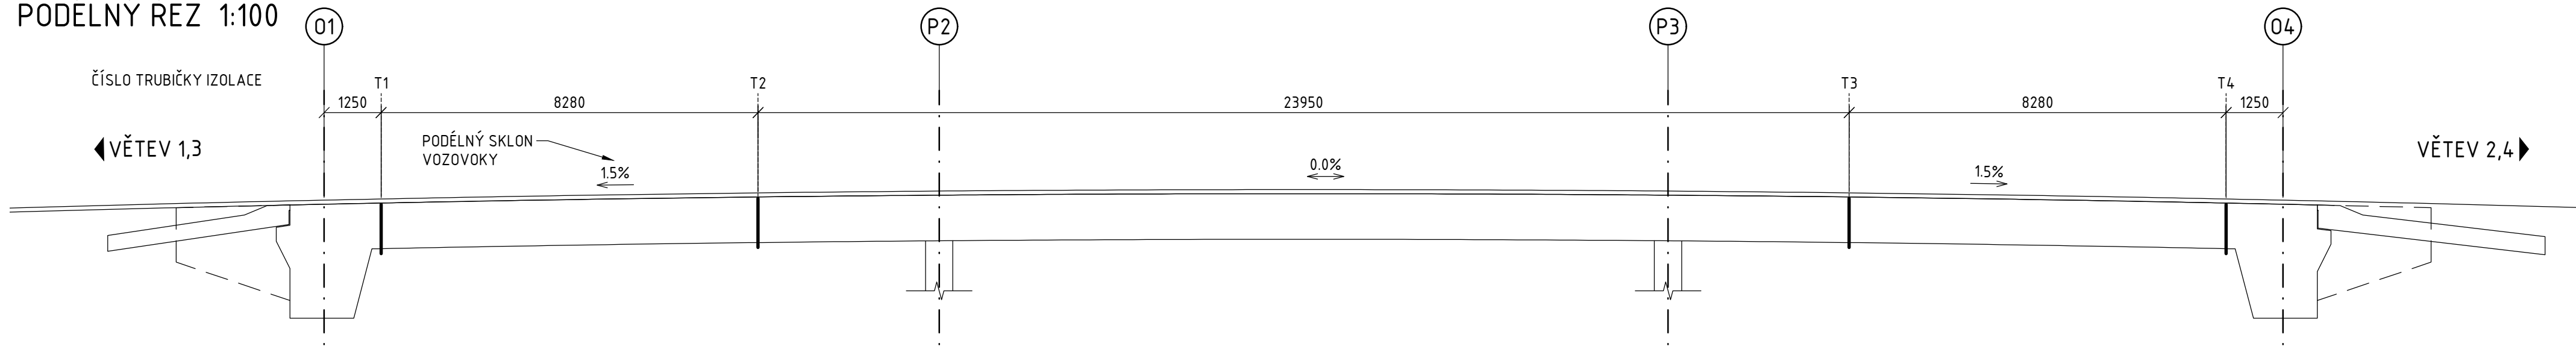


PŮDORYS 1:100


SCHÉMA ODVODNĚNÍ
PODÉLNÝ ŘEZ 1:100

PŮDORYS VYTYČENÍ 1:200

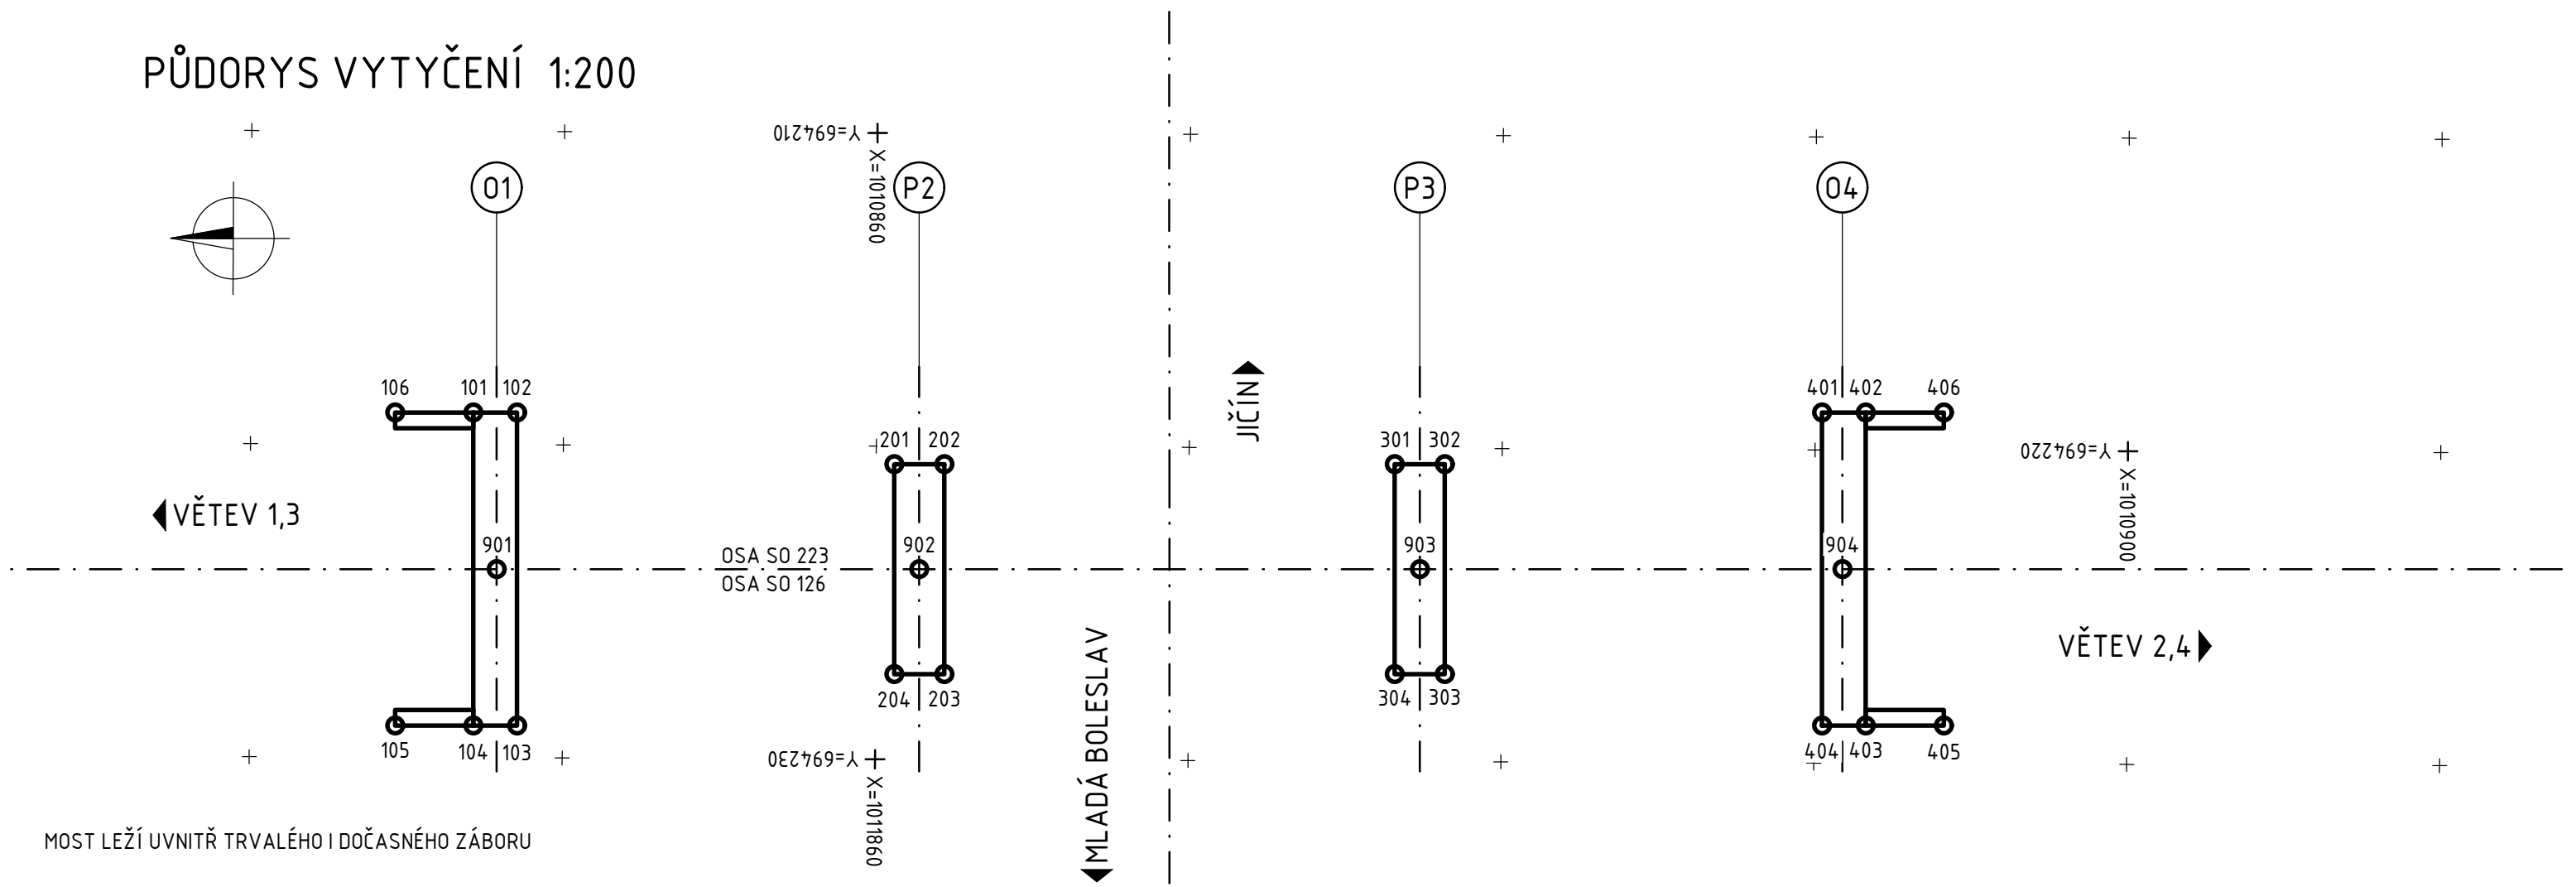


PŘECHODOVÉ OBLASTI, PODÉLNÝ ŘEZ 1:100


PŘECHODOVÉ OBLASTI S VLEČENOU PŘECHODOVOU DESKOU DLE VL4 201.07 A ČSN 73 6244

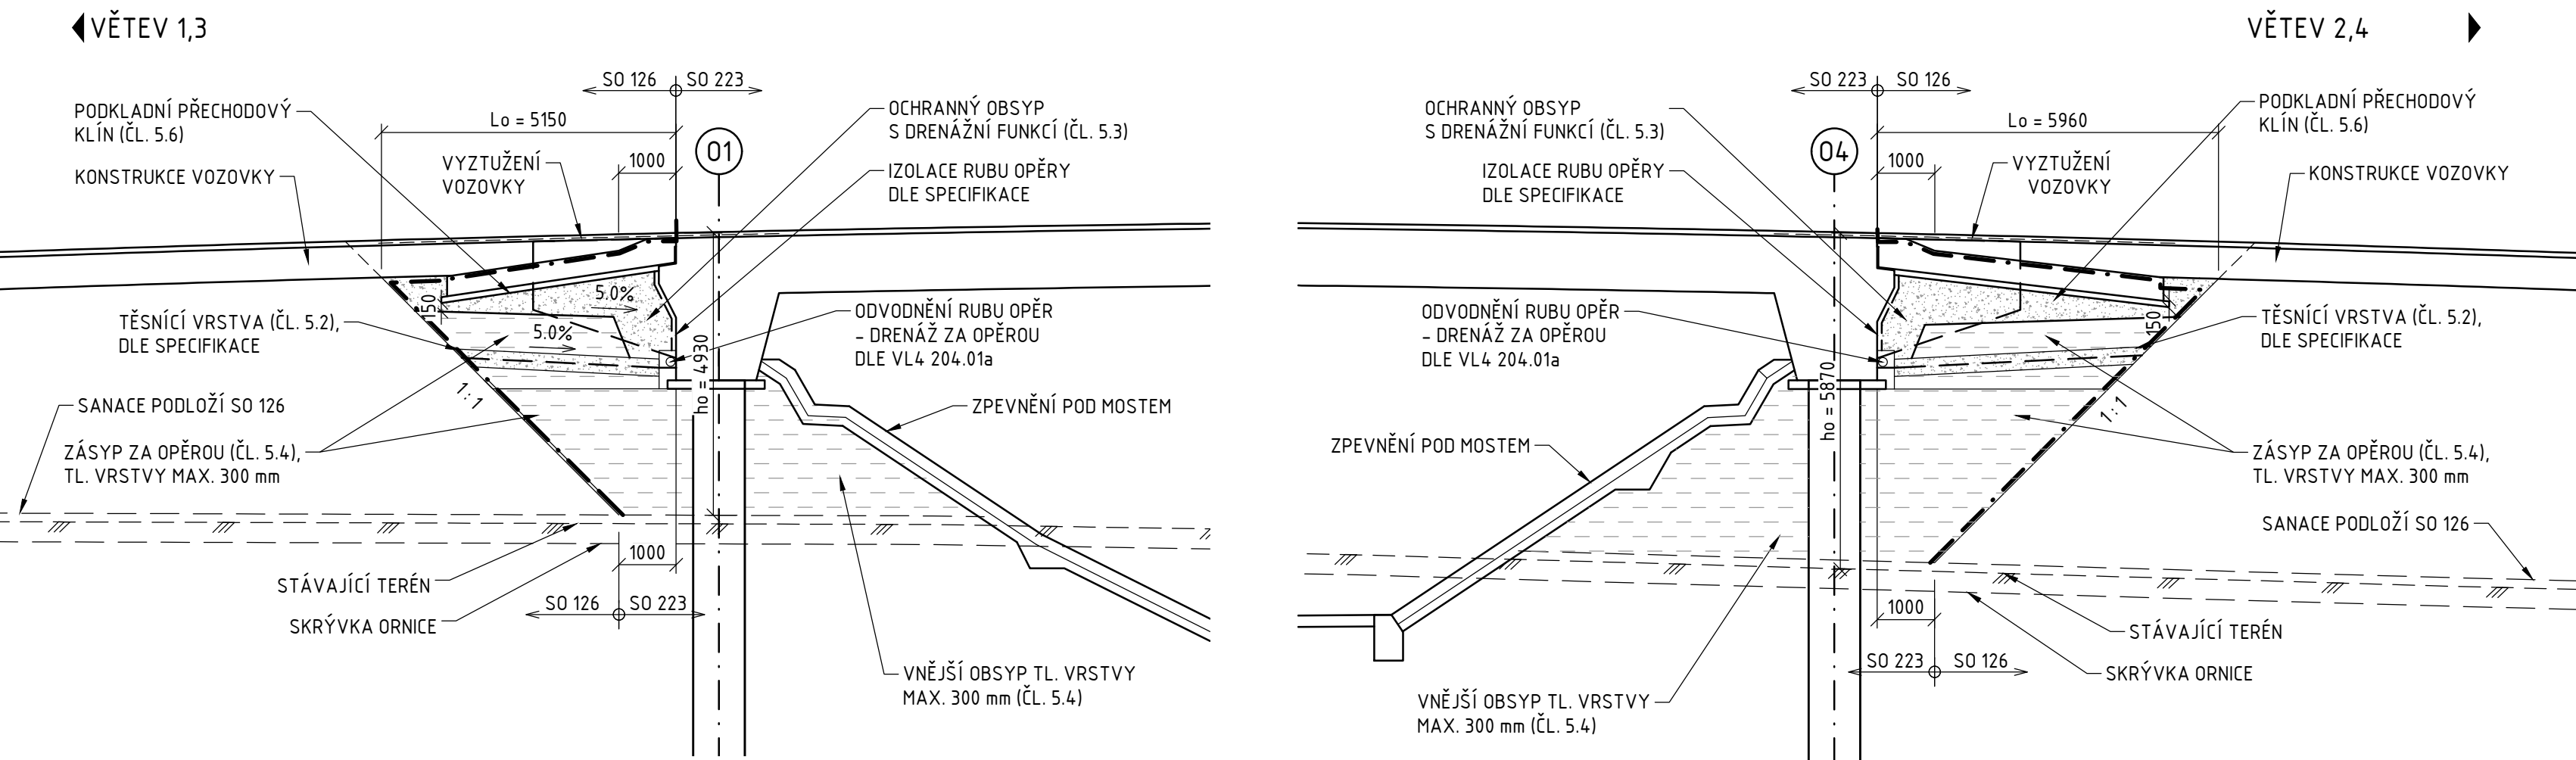


ŘEZ A-A 1:20

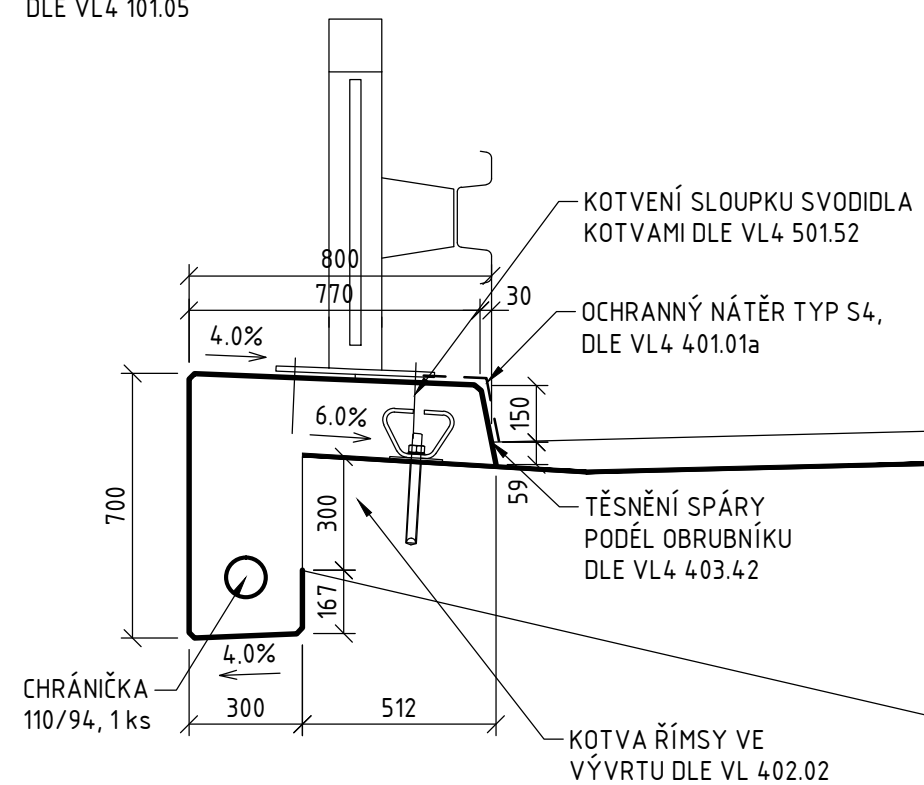KRAJNÍ ŘÍMSA SE ZÁBRADELNÍM SVODIDLEM
DLE VL4 101.05

ŘEZ B-B 1:20

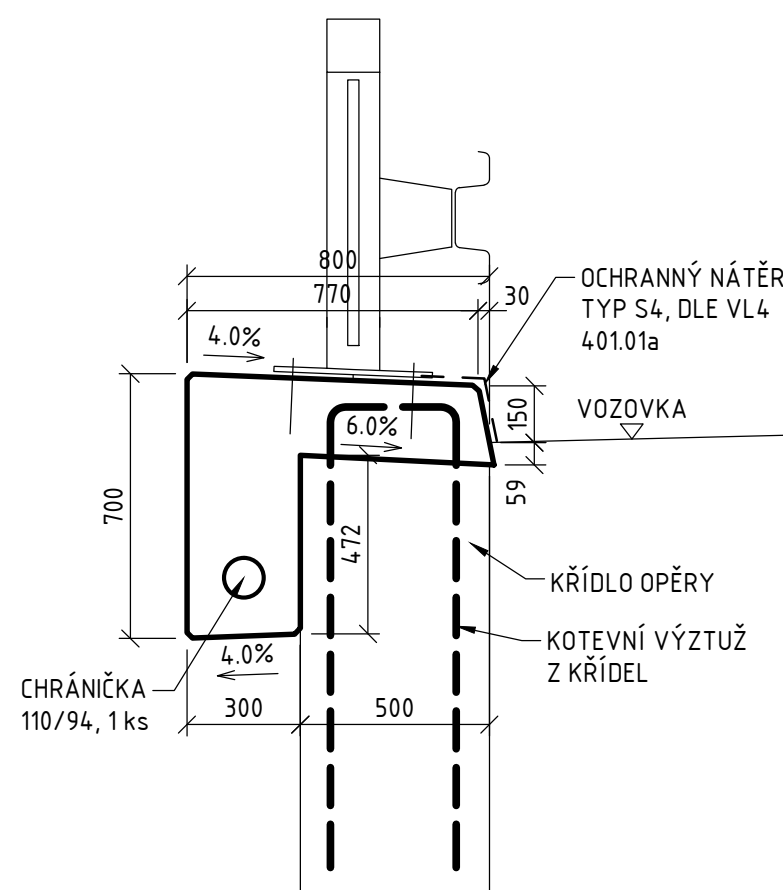

PŘÍČNÝ ŘEZ 1:50

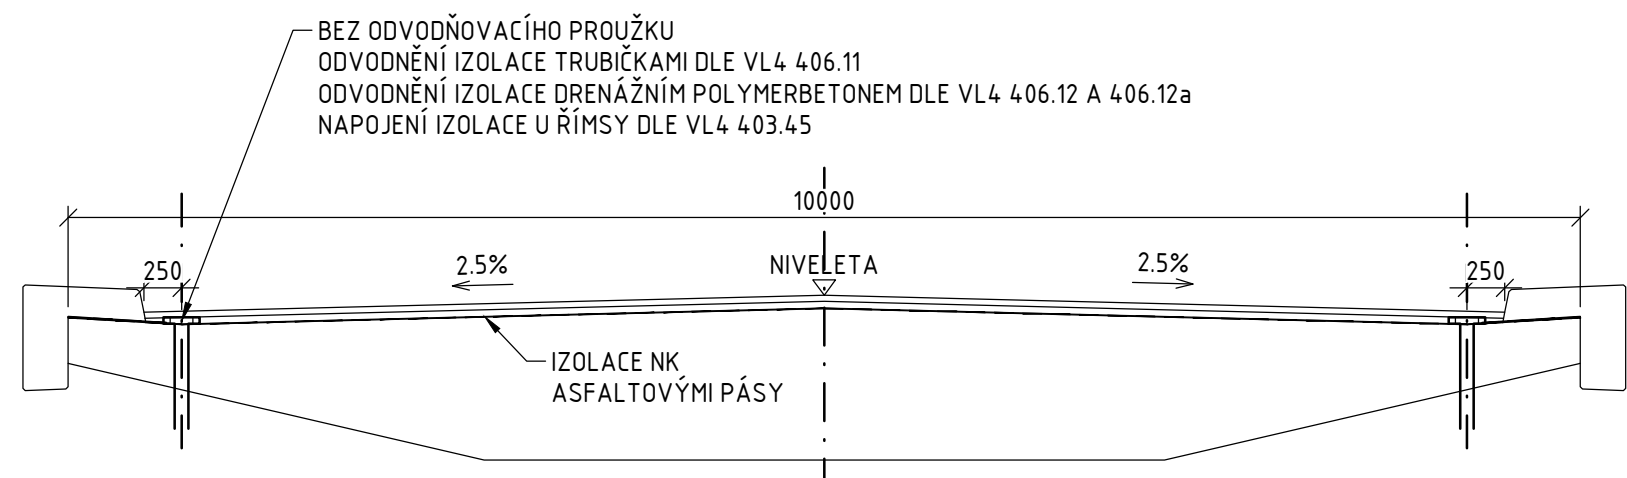

POZNÁMKY:

- VYTYČOVACÍ ODCHYLKY: VIZ PŘÍLOHA E.4.5.1 - GVS - SEZNAM SOUŘADNIC
- NEDÍLNOU SOUČÁSTÍ VÝKRESU JSOU POZNÁMKY A SPECIFIKACE UVEDENÉ NA VÝKRESE POZNÁMEK A TECHNICKÝCH SPECIFIKACÍ

SOUŘADNICE VB

BOD	Y [m]	X [m]	Z [m]
901	694223.979	101084.7.885	-
902	694223.923	1010861.385	-
903	694223.858	1010877.385	-
904	694223.802	1010890.885	-
101	694218.982	101084.7.114	228.279
102	694218.976	1010848.514	228.279
103	694228.976	1010848.555	228.279
104	694228.982	101084.7.155	228.279
105	694228.992	1010844.655	230.704
106	694218.992	1010844.614	230.704
201	694220.577	1010860.571	222.038
202	694220.570	1010862.171	222.038
203	694227.270	1010862.199	222.038
204	694227.276	1010860.599	222.038
301	694220.511	1010876.571	222.038
302	694220.504	1010878.171	222.038
303	694227.204	1010878.198	222.038
304	694227.211	1010876.598	222.038
401	694218.805	1010890.214	228.279
402	694218.799	1010891.614	228.279
403	694228.799	1010891.655	228.279
404	694228.805	1010890.255	228.279
405	694228.789	1010894.155	230.704
406	694218.789	1010894.114	230.704

Souřadnicový systém: S-JTSK
Výškový systém: Bpv

SO 223 NADJEZD MŮK MARTINOVICE V KM 7,320

Objednatel:

Ředitelství silnic a dálnic s. p.
Čerčanská 2023/12, Krč, 140 00 Praha 4Valbek, spol. s r.o.
Vaňurova 505/17
460 07 Liberec 3

Vypracoval	M. KNESPLOVÁ	Zak. číslo	21-L113-001
Zodp. projektant	ING. S. RŮŽIČKA	Datum	02/2025
Tech. kontrola	ING. I. BELDA	Stupeň	PDP5
Akce		Počet formátů	8x A4
		Měřítko	1:200, 100, 50, 20
		Č. přílohy	Paré
Zhotovitel:	Příloha		
Valbek, spol. s r.o. Vaňurova 505/17 460 07 Liberec 3	TVAR ŘÍMS, SCHÉMA ODVODNĚNÍ, PŘECHODOVÉ OBLASTI, VYTYČENÍ		
		204	