




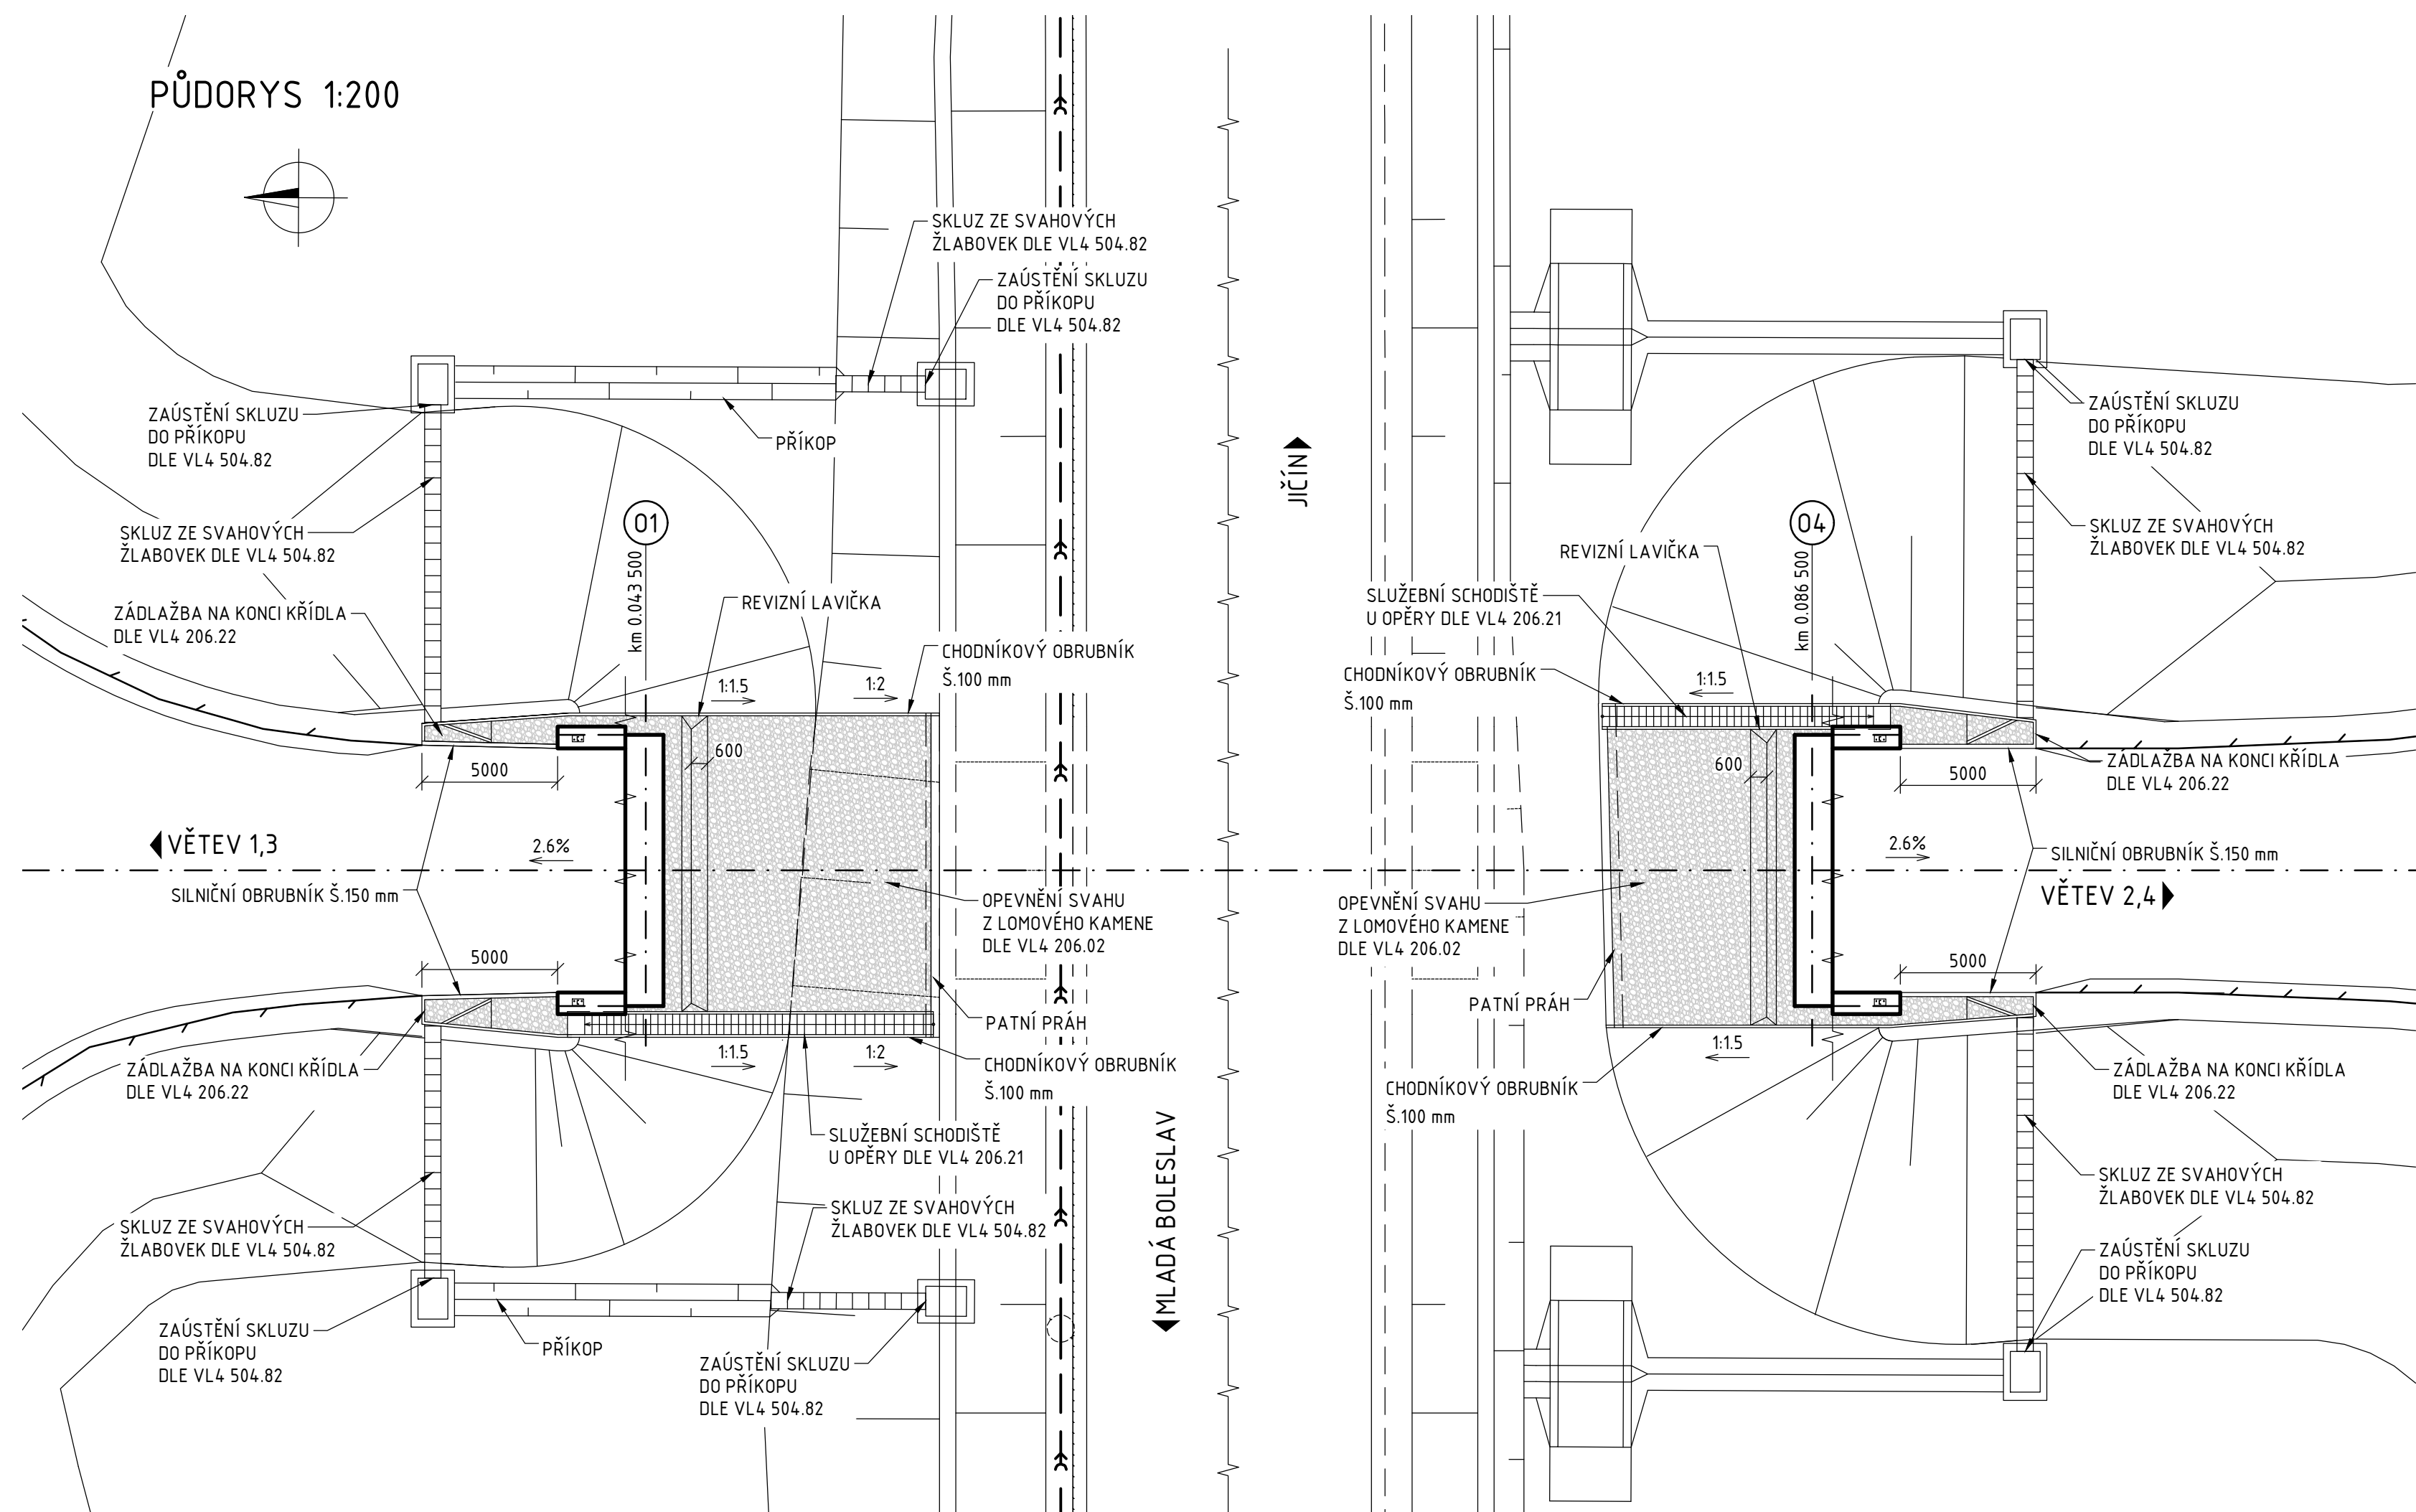


SLUŽEBNÍ SCHODIŠTĚ PODÉL KŘÍDLA OPĚRY 01 1: 100
VĚTEV 1,3

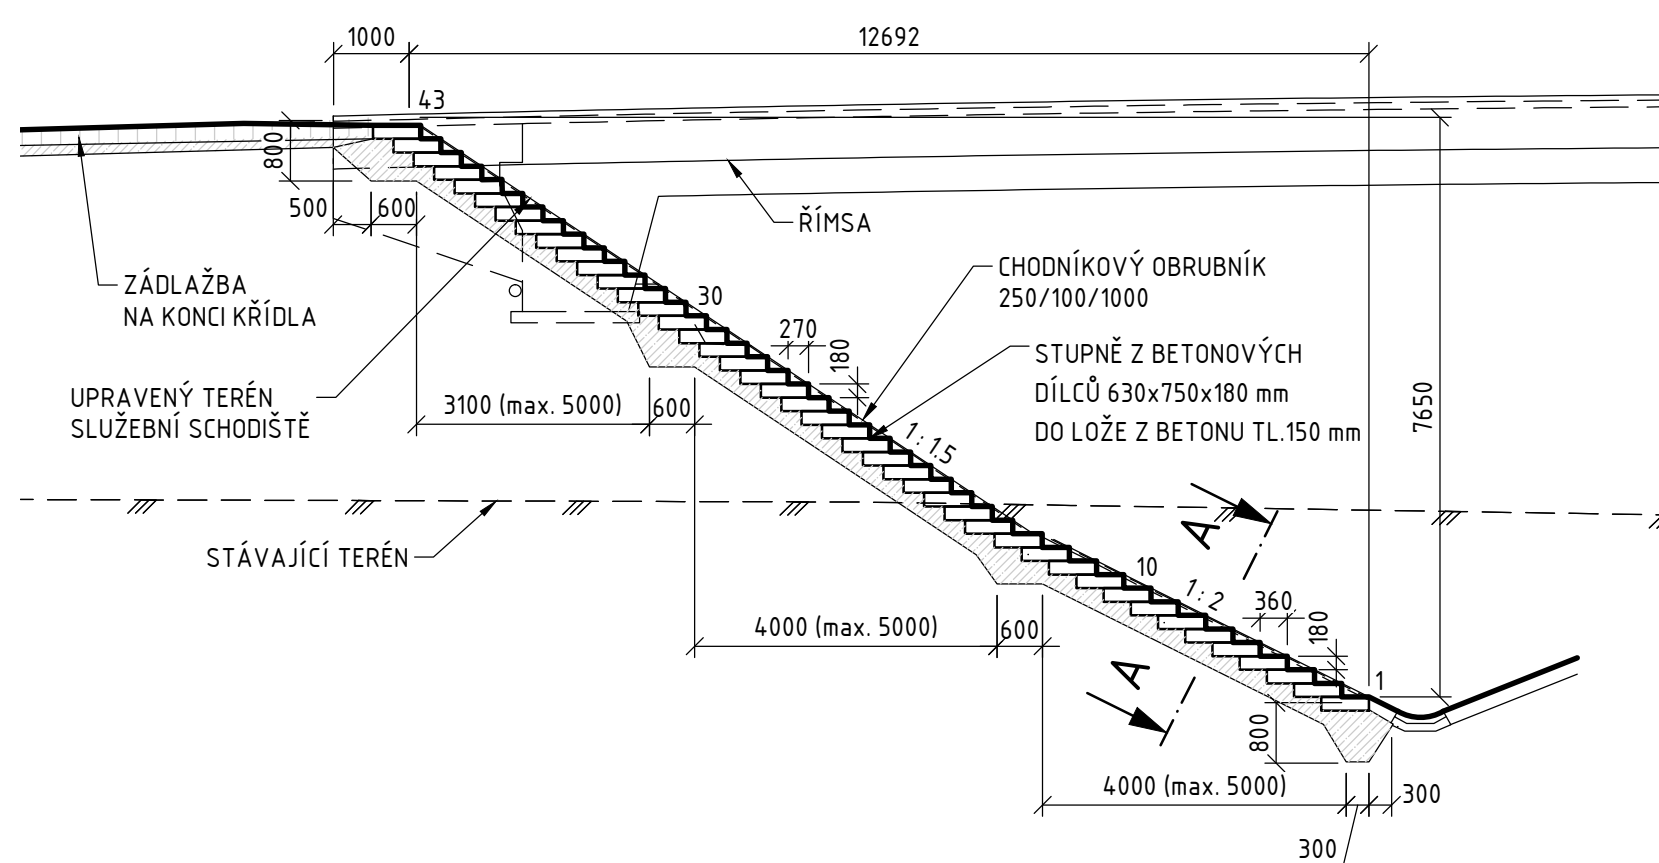


PODÉLNÝ ŘEZ ODLÁŽDĚNÍM POD MOSTEM
OPĚRA 01 1:100

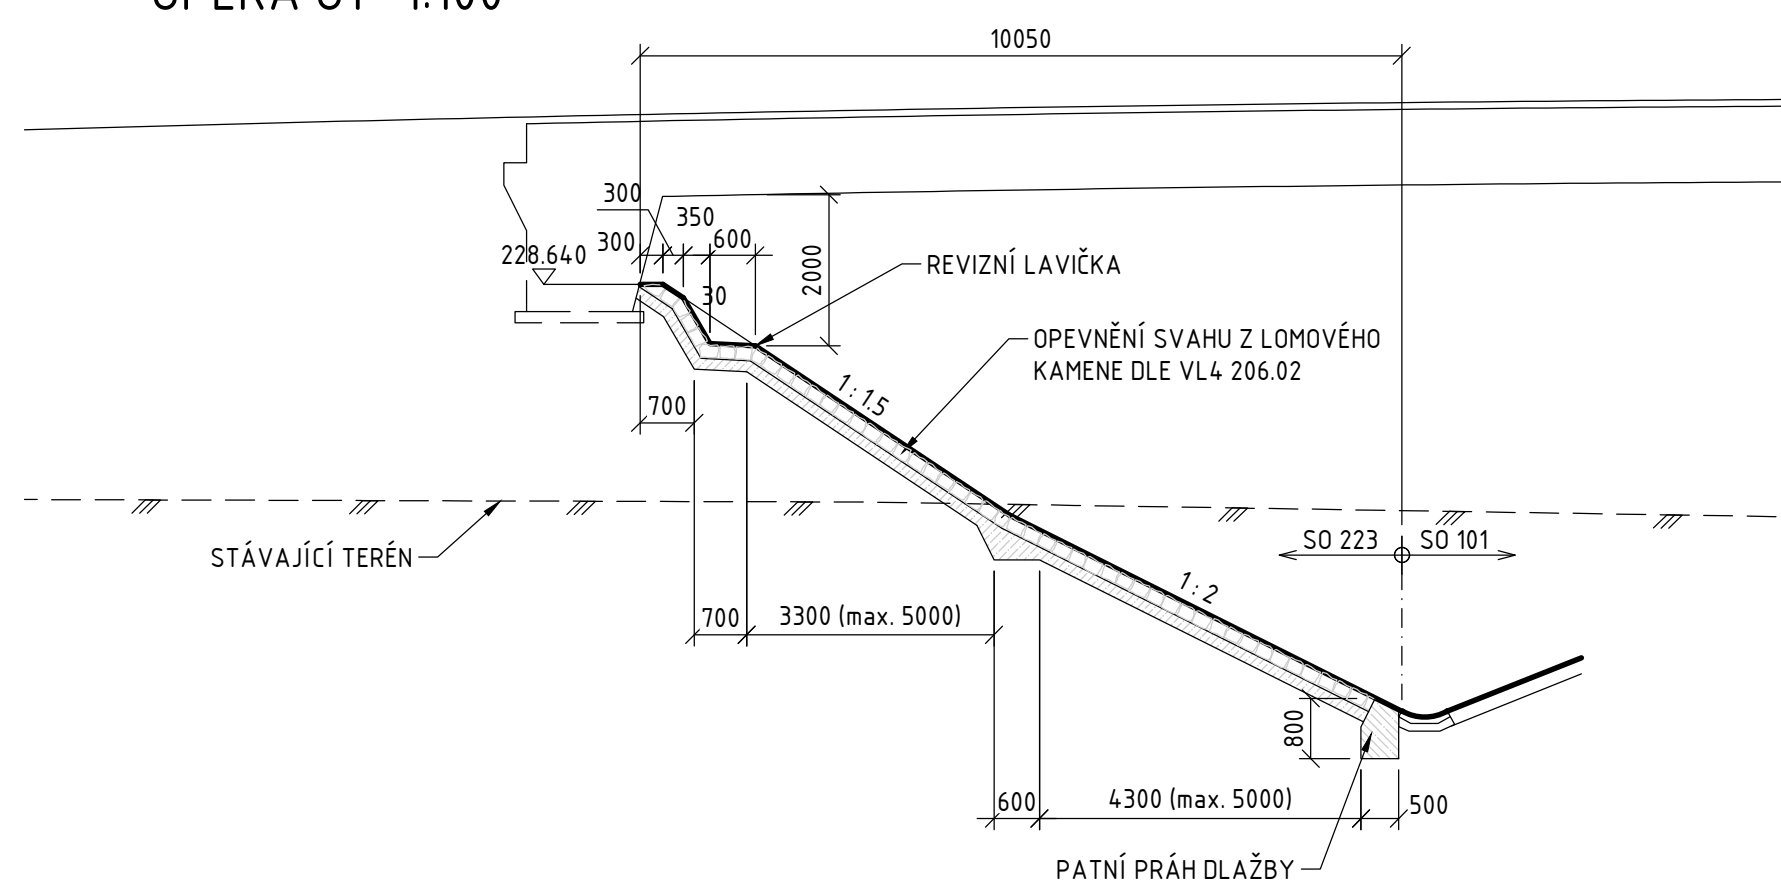



SLUŽEBNÍ SCHODIŠTĚ PODÉL KŘÍDLA OPĚRY 04 1: 100
VĚTEV 2,4

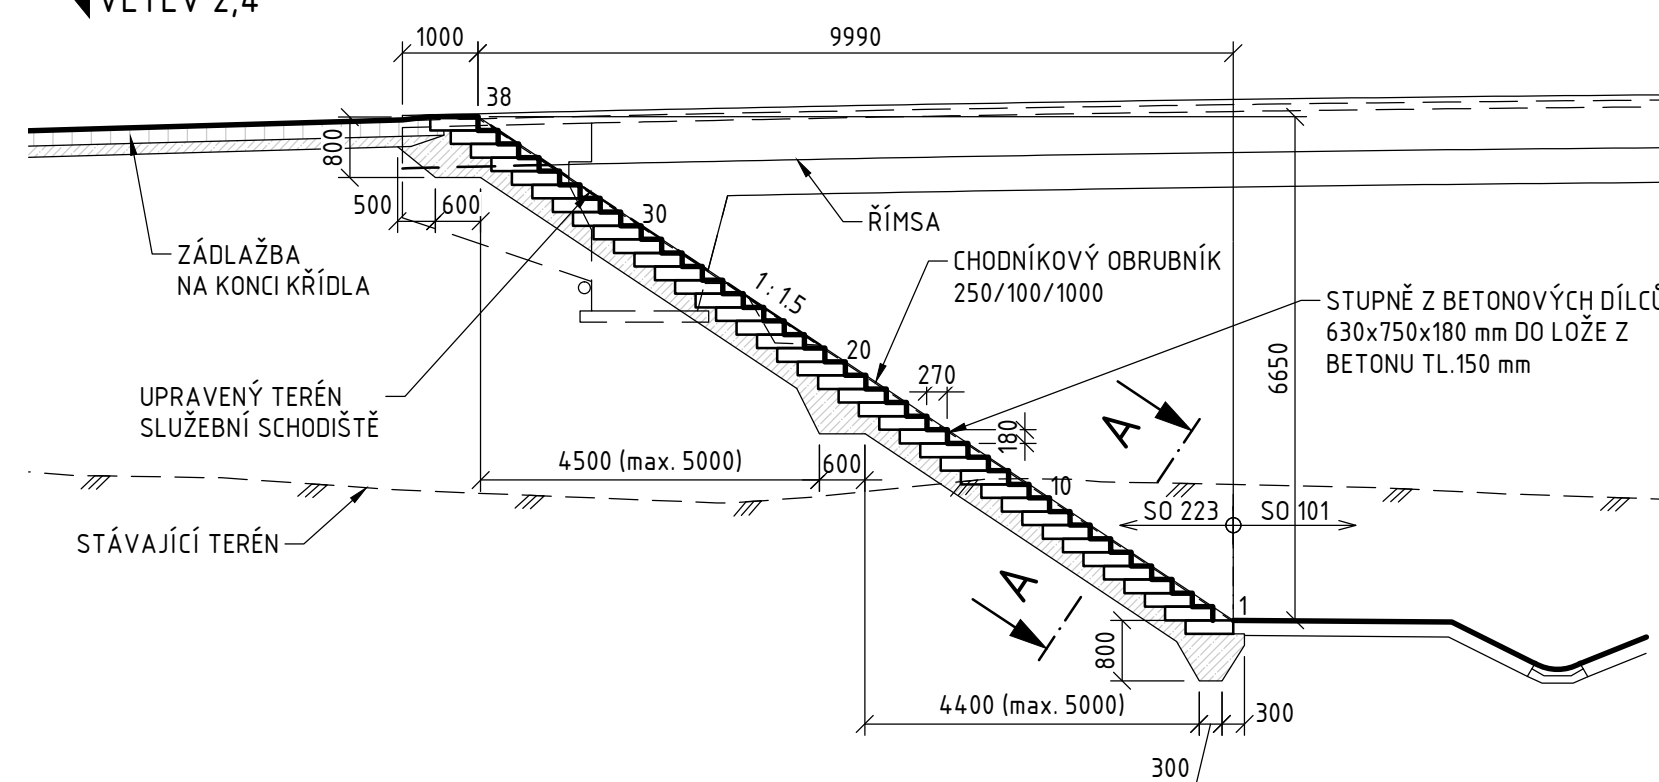

PODÉLNÝ ŘEZ ODLÁŽDĚNÍM POD MOSTEM
OPĚRA 04 1:100

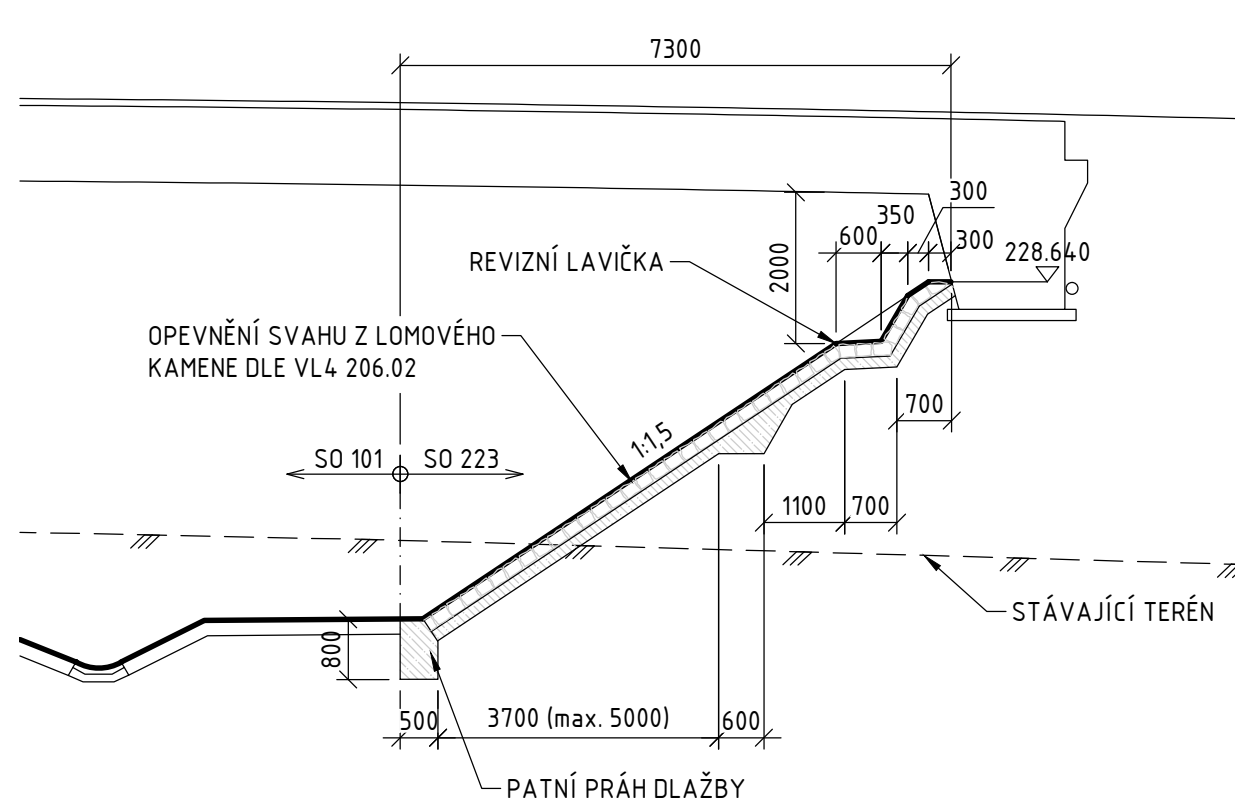

ŘEZ A-A 1:25

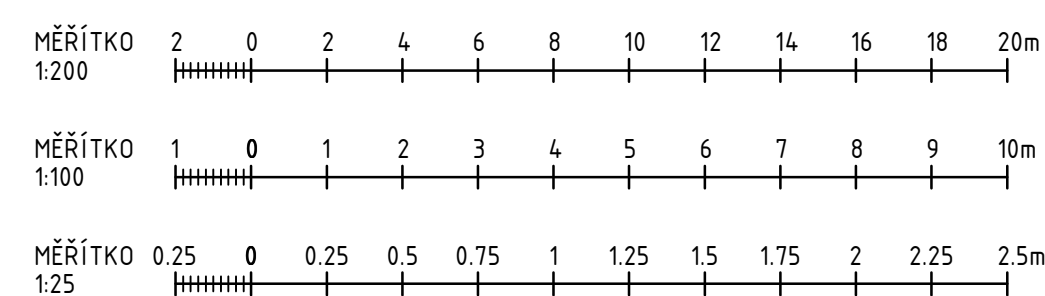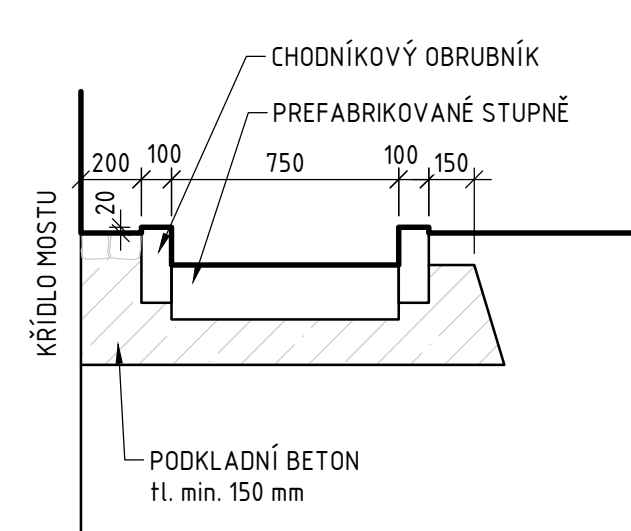

POZNÁMKY:

- NEDÍLNOU SOUČÁSTÍ VÝKRESU JSOU POZNÁMKY A SPECIFIKACE UVEDENÉ NA VÝKRESE POZNÁMEK A TECHNICKÝCH SPECIFIKACÍ

Souřadnicový systém: S-JTSK
Výškový systém: Bpv

SO 223 NADJEZD MŮK MARTINOVICE V KM 7,320

Objednatel: Ředitelství silnic a dálnic
Ředitelství silnic a dálnic s. p.
Čerčanská 2023/12, Krč, 140 00 Praha 4

Valbek, spol. s r.o.
Vaňurova 505/17
460 07 Liberec 3

Vypracoval: M. KNESPOVÁ
Zodp. projektant: ING. S. RŮŽIČKA
Tech. kontrola: ING. I. BELDA
Akce: I/16 MLADÁ BOLESLAV - MARTINOVICE
Zhotovitel: Valbek, spol. s r.o.
Vaňurova 505/17
460 07 Liberec 3
Příloha: ÚPRAVY POD MOSTEM, SLUŽEBNÍ SCHODIŠTĚ
Zak. číslo: 21-L113-001
Datum: 02/2025
Stupeň: PDPS
Počet formátů: 8x A4
Měřítko: 1:200, 100, 25
Č. přílohy: Paré
205