




SCHÉMA VÝZTUŽE ZÁKLADŮ PILÍŘŮ
PŘÍČNÝ ŘEZ A-A 1:50

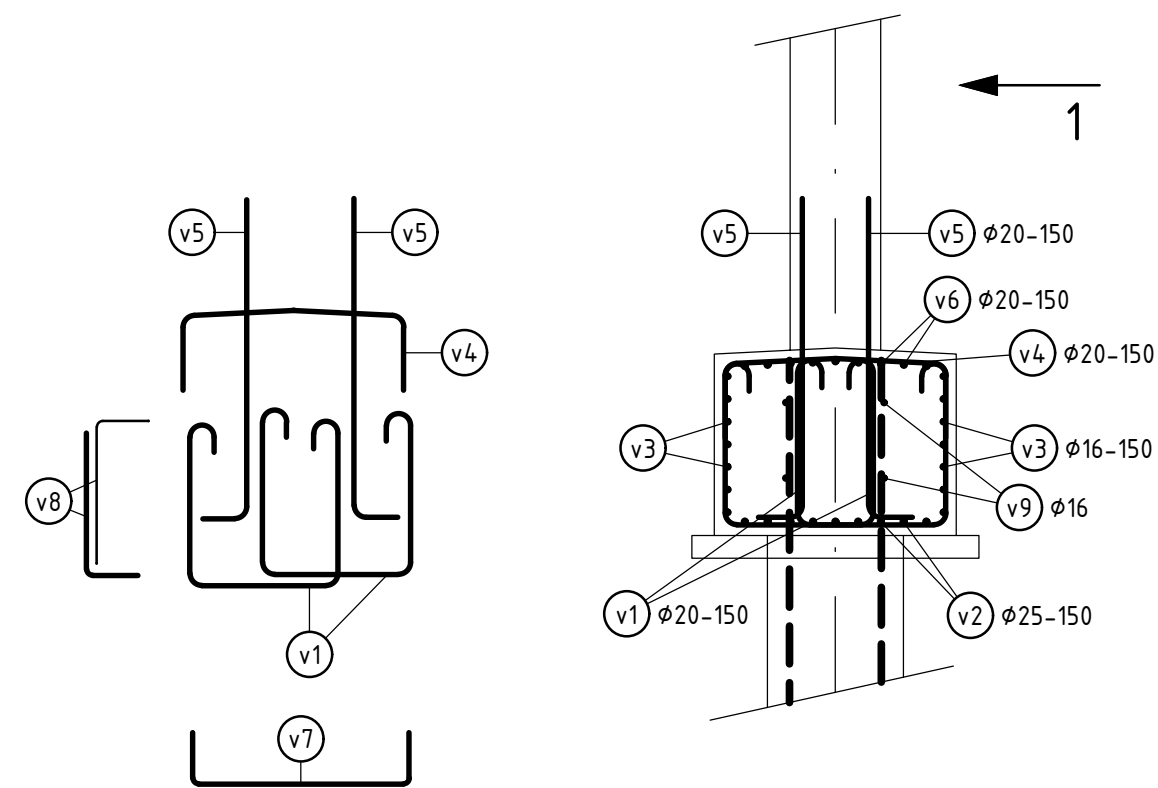


POHLED 1 1:50

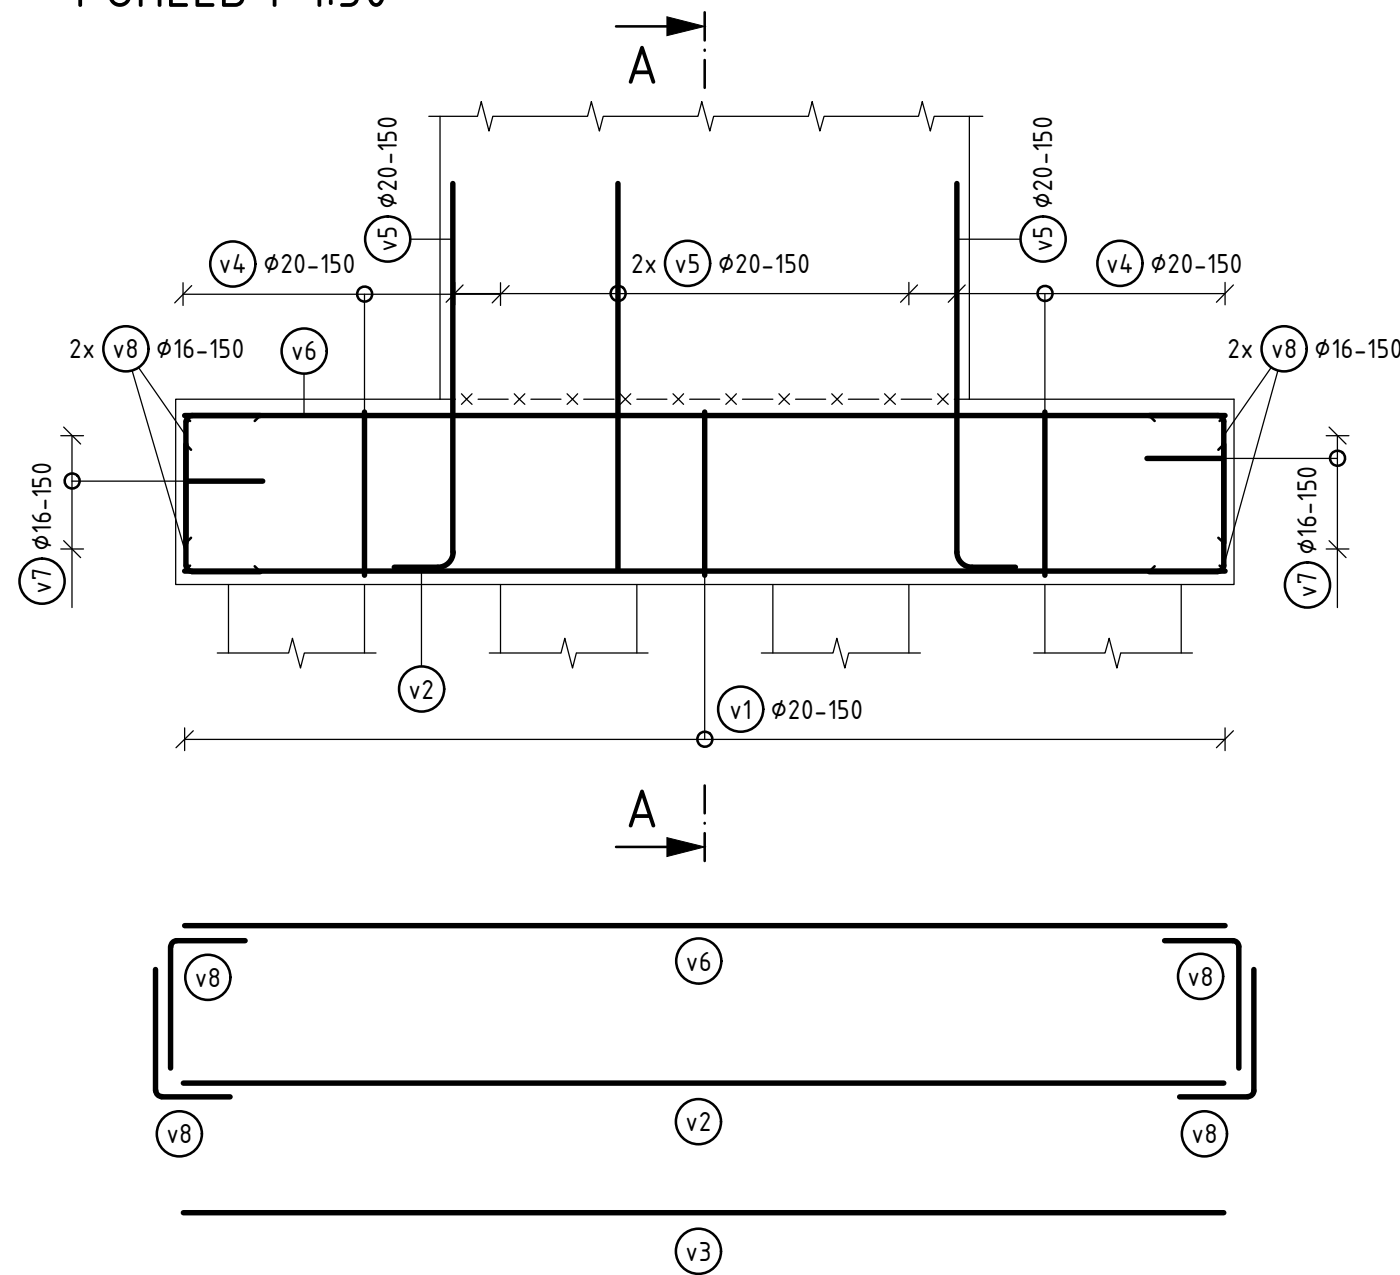

ŘEZ DŘÍKEM PILÍŘE 1:50

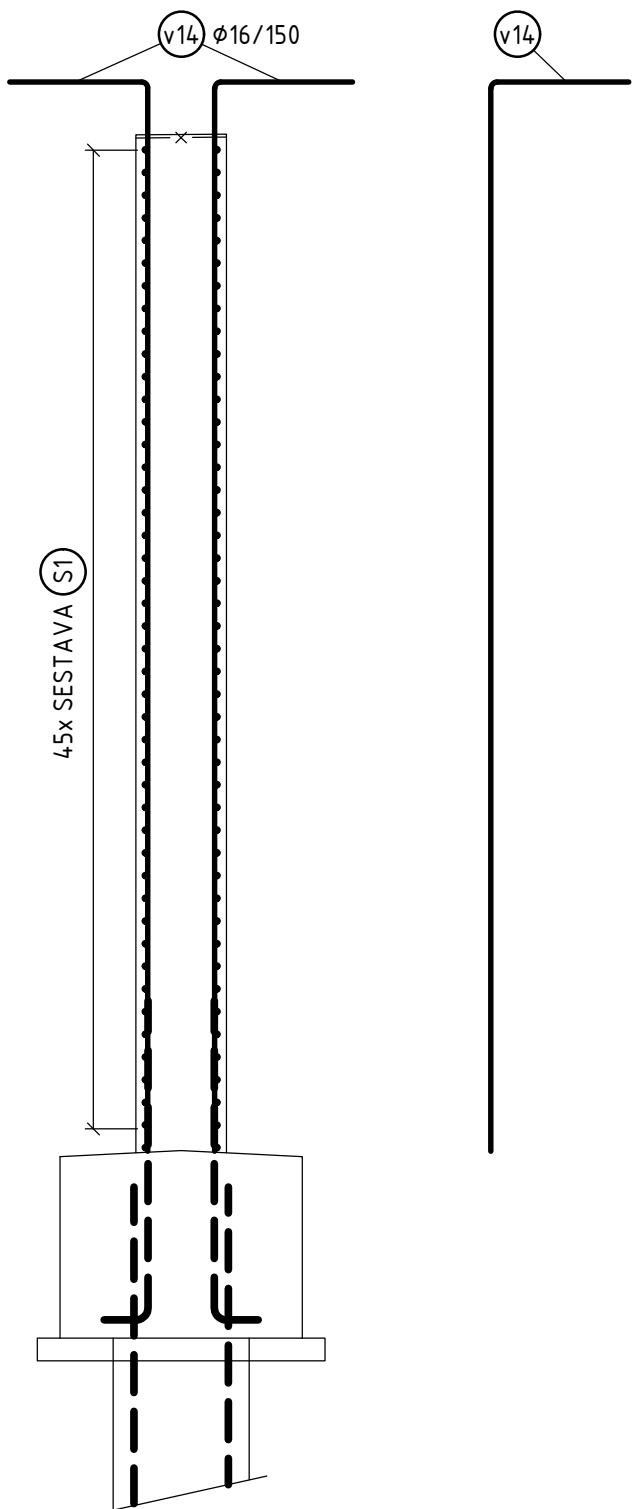


ŘEZ KŘÍDLEM 1:50

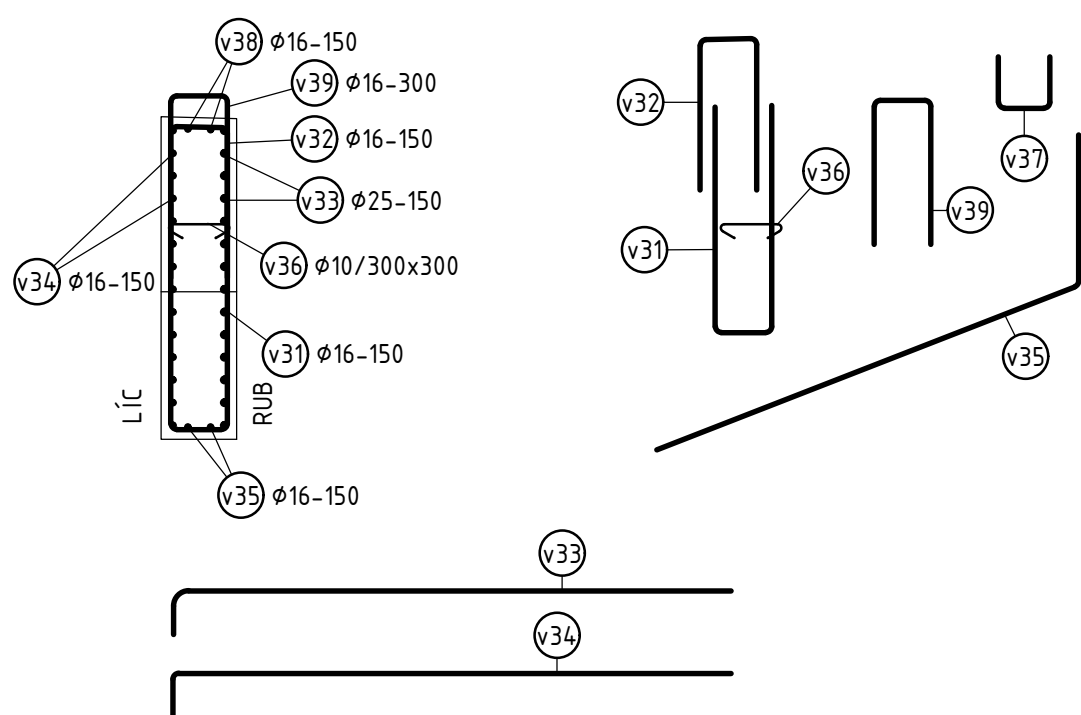


ODHAD MNOŽSTVÍ BETONÁŘSKÉ VÝZTUŽE SO 223	MNOŽSTVÍ VÝZTUŽE V %	MNOŽSTVÍ VÝZT. V KG/M3
VÝZTUŽ PILOT POD OPĚROU 1, D 900MM	1.44%	113.0
VÝZTUŽ PILOT POD OPĚROU 4, D 900MM	1.44%	113.0
VÝZTUŽ PILOT POD PILÍŘI, D 900MM	0.75%	59.0
VÝZTUŽ ZÁKLADŮ PILÍŘŮ	2.19%	172.0
VÝZTUŽ PILÍŘŮ	1.4%	110.0
VÝZTUŽ NOSNÉ KONSTRUKCE	1.98%	155.7
VÝZTUŽ ŘÍMS	1.65%	130.0
VÝZTUŽ PŘECHODOVÝCH DESEK	2.57%	201.8


SCHÉMA VÝZTUŽE NOSNÉ KONSTRUKCE
PŘÍČNÝ ŘEZ 1:25
V KRAJNÍM PŘÍČNÍKU

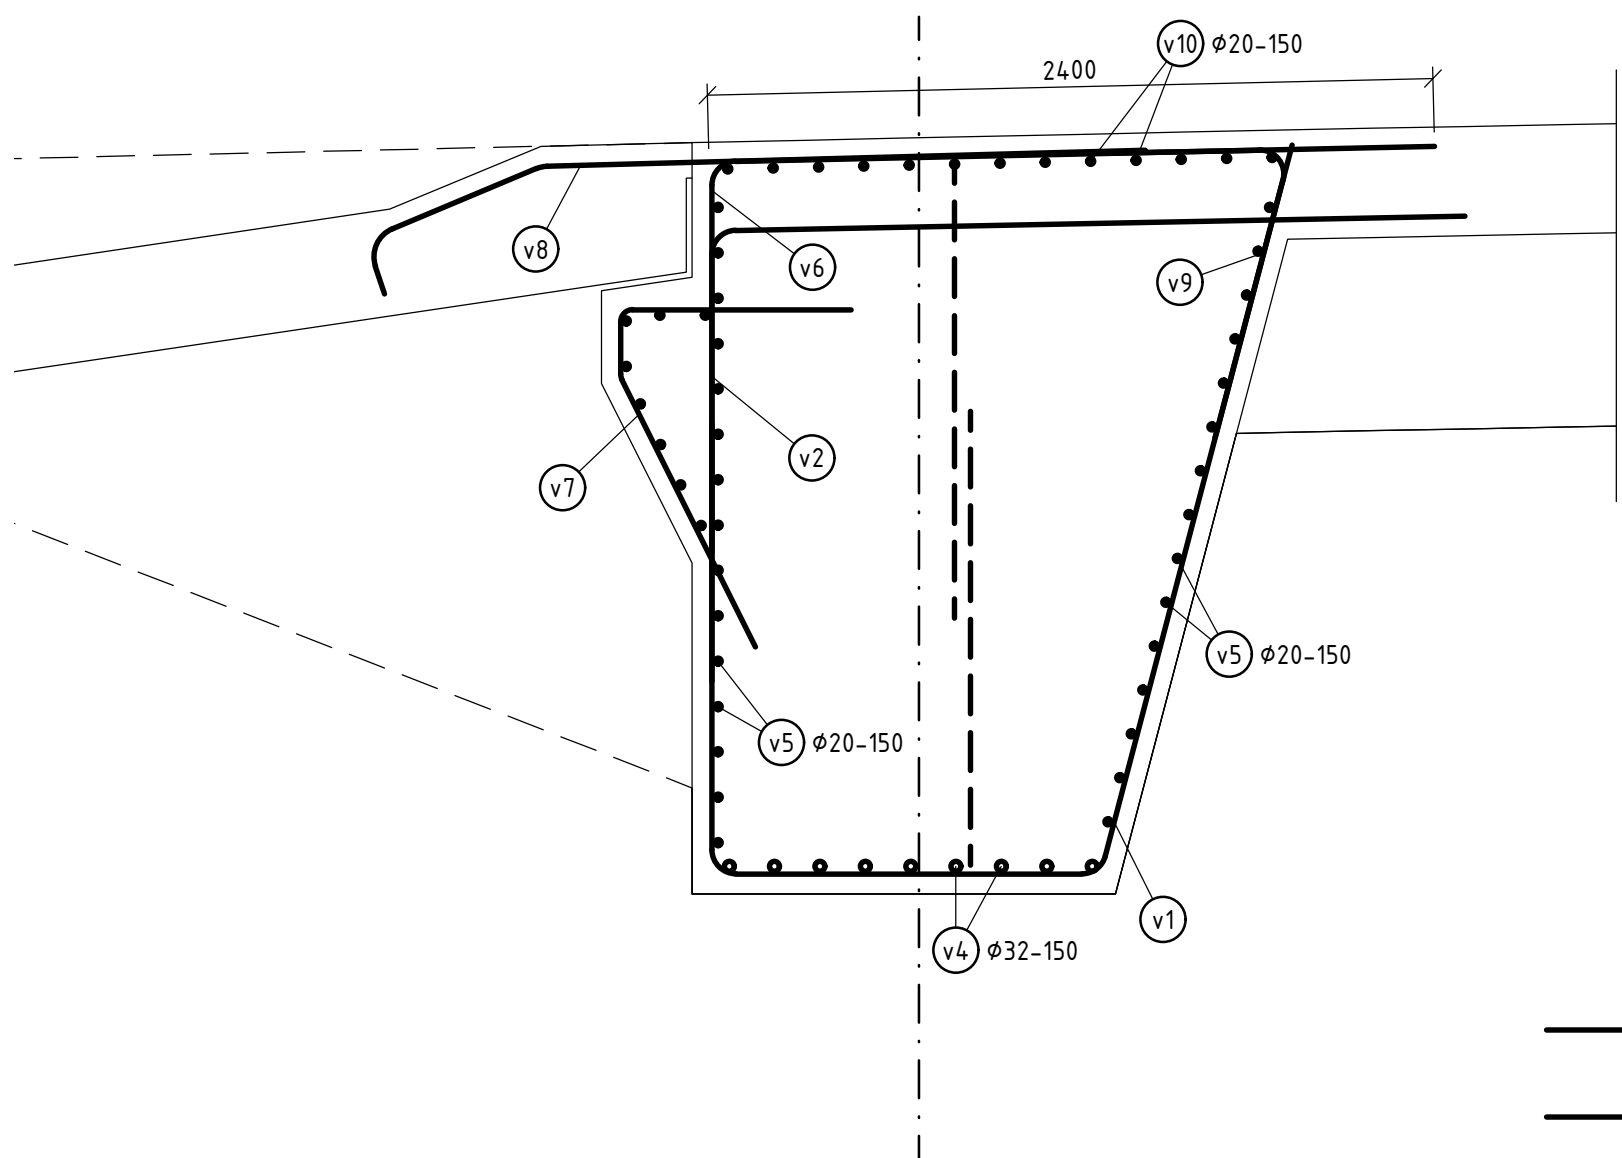

PŮDORYS DŘÍKU PILÍŘE 1:35

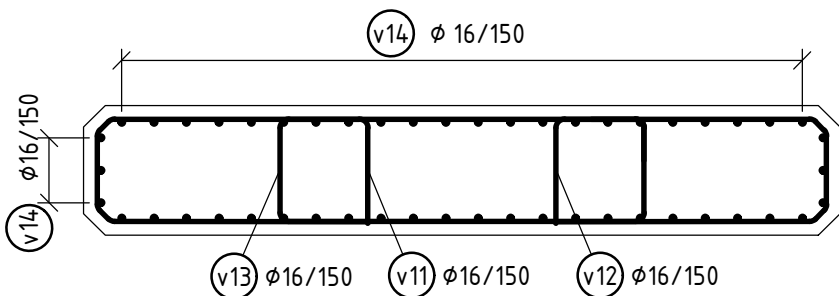

SESTAVA (S) OBSAHUJE POLOŽKY
Č. v11 - 1ks, v12 - 1ks, v13 - 1ks

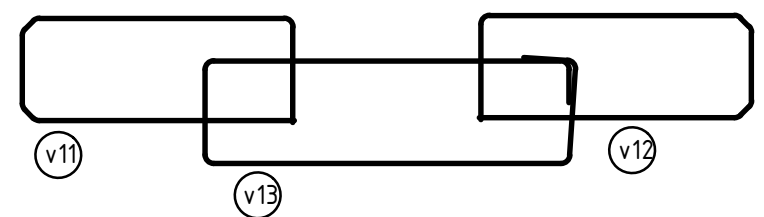

Souřadnicový systém: S-JTSK
Výškový systém: Bpv

SO 223 NADJEZD MŮK MARTINOVICE V KM 7,320

Objednatel:



Ředitelství silnic a dálnic s. p.
Čerčanská 2023/12, Krč, 140 00 Praha 4



Valbek, spol. s r.o.
Vaňurova 505/17
460 07 Liberec 3



Vypracoval	M. KNESPOVÁ	Zak. číslo	21-L113-001
Zodp. projektant	ING. S. RŮŽIČKA	Datum	02/2025
Tech. kontrola	ING. I. BELDA	Stupeň	PDPS
Akce	I/16 MLADÁ BOLESLAV - MARTINOVICE	Počet formátů	8x A4
Zhotovitel:	Příloha	Měřítko	-
Valbek, spol. s r.o. Vaňurova 505/17 460 07 Liberec 3	SCHÉMATICKÉ VÝKRESY VÝZTUŽE 1(2)	Č. přílohy	Paré
		301	