

SCHÉMA VÝZTUŽE NK
VÝZTUŽ V PODÉLNÉM SMĚRU 1:100

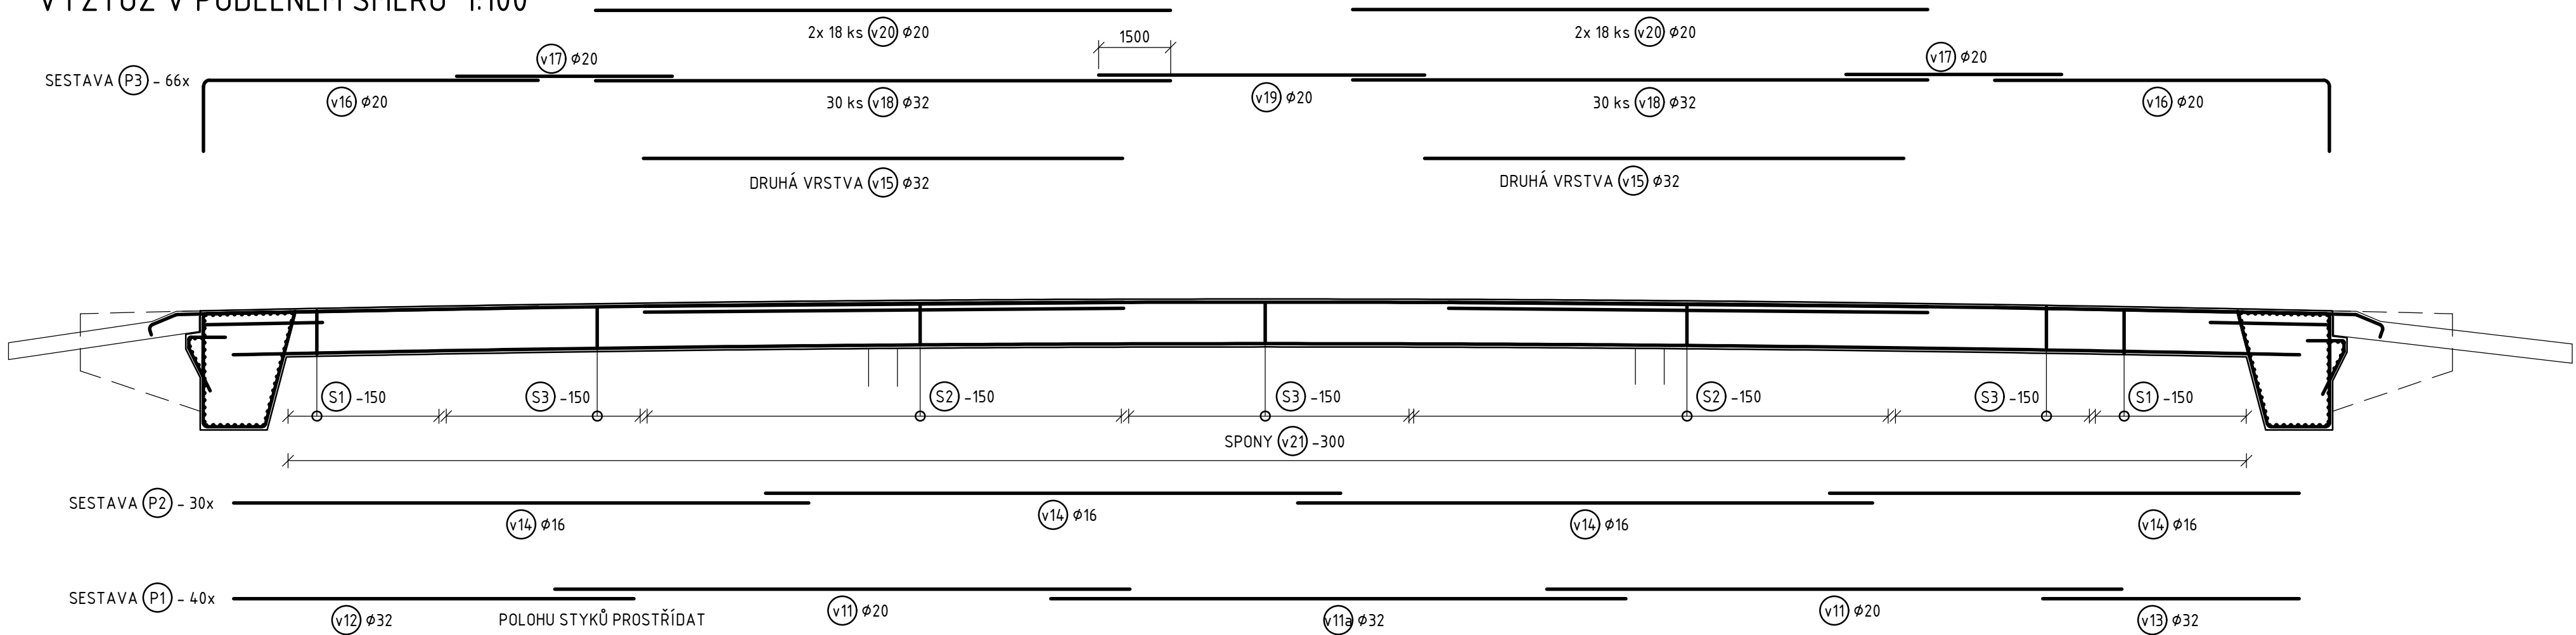


SCHÉMA VÝZTUŽE NOSNÉ KONSTRUKCE
PŘÍČNÝ ŘEZ PŘED OPĚROU 1:50

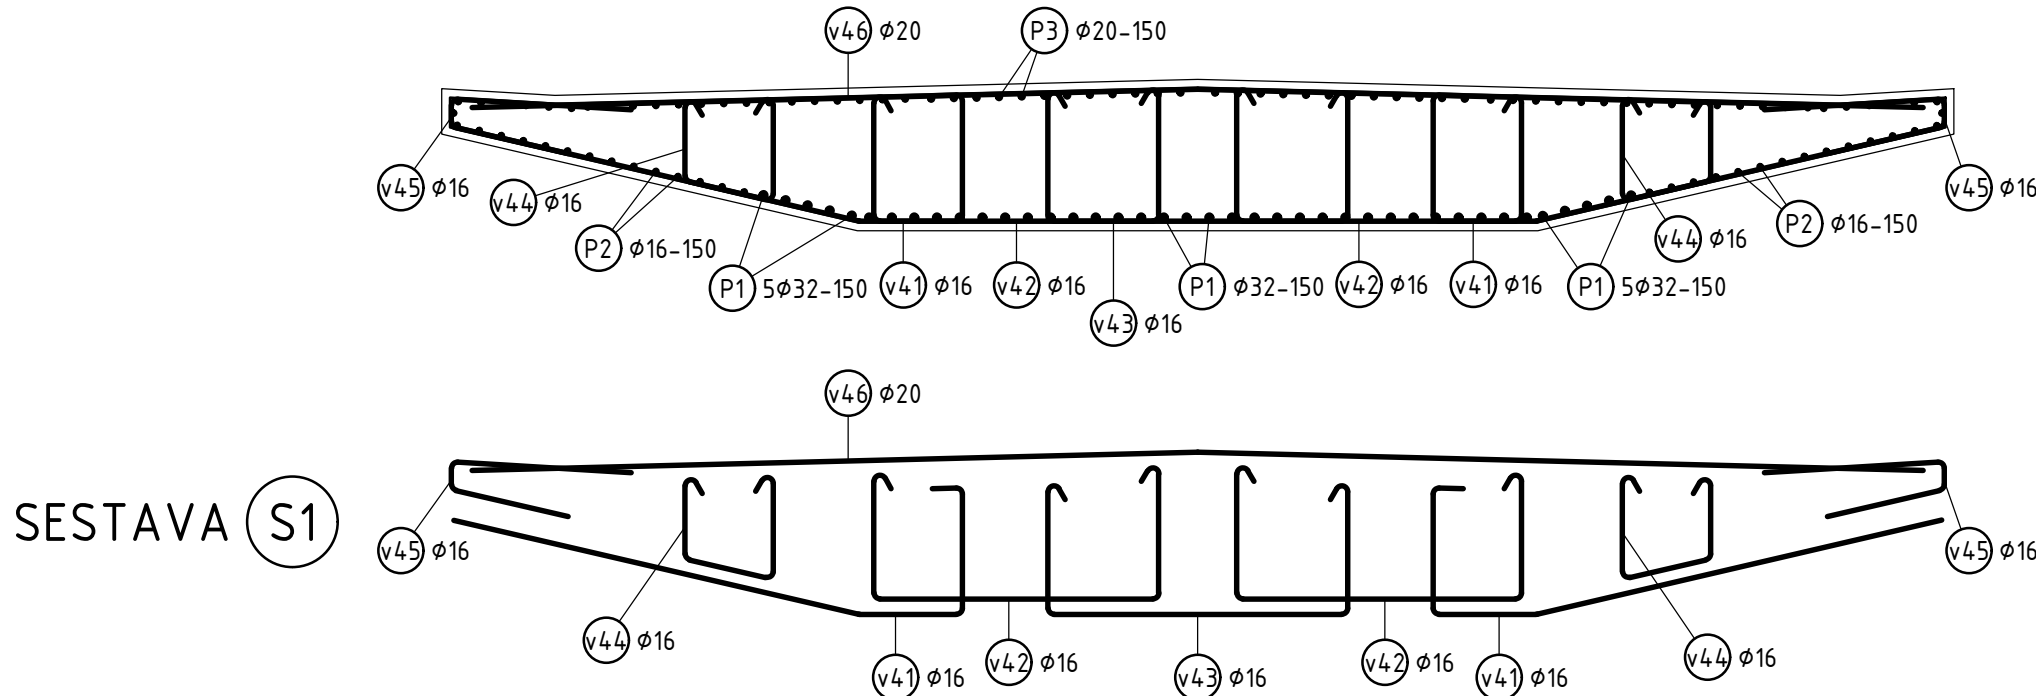


SCHÉMA VÝZTUŽE NOSNÉ KONSTRUKCE
PŘÍČNÝ ŘEZ V POLI 1:50


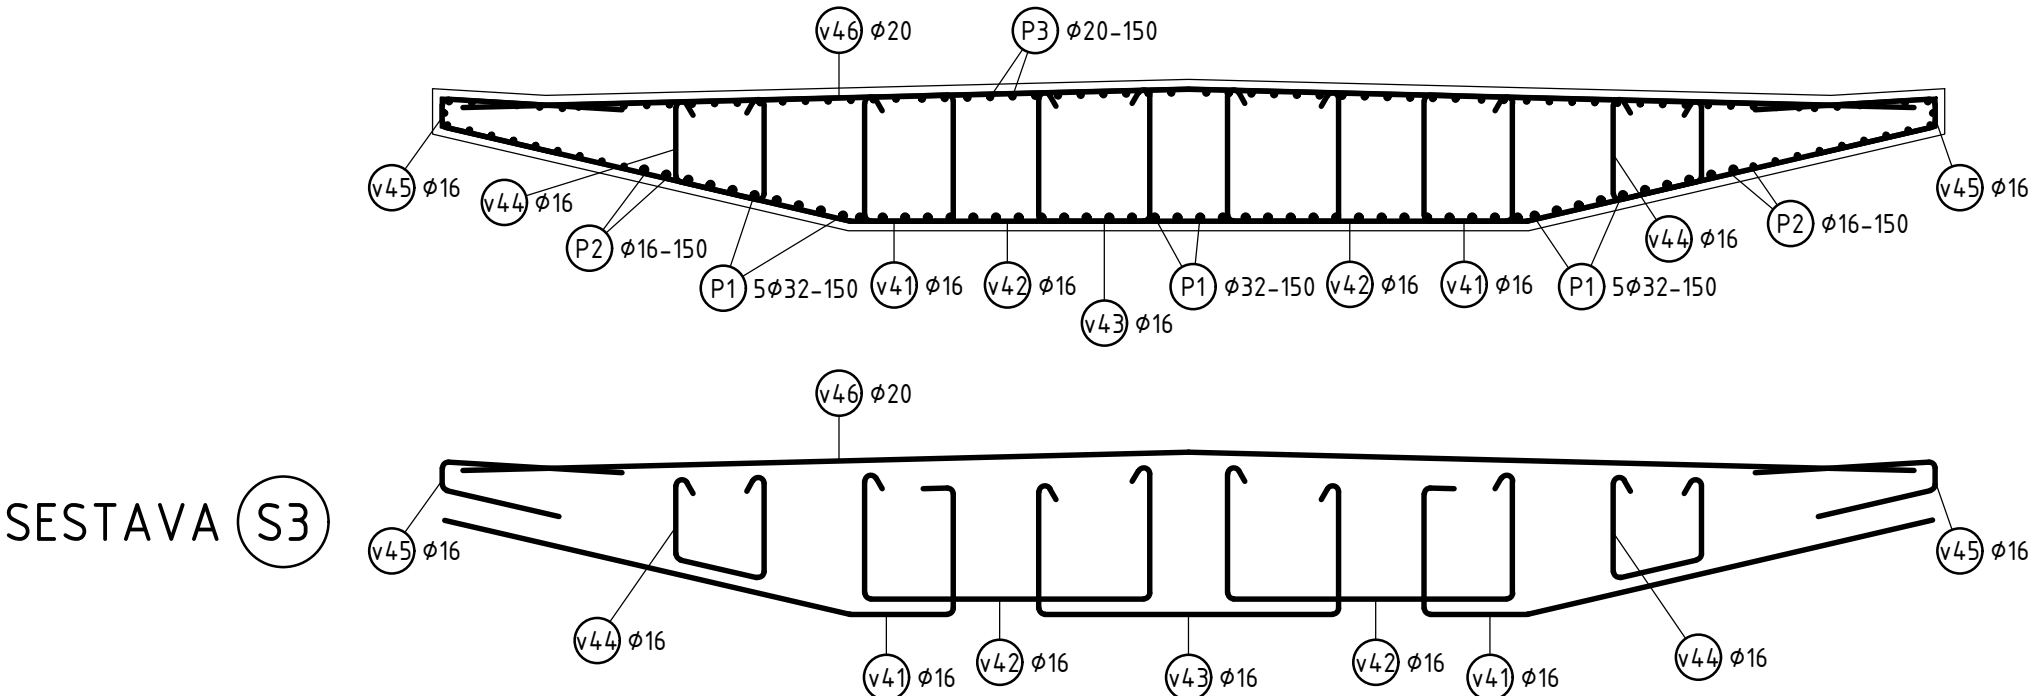


SCHÉMA VÝZTUŽE NOSNÉ KONSTRUKCE
PŘÍČNÝ ŘEZ NAD PODPOROU 1:50

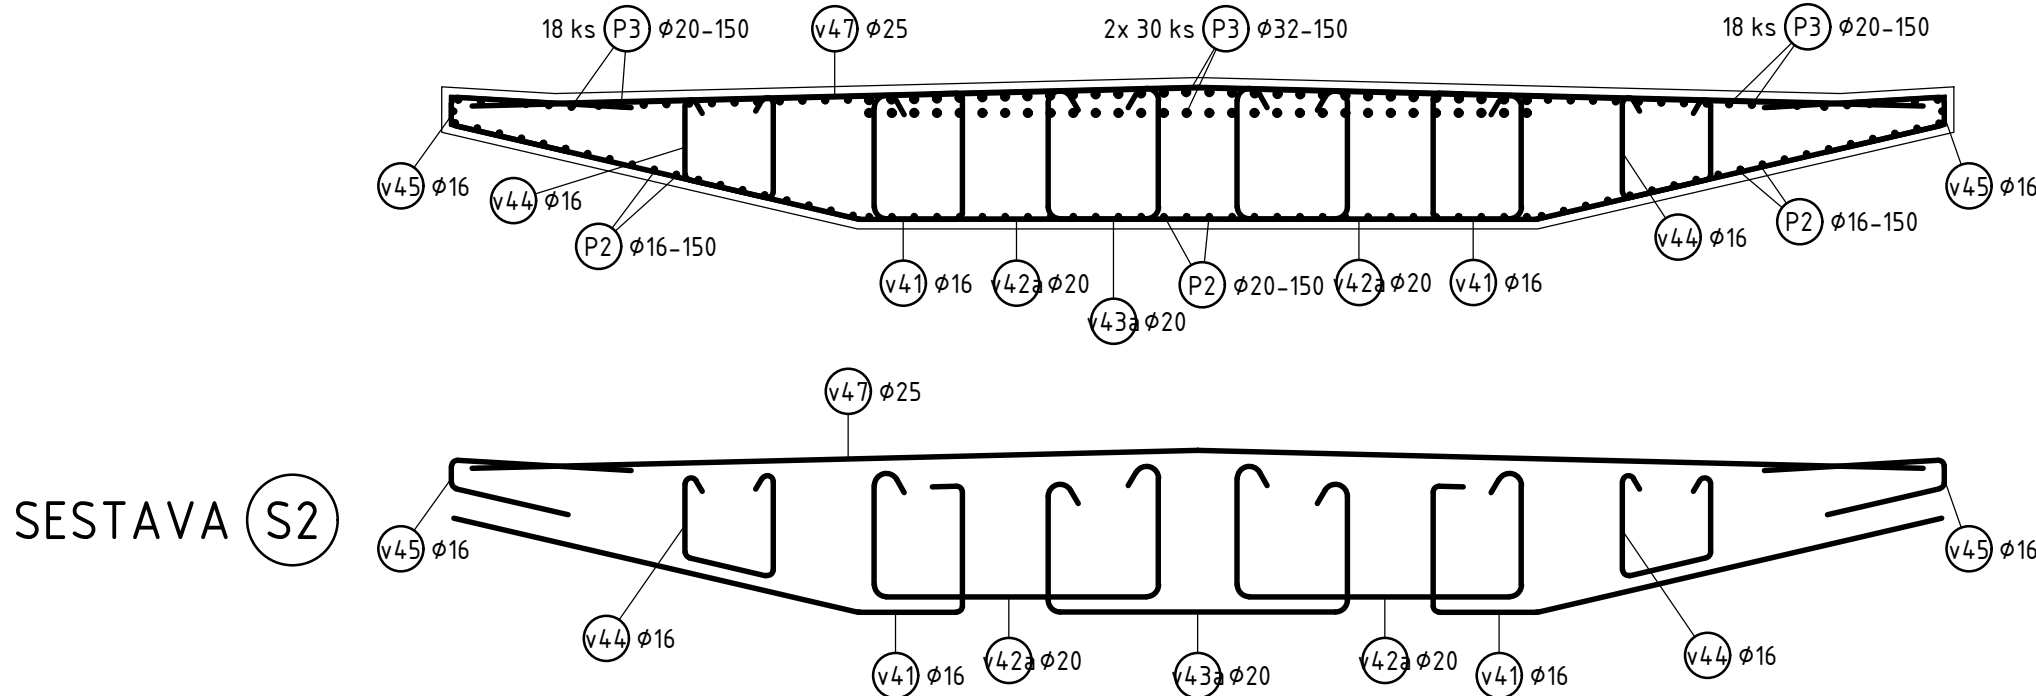

Souřadnicový systém: S-JTSK
Výškový systém: Bpv

SO 223 NADJEZD MŮK MARTINOVICE V KM 7,320

Objednatel:
ŘEDITELSTVÍ SILNIC A DÁLNIC
Ředitelství silnic a dálnic s. p.
Čerčanská 2023/12, Krč, 140 00 Praha 4

Valbek, spol. s r.o.
Vaňurova 505/17
460 07 Liberec 3

	Vypracoval	M. KNESPOVÁ	Zak. číslo	21-L113-001	
	Zodp. projektant	ING. S. RŮŽIČKA	Datum	02/2025	
	Tech. kontrola	ING. I. BELDA	Stupeň	PDPS	
	Akce	I/16 MLADÁ BOLESLAV - MARTINOVICE		Počet formátů	8x A4
Zhotovitel:		Příloha		Měřítko	-
Valbek, spol. s r.o. Vaňurova 505/17 460 07 Liberec 3		SCHÉMATICKÉ VÝKRESY VÝZTUŽE 2(2)		Č. přílohy	Paré
				302	